



SO 153 - PŘÍSTUPY NA POZEMKY k.ú. SUKORADY U MLADÉ BOLESLAVI

PODÉLNÝ PROFIL SO 153.3, M 1 : 1000 / 100

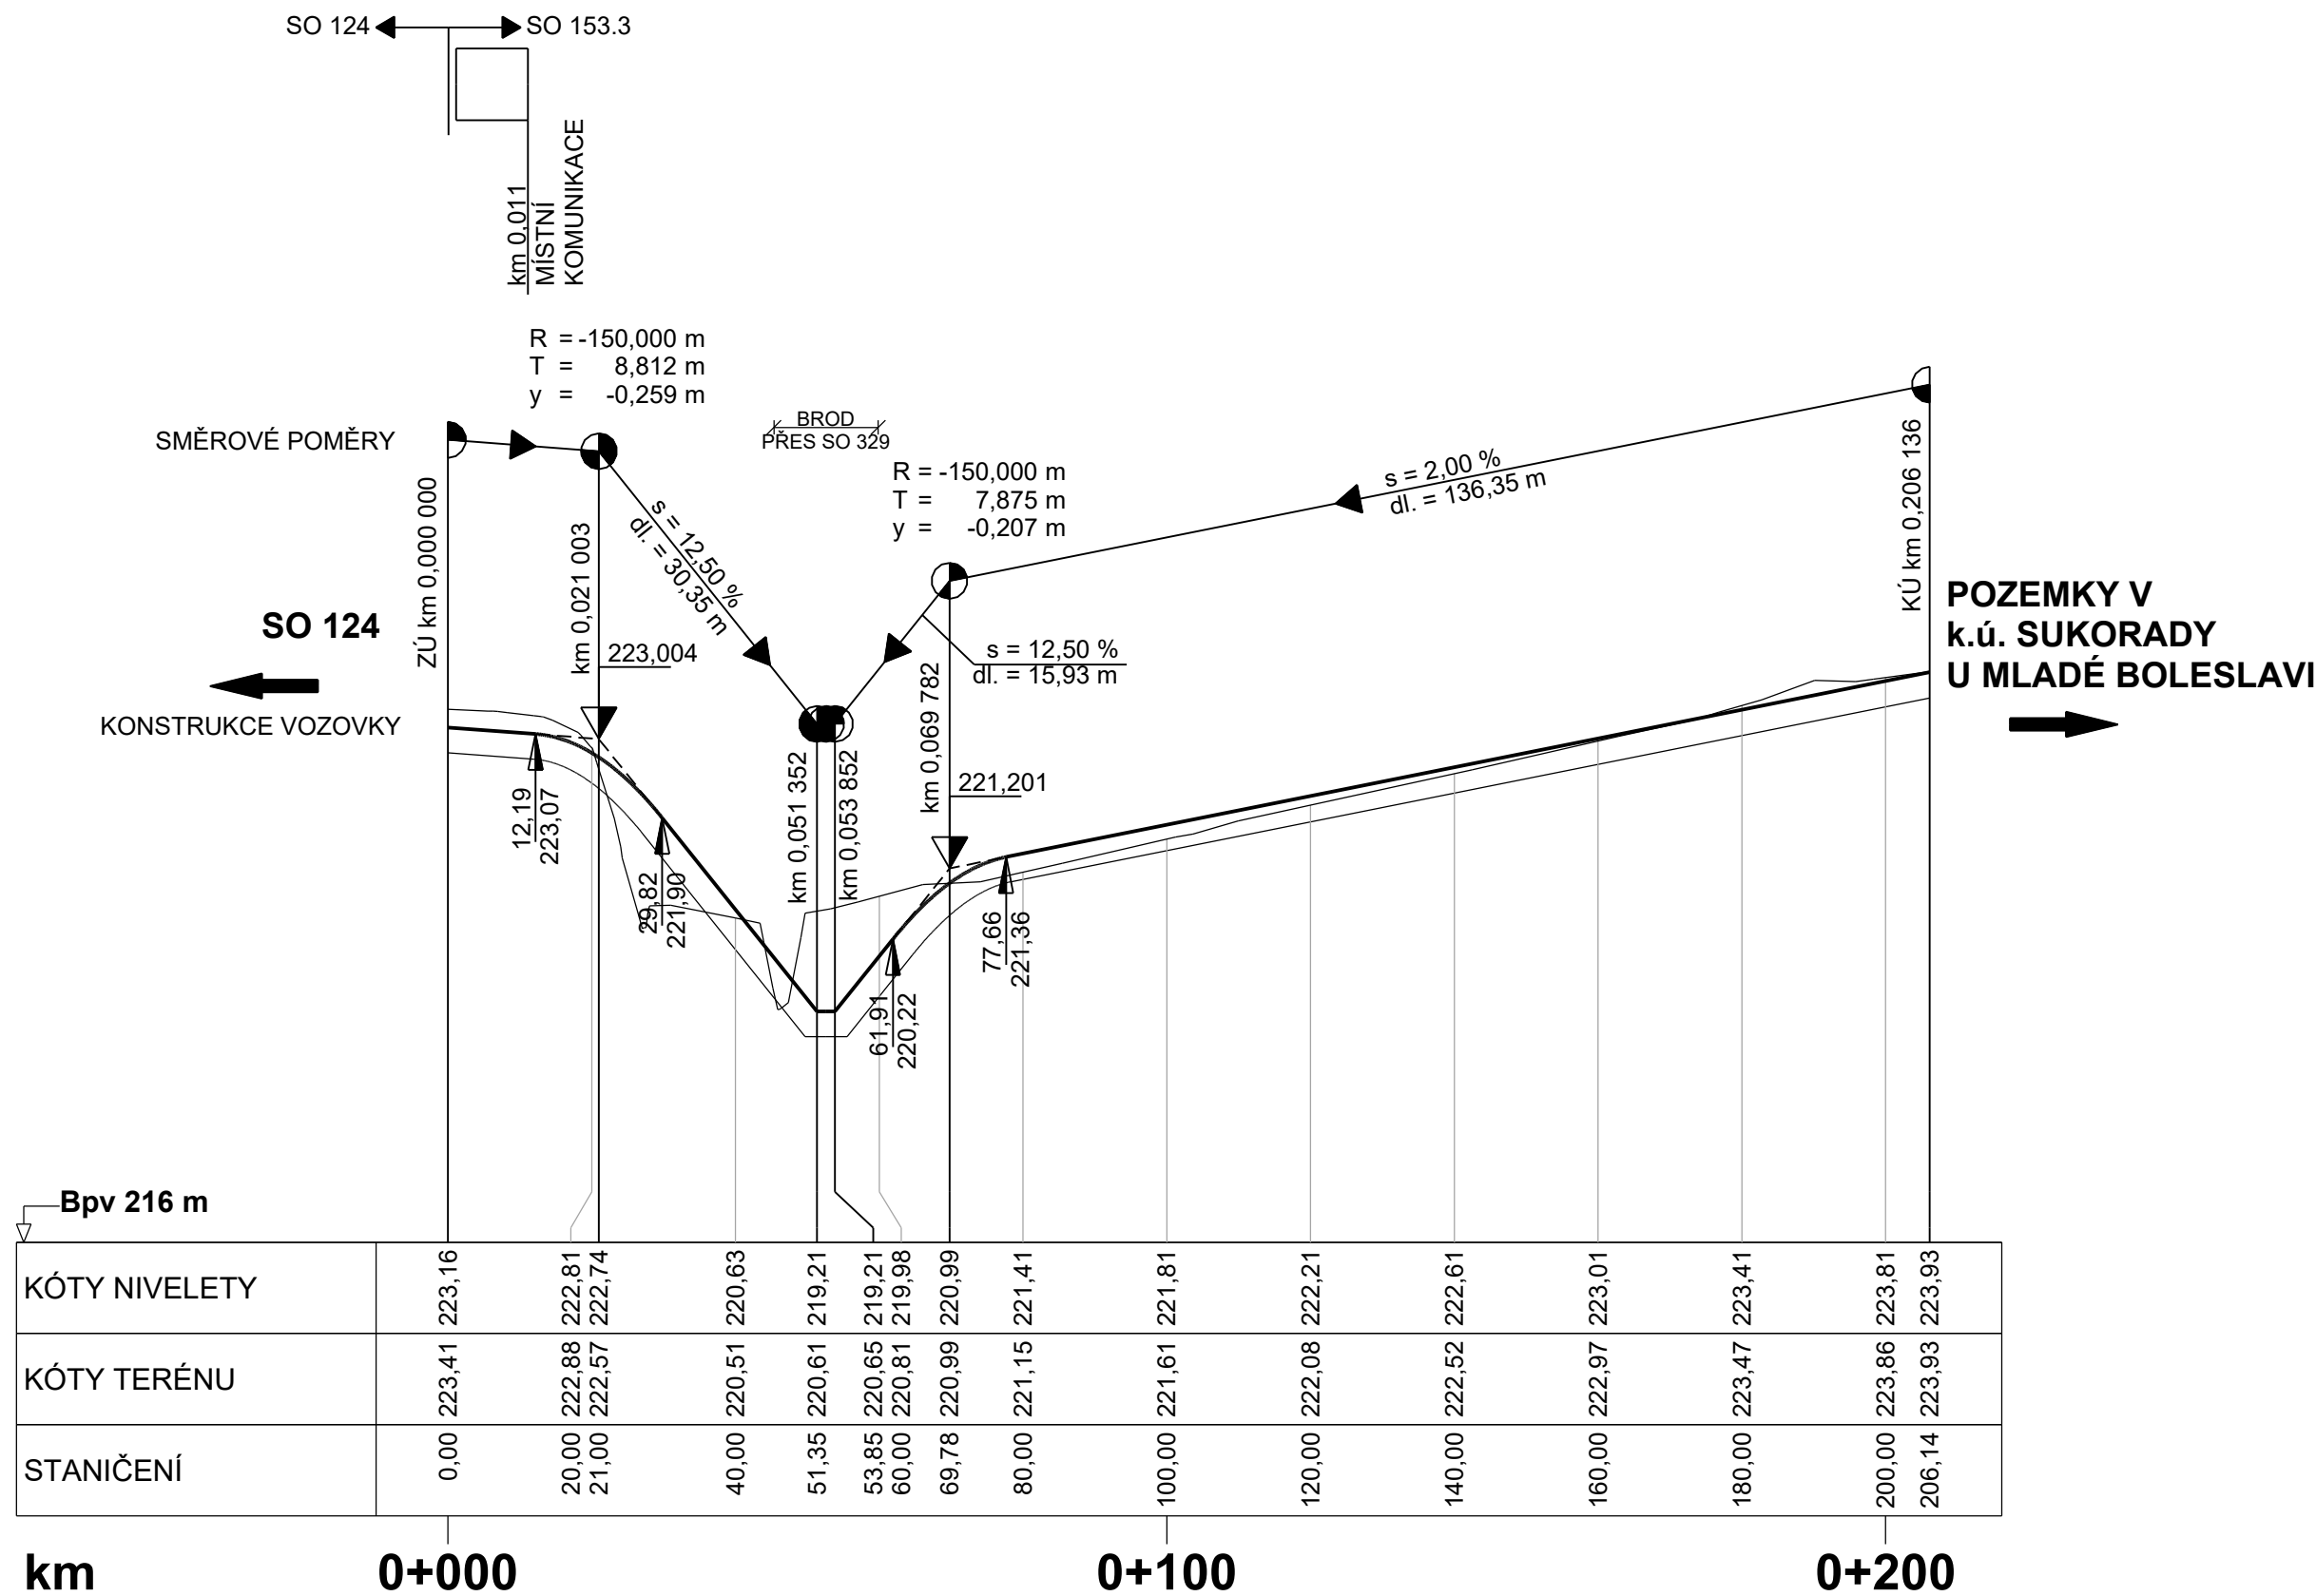

KÓTY NIVELETY	223,16	222,81	222,74	220,63	219,21	219,21	219,98	220,99	221,41	221,81	222,21	222,61	223,01	223,41	223,81	223,93
KÓTY TERÉNU	223,41	222,88	222,57	220,51	220,61	220,65	220,81	220,99	221,15	221,61	222,08	222,52	222,97	223,47	223,86	223,93
STANIČENÍ	0,00	20,00	21,00	40,00	51,35	53,85	60,00	69,78	80,00	100,00	120,00	140,00	160,00	180,00	200,00	206,14

km 0+000 0+100 0+200

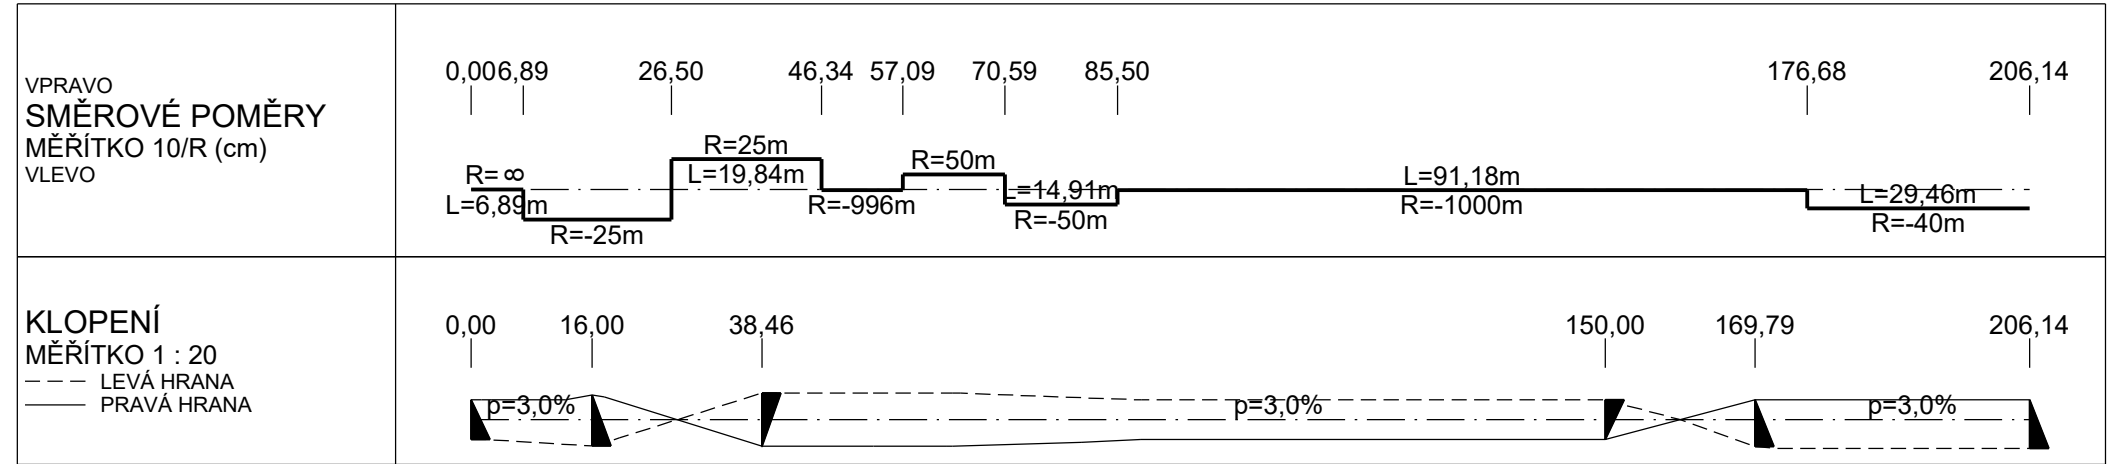

Výškový systém: BpV

SO 153 Přístupy na pozemky k.ú. Sukorady u Mladé Boleslavi

Objednatel:



Ředitelství silnic a dálnic s. p.
Čerčanská 2023/12, Krč, 140 00 Praha 4

Zhotovitel:



Valbek, spol. s r.o.
Vaňurova 505/17
460 07 Liberec 3

	Vypracoval	P. BARTUSEK	Zak. číslo	21-LI13-001
	Zodp. projektant	ING. T. KLIMENT	Datum	02/2025
	Tech. kontrola	ING. M. HANŽL	Stupeň	PDPS
	Akce I/16 MLADÁ BOLESLAV - MARTINOVICE		Počet formátů	3 x A4
			Měřítko	1 : 1 000/100
Zhotovitel: Valbek, spol. s r.o. Vaňurova 505/17 460 07 Liberec 3		Příloha PODÉLNÝ PROFIL SO 153.3		Č. přílohy Paré 3.3