


**SO 153 - PŘÍSTUPY NA POZEMKY k.ú. SUKORADY U MLADÉ BOLESLAVI
VZOROVÉ PŘÍČNÉ ŘEZY, M 1 : 50**

KATEGORIE P 4,0/30
JEDNOPRUHOVÁ, OBOUSMĚRNÁ

TŘÍDA DOPRAVNÍHO ZATÍŽENÍ VI
NÁVRHOVÁ ÚROVEŇ PORUŠENÍ D2
TYP PODLOŽÍ PII (PN 6-5)

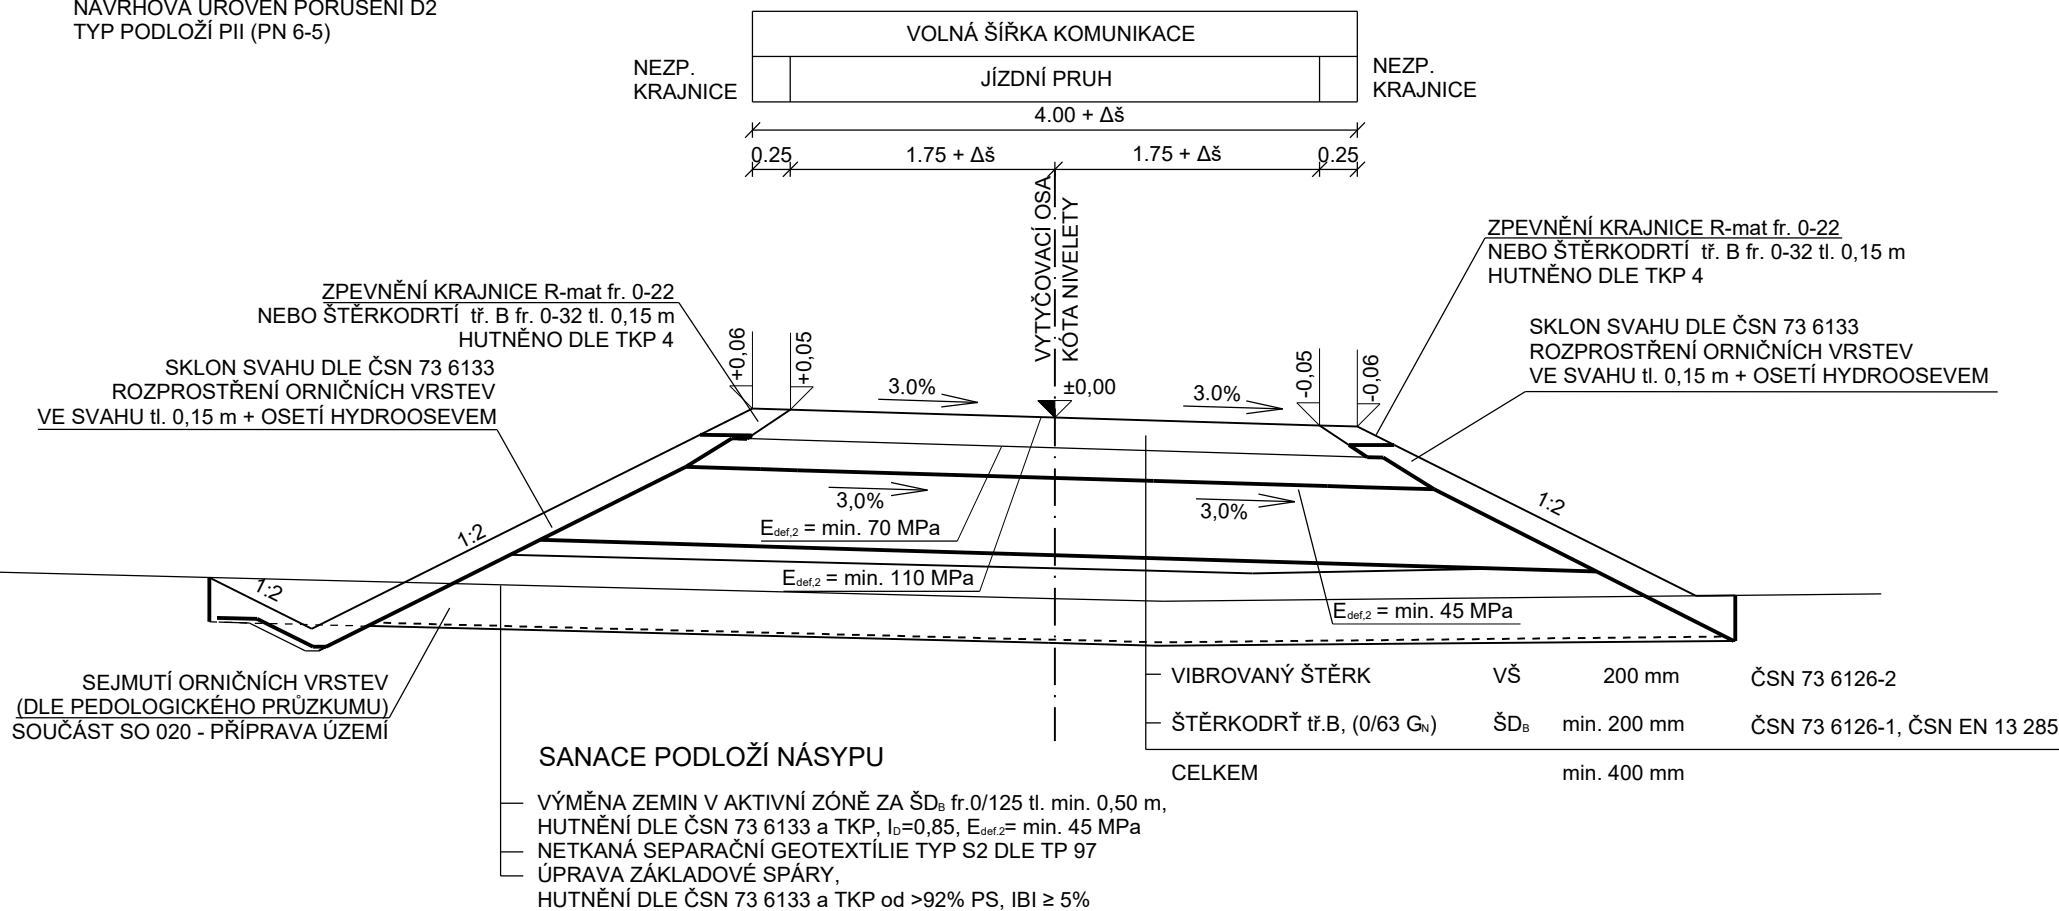

KATEGORIE P 4,0/30
JEDNOPRUHOVÁ, OBOUSMĚRNÁ

TŘÍDA DOPRAVNÍHO ZATÍŽENÍ VI
NÁVRHOVÁ ÚROVEŇ PORUŠENÍ D2
TYP PODLOŽÍ PII (PN 6-5)



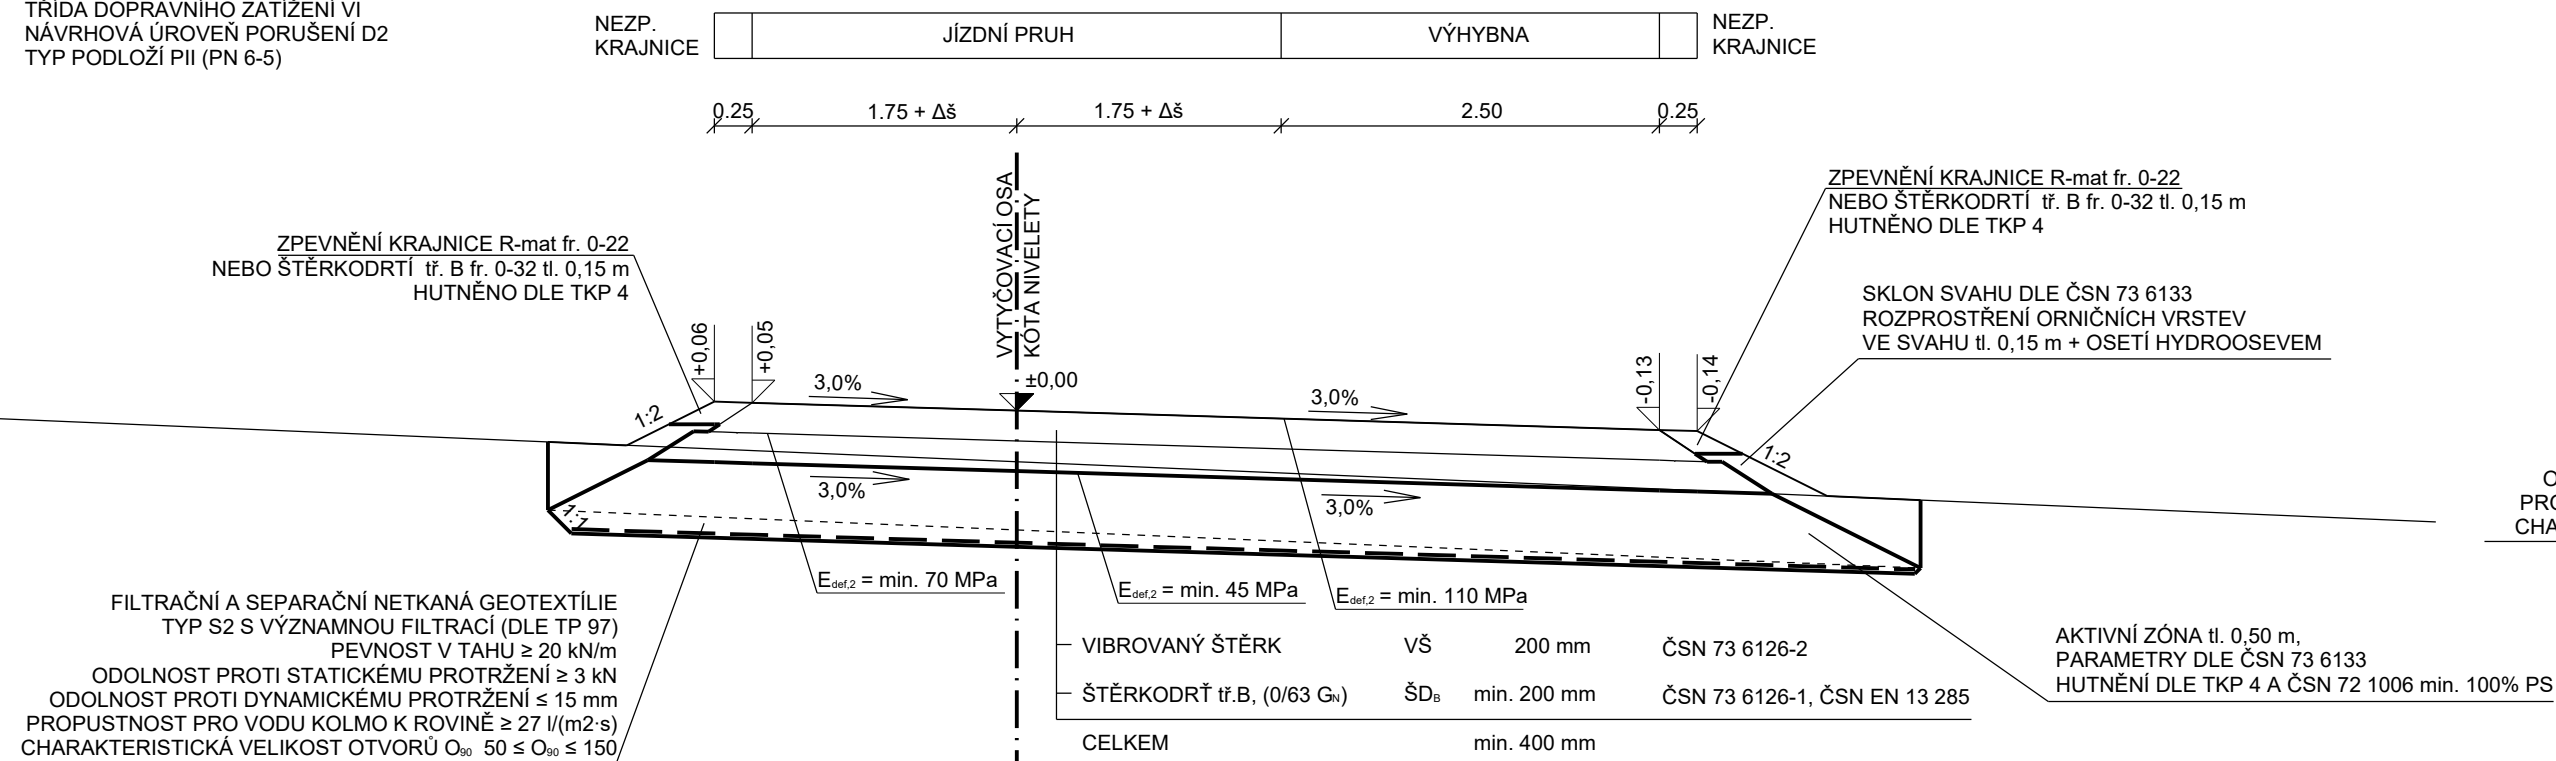


SCHÉMA BRODU V OSE PŘÍSTUPOVÉ KOMUNIKACE, M 1 : 100


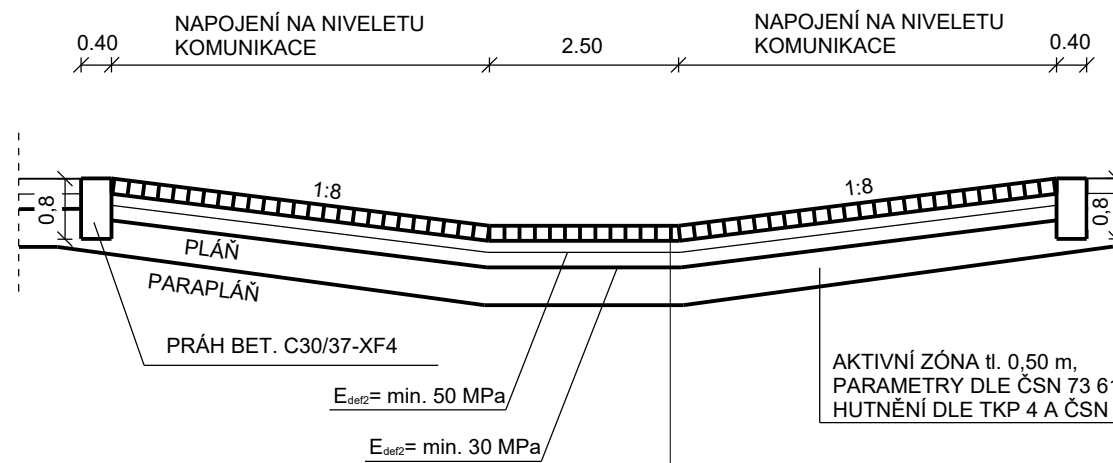


DETAIL ZPEVNĚNÉHO PŘÍKOPU

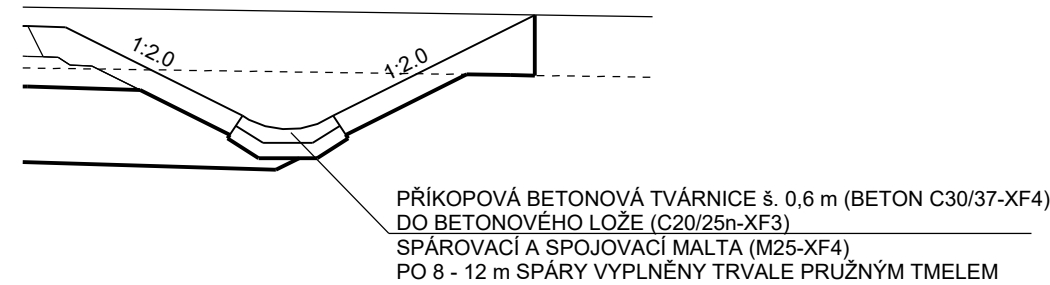

DLAŽBA Z LOMOVÉHO KAMENE	DL 200	200 mm	ČSN 73 6131
PODKLADNÍ BETON C20/25n - XF3		150 mm	ČSN EN 206
ŠTĚRKODŘŤ tř. A, (0/32 G ₆)	ŠD _A	min. 200 mm	ČSN 73 6126-1, ČSN EN 13 285
CELKEM		min. 550 mm	

PŘÍČNÝ ŘEZ BRODEM

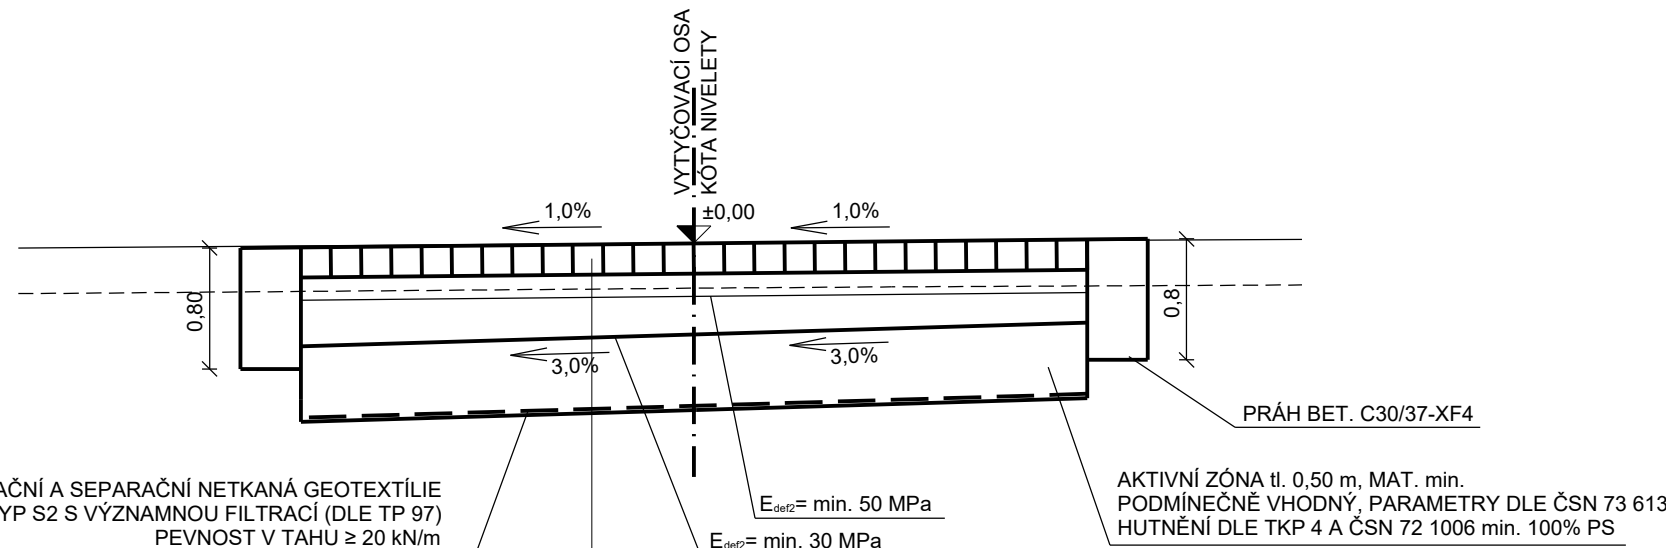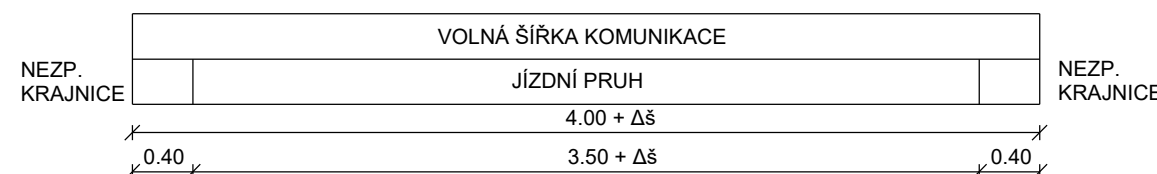

DLAŽBA Z LOMOVÉHO KAMENE	DL 200	200 mm	ČSN 73 6131
PODKLADNÍ BETON C20/25n - XF3		150 mm	ČSN EN 206
ŠTĚRKODRŤ tř. A ₁ (0/32 G ₁)	ŠD _A	min. 200 mm	ČSN 73 6126-1, ČSN EN 13 285
CELKEM		min. 550 mm	

Výškový systém: Bpv

SO 153 Přístupy na pozemky k.ú. Sukorady u Mladé Boleslavi**Objednatel:**

ŘEDITELSTVÍ SILNIC A DÁLNIC

Ředitelství silnic a dálnic s. p.
Čerčanská 2023/12, Krč, 140 00 Praha 4

Zhotovitel:



Valbek, spol. s r.o.
Vaňurova 505/17
460 07 Liberec 3



Zhotovitel:

Valbek, spol. s r.o.
Vaňurova 505/17
460 07 Liberec 3

Vypracoval	P. BARTUSEK		Zak. číslo	21-L113-001
Zodp. projektant	ING. T. KLIMENT		Datum	02/2025
Tech. kontrola	ING. M. HANŽL		Stupeň	PDPS
Akce I/16 MLADÁ BOLESLAV - MARTINOVICE			Počet formátů	4 x A4
			Měřítko	1 : 50
			Č. přílohy	Paré
Příloha VZOROVÉ PŘÍČNÉ ŘEZY			4	