




SO 153 - PŘÍSTUPY NA POZEMKY k.ú. SUKORADY U MLADÉ BOLESLAVI
PŘÍČNÉ ŘEZY SO 153.1 - km 0,020 - 0,480, M 1 : 100

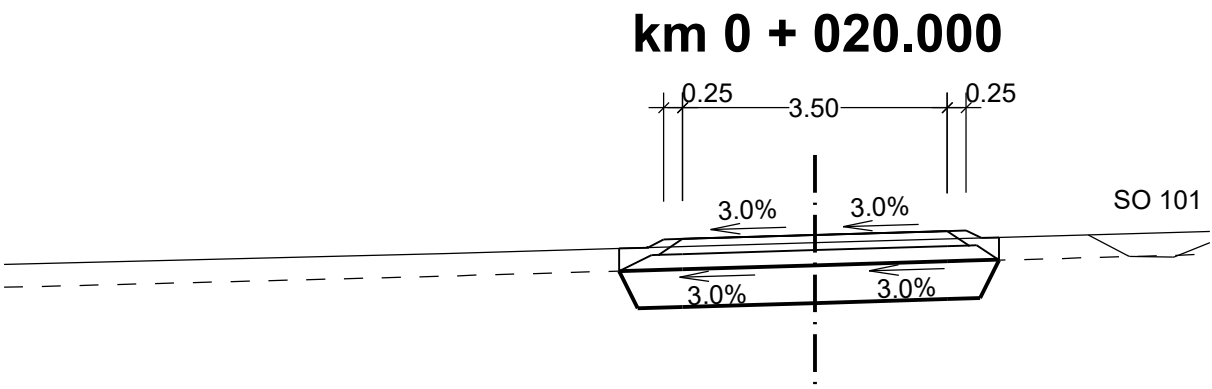


PROJEKTOVANÝ STAV	S. R. 215 m
ODSAZENÍ OD OSY	-2.59 218.40 -2.59 218.71 -2.21 218.70 -2.00 218.62 -1.75 218.62
STÁVAJÍCÍ TERÉN	0.00 218.77
ODSAZENÍ OD OSY	-4.87 218.63 1.75 218.93 2.00 218.94 2.16 218.94 2.44 218.54 2.44 218.54

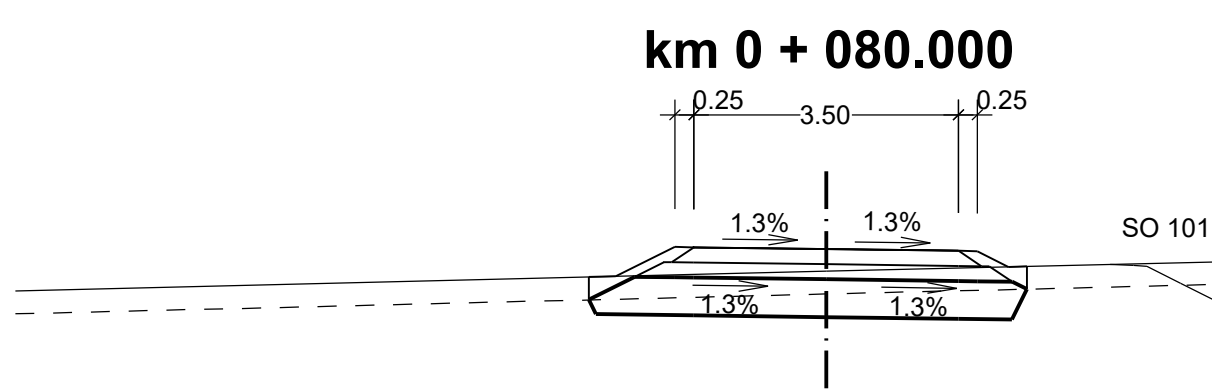


PROJEKTOVANÝ STAV	S. R. 219 m
ODSAZENÍ OD OSY	-3.14 222.02 -3.14 222.32 -2.78 222.33 -2.00 222.72 -1.75 222.71
STÁVAJÍCÍ TERÉN	0.00 222.40
ODSAZENÍ OD OSY	1.75 222.67 2.00 223.36 2.41 222.45 2.66 222.46 2.66 222.16

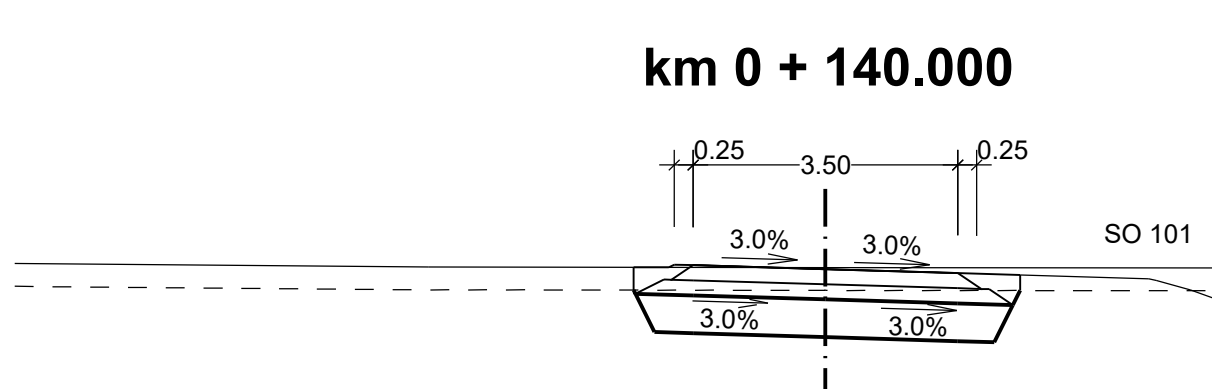


PROJEKTOVANÝ STAV	S. R. 220 m
ODSAZENÍ OD OSY	-2.54 223.45 -2.54 223.66 -2.07 223.45 -2.00 223.71 -1.75 223.46
STÁVAJÍCÍ TERÉN	0.00 223.45
ODSAZENÍ OD OSY	1.75 223.37 2.00 223.44 2.16 223.44 2.44 223.14 2.66 223.14

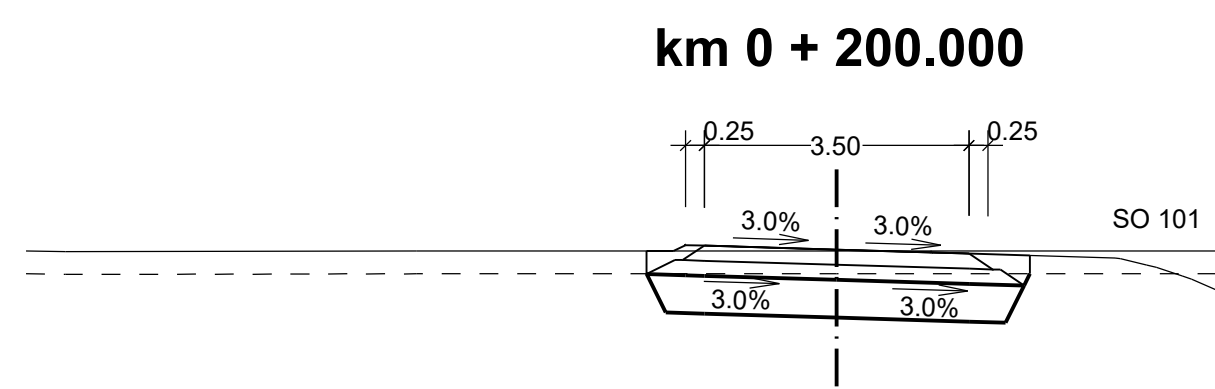


PROJEKTOVANÝ STAV	S. R. 220 m
ODSAZENÍ OD OSY	-2.52 223.36 -2.52 223.66 -2.00 223.71 -2.00 223.71 -1.75 223.73
STÁVAJÍCÍ TERÉN	0.00 223.66
ODSAZENÍ OD OSY	1.75 223.63 2.00 223.63 2.08 223.66 2.56 223.66 2.56 223.36

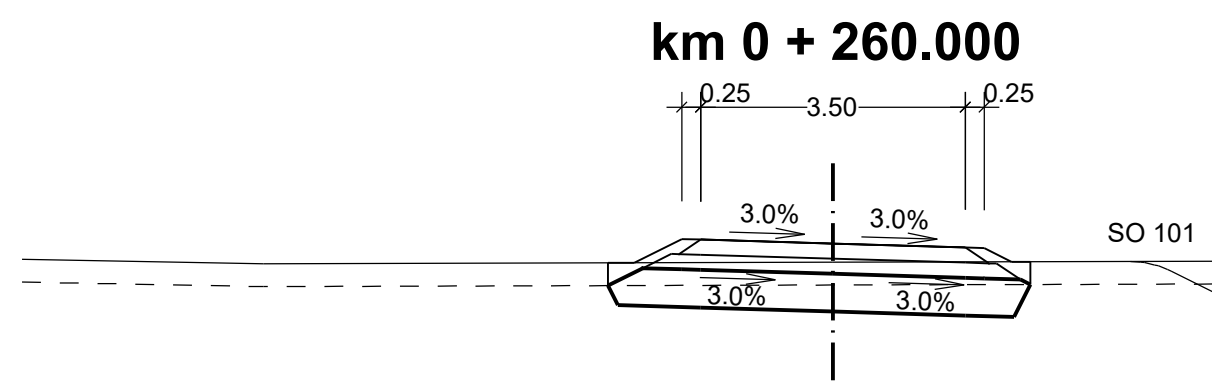


PROJEKTOVANÝ STAV	S. R. 220 m
ODSAZENÍ OD OSY	-2.08 223.21 -2.88 223.51 -2.63 223.51 -2.00 223.82 -1.75 223.81
STÁVAJÍCÍ TERÉN	0.00 223.51
ODSAZENÍ OD OSY	1.75 223.71 2.00 223.70 2.36 223.52 2.61 223.52 2.61 223.42

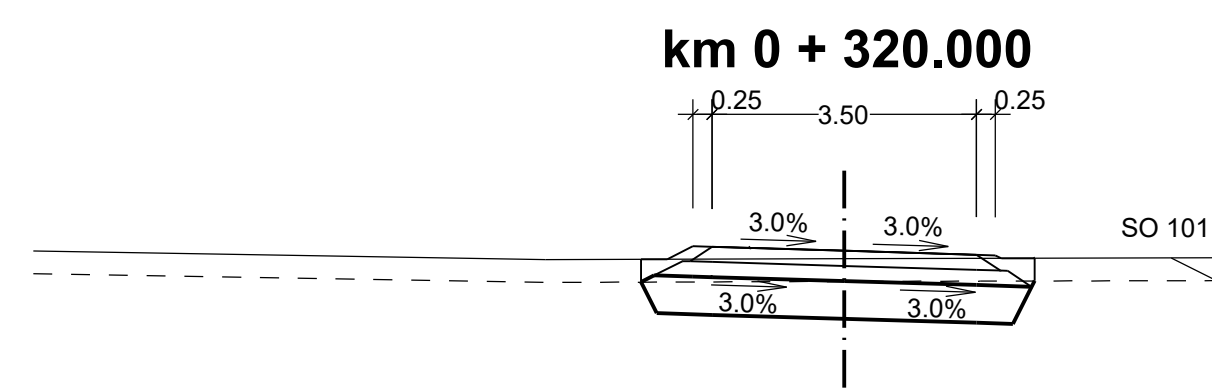


PROJEKTOVANÝ STAV	S. R. 220 m
ODSAZENÍ OD OSY	-2.69 223.25 -2.69 223.56 -2.34 223.56 -2.00 223.66 -1.75 223.72
STÁVAJÍCÍ TERÉN	0.00 223.56
ODSAZENÍ OD OSY	1.75 223.67 2.00 223.61 2.21 223.43 2.52 223.27 2.52 223.27

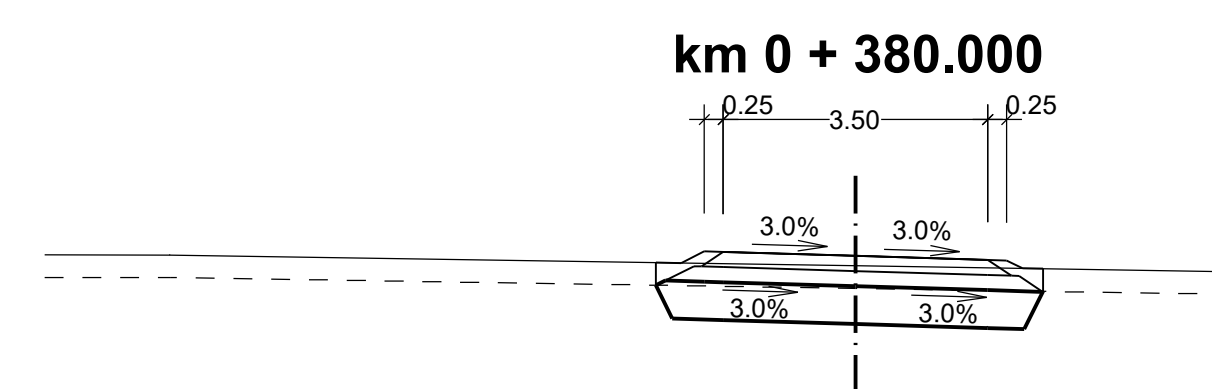


PROJEKTOVANÝ STAV	S. R. 220 m
ODSAZENÍ OD OSY	-2.64 223.21 -2.64 223.51 -2.31 223.51 -2.00 223.66 -1.75 223.65
STÁVAJÍCÍ TERÉN	0.00 223.47
ODSAZENÍ OD OSY	1.75 223.55 2.00 223.55 2.21 223.43 2.48 223.13 2.48 223.13

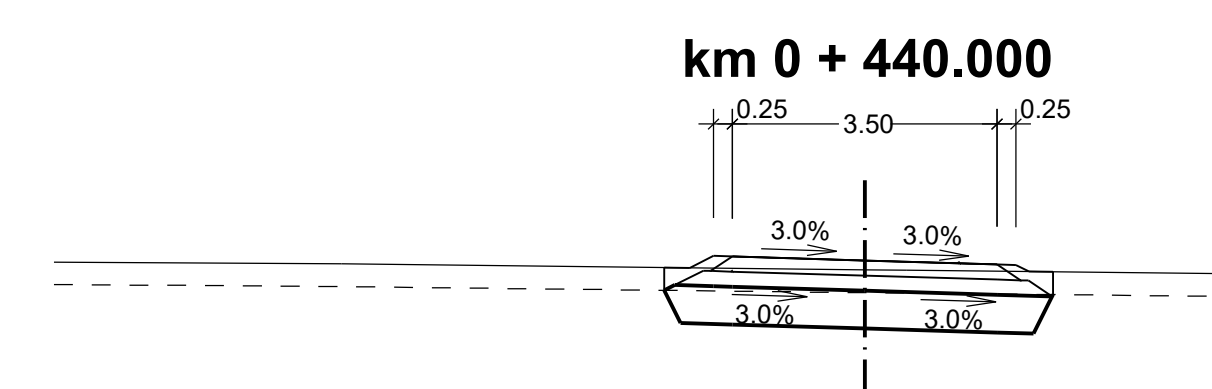


PROJEKTOVANÝ STAV	S. R. 220 m
ODSAZENÍ OD OSY	-2.65 223.14 -2.65 223.44 -2.31 223.44 -2.00 223.60 -1.75 223.59
STÁVAJÍCÍ TERÉN	0.00 223.41
ODSAZENÍ OD OSY	1.75 223.49 2.00 223.48 2.17 223.39 2.49 223.09 2.49 223.09

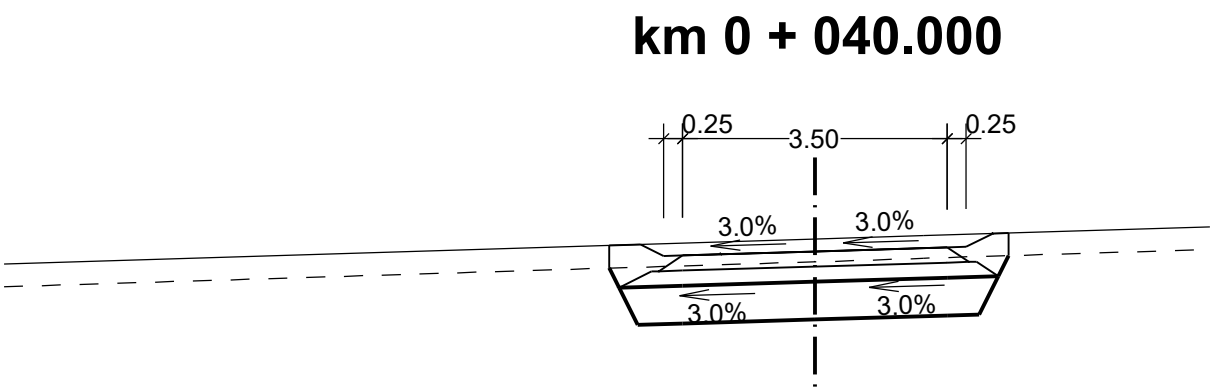


PROJEKTOVANÝ STAV	S. R. 217 m
ODSAZENÍ OD OSY	-2.72 220.16 -2.72 220.46 -2.31 220.48 -2.00 220.33 -1.75 220.33
STÁVAJÍCÍ TERÉN	0.00 220.55
ODSAZENÍ OD OSY	1.44 220.59 1.75 220.44 2.00 220.44 2.00 220.44 2.56 220.33

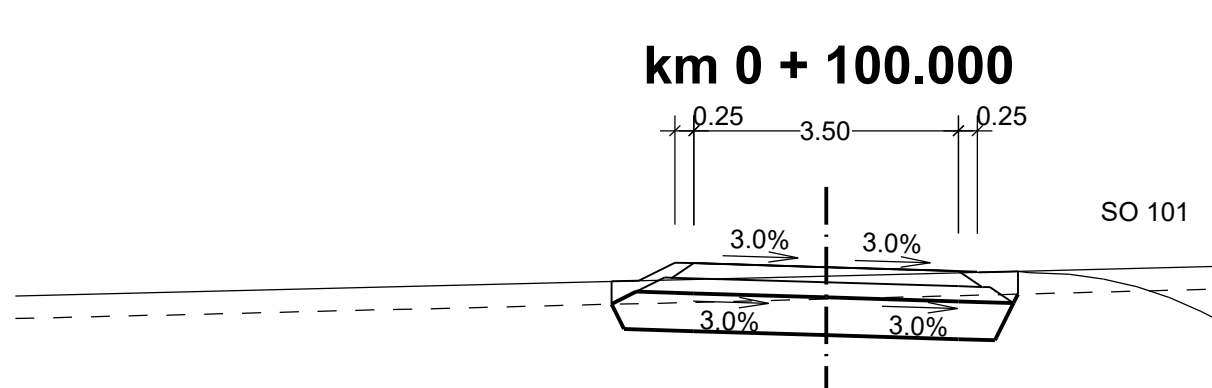


PROJEKTOVANÝ STAV	S. R. 220 m
ODSAZENÍ OD OSY	-2.84 222.69 -2.84 222.99 -2.54 223.56 -2.00 223.24 -1.75 223.23
STÁVAJÍCÍ TERÉN	0.00 223.06
ODSAZENÍ OD OSY	1.75 223.12 2.00 223.11 2.02 223.11 2.54 223.12 2.54 222.82

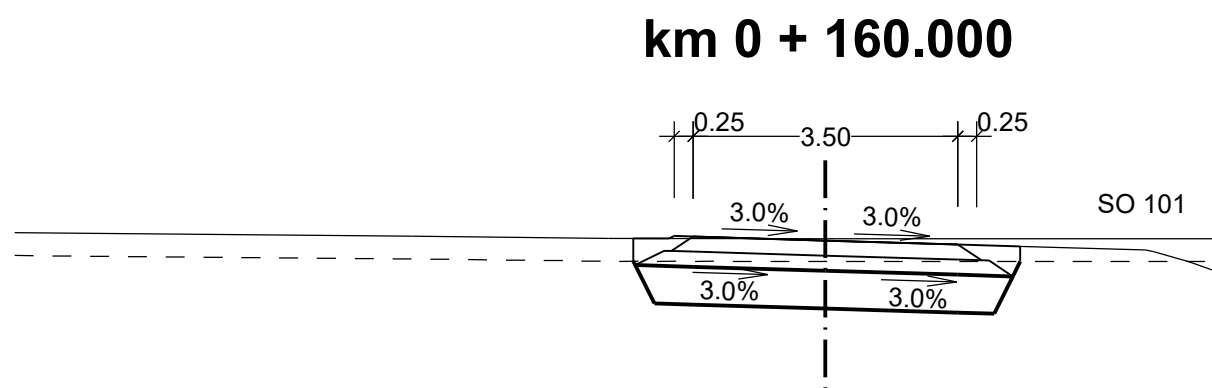


PROJEKTOVANÝ STAV	S. R. 220 m
ODSAZENÍ OD OSY	-2.54 223.26 -2.54 223.56 -2.07 223.55 -2.00 223.59 -1.75 223.58
STÁVAJÍCÍ TERÉN	0.00 223.55
ODSAZENÍ OD OSY	1.75 223.48 2.00 223.47 2.17 223.55 2.44 223.25 2.58 223.25

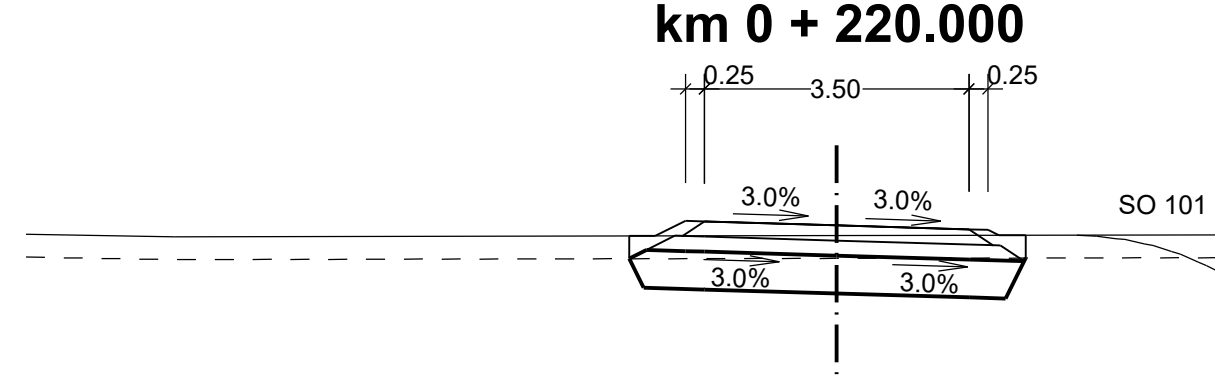


PROJEKTOVANÝ STAV	S. R. 220 m
ODSAZENÍ OD OSY	-2.75 223.29 -2.75 223.59 -2.49 223.59 -2.00 223.81 -1.75 223.78
STÁVAJÍCÍ TERÉN	0.00 223.59
ODSAZENÍ OD OSY	1.75 223.69 2.00 223.69 2.14 223.60 2.50 223.60 2.50 223.30

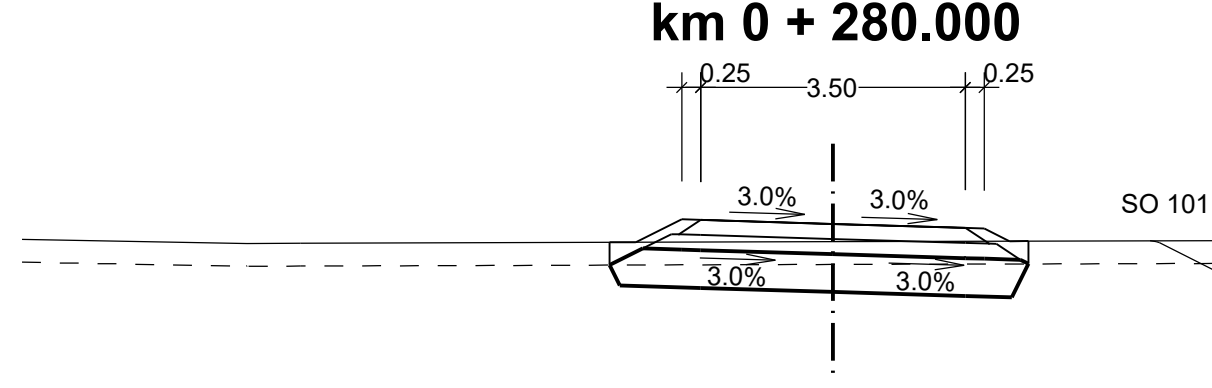


PROJEKTOVANÝ STAV	S. R. 220 m
ODSAZENÍ OD OSY	-2.05 223.20 -2.05 223.50 -2.61 223.51 -2.00 223.81 -1.75 223.80
STÁVAJÍCÍ TERÉN	0.00 223.51
ODSAZENÍ OD OSY	1.75 223.70 2.00 223.69 2.34 223.52 2.59 223.52 2.59 223.42

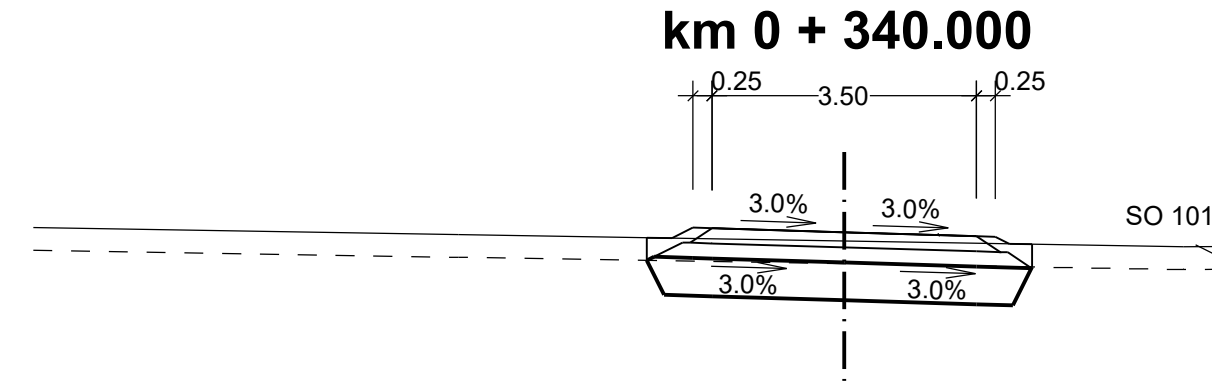


PROJEKTOVANÝ STAV	S. R. 220 m
ODSAZENÍ OD OSY	-2.61 223.27 -2.61 223.57 -2.28 223.56 -2.00 223.69 -1.75 223.69
STÁVAJÍCÍ TERÉN	0.00 223.52
ODSAZENÍ OD OSY	1.75 223.59 2.00 223.58 2.29 223.37 2.49 223.48 2.49 223.18

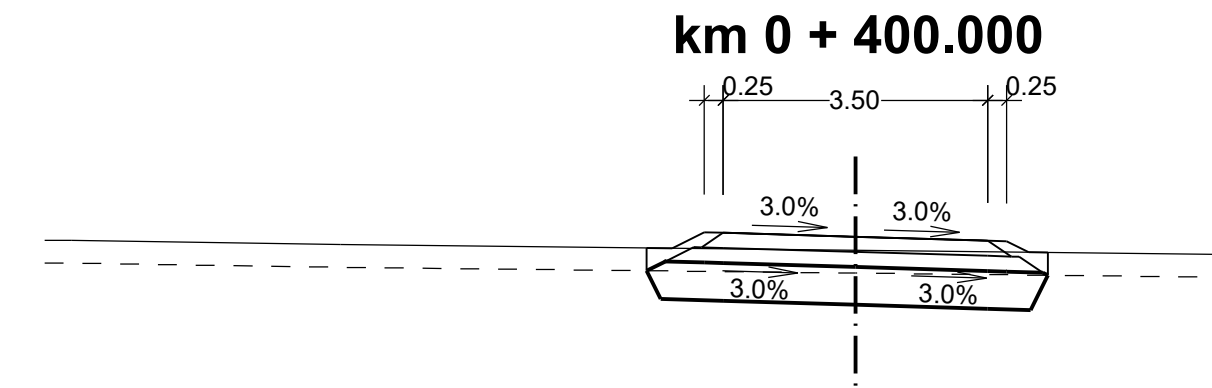


PROJEKTOVANÝ STAV	S. R. 220 m
ODSAZENÍ OD OSY	-2.76 223.13 -2.76 223.43 -2.43 223.43 -2.00 223.64 -1.75 223.63
STÁVAJÍCÍ TERÉN	0.00 223.40
ODSAZENÍ OD OSY	1.75 223.53 2.00 223.52 2.29 223.37 2.55 223.37 2.55 223.07

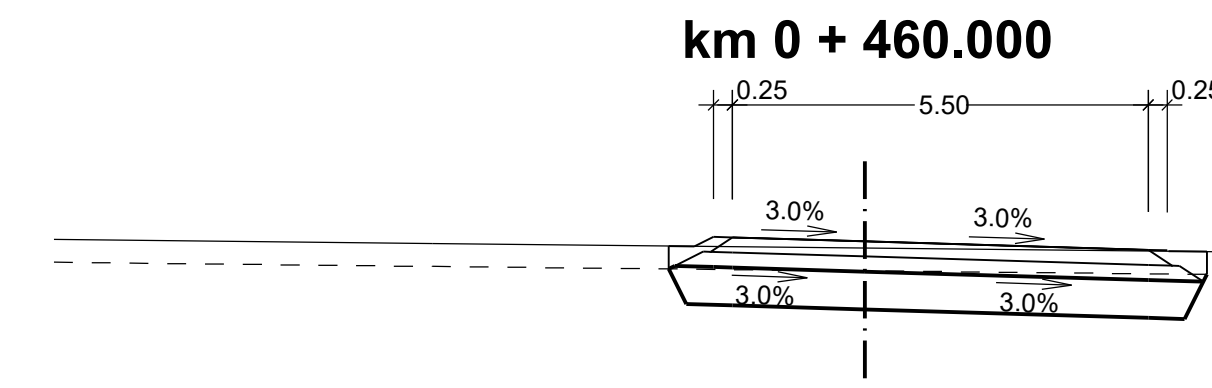


PROJEKTOVANÝ STAV	S. R. 220 m
ODSAZENÍ OD OSY	-2.59 223.16 -2.59 223.46 -2.25 223.45 -2.00 223.59 -1.75 223.57
STÁVAJÍCÍ TERÉN	0.00 223.43
ODSAZENÍ OD OSY	1.75 223.52 2.00 223.52 2.29 223.37 2.55 223.37 2.55 223.07

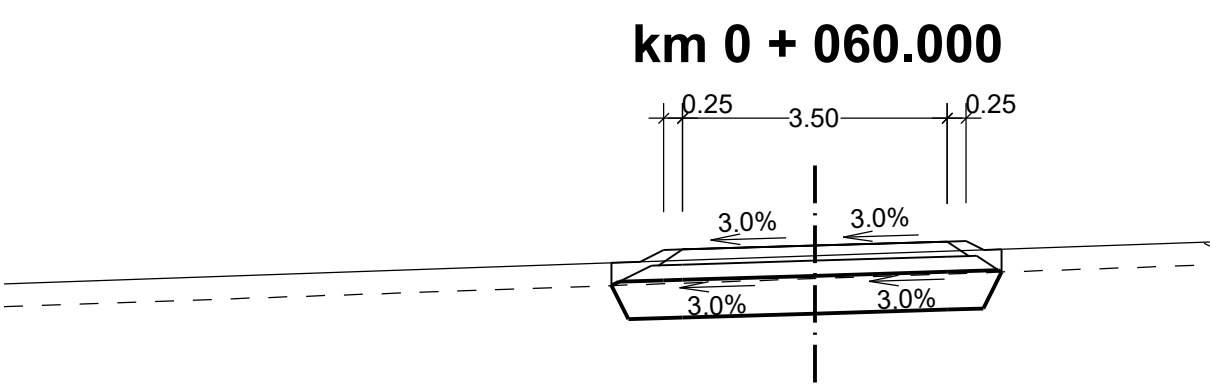


PROJEKTOVANÝ STAV	S. R. 218 m
ODSAZENÍ OD OSY	-2.69 221.23 -2.69 221.53 -2.31 221.54 -2.00 221.50 -1.75 221.71
STÁVAJÍCÍ TERÉN	0.00 221.62
ODSAZENÍ OD OSY	1.75 221.81 2.00 221.82 2.00 221.82 2.47 221.71 2.47 221.41

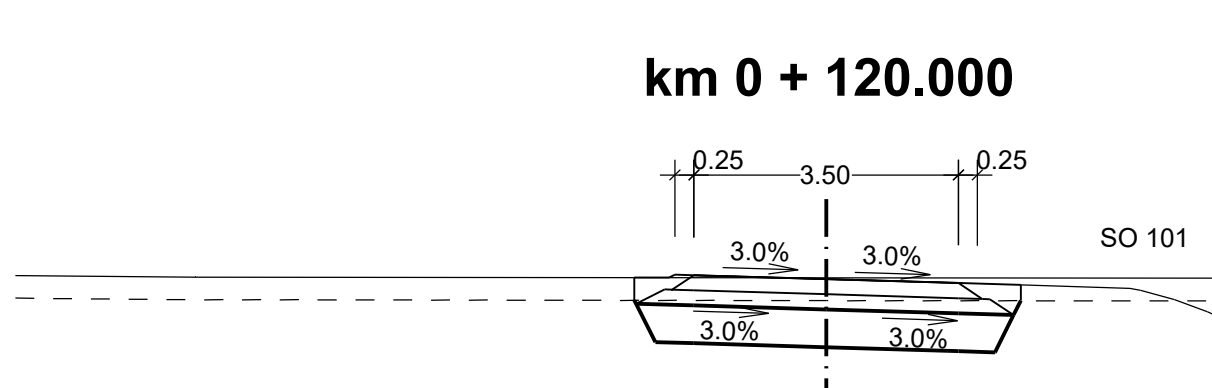


PROJEKTOVANÝ STAV	S. R. 220 m
ODSAZENÍ OD OSY	-2.54 223.03 -2.54 223.33 -2.14 223.33 -2.00 223.37 -1.75 223.37
STÁVAJÍCÍ TERÉN	0.00 223.31
ODSAZENÍ OD OSY	1.75 223.26 2.00 223.33 2.15 223.33 2.57 223.33 2.57 223.03

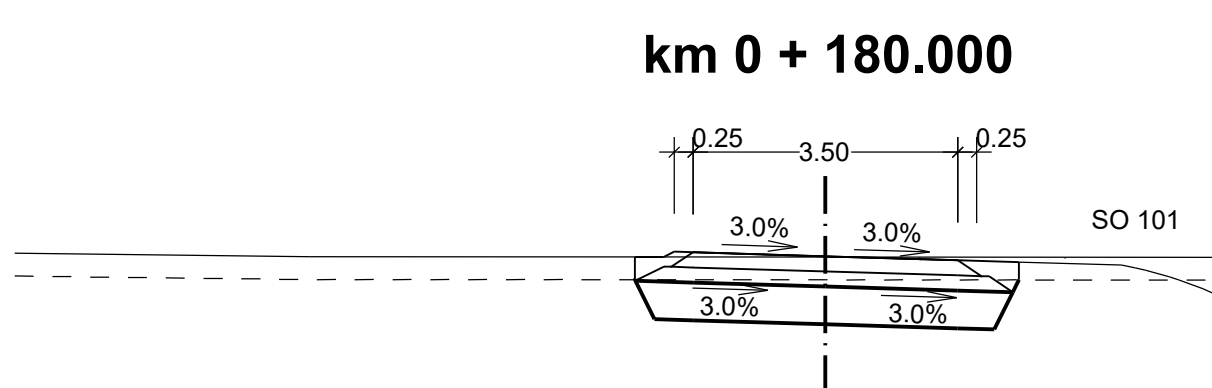


PROJEKTOVANÝ STAV	S. R. 220 m
ODSAZENÍ OD OSY	-2.52 223.31 -2.52 223.61 -2.14 223.61 -2.00 223.66 -1.75 223.67
STÁVAJÍCÍ TERÉN	0.00 223.61
ODSAZENÍ OD OSY	1.75 223.56 2.00 223.56 2.10 223.60 2.48 223.30 2.58 223.30

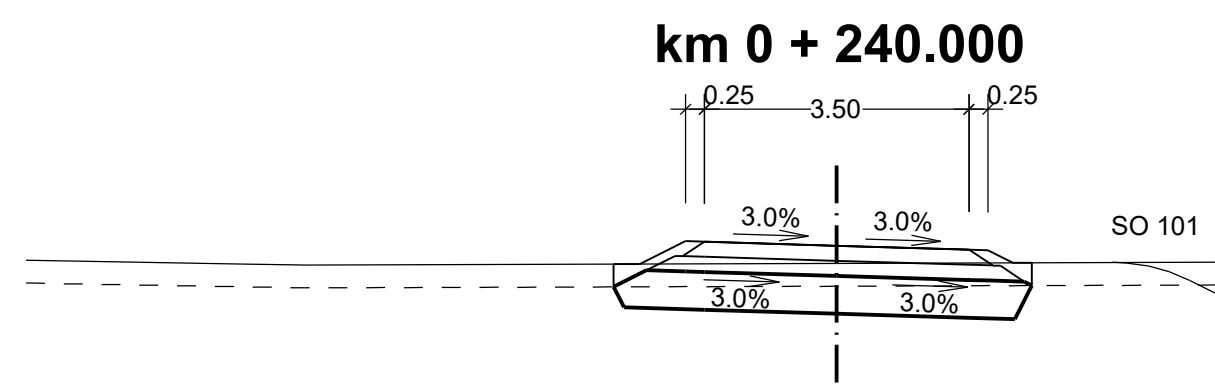


PROJEKTOVANÝ STAV	S. R. 220 m
ODSAZENÍ OD OSY	-2.95 223.21 -2.95 223.51 -2.49 223.53 -2.00 223.82 -1.75 223.81
STÁVAJÍCÍ TERÉN	0.00 223.52
ODSAZENÍ OD OSY	1.75 223.70 2.00 223.66 2.22 223.54 2.48 223.24 2.48 223.24

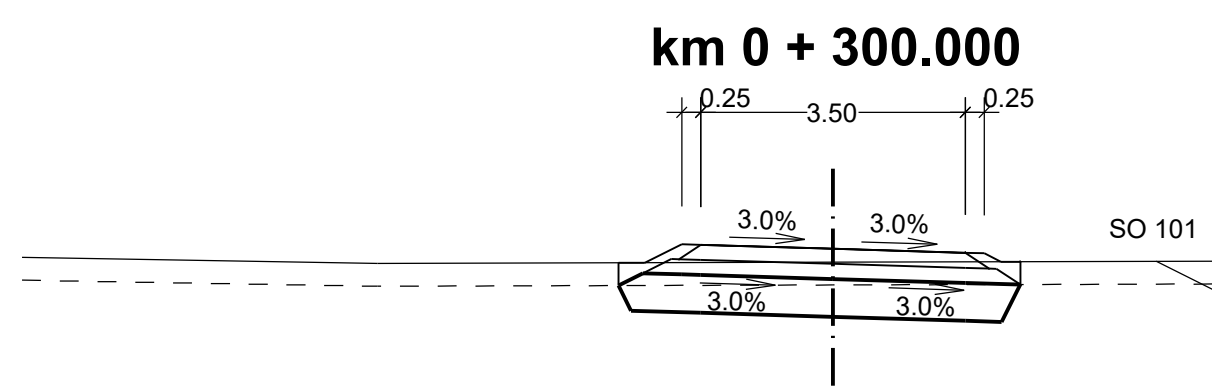


PROJEKTOVANÝ STAV	S. R. 220 m
ODSAZENÍ OD OSY	-2.84 223.23 -2.84 223.53 -2.49 223.53 -2.00 223.77 -1.75 223.77
STÁVAJÍCÍ TERÉN	0.00 223.54
ODSAZENÍ OD OSY	1.75 223.66 2.00 223.66 2.22 223.54 2.48 223.24 2.48 223.24

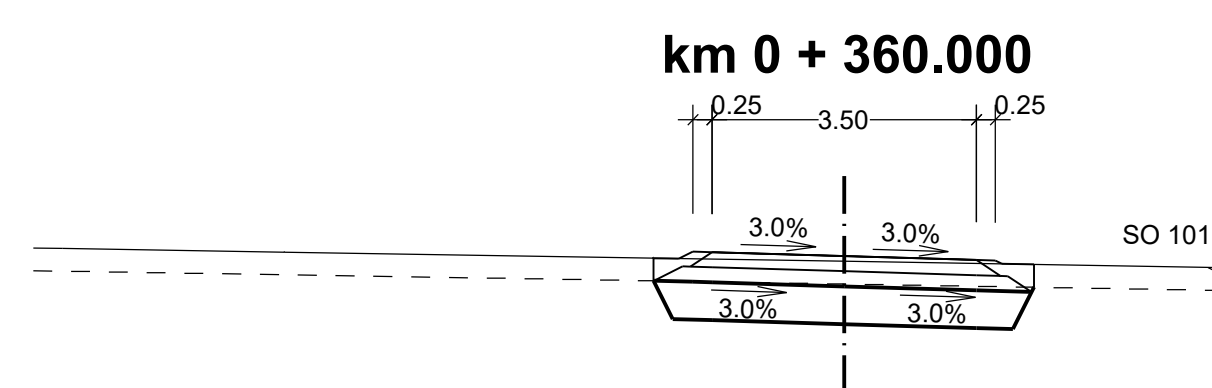

PROJEKTOVANÝ STAV	S. R. 220 m
ODSAZENÍ OD OSY	-2.52 223.29 -2.52 223.59 -2.19 223.59 -2.00 223.63 -1.75 223.67
STÁVAJÍCÍ TERÉN	0.00 223.62
ODSAZENÍ OD OSY	1.75 223.57 2.00 223.56 2.22 223.54 2.48 223.24 2.48 223.24

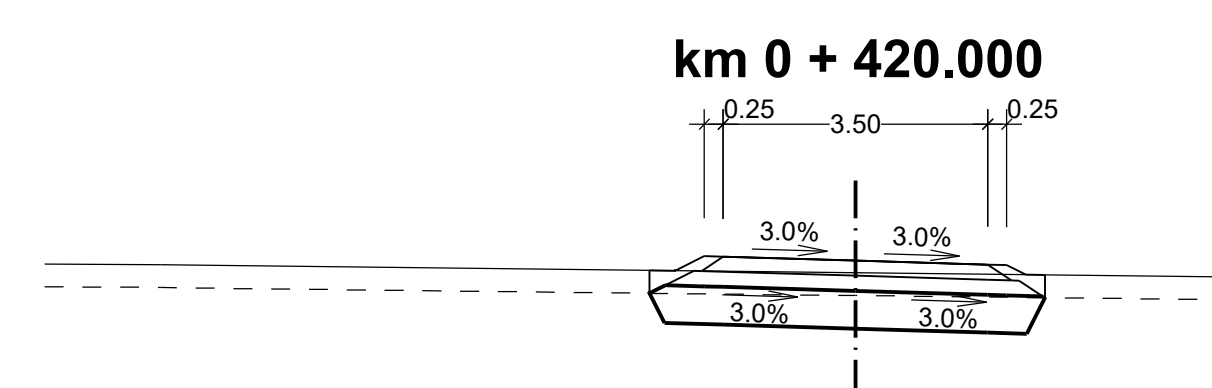

PROJEKTOVANÝ STAV	S. R. 220 m
ODSAZENÍ OD OSY	-2.72 223.13 -2.72 223.43 -2.36 223.43 -2.00 223.61 -1.75 223.61
STÁVAJÍCÍ TERÉN	0.00 223.40
ODSAZENÍ OD OSY	1.75 223.51 2.00 223.50 2.25 223.37 2.51 223.37 2.51 223.07

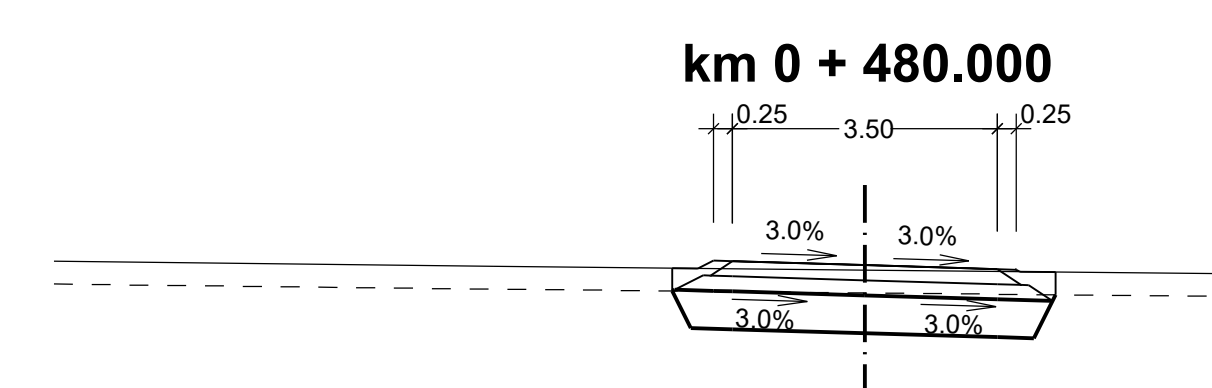

PROJEKTOVANÝ STAV	S. R. 220 m
ODSAZENÍ OD OSY	-2.54 223.16 -2.54 223.46 -2.21 223.46 -2.00 223.55 -1.75 223.55
STÁVAJÍCÍ TERÉN	0.00 223.43
ODSAZENÍ OD OSY	1.75 223.45 2.00 223.44 2.06 223.41 2.52 223.11 2.52 223.11

Výškový systém: Bpv

SO 153 Přístupy na pozemky k.ú. Sukorady u Mladé Boleslavi

**ŘEDITELSTVÍ
SILNIC
A DÁLNIC**

Ředitelství silnic a dálnic s. p.
Čerčanská 2023/12, Krč, 140 00 Praha 4

Valbek, spol. s r.o.
Vaňurova 505/17
460 07 Liberec 3

HIP:
ING. T. KLIMENT

Valbek

1/16 MLADÁ BOLESLAV - MARTINOVICE

5.1.1

Vypracoval: ING. A. DUMANSKA
Zodp. projektant: ING. T. KLIMENT
Tech. kontrola: ING. M. HANŽL
Akce: I/16 MLADÁ BOLESLAV - MARTINOVICE

Zak. číslo: 21-L113-001
Datum: 02/2025
Stupeň: PDPS
Počet formátů: 16 x A4
Měřítko: 1:100
Č. přílohy: Pare