




SO 153 - PŘÍSTUPY NA POZEMKY k.ú. SUKORADY U MLADÉ BOLESLAVI
PŘÍČNÉ ŘEZY SO 153.1 - km 0,500 - 0,960, M 1 : 100

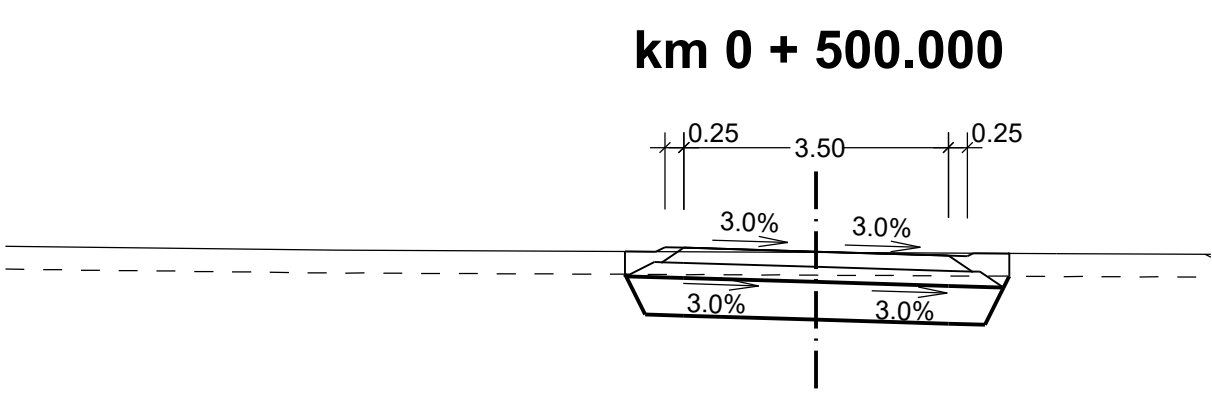


PROJEKTOVANÝ STAV	S. R. 220 m
ODSAZENÍ OD OSY	-2.53 223.18 -2.53 223.48 -2.53 223.50 -2.00 223.52 -1.75 223.53
STÁVAJÍCÍ TERÉN	1.75 223.43 2.00 223.46 2.08 223.46 2.27 223.43 2.55 223.45 2.95 223.15
ODSAZENÍ OD OSY	0.00 223.47 3.18 223.45

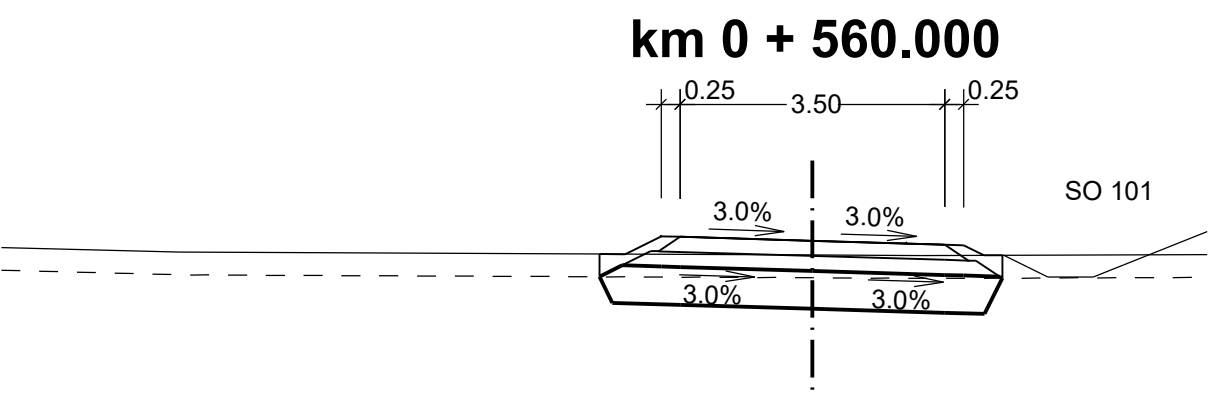


PROJEKTOVANÝ STAV	S. R. 220 m
ODSAZENÍ OD OSY	-2.82 223.15 -2.82 223.45 -2.47 223.45 -2.00 223.68 -1.75 223.68
STÁVAJÍCÍ TERÉN	0.00 223.62 1.75 223.57 2.00 223.56 2.27 223.43 2.55 223.43 2.92 223.13
ODSAZENÍ OD OSY	0.00 223.43 1.45 223.43

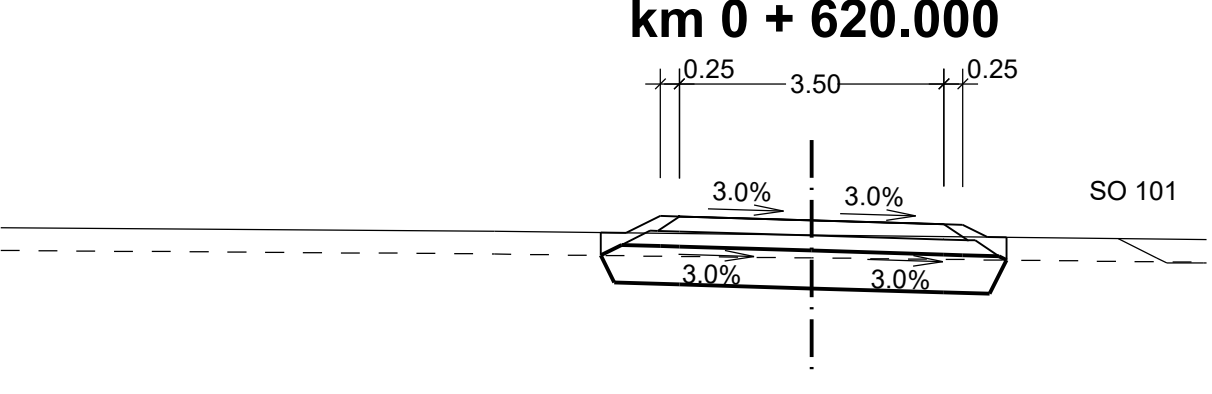


PROJEKTOVANÝ STAV	S. R. 220 m
ODSAZENÍ OD OSY	-2.79 223.43 -2.79 223.73 -2.82 223.73 -2.00 223.95 -1.75 223.95
STÁVAJÍCÍ TERÉN	0.00 223.89 1.75 223.84 2.00 223.83 2.30 223.83 2.58 223.67 2.98 223.37
ODSAZENÍ OD OSY	-4.19 223.75 0.00 223.70

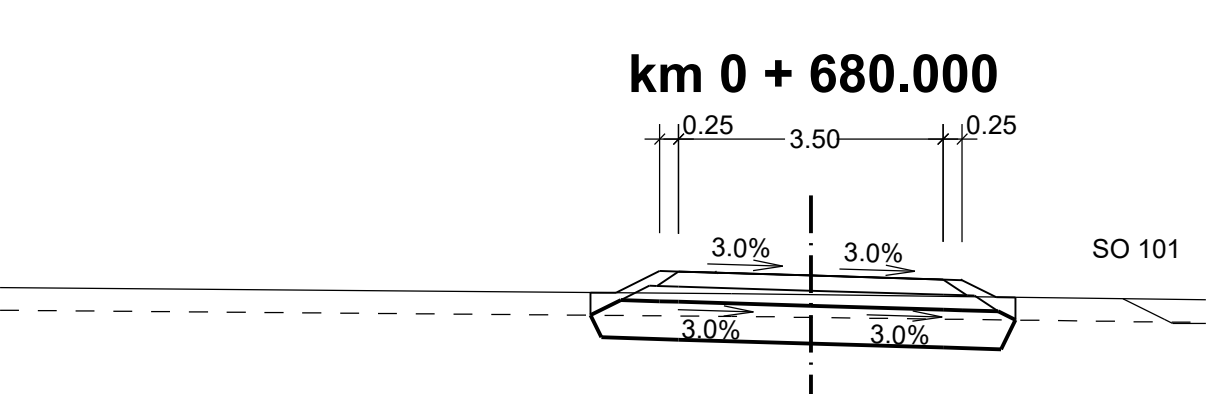


PROJEKTOVANÝ STAV	S. R. 221 m
ODSAZENÍ OD OSY	-2.69 223.84 -2.69 224.08 -2.82 224.37 -2.00 224.22 -1.75 224.22
STÁVAJÍCÍ TERÉN	0.00 224.16 1.75 224.11 2.00 224.10 2.45 223.88 2.71 223.87 2.71 223.57
ODSAZENÍ OD OSY	-1.05 223.92 0.00 223.91

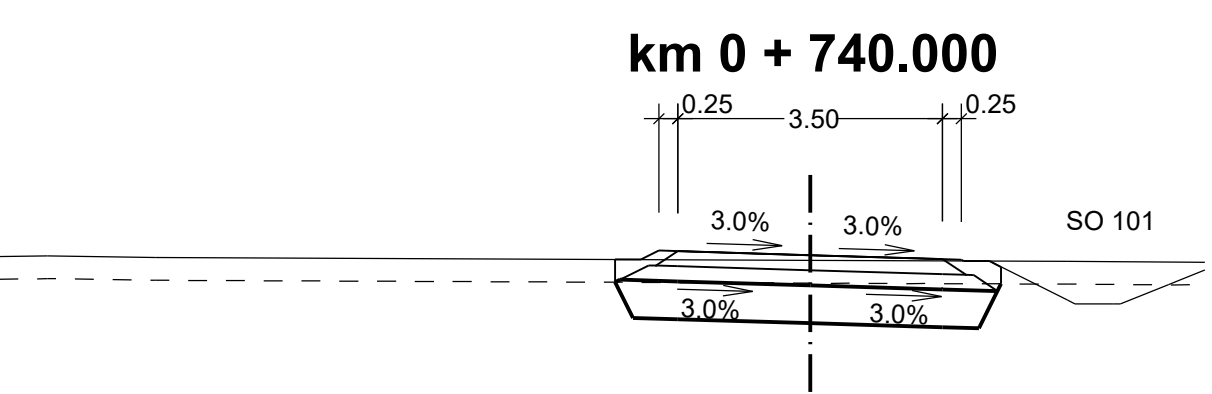


PROJEKTOVANÝ STAV	S. R. 221 m
ODSAZENÍ OD OSY	-2.58 224.08 -2.58 224.37 -2.84 224.37 -2.00 224.49 -1.75 224.49
STÁVAJÍCÍ TERÉN	0.00 224.43 1.75 224.38 2.00 224.37 2.53 224.35 2.53 224.05
ODSAZENÍ OD OSY	3.41 224.35

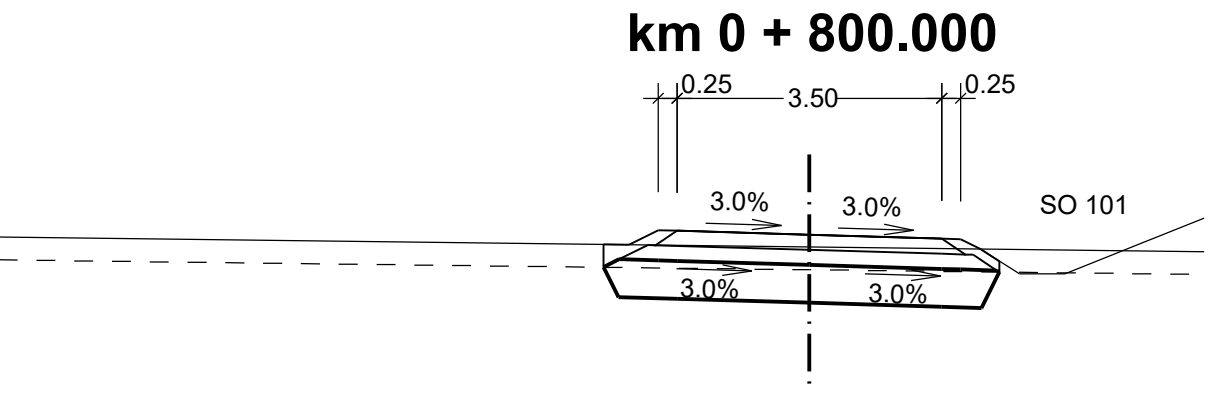


PROJEKTOVANÝ STAV	S. R. 221 m
ODSAZENÍ OD OSY	-2.72 224.27 -2.72 224.57 -2.80 224.76 -2.00 224.76 -1.75 224.76
STÁVAJÍCÍ TERÉN	0.00 224.70 1.75 224.65 2.00 224.65 2.26 224.51 2.51 224.21
ODSAZENÍ OD OSY	0.00 224.54

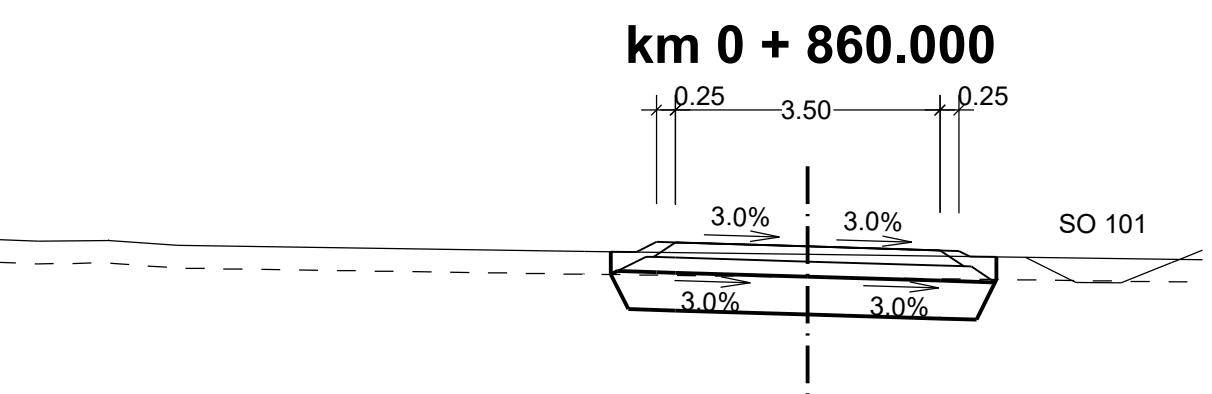


PROJEKTOVANÝ STAV	S. R. 221 m
ODSAZENÍ OD OSY	-2.60 224.18 -2.60 224.48 -2.27 224.47 -2.00 224.61 -1.75 224.60
STÁVAJÍCÍ TERÉN	0.00 224.55 1.75 224.50 2.00 224.49 2.15 224.41 2.50 224.11
ODSAZENÍ OD OSY	-2.96 224.48 0.00 224.44

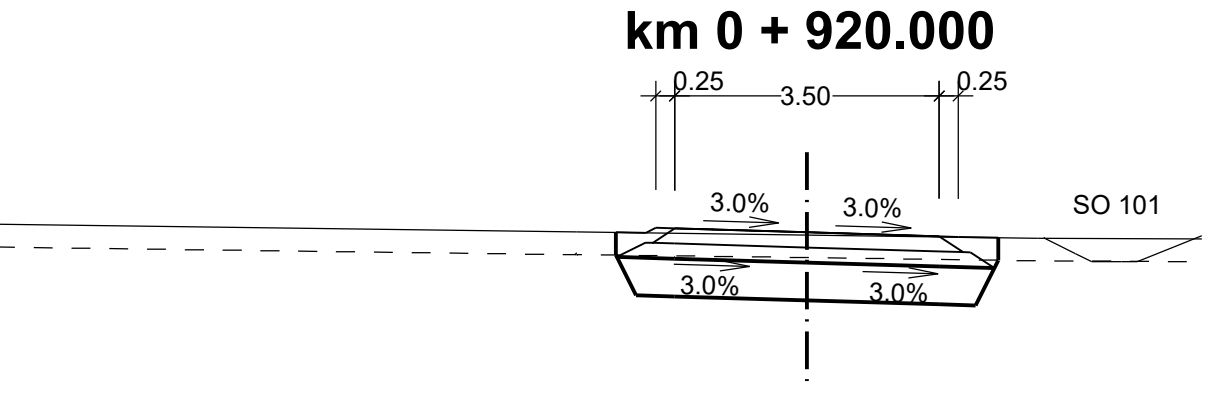


PROJEKTOVANÝ STAV	S. R. 221 m
ODSAZENÍ OD OSY	-2.53 224.43 -2.53 224.73 -2.53 224.73 -2.00 224.79 -1.75 224.79
STÁVAJÍCÍ TERÉN	0.00 224.73 1.75 224.68 2.00 224.68 2.53 224.36
ODSAZENÍ OD OSY	-3.05 224.74 0.00 224.70 3.05 224.66

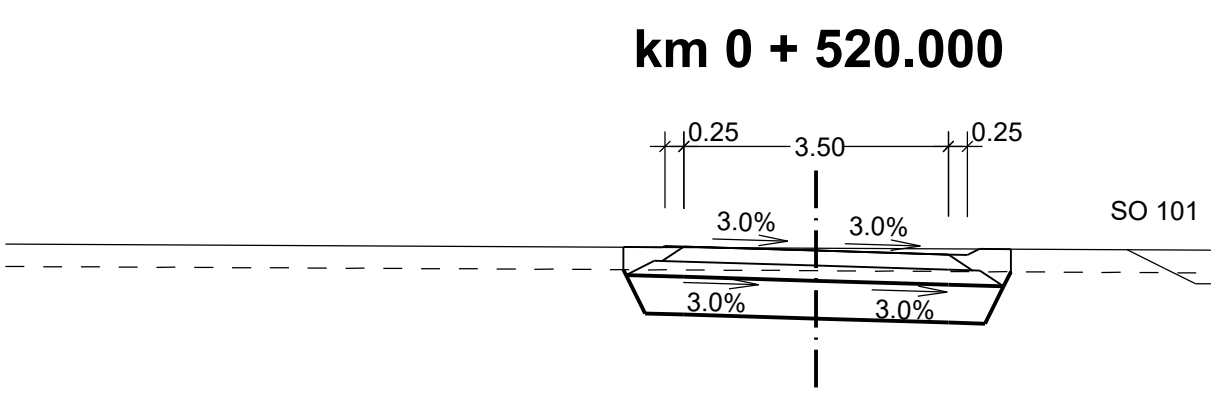


PROJEKTOVANÝ STAV	S. R. 220 m
ODSAZENÍ OD OSY	-2.55 223.20 -2.55 223.49 -2.55 223.50 -2.00 223.52 -1.75 223.51
STÁVAJÍCÍ TERÉN	0.00 223.49 1.75 223.41 2.00 223.40 2.16 223.48 2.58 223.18
ODSAZENÍ OD OSY	0.00 223.46

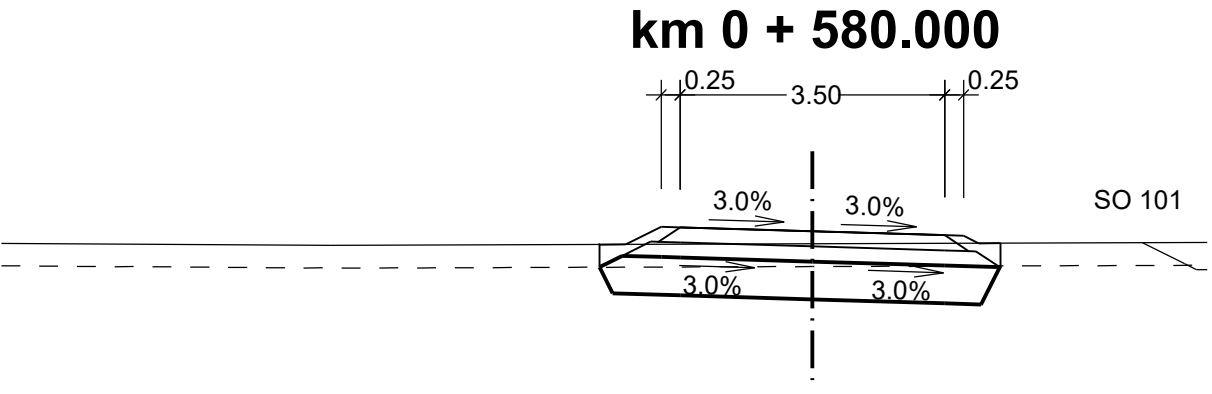


PROJEKTOVANÝ STAV	S. R. 220 m
ODSAZENÍ OD OSY	-2.82 223.24 -2.82 223.54 -2.47 223.54 -2.00 223.77 -1.75 223.77
STÁVAJÍCÍ TERÉN	0.00 223.71 1.75 223.66 2.00 223.65 2.20 223.55 2.48 223.25
ODSAZENÍ OD OSY	0.00 223.55

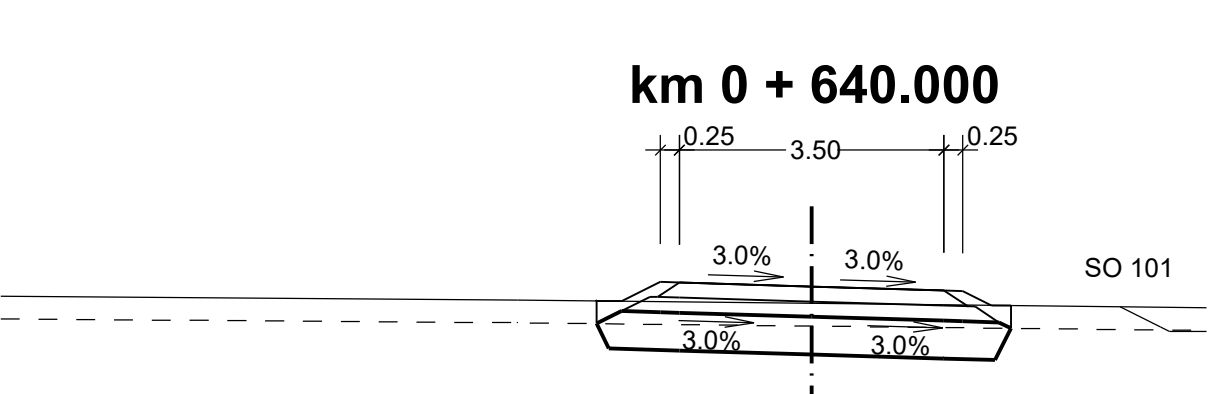


PROJEKTOVANÝ STAV	S. R. 221 m
ODSAZENÍ OD OSY	-2.85 223.49 -2.85 223.79 -2.60 224.01 -2.00 224.04 -1.75 224.04
STÁVAJÍCÍ TERÉN	0.00 223.98 1.75 223.93 2.00 223.92 2.36 223.73 2.64 223.43
ODSAZENÍ OD OSY	-3.89 223.80 0.00 223.76

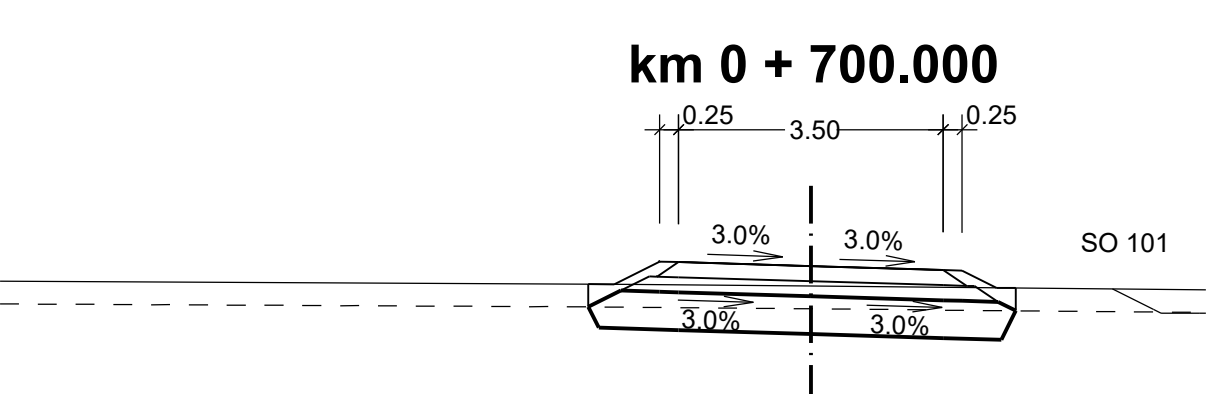


PROJEKTOVANÝ STAV	S. R. 221 m
ODSAZENÍ OD OSY	-2.65 224.01 -2.65 224.31 -2.60 224.31 -2.00 224.31 -1.75 224.31
STÁVAJÍCÍ TERÉN	0.00 224.25 1.75 224.20 2.00 224.19 2.46 223.96 2.71 223.96 2.71 223.66
ODSAZENÍ OD OSY	-2.38 224.01 0.00 224.29

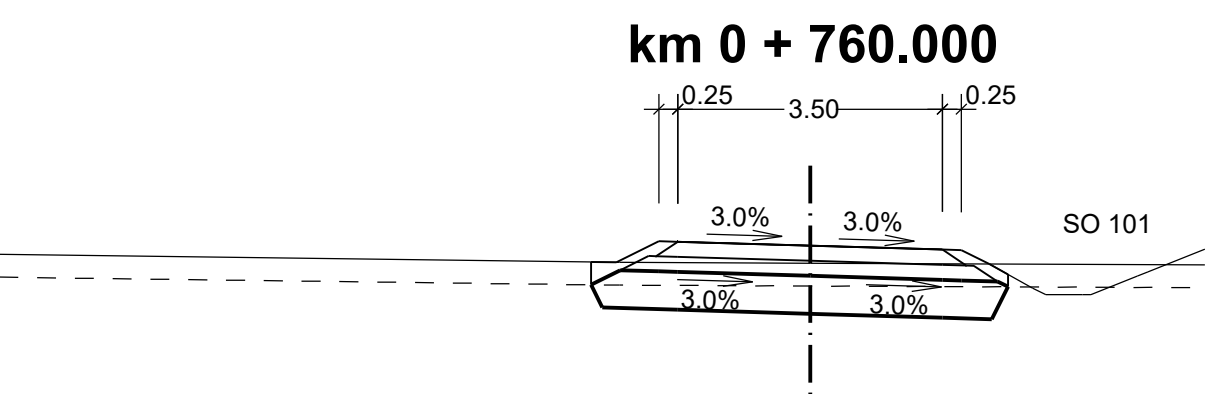


PROJEKTOVANÝ STAV	S. R. 221 m
ODSAZENÍ OD OSY	-2.90 224.01 -2.90 224.31 -2.58 224.30 -2.00 224.68 -1.75 224.68
STÁVAJÍCÍ TERÉN	0.00 224.52 1.75 224.47 2.00 224.46 2.53 224.35 2.62 224.28 2.62 223.98
ODSAZENÍ OD OSY	-2.62 224.30 0.00 224.77

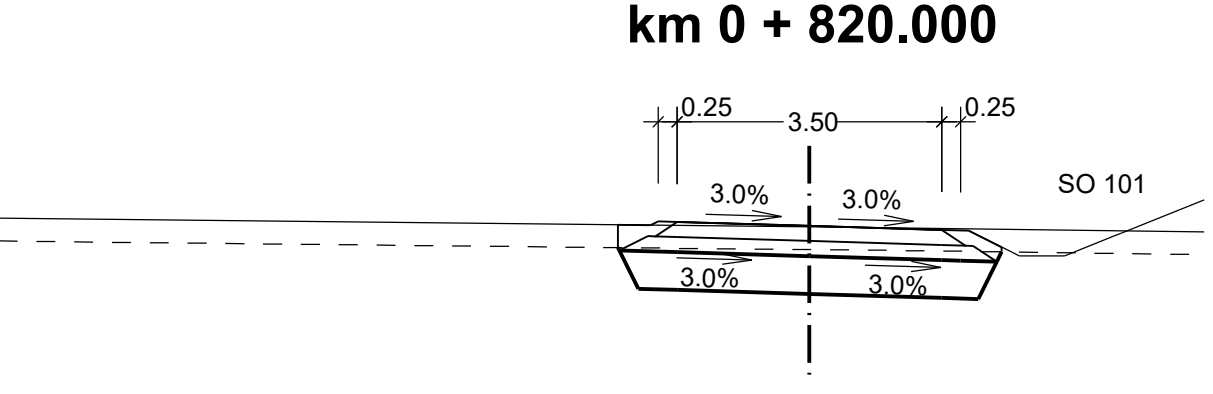


PROJEKTOVANÝ STAV	S. R. 221 m
ODSAZENÍ OD OSY	-2.53 224.50 -2.53 224.80 -2.33 224.80 -2.00 224.84 -1.75 224.84
STÁVAJÍCÍ TERÉN	0.00 224.78 1.75 224.73 2.00 224.72 2.05 224.75 2.54 224.74 2.54 224.44
ODSAZENÍ OD OSY	1.63 224.75 0.00 224.36

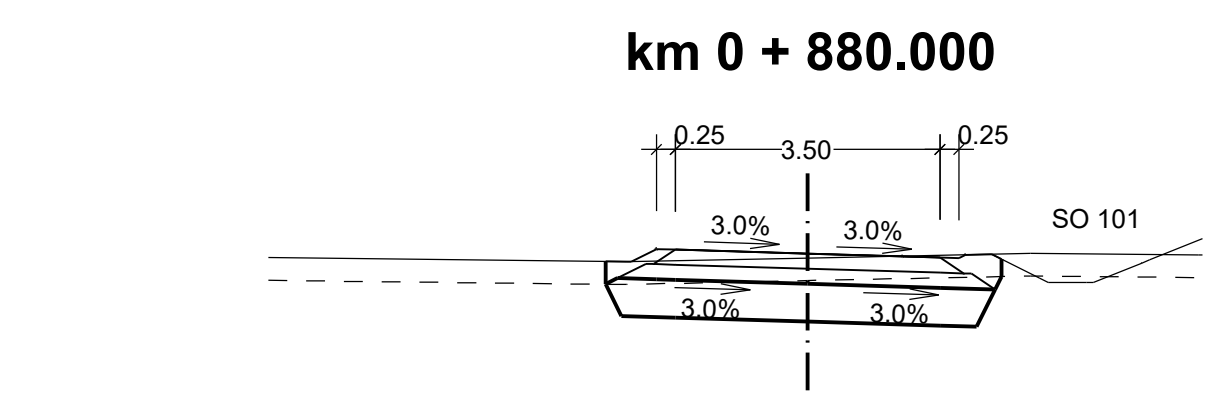


PROJEKTOVANÝ STAV	S. R. 221 m
ODSAZENÍ OD OSY	-2.67 224.01 -2.67 224.31 -2.33 224.31 -2.00 224.47 -1.75 224.47
STÁVAJÍCÍ TERÉN	0.00 224.42 1.75 224.37 2.00 224.36 2.08 224.40 2.56 224.11
ODSAZENÍ OD OSY	-2.40 224.31 0.00 224.36

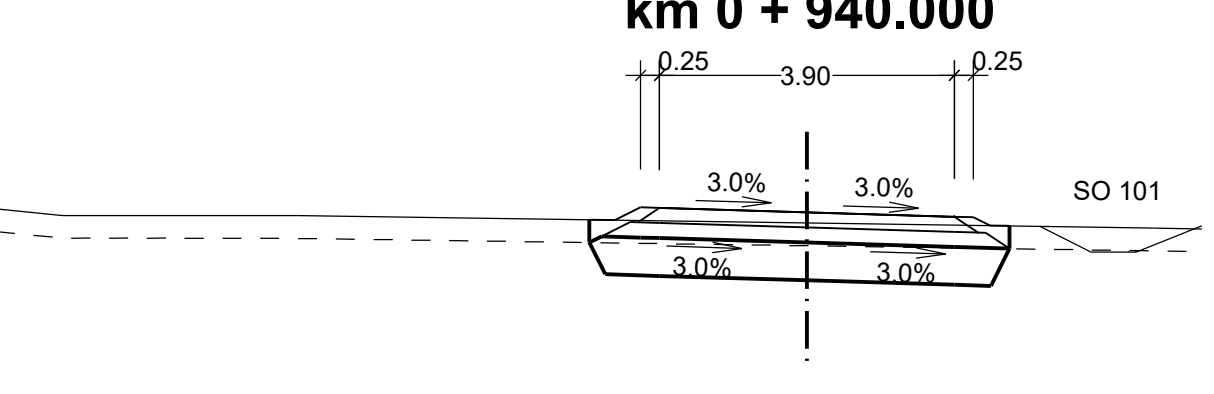


PROJEKTOVANÝ STAV	S. R. 221 m
ODSAZENÍ OD OSY	-2.88 224.56 -2.88 224.86 -2.54 224.86 -2.20 225.03 -1.95 225.02
STÁVAJÍCÍ TERÉN	0.00 224.96 1.95 224.91 2.20 224.90 2.48 224.79 2.68 224.48
ODSAZENÍ OD OSY	0.00 224.82 4.57 224.76

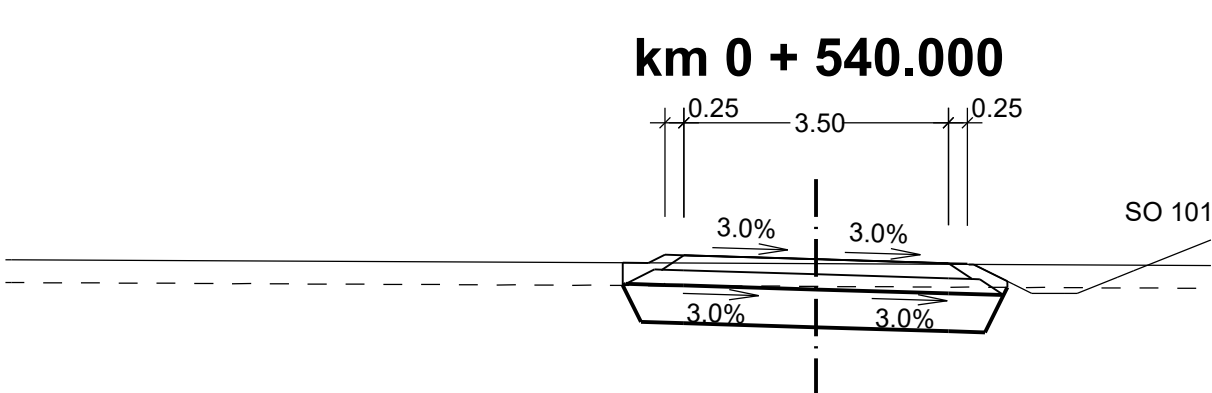


PROJEKTOVANÝ STAV	S. R. 220 m
ODSAZENÍ OD OSY	-2.56 223.19 -2.56 223.49 -2.56 223.50 -2.00 223.59 -1.75 223.59
STÁVAJÍCÍ TERÉN	0.00 223.47 1.75 223.48 2.02 223.46 2.53 223.46 2.83 223.16
ODSAZENÍ OD OSY	0.00 223.47

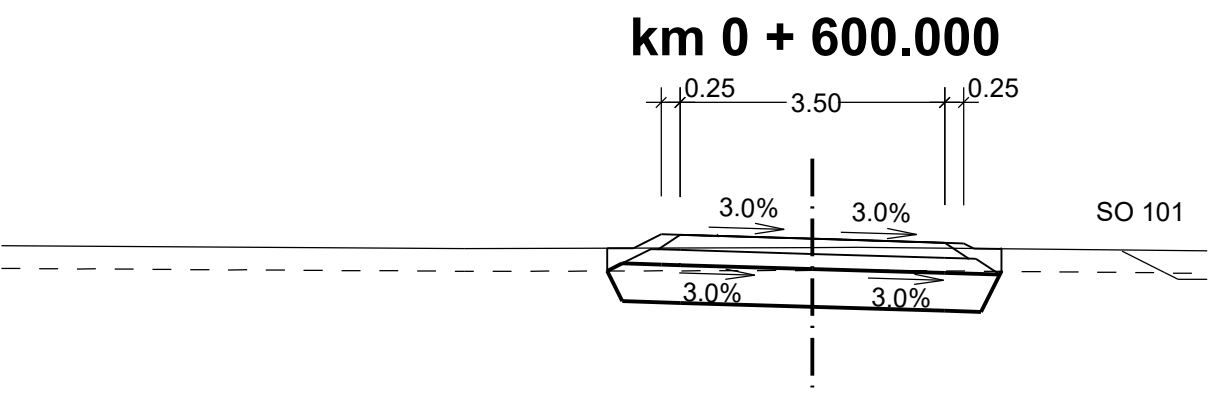


PROJEKTOVANÝ STAV	S. R. 220 m
ODSAZENÍ OD OSY	-2.72 223.38 -2.72 223.68 -2.37 223.68 -2.00 223.86 -1.75 223.86
STÁVAJÍCÍ TERÉN	0.00 223.80 1.75 223.75 2.00 223.74 2.14 223.67 2.50 223.37
ODSAZENÍ OD OSY	-4.60 223.67 0.00 223.69

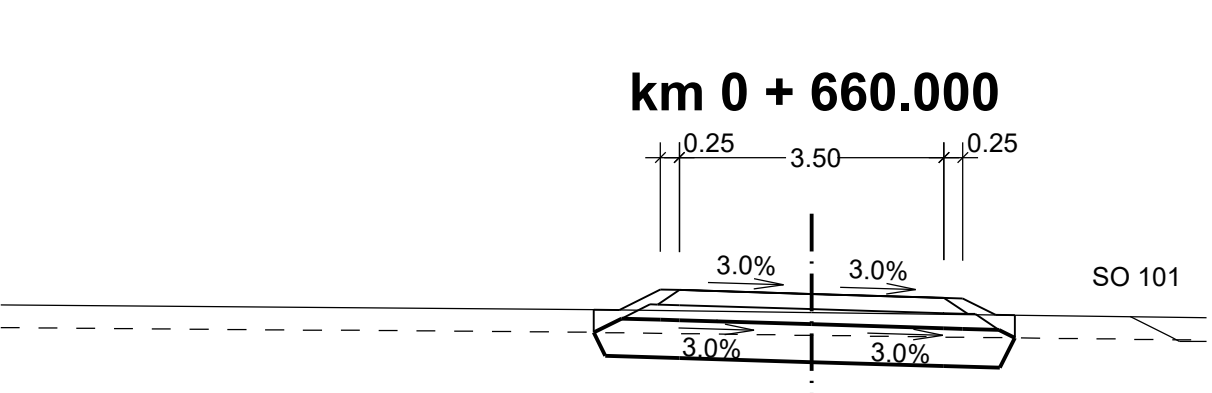


PROJEKTOVANÝ STAV	S. R. 221 m
ODSAZENÍ OD OSY	-2.88 223.56 -2.88 223.86 -2.60 224.08 -2.00 224.13 -1.75 224.13
STÁVAJÍCÍ TERÉN	0.00 224.07 1.75 224.02 2.00 224.28 2.36 223.80 2.69 223.49
ODSAZENÍ OD OSY	-2.75 223.86 0.00 223.83

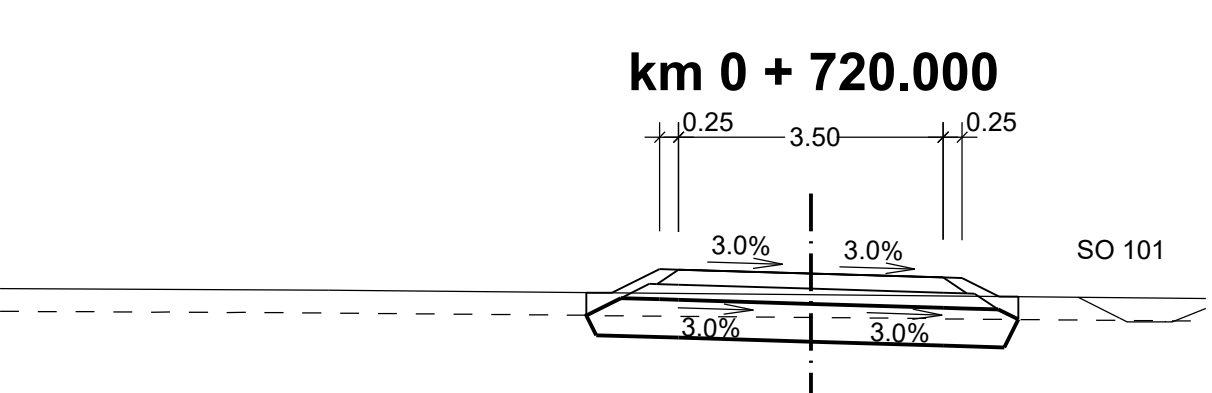


PROJEKTOVANÝ STAV	S. R. 221 m
ODSAZENÍ OD OSY	-2.67 223.70 -2.67 224.00 -2.60 224.09 -2.00 224.40 -1.75 224.40
STÁVAJÍCÍ TERÉN	0.00 224.34 1.75 224.29 2.00 224.28 2.49 224.04 2.74 223.74
ODSAZENÍ OD OSY	-2.75 223.86 0.00 224.06

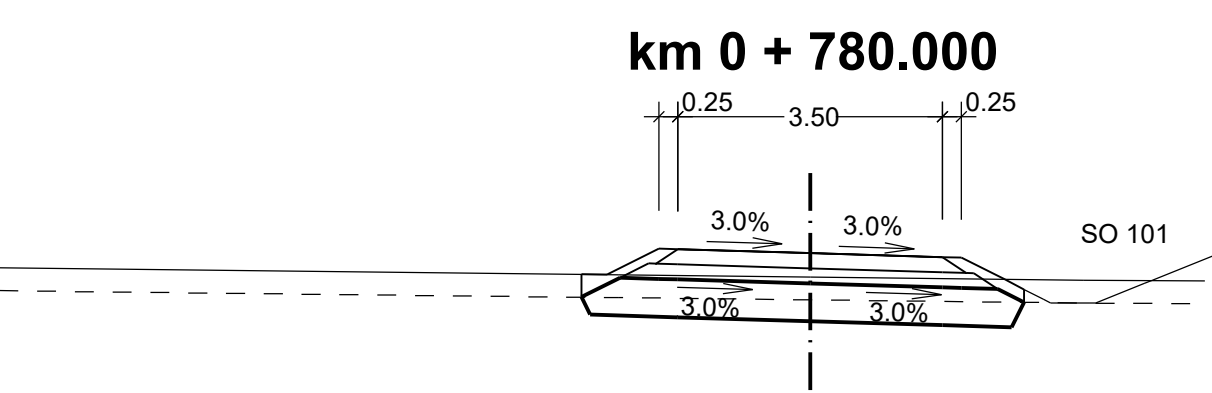


PROJEKTOVANÝ STAV	S. R. 221 m
ODSAZENÍ OD OSY	-3.03 224.03 -3.03 224.33 -2.69 224.33 -2.00 224.67 -1.75 224.67
STÁVAJÍCÍ TERÉN	0.00 224.61 1.75 224.56 2.00 224.55 2.09 224.57 2.51 224.27
ODSAZENÍ OD OSY	-2.53 224.33 0.00 224.30

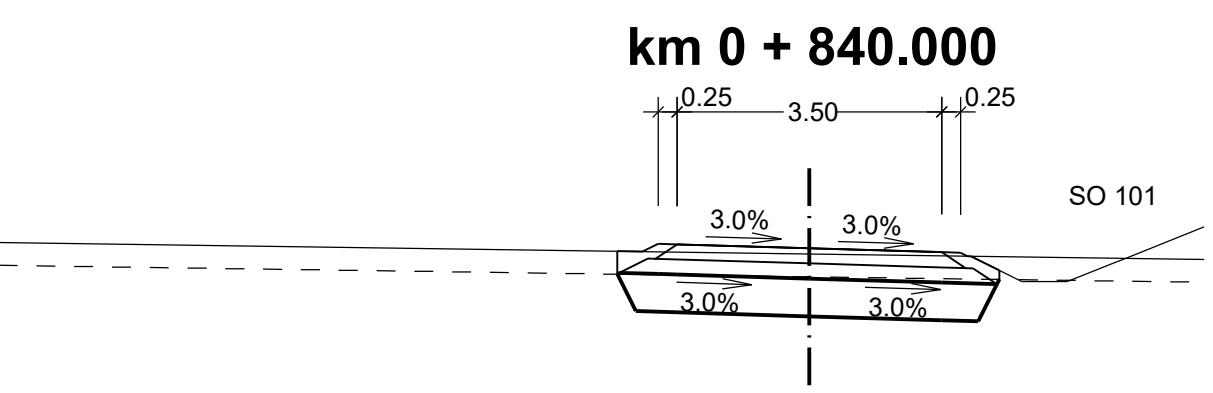

PROJEKTOVANÝ STAV	S. R. 221 m
ODSAZENÍ OD OSY	-2.54 224.34 -2.54 224.64 -2.40 224.64 -2.00 224.74 -1.75 224.73
STÁVAJÍCÍ TERÉN	0.00 224.68 1.75 224.63 2.00 224.62 2.09 224.57 2.51 224.27
ODSAZENÍ OD OSY	3.62 224.25 0.00 224.60

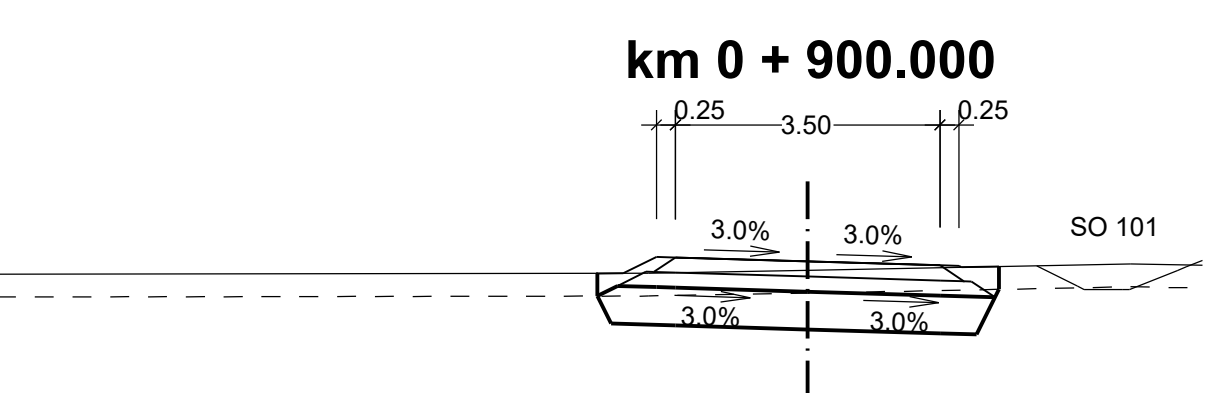

PROJEKTOVANÝ STAV	S. R. 221 m
ODSAZENÍ OD OSY	-2.78 224.05 -2.78 224.35 -3.40 224.35 -2.00 224.56 -1.75 224.56
STÁVAJÍCÍ TERÉN	0.00 224.50 1.75 224.45 2.00 224.44 2.04 224.43 2.53 224.14
ODSAZENÍ OD OSY	-2.11 224.35 0.00 224.39

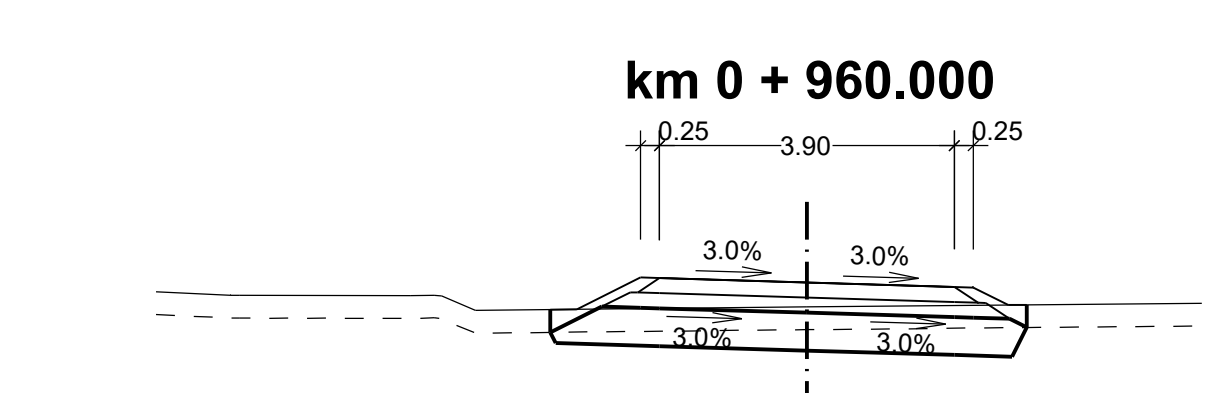

PROJEKTOVANÝ STAV	S. R. 222 m
ODSAZENÍ OD OSY	-4.93 225.06 -4.83 225.05 -4.39 224.86
STÁVAJÍCÍ TERÉN	0.00 225.22 1.95 225.17 2.20 225.16 2.66 224.93 2.81 224.63
ODSAZENÍ OD OSY	0.00 224.90

Výškový systém: Bpv

SO 153 Přístupy na pozemky k.ú. Sukorady u Mladé Boleslavi

ŘEDITELSTVÍ
SILNIC
A DÁLNIC

Ředitelství silnic a dálnic s. p.
Čerčanská 203/12, Krč, 140 00 Praha 4

Valbek

Valbek, spol. s r.o.
Vaňurova 505/17
460 07 Liberec 3

HIP:
ING. T. KLIMENT

Valbek

Vypracoval ING. A. DUMANSKA
Zodp. projektant ING. T. KLIMENT
Tech. kontrola ING. M. HANŽL
Akce I/16 MLADÁ BOLESLAV - MARTINOVICE
Příloha PŘÍČNÉ ŘEZY SO 153.1 - km 0,500 - 0,960

Zak. číslo 21-L113-001
Datum 02/2025
Stupeň PDPS
Počet formátů 16 x A4
Měřítko 1:100
Č. přílohy Pare

5.1.2