
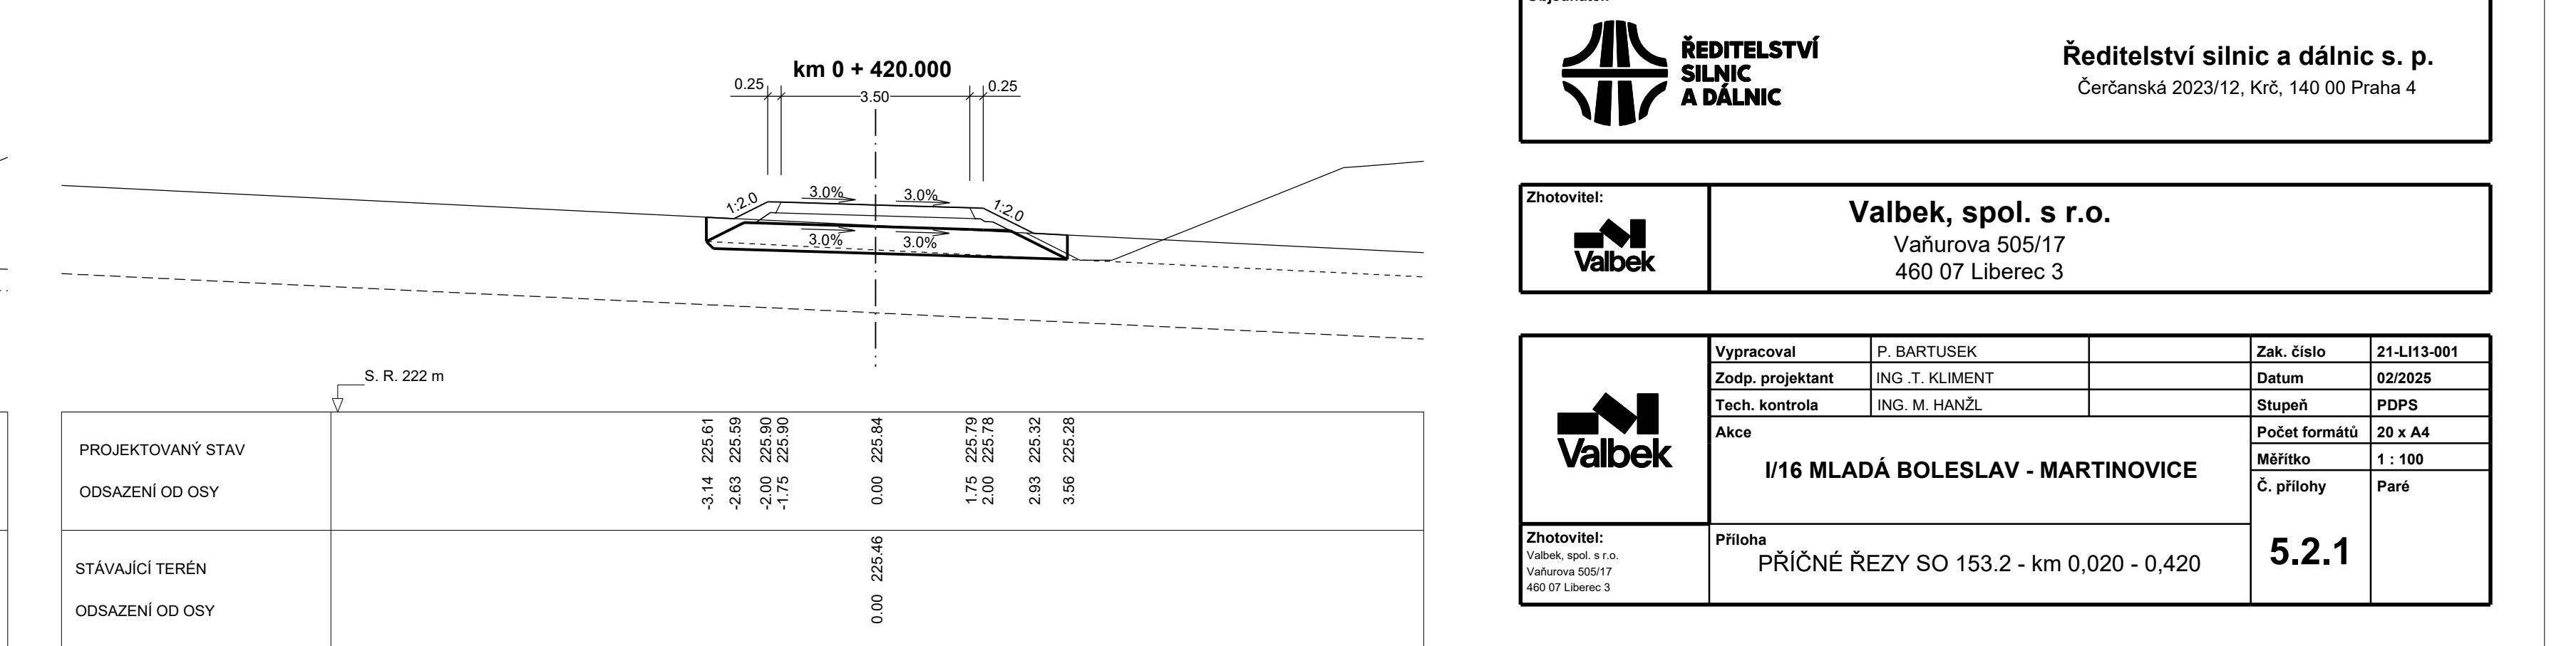
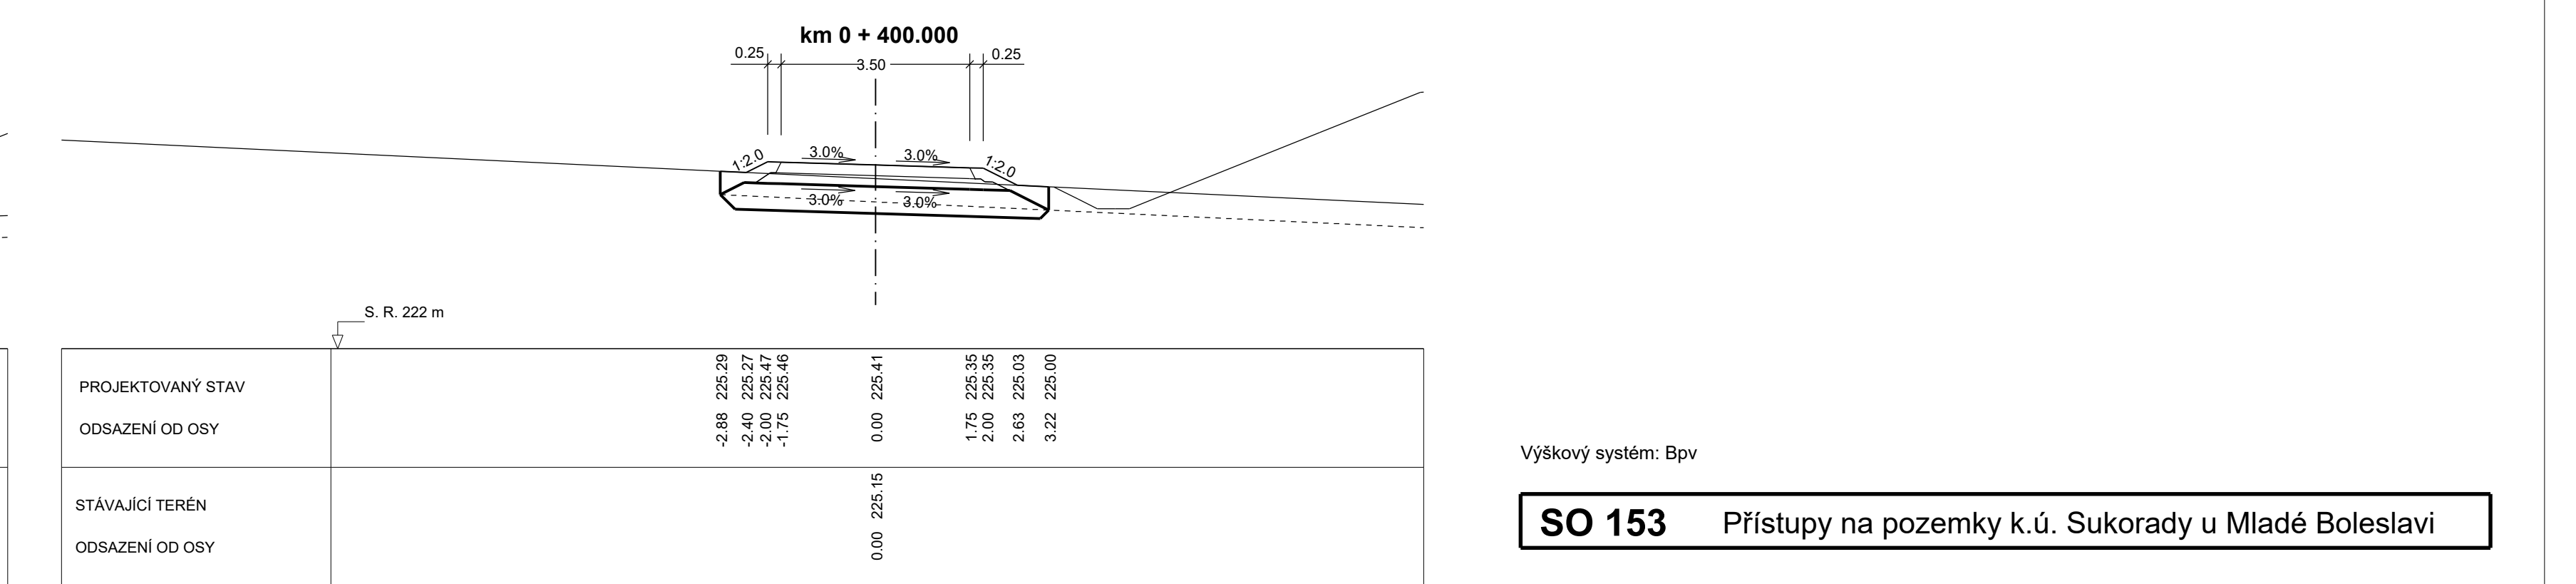
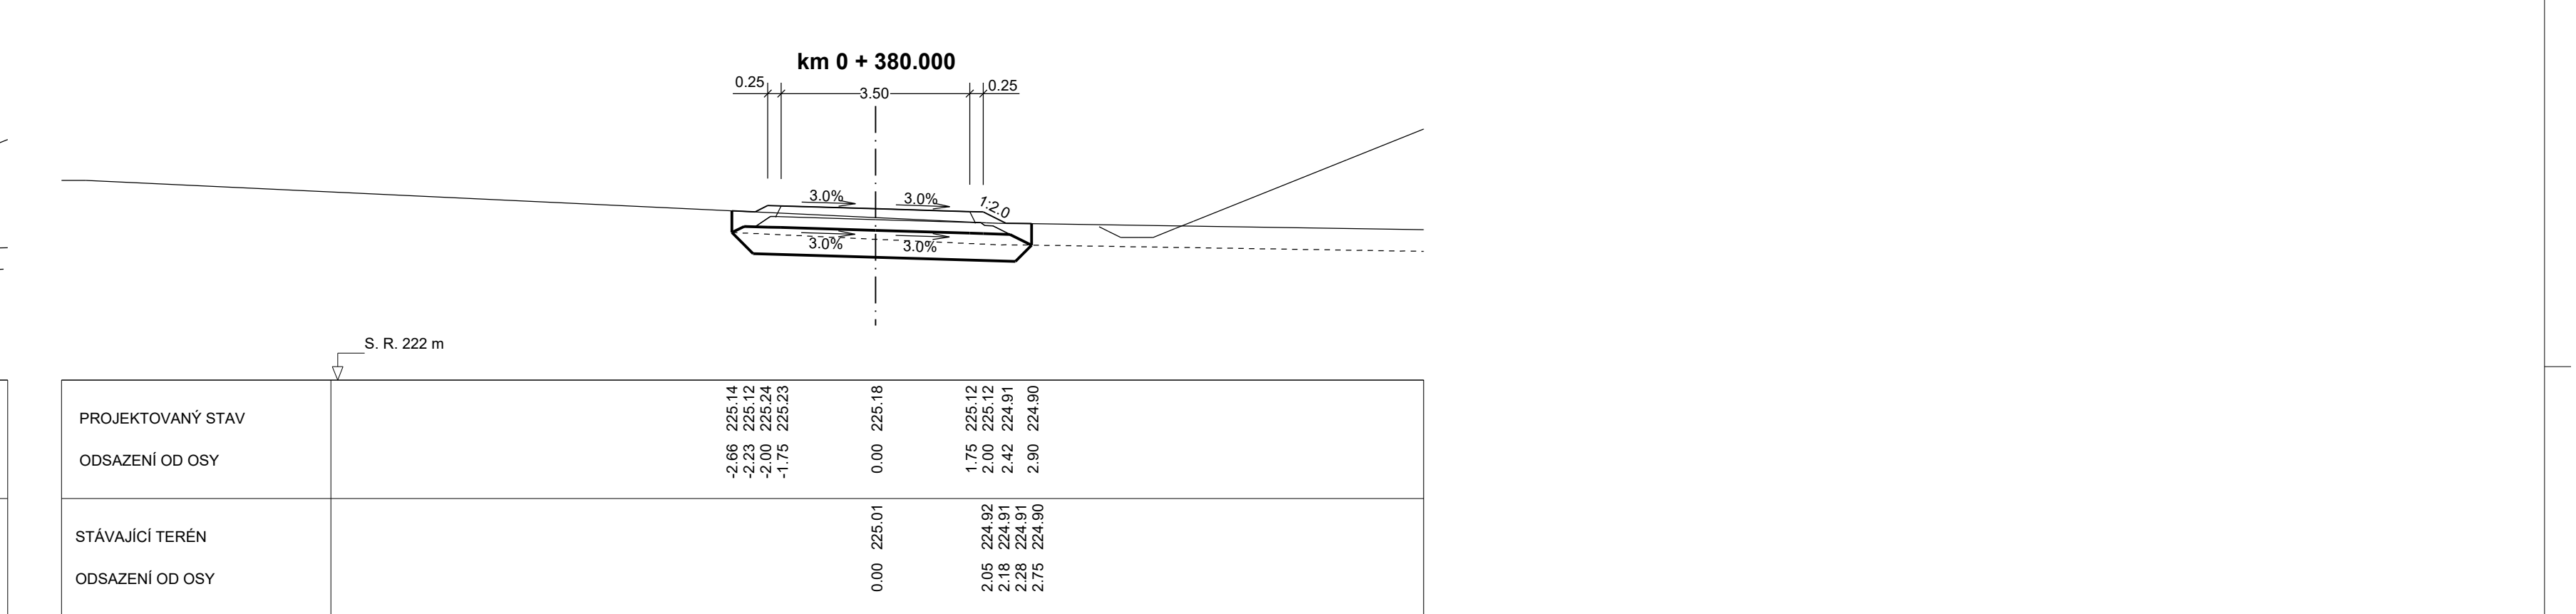
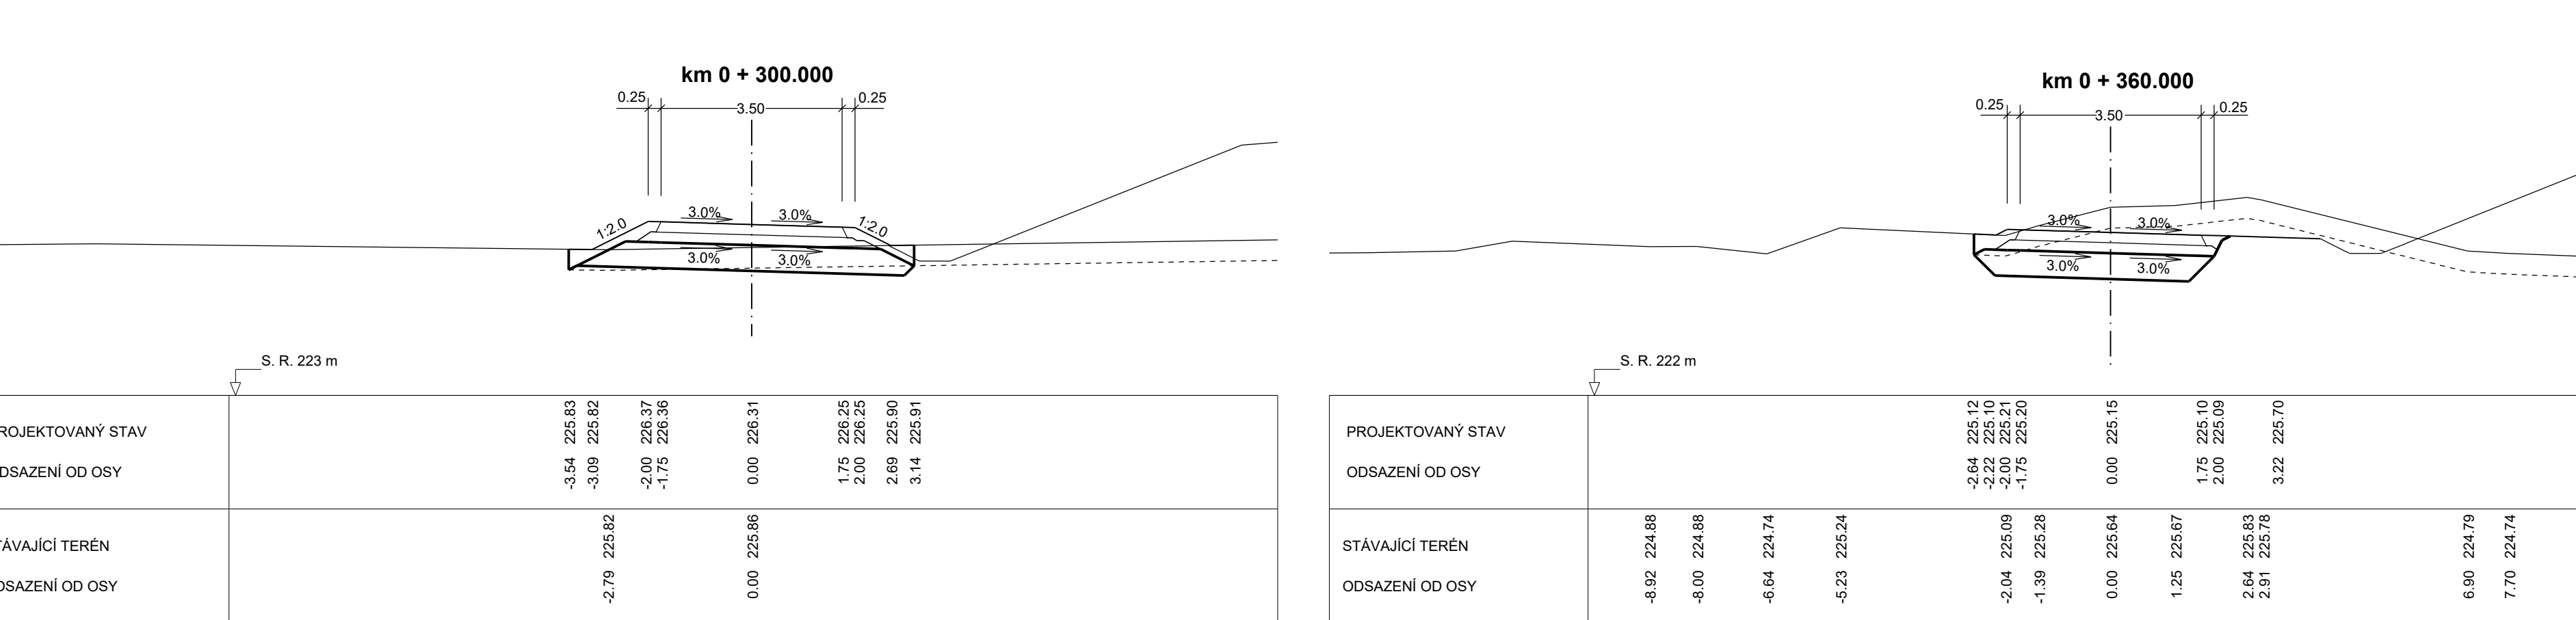
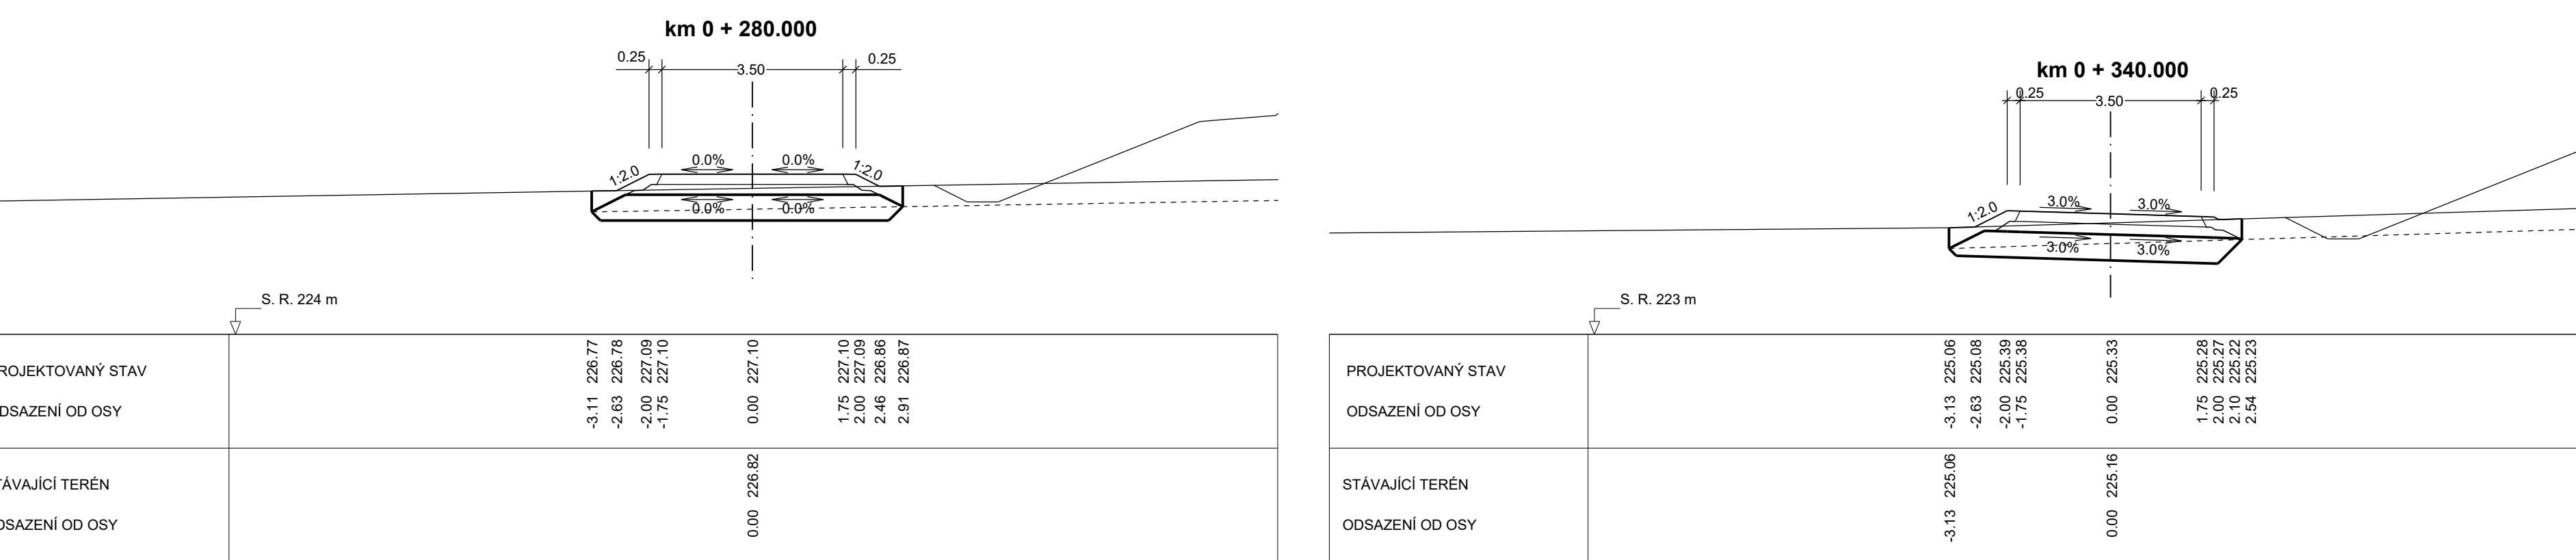
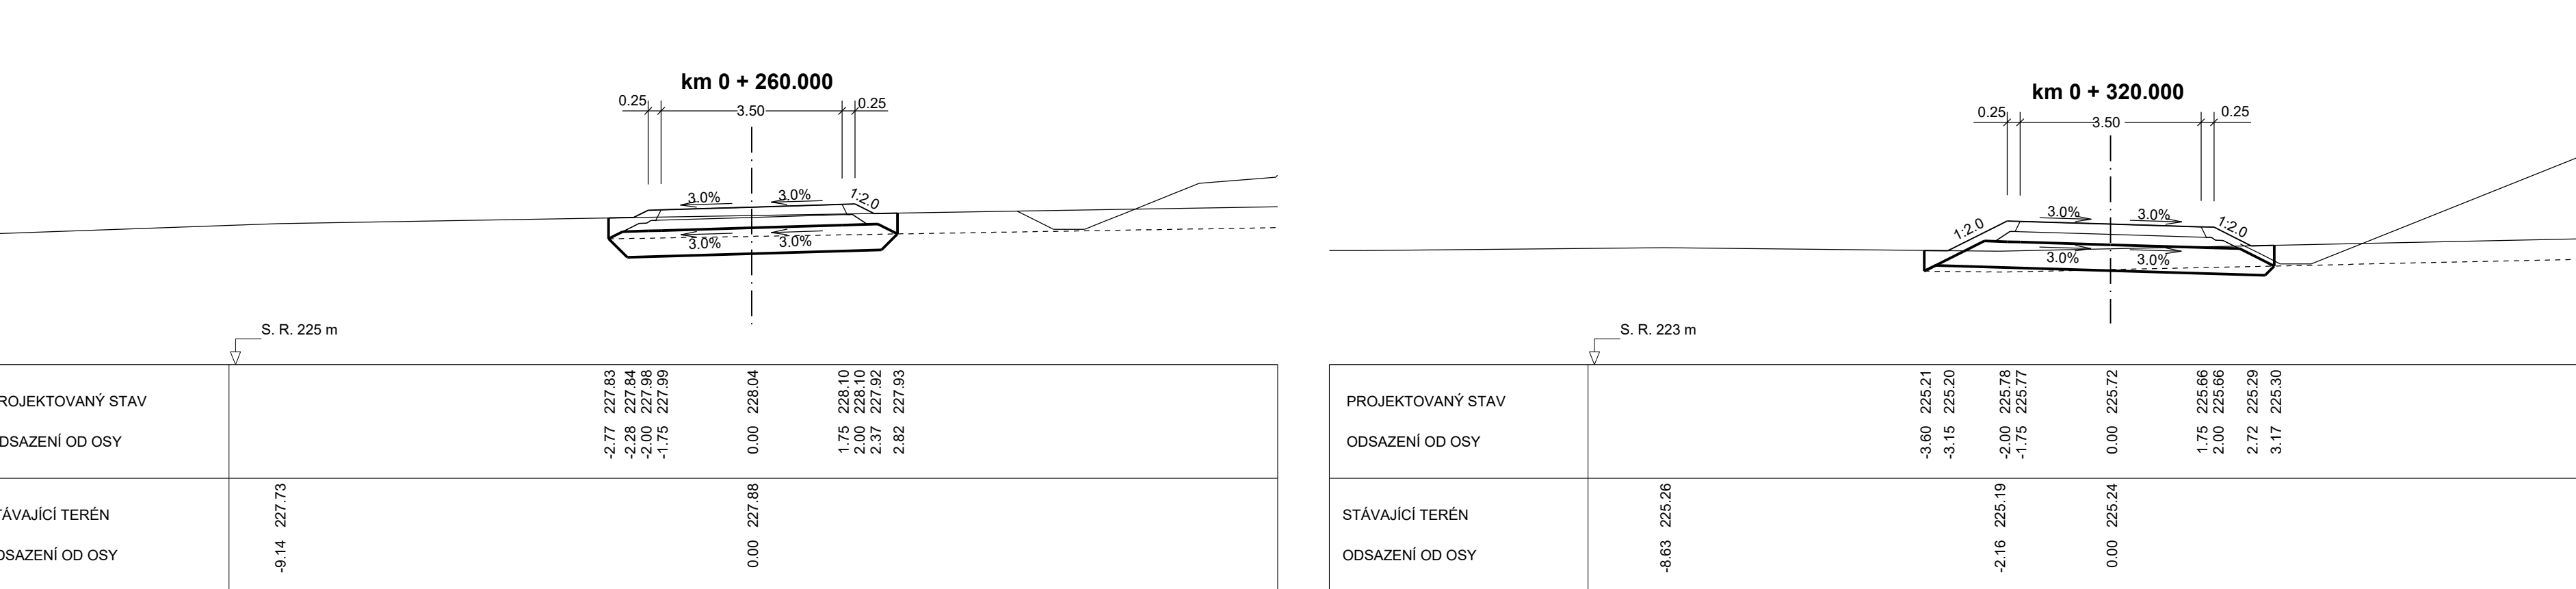
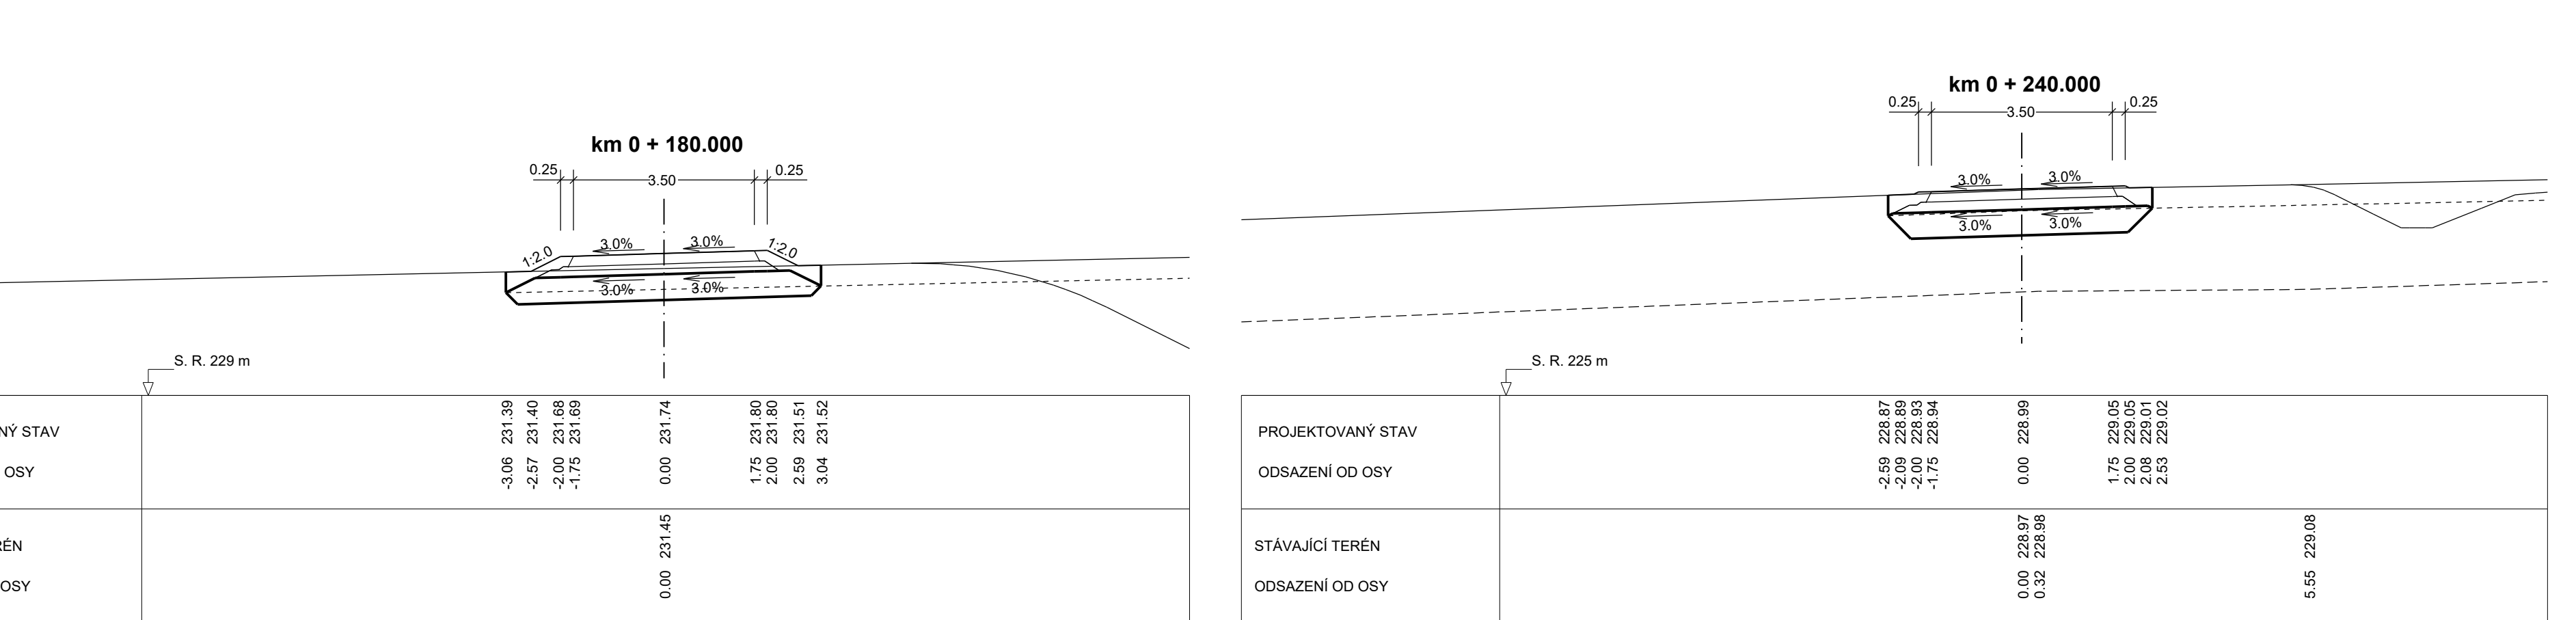
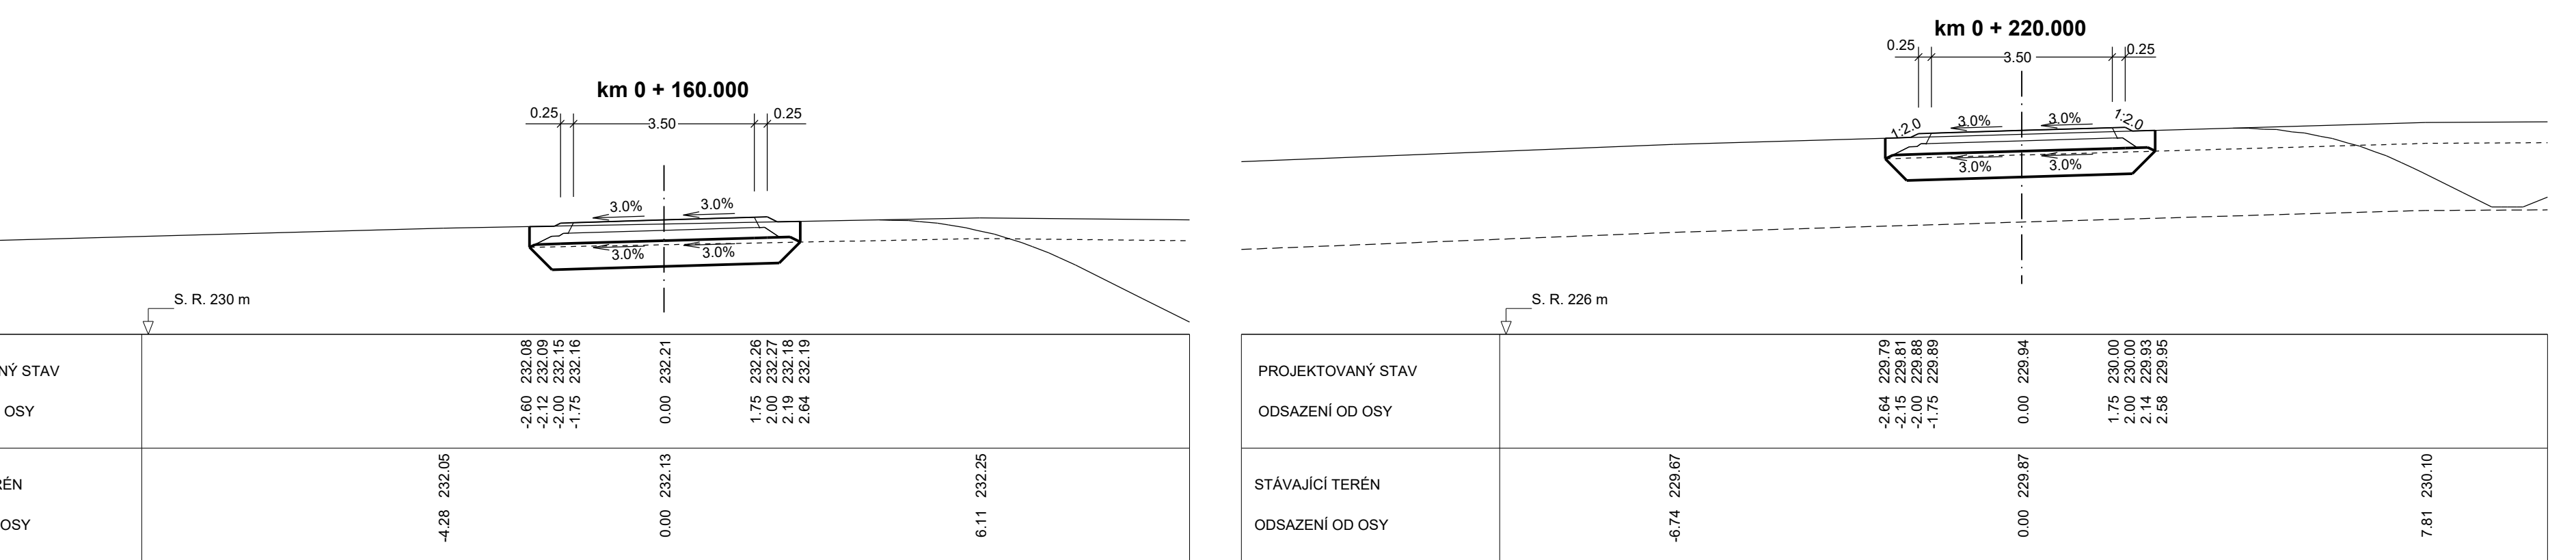
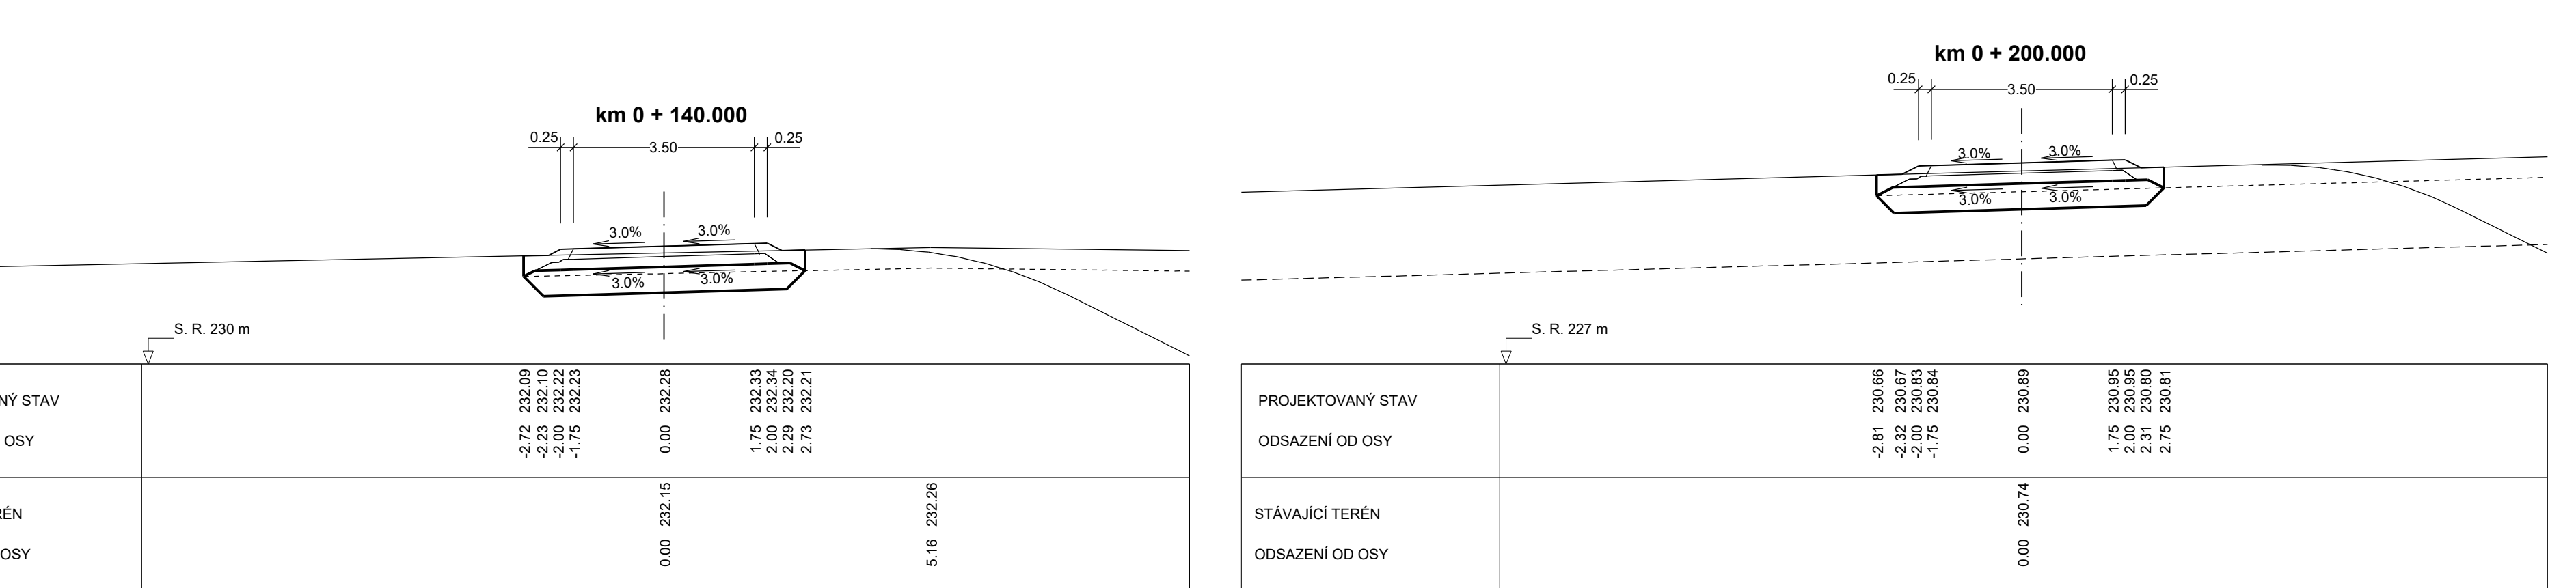
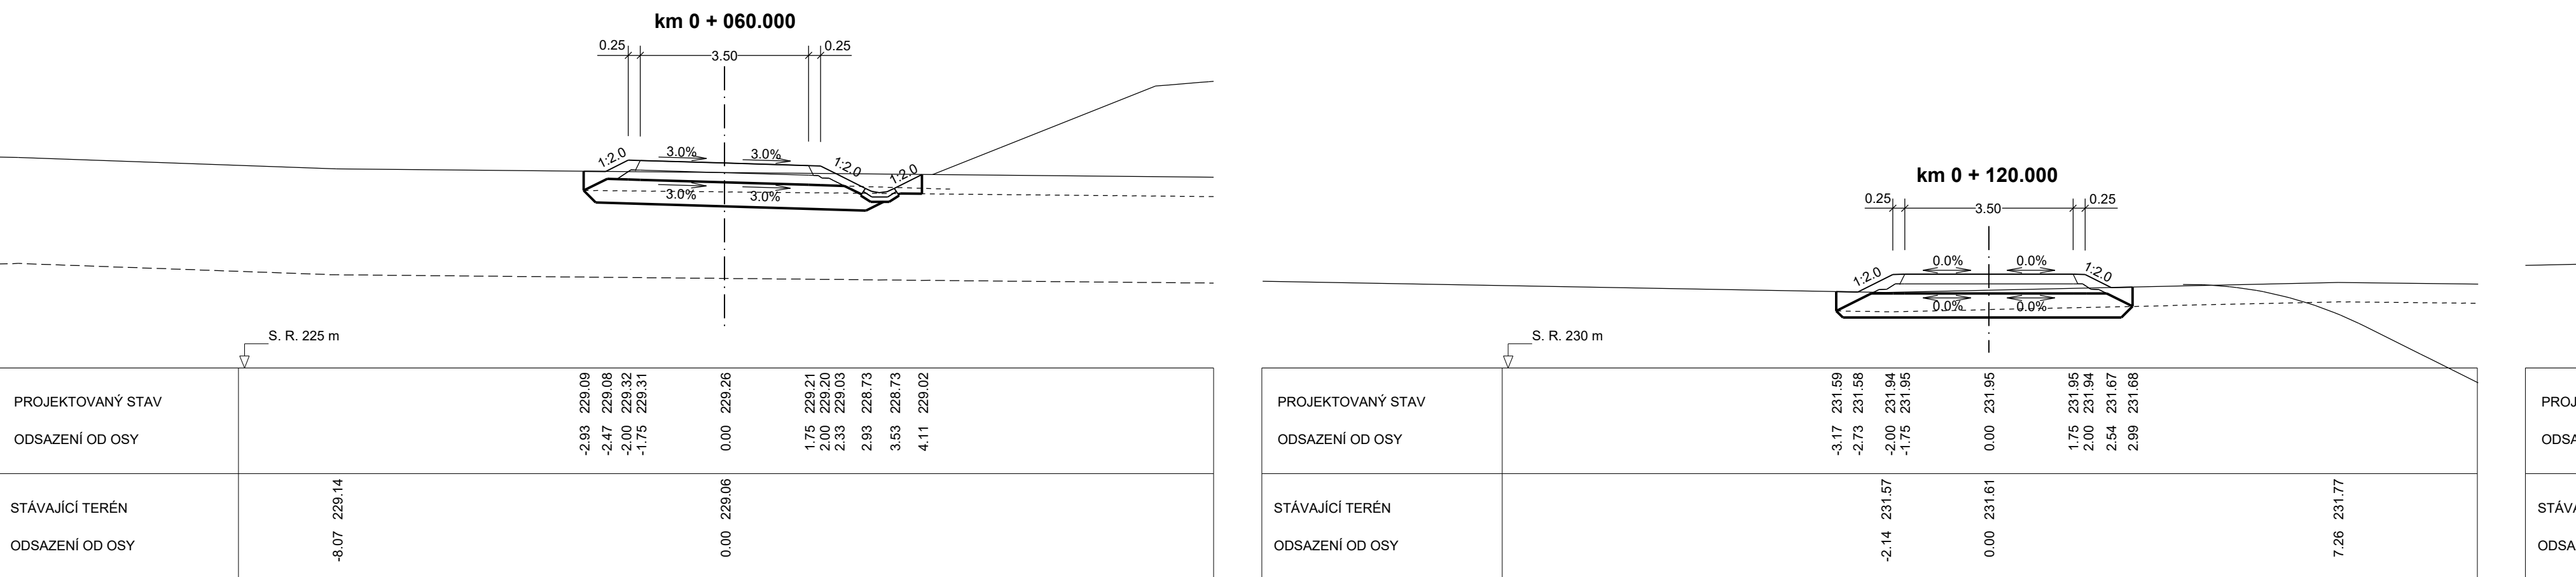
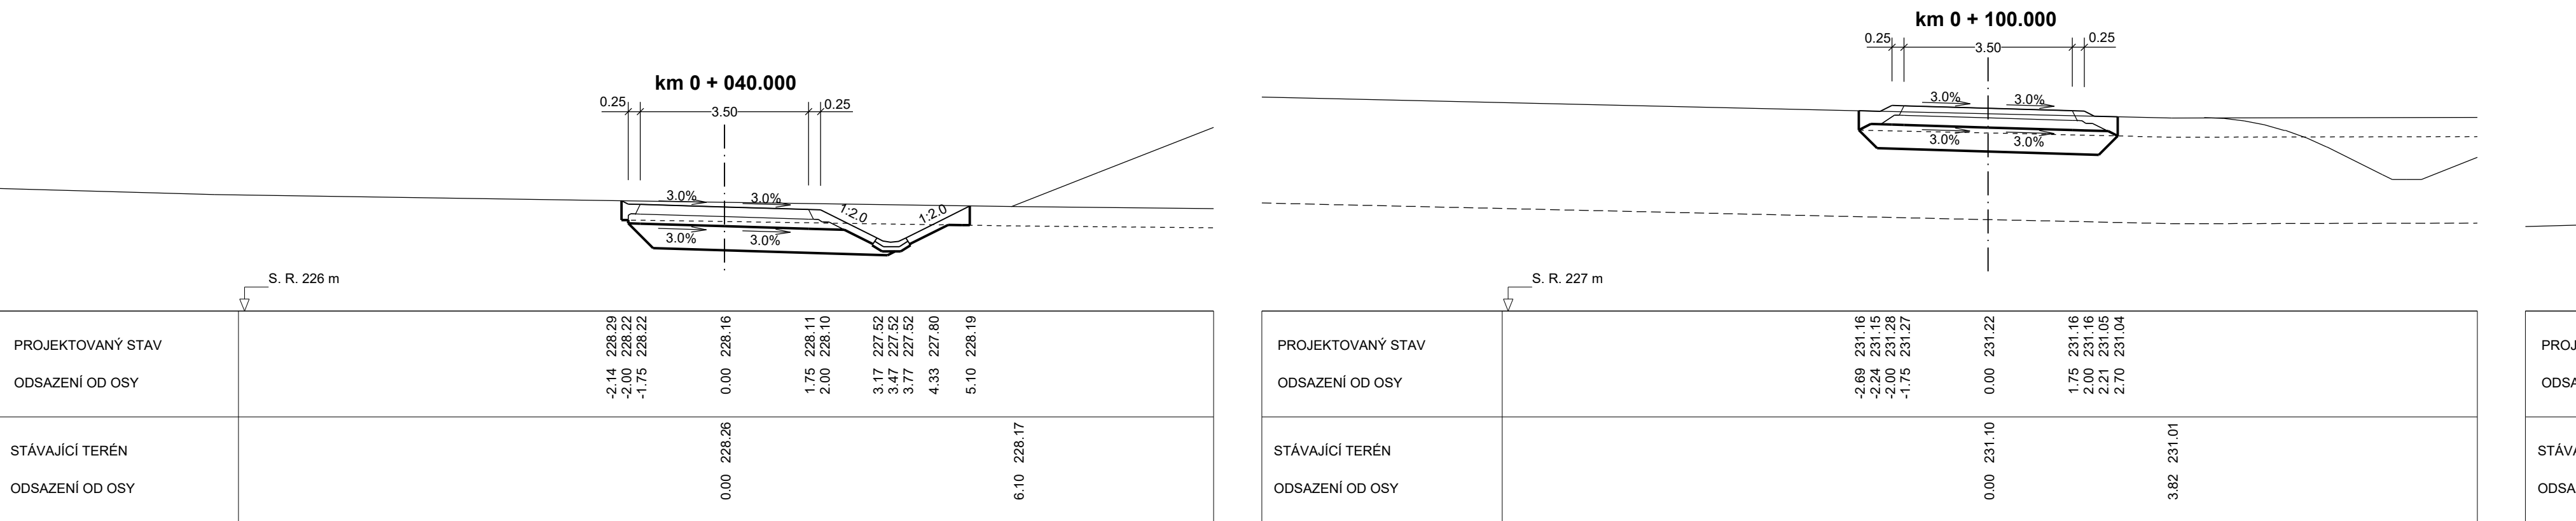


SO 153 - PŘÍSTUPY NA POZEMKY k.ú. SUKORADY U MLADÉ BOLESLAVI
PŘÍČNÉ ŘEZY SO 153.2 - km 0,020 - 0,420, M 1 : 100

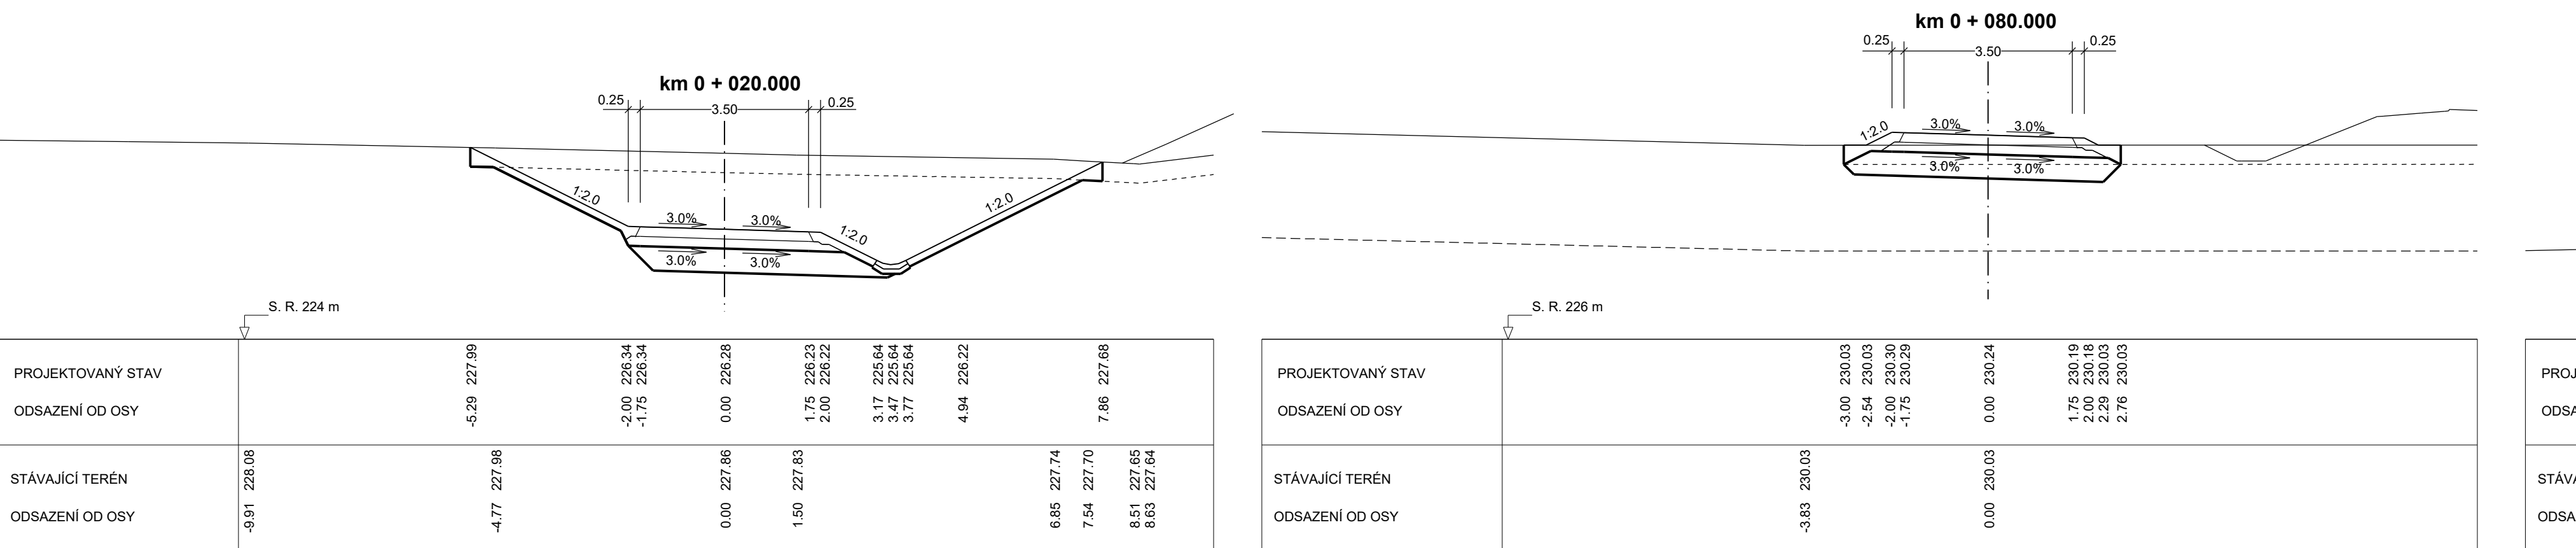

Výškový systém: Bpr

SO 153 Přístupy na pozemky k.ú. Sukorady u Mladé Boleslavi

Objednatel:



Ředitelství silnic a dálnic s. p.
Čerčanská 2023/12, Krč, 140 00 Praha 4

Zhotovitel:



Valbek, spol. s r.o.
Vaňurova 505/17
460 07 Liberec 3

	Vypracoval	P. BARTUŠEK	Zak. číslo	21-11/3
	Zast. projektant	ING. T. KLIMENT	Datum	02/2025
	Tech. kontrola	ING. M. HANZL	Stupeň	PDPŠ
	Akce		Počet formulí	20 x 4
	I/16 MLADÁ BOLESLAV - MARTINOVICE		Měřítko	1 : 100
			Č. přílohy	Paré
Zhotovitel: Valbek, spol. s r.o. Valbarkova 555/17 450 07, Lborec 3	Příloha PŘÍČNÉ ŘEZY SO 153.2 - km 0,020 - 0,420	5.2.1		