
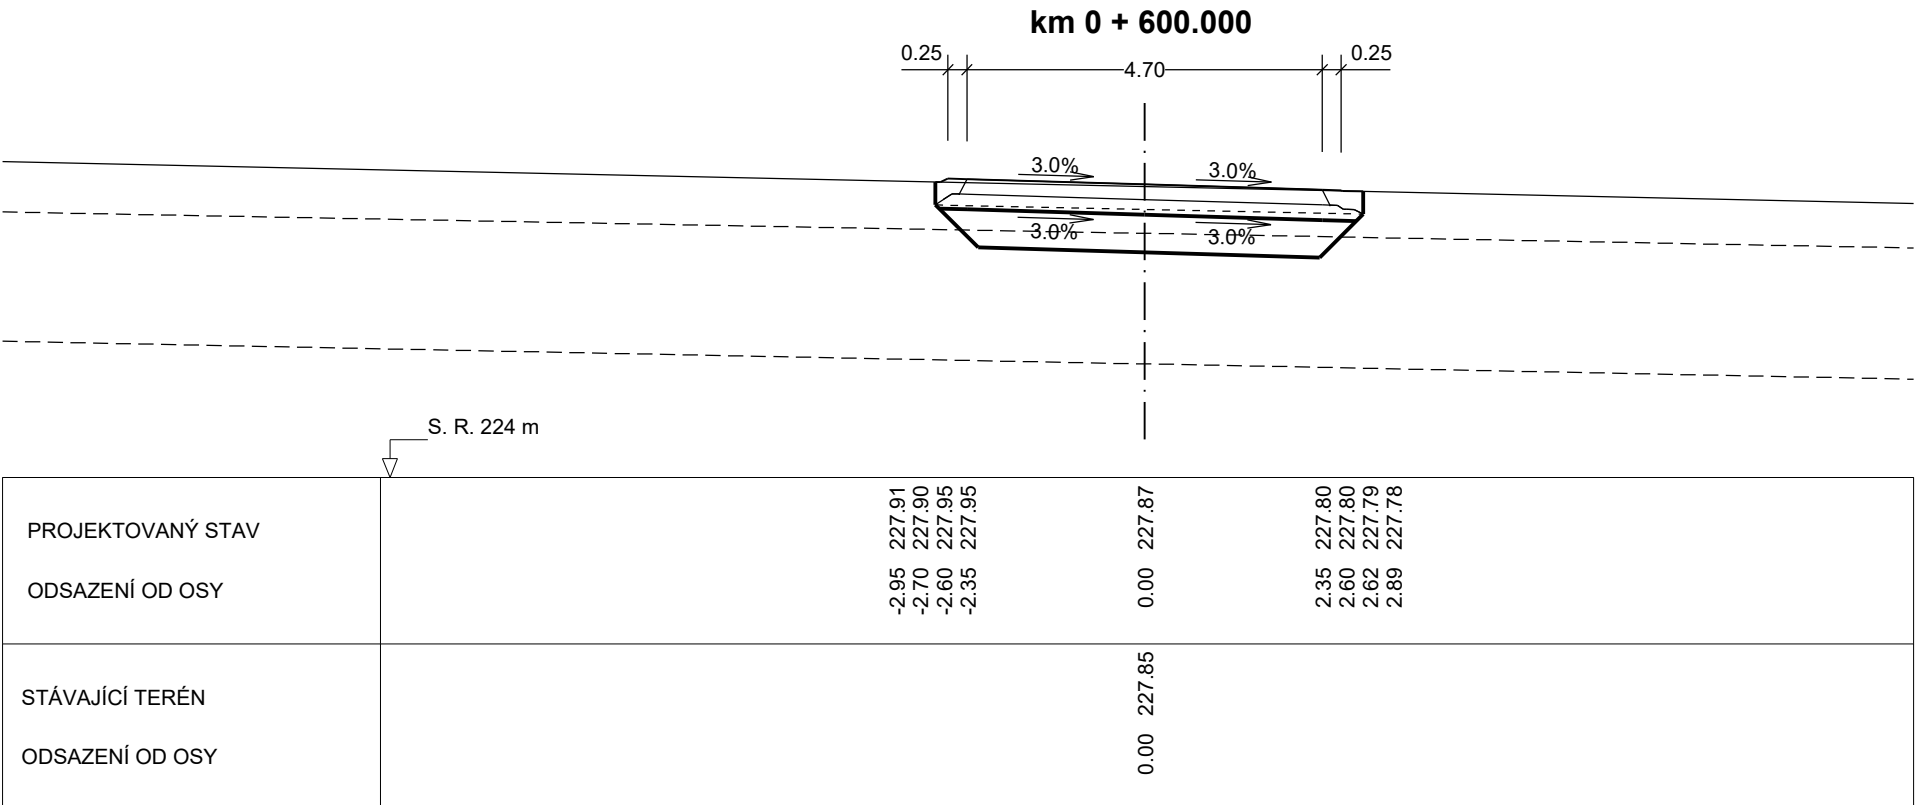
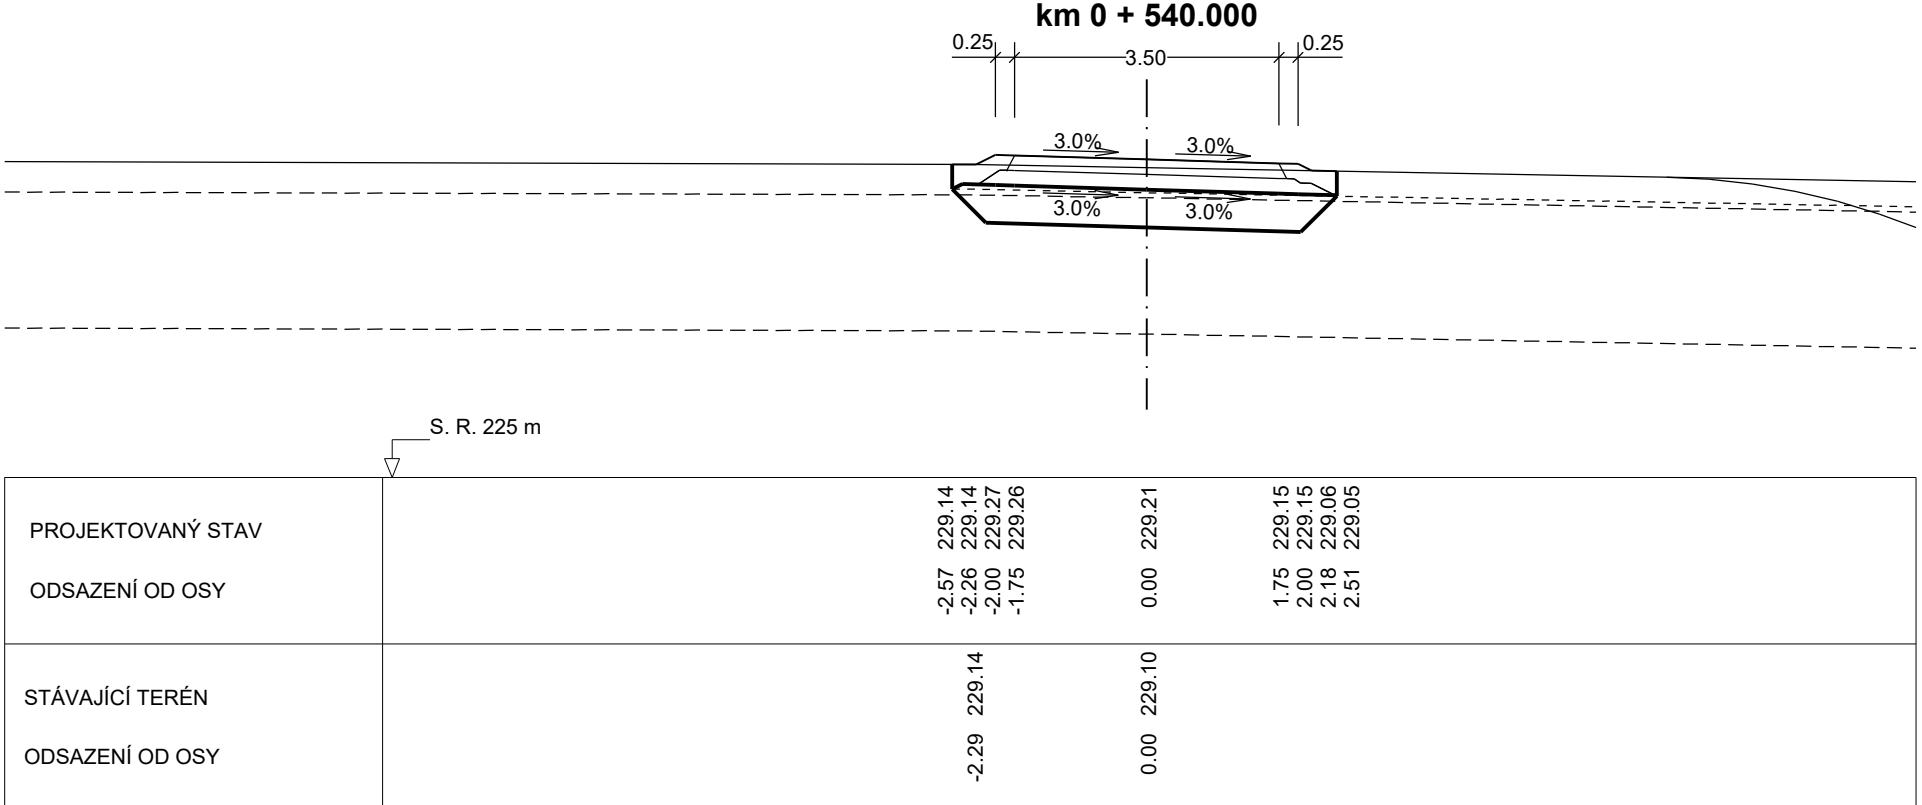
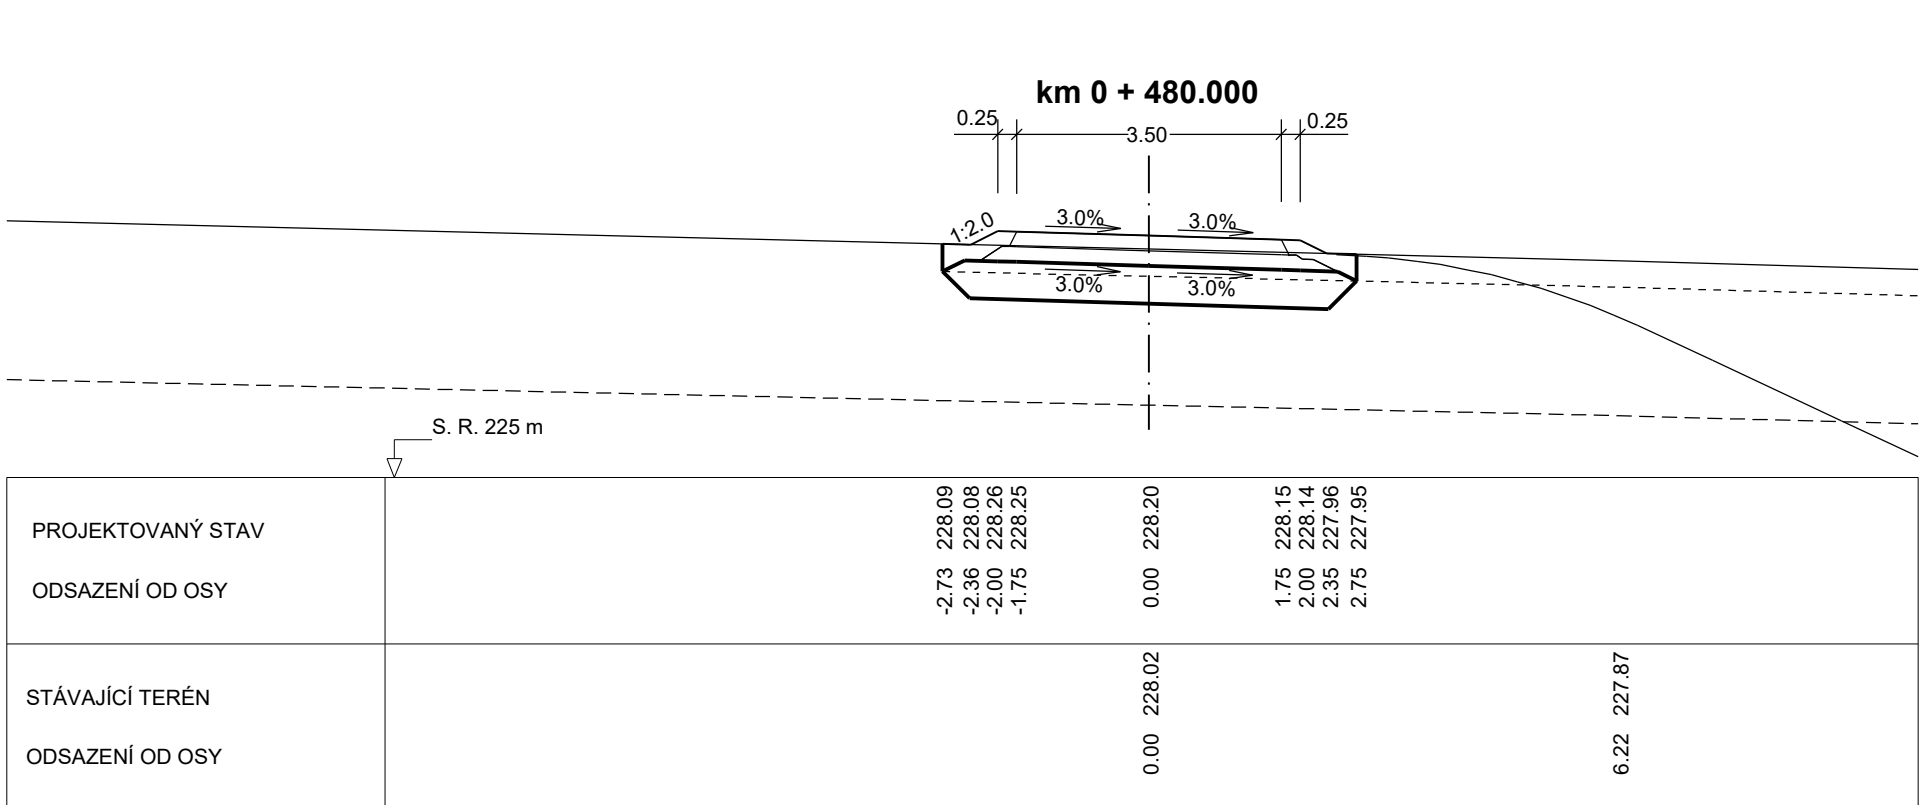
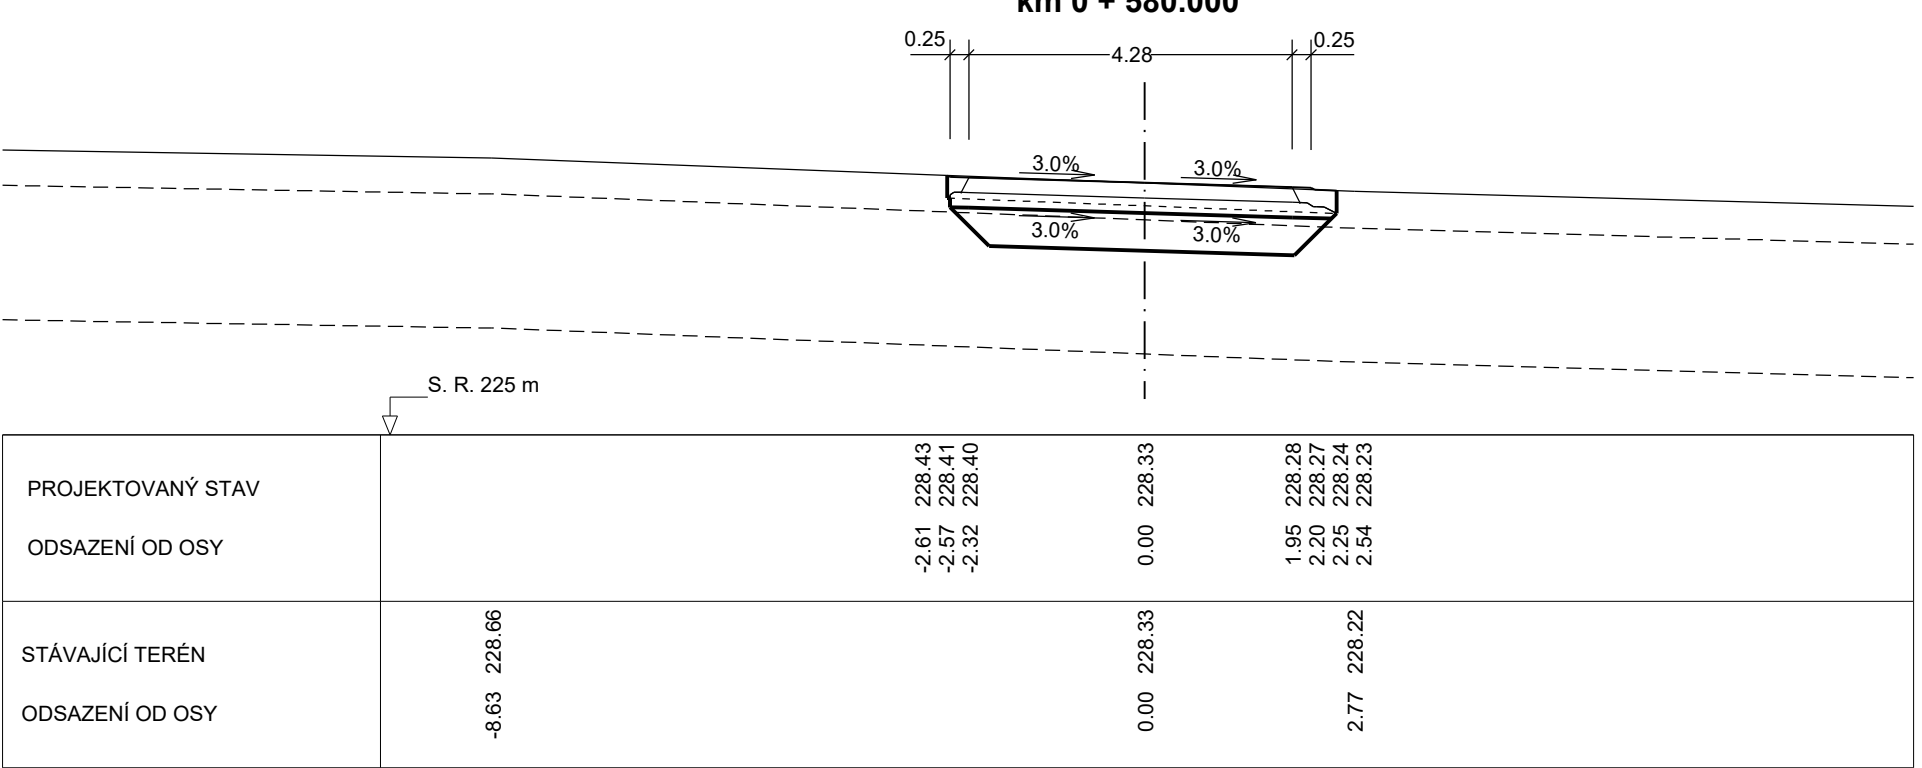
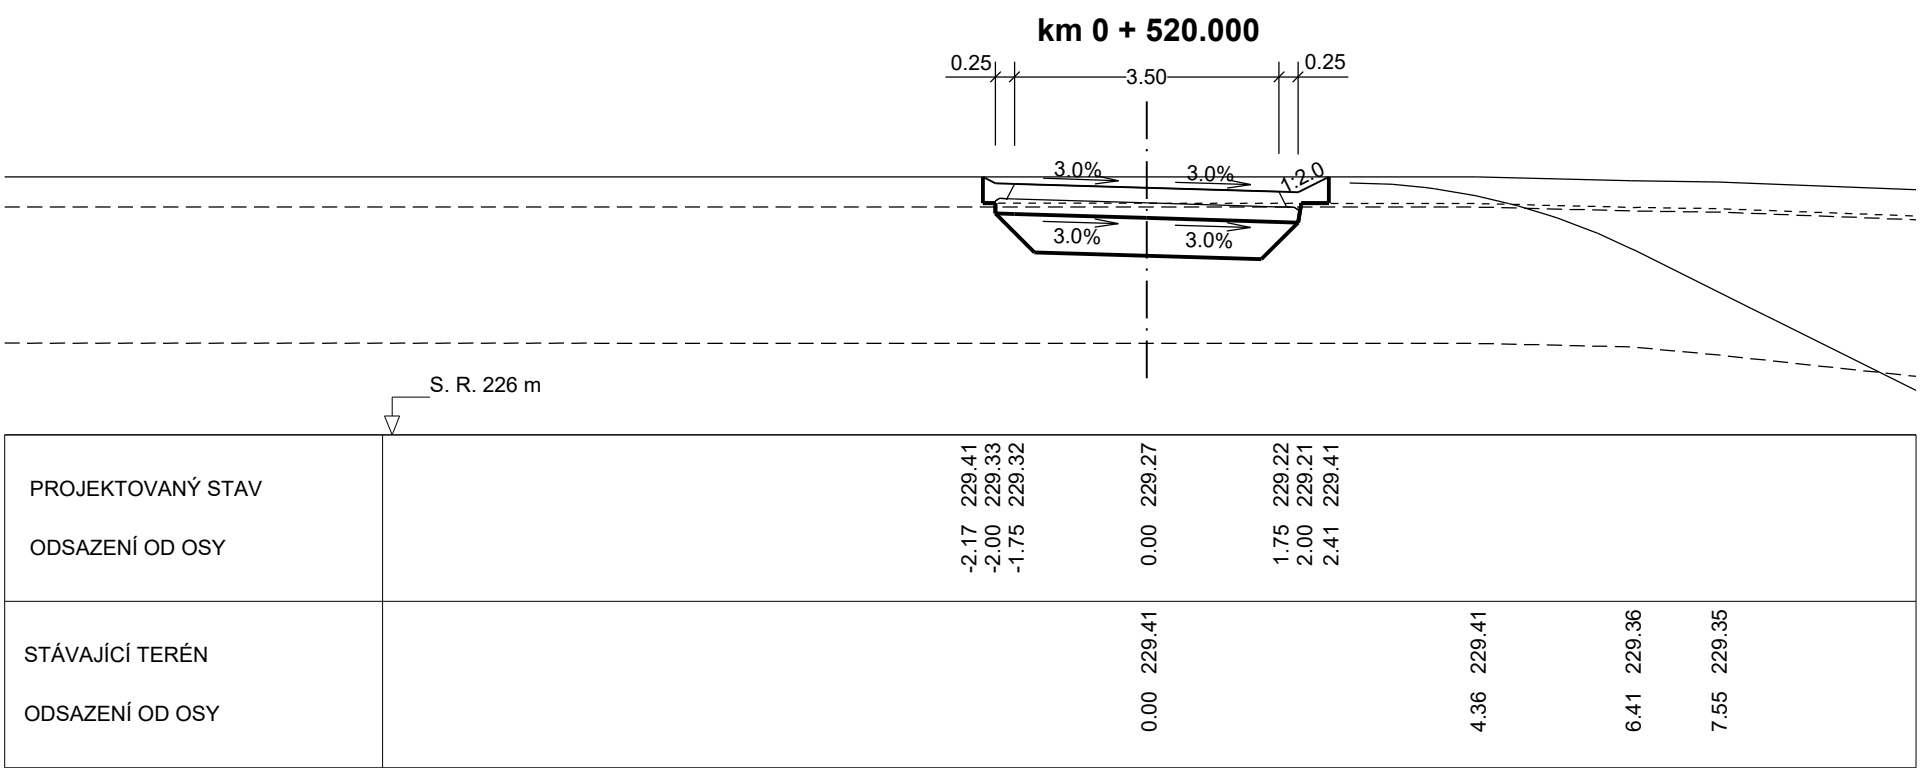
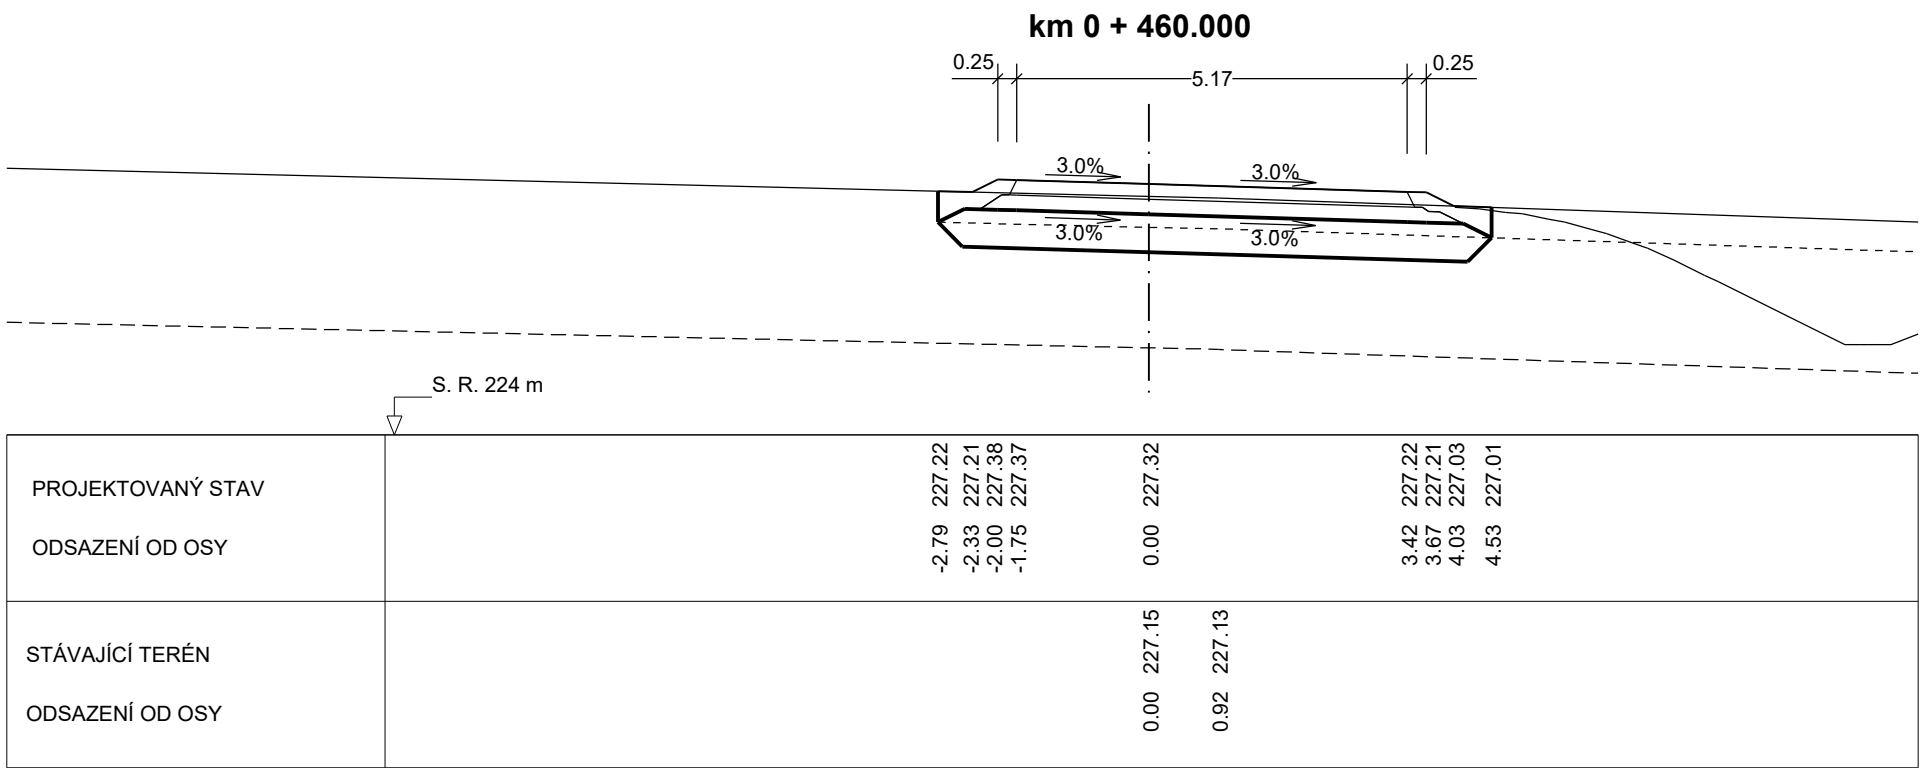
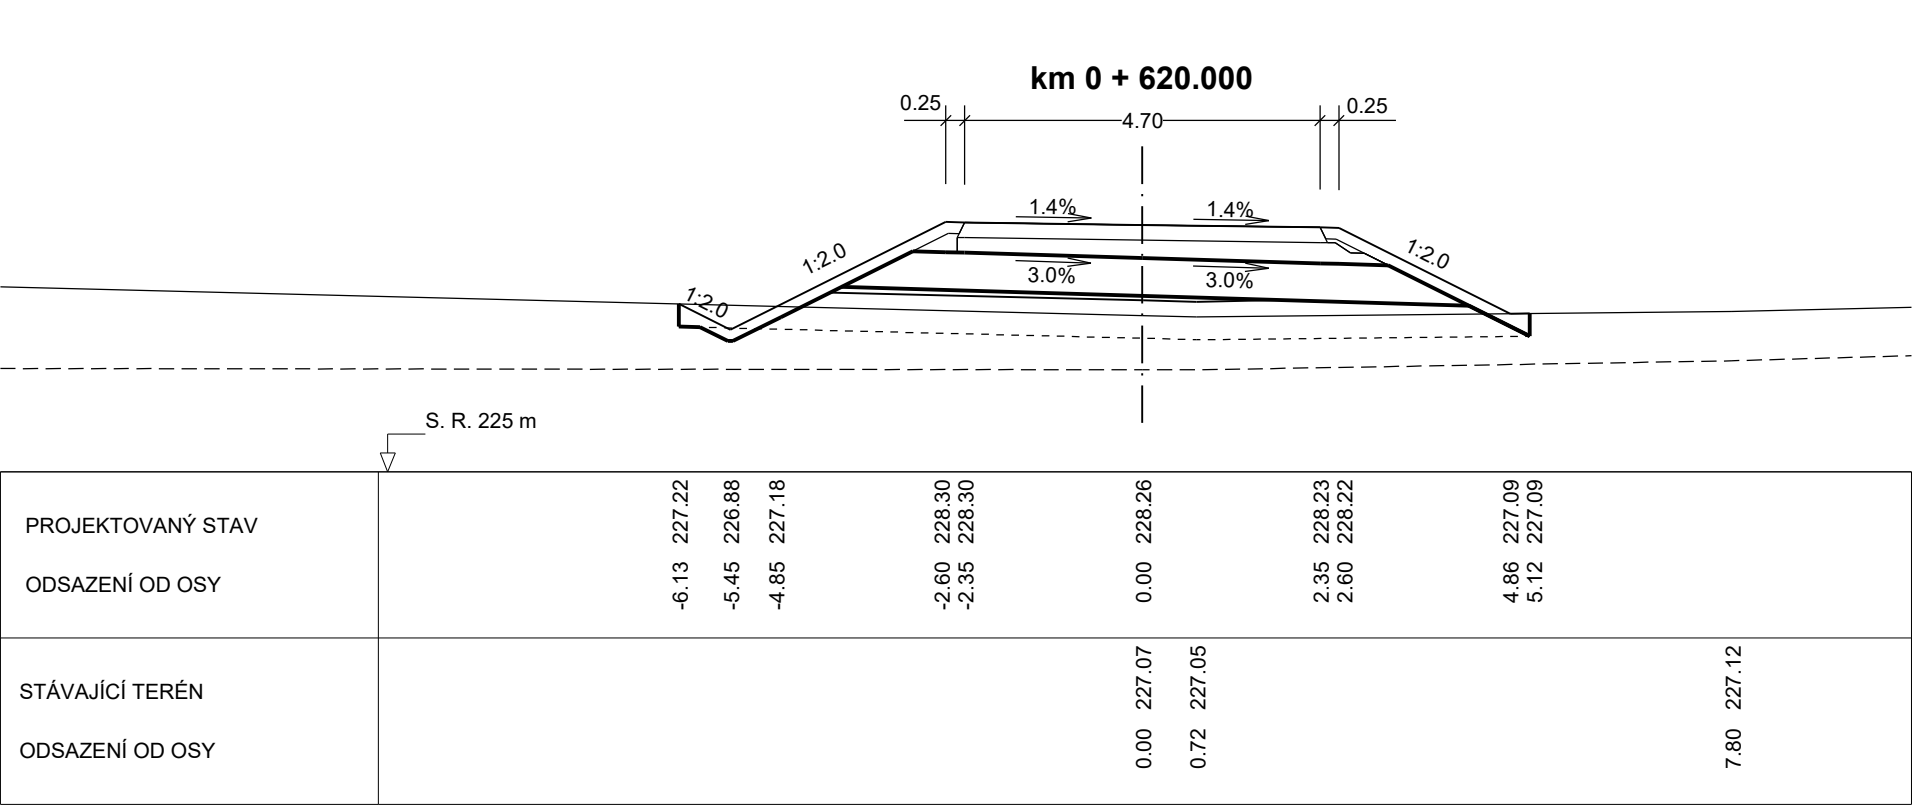
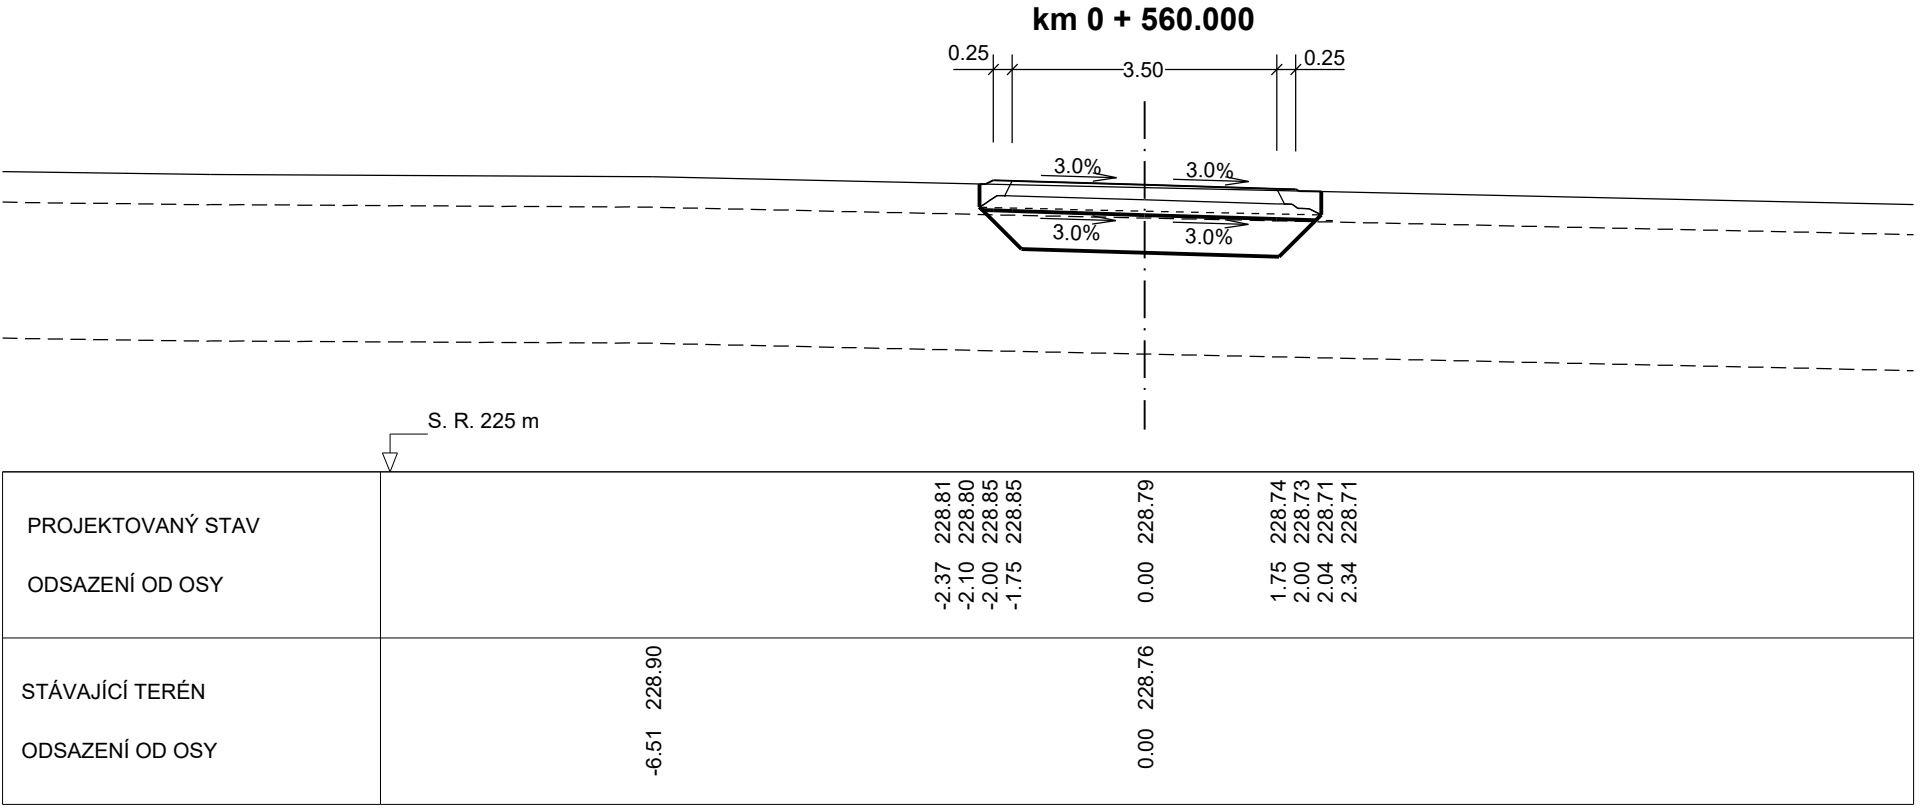
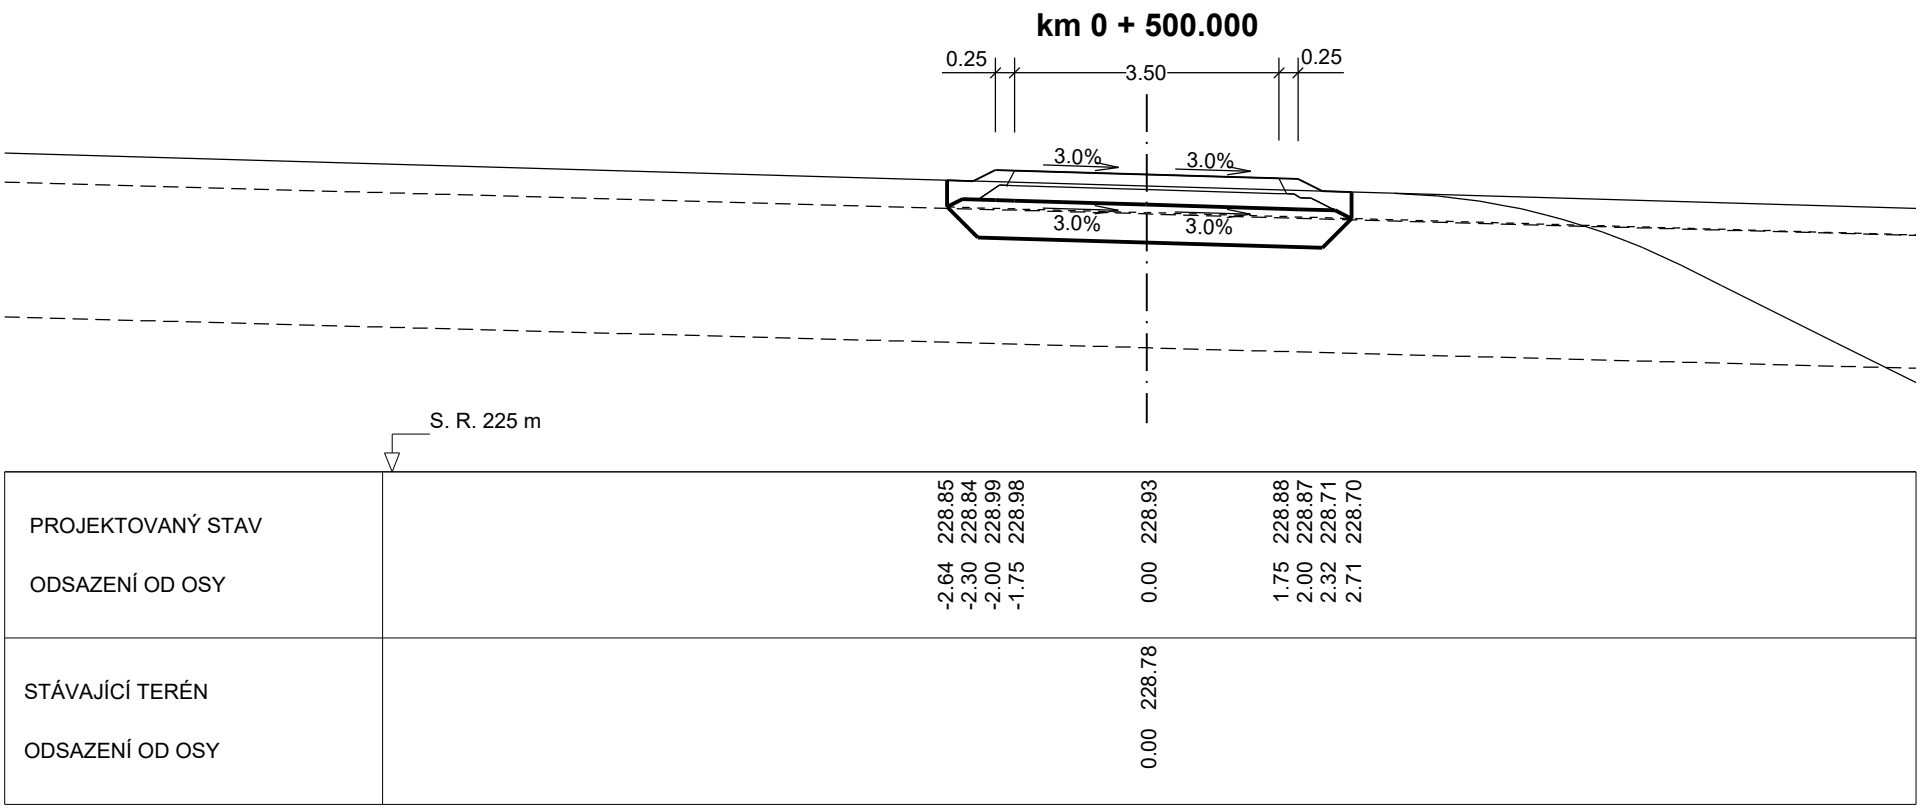


SO 153 - PŘÍSTUPY NA POZEMKY k.ú. SUKORADY U MLADÉ BOLESLAVI
PŘÍČNÉ ŘEZY SO 153.2 - km 0,440 - 0,620, M 1 : 100

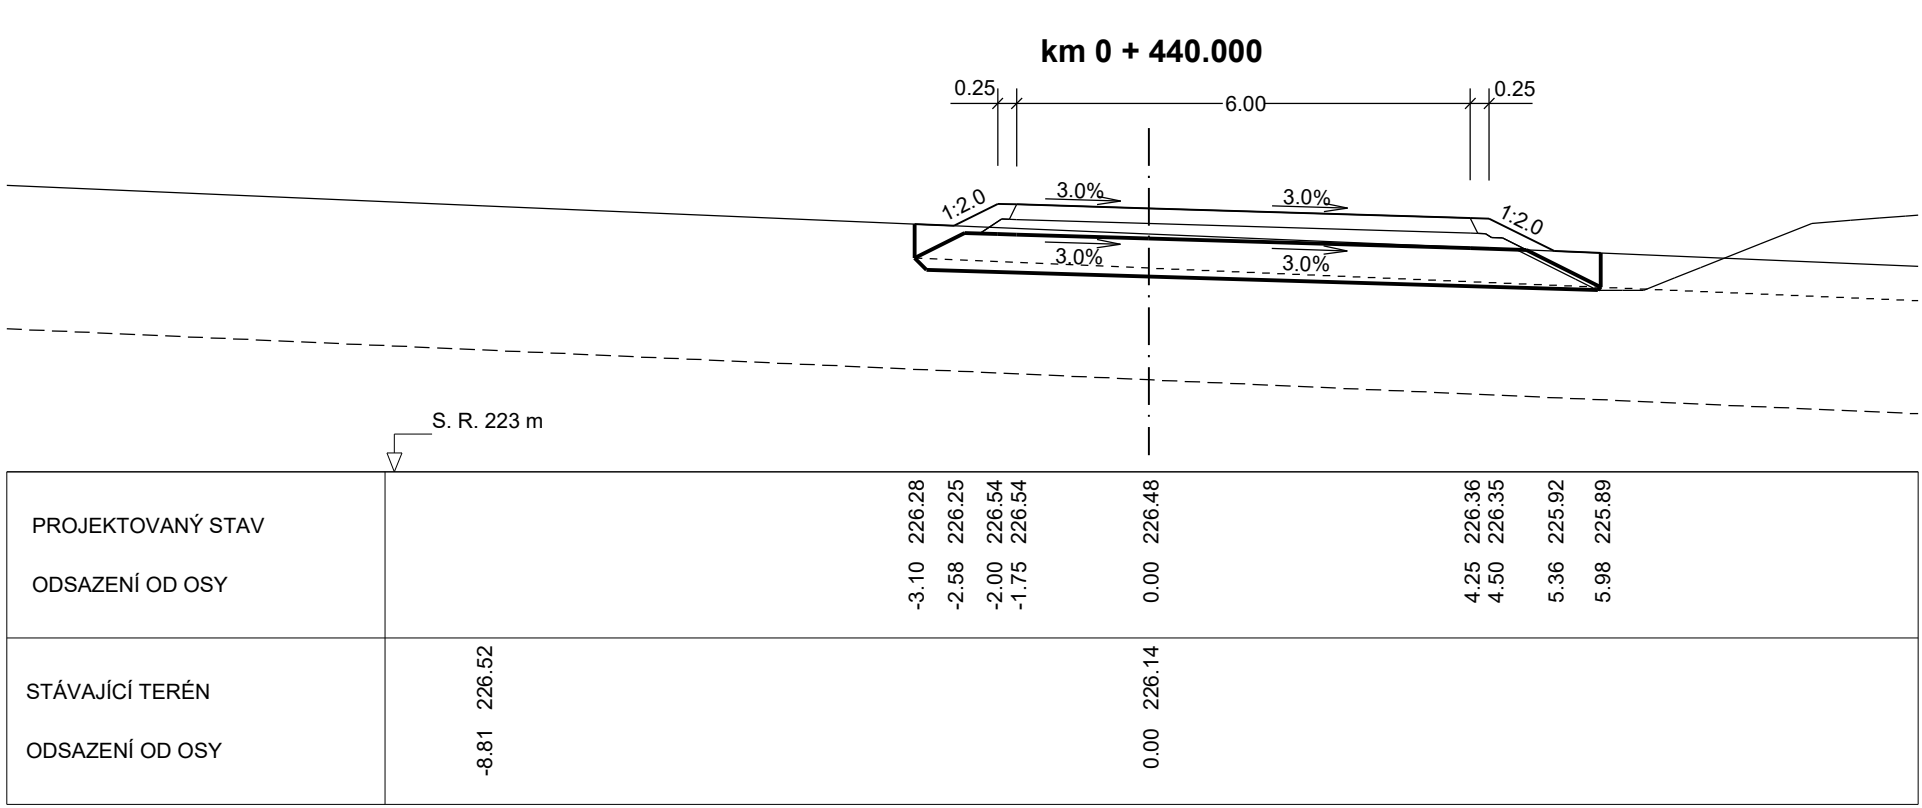

Výškový systém: Bpv

SO 153 Přístupy na pozemky k.ú. Sukorady u Mladé Boleslavi

Objednatel:

 **ŘEDITELSTVÍ SILNIC A DÁLNIC**

Ředitelství silnic a dálnic s. p.
Čerčanská 2023/12, Krč, 140 00 Praha 4

Zhotovitel:

 **Valbek**

Valbek, spol. s r.o.
Vaňurova 505/17
460 07 Liberec 3

 **Valbek**

I/16 MLADÁ BOLESLAV - MARTINOVICE

Příloha
PŘÍČNÉ ŘEZY SO 153.2 - km 0,440 - 0,620

Vypracoval	P. BARTUSEK	Zak. číslo	21-L113-001
Zodp. projektant	ING. T. KLIMENT	Datum	02/2025
Tech. kontrola	ING. M. HANŽL	Stupeň	PDPS
Akce		Počet formátů	12 x A4
		Měřítko	1 : 100
		Č. přílohy	Paré

5.2.2