




SO 153 - PŘÍSTUPY NA POZEMKY k.ú. SUKORADY U MLADÉ BOLESLAVI
PŘÍČNÉ ŘEZY SO 153.3, M 1 : 100

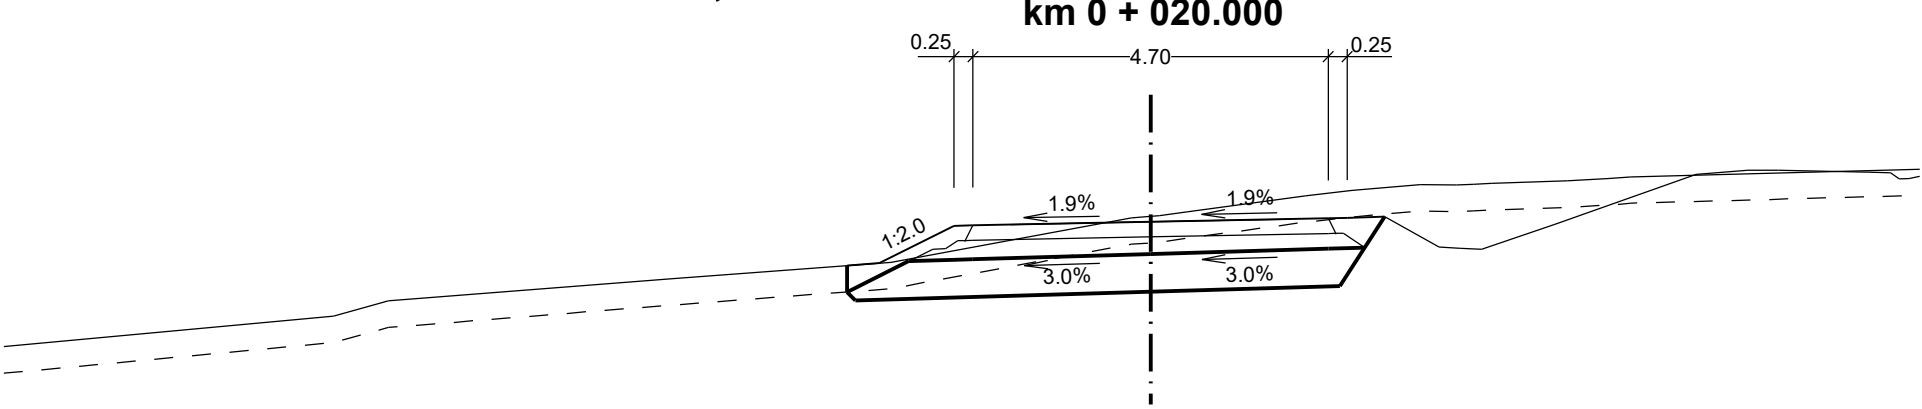


PROJEKTOVANÝ STAV	
ODSAZENÍ OD OSY	-4.02 222.23 -3.59 222.26 -2.66 222.75 -2.35 222.76 0.00 222.81 2.35 222.85 2.60 222.86 3.46 223.29
STÁVAJÍCÍ TERÉN	-6.33 222.06 -3.44 222.27 -0.26 222.86 0.00 222.88 0.12 222.89 0.49 222.94 2.05 223.15 2.06 223.22 3.57 223.30 4.05 223.29 4.27 223.30 4.51 223.32 5.51 223.35 6.05 223.38 6.35 223.40
ODSAZENÍ OD OSY	

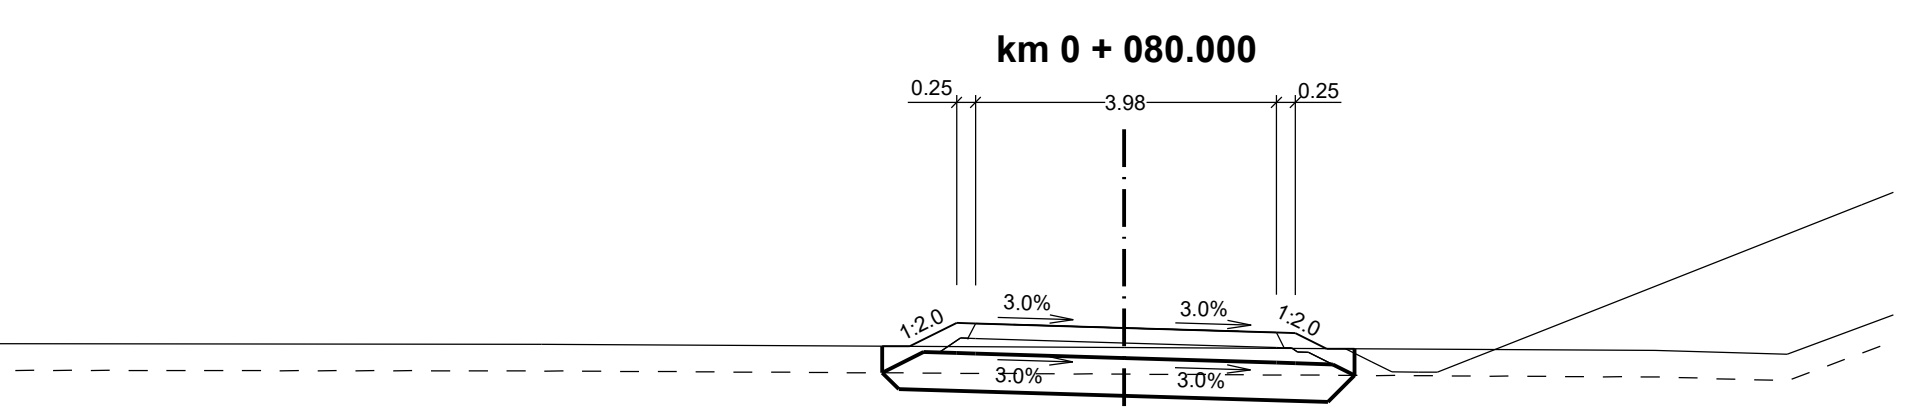


PROJEKTOVANÝ STAV	
ODSAZENÍ OD OSY	-3.20 221.16 -2.84 221.16 -2.22 221.47 -1.97 221.46 0.00 221.41 2.01 221.35 2.26 221.34 2.68 221.13 3.05 221.13
STÁVAJÍCÍ TERÉN	-7.71 221.19 0.00 221.14 7.02 221.11 8.77 221.05
ODSAZENÍ OD OSY	

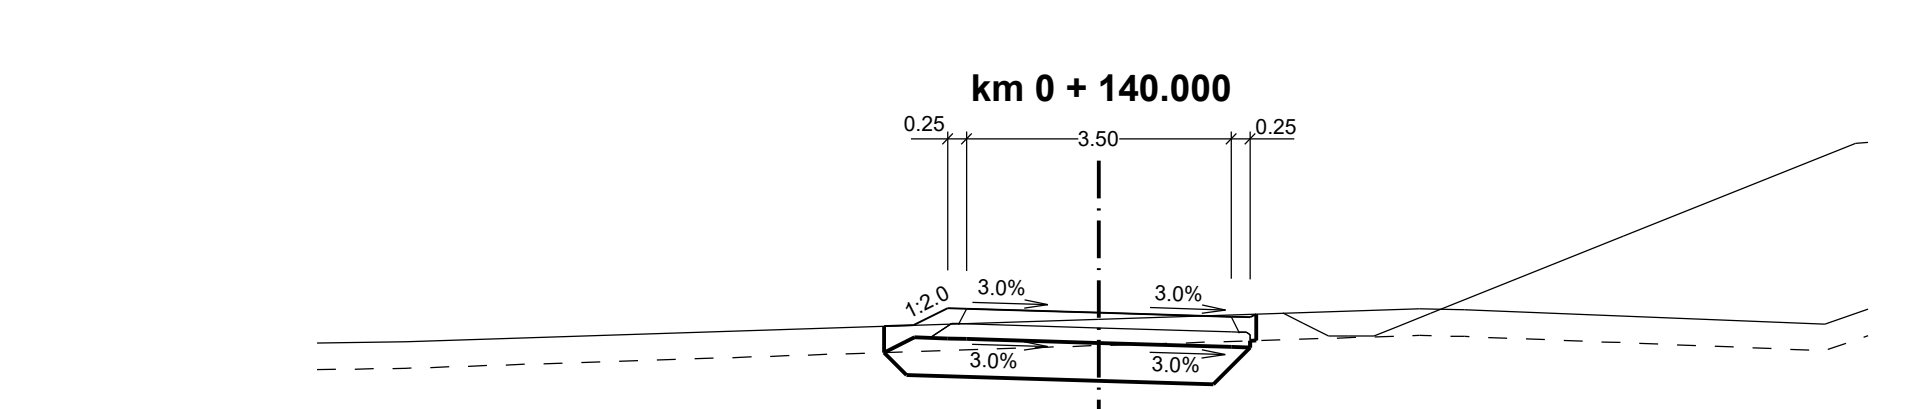


PROJEKTOVANÝ STAV	
ODSAZENÍ OD OSY	-2.84 222.43 -2.45 222.44 -2.00 222.67 -1.75 222.66 0.00 222.61 1.75 222.55 2.00 222.55 2.06 222.59
STÁVAJÍCÍ TERÉN	-9.16 222.22 0.00 222.52 4.24 222.86 4.84 222.64 9.60 222.46
ODSAZENÍ OD OSY	

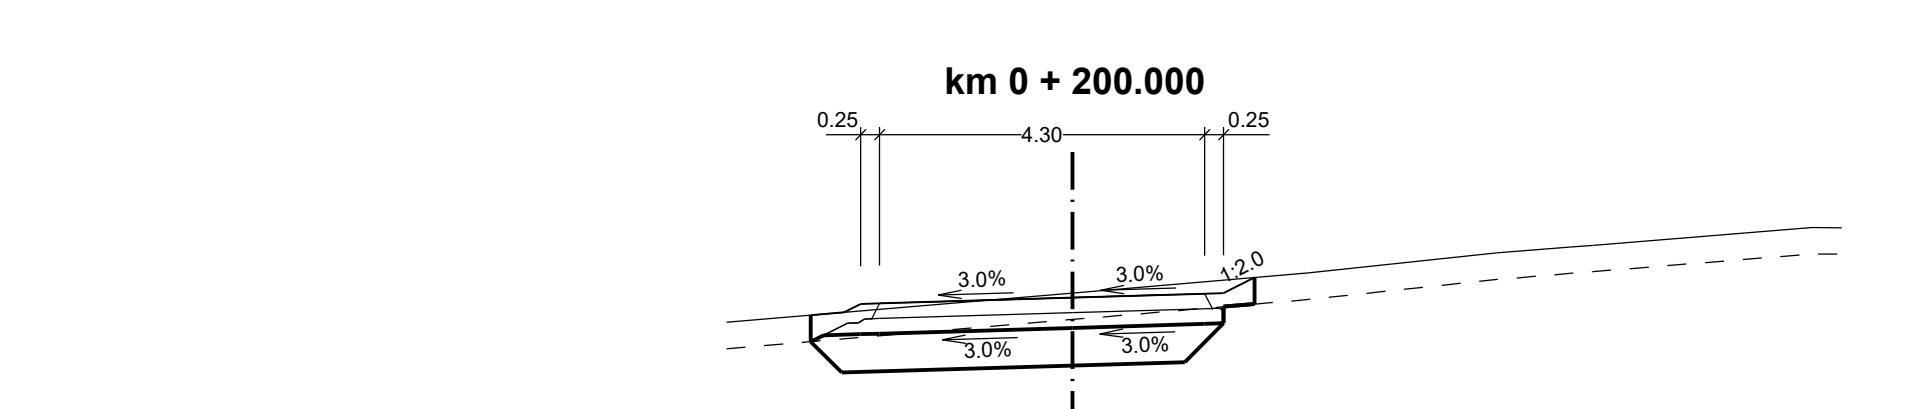


PROJEKTOVANÝ STAV	
ODSAZENÍ OD OSY	-3.46 223.57 -3.05 223.61 -2.80 223.72 -2.55 223.73 0.00 223.81 1.75 223.86 2.00 223.87 2.41 224.07
STÁVAJÍCÍ TERÉN	-4.57 223.48 0.00 223.87 3.11 224.13 5.62 224.40 6.85 224.46 6.88 224.50 9.78 224.73
ODSAZENÍ OD OSY	

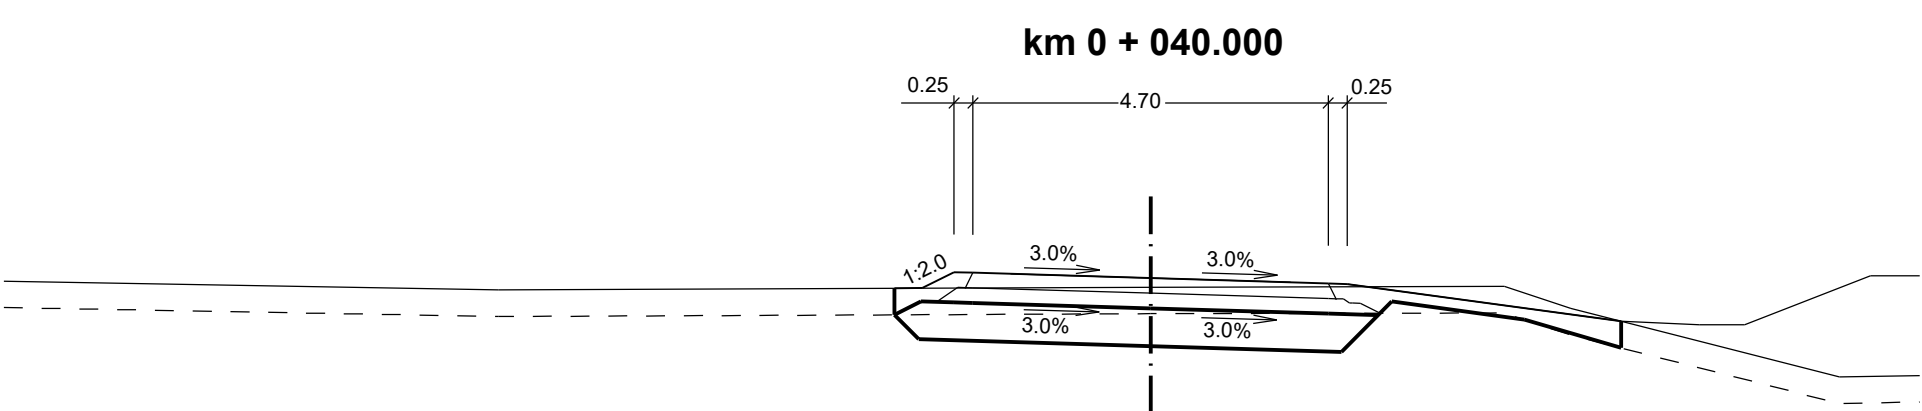


PROJEKTOVANÝ STAV	
ODSAZENÍ OD OSY	-3.39 220.49 -3.02 220.50 -2.60 220.71 -2.35 220.70 0.00 220.63 2.35 220.56 2.60 220.55 6.22 220.06
STÁVAJÍCÍ TERÉN	-8.63 220.47 0.00 220.51 4.68 220.52 5.56 220.23 9.11 219.32
ODSAZENÍ OD OSY	

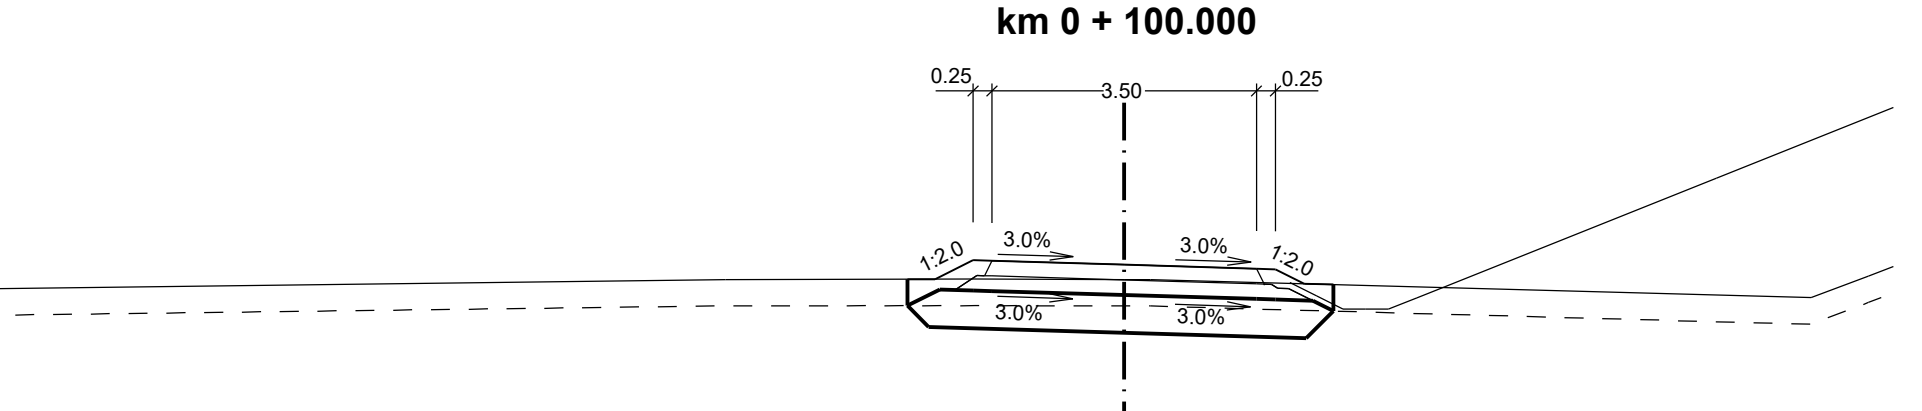


PROJEKTOVANÝ STAV	
ODSAZENÍ OD OSY	-2.67 221.61 -2.50 221.61 -2.00 221.87 -1.75 221.86 0.00 221.81 1.75 221.75 2.00 221.75 2.38 221.55 2.77 221.54
STÁVAJÍCÍ TERÉN	-5.27 221.61 -1.97 221.62 0.00 221.61 0.35 221.61 9.09 221.37 9.85 221.66
ODSAZENÍ OD OSY	

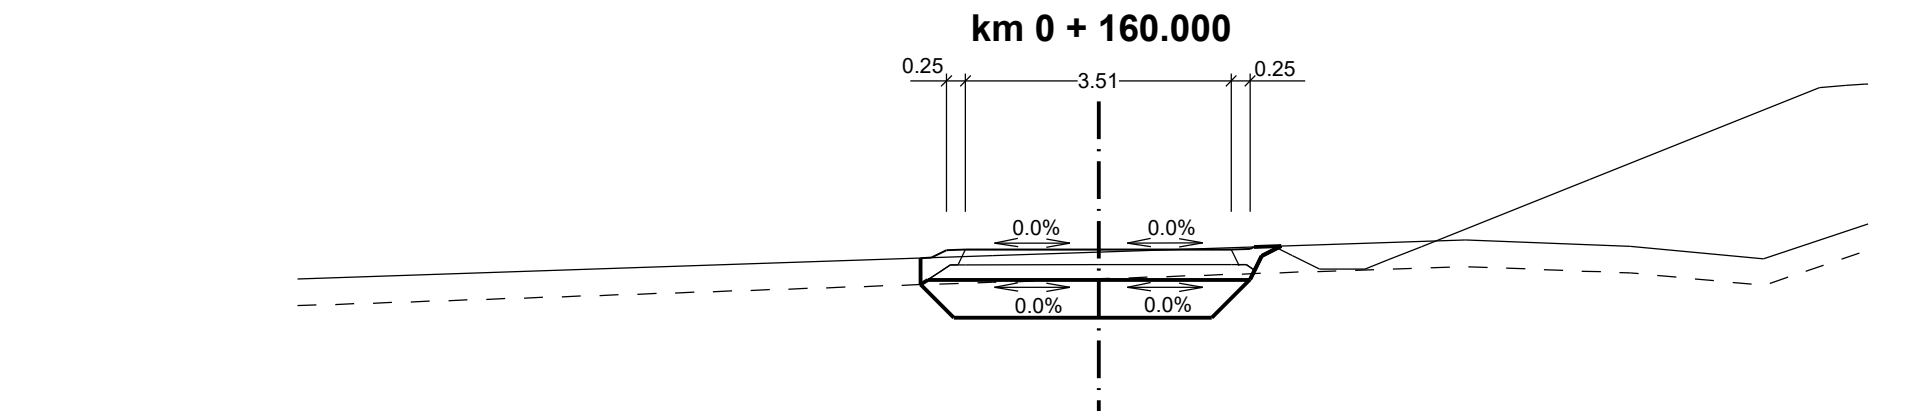


PROJEKTOVANÝ STAV	
ODSAZENÍ OD OSY	-2.60 222.89 -2.41 222.90 -2.01 223.00 -1.76 223.01 0.00 223.01 1.75 223.01 2.00 223.01 2.05 223.04
STÁVAJÍCÍ TERÉN	-1.41 222.83 0.00 222.87 4.85 223.13 7.03 223.05 8.79 222.88
ODSAZENÍ OD OSY	

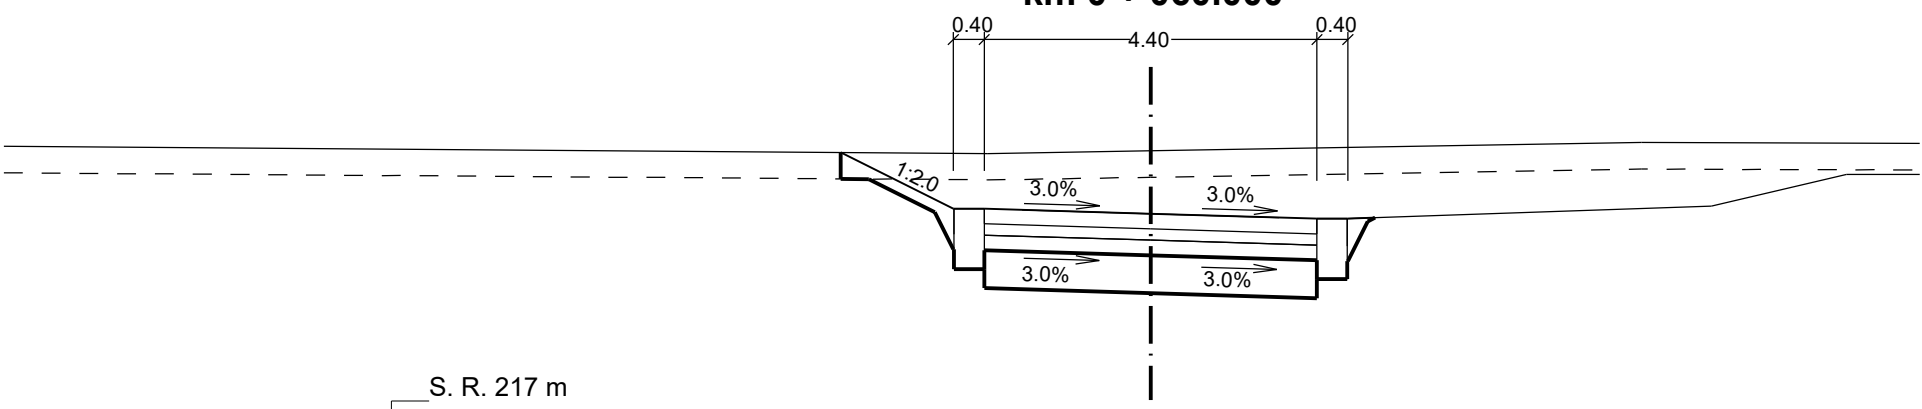

PROJEKTOVANÝ STAV	
ODSAZENÍ OD OSY	-4.10 220.79 -2.61 220.04 -2.60 220.04 -2.20 220.04 0.00 219.98 2.20 219.91 2.60 219.91 2.61 219.91 4.56 220.89
STÁVAJÍCÍ TERÉN	-2.15 220.77 0.00 220.81 6.49 220.92
ODSAZENÍ OD OSY	

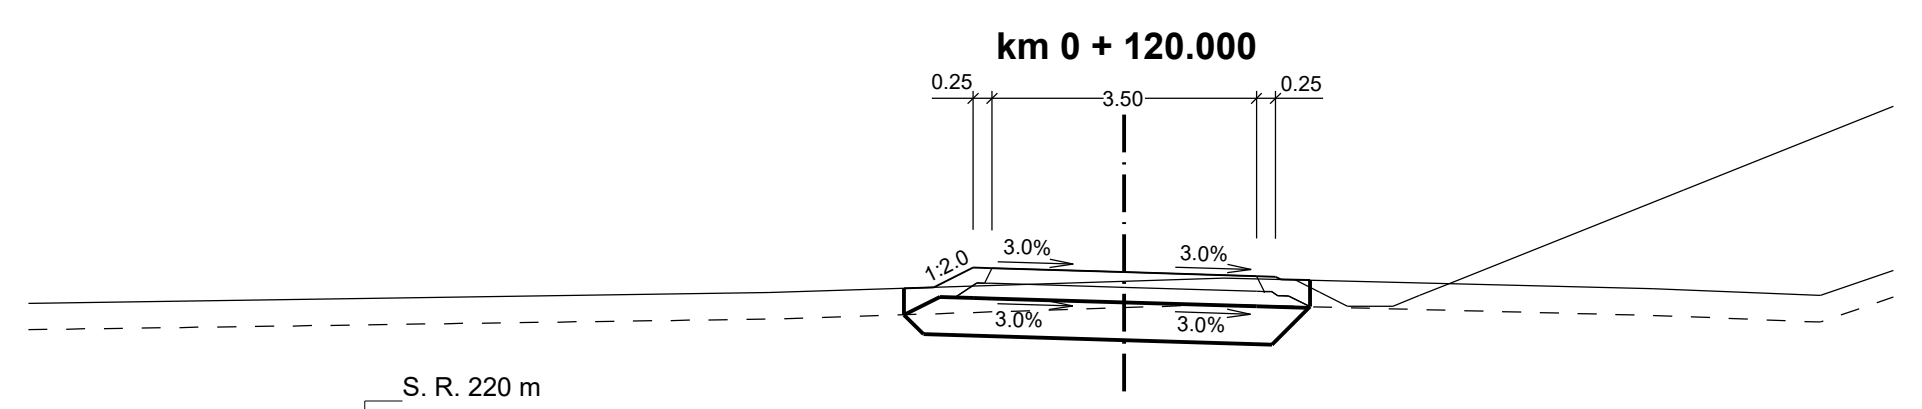

PROJEKTOVANÝ STAV	
ODSAZENÍ OD OSY	-2.91 221.99 -2.52 222.00 -2.00 222.27 -1.75 222.26 0.00 222.21 1.75 222.15 2.00 222.15 2.07 222.11 2.46 222.10
STÁVAJÍCÍ TERÉN	-4.70 221.93 0.00 222.09 1.32 222.13 6.98 221.99 9.21 221.90
ODSAZENÍ OD OSY	

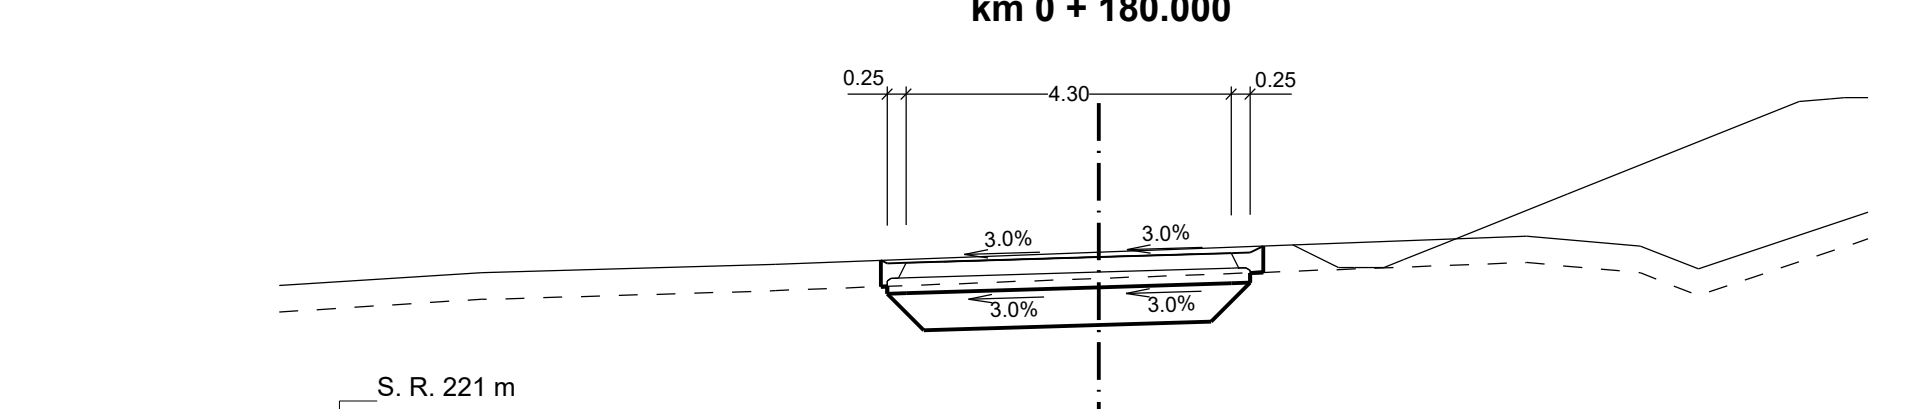

PROJEKTOVANÝ STAV	
ODSAZENÍ OD OSY	-2.88 223.36 -2.65 223.33 -2.55 223.33 0.00 223.41 1.75 223.46 2.00 223.47 2.17 223.50
STÁVAJÍCÍ TERÉN	-8.16 223.20 -4.28 223.31 0.00 223.47 5.66 223.68 7.16 223.55 7.93 223.25
ODSAZENÍ OD OSY	

Výškový systém: Bpv

SO 153

Přístupy na pozemky k.ú. Sukorady u Mladé Boleslavi

Objednatel:



Ředitelství silnic a dálnic s. p.
Čerčanská 2023/12, Kré, 140 00 Praha 4

Zhotovitel:



Valbek, spol. s r.o.
Vaňurova 505/17
460 07 Liberec 3



Valbek, spol. s r.o.
Vaňurova 505/17
460 07 Liberec 3

Ypracoval

Zodp. projektant

Tech. kontrola

Akce

Zhotovitel:

P. BARTUSEK

ING. T. KLIMENT

ING. M. HANŽL

I/16 MLADÁ BOLESLAV - MARTINOVICE

Příloha

Zak. číslo

Datum

Stupeň

Počet formátů

Měřítko

Č. přílohy

21-LI13-001

02/2025

PDPS

12 x A4

1 : 100

Paré

5.3