



SO 154 - PŘELOŽKA POLNÍ CESTY V km 6,700
PODÉLNÝ PROFIL, M 1 : 1000 / 100

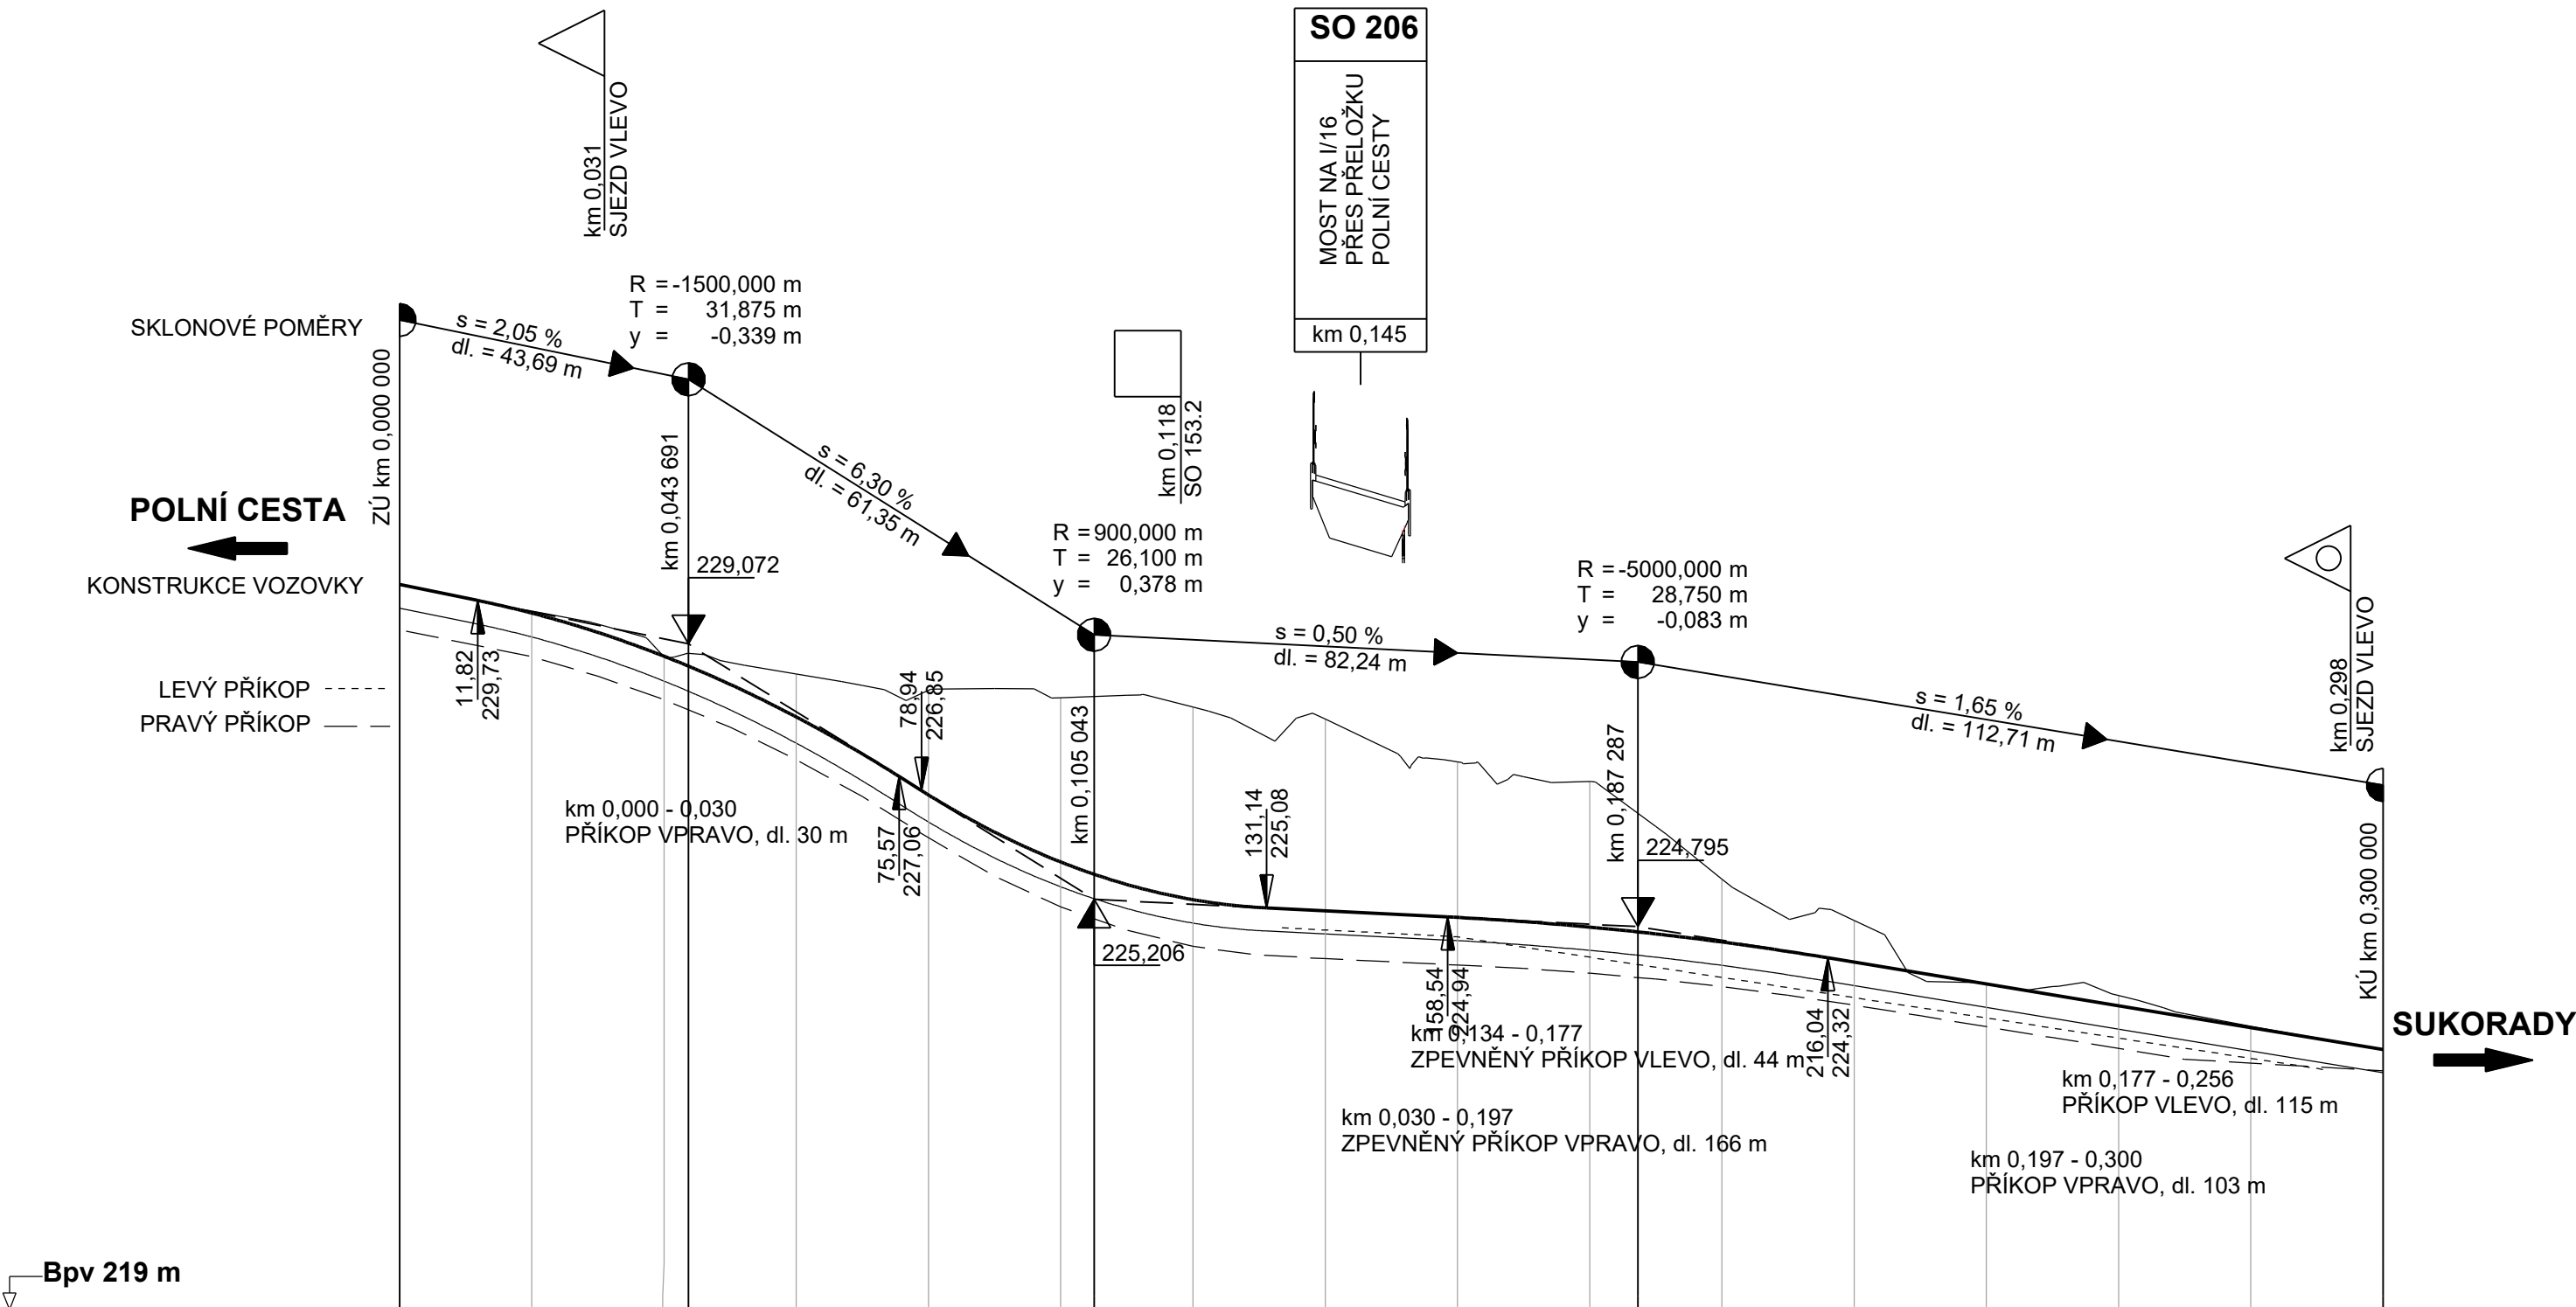

KÓTY NIVELETY	229,97	229,54	228,88	228,73	227,96	226,78	225,77	225,58	225,20	225,03	224,93	224,79	224,71	224,56	224,26	223,93	223,60	223,27	222,94
KÓTY TERÉNU	229,97	229,57	228,88	228,93	228,61	228,37	228,26	228,28	228,11	227,93	227,29	226,99	226,51	225,51	224,89	223,93	223,75	223,28	222,94
STANIČENÍ	0,00	20,00	40,00	43,69	60,00	80,00	100,00	105,04	120,00	140,00	160,00	180,00	187,29	200,00	220,00	240,00	260,00	280,00	300,00

km 0+000 0+100 0+200 0+300

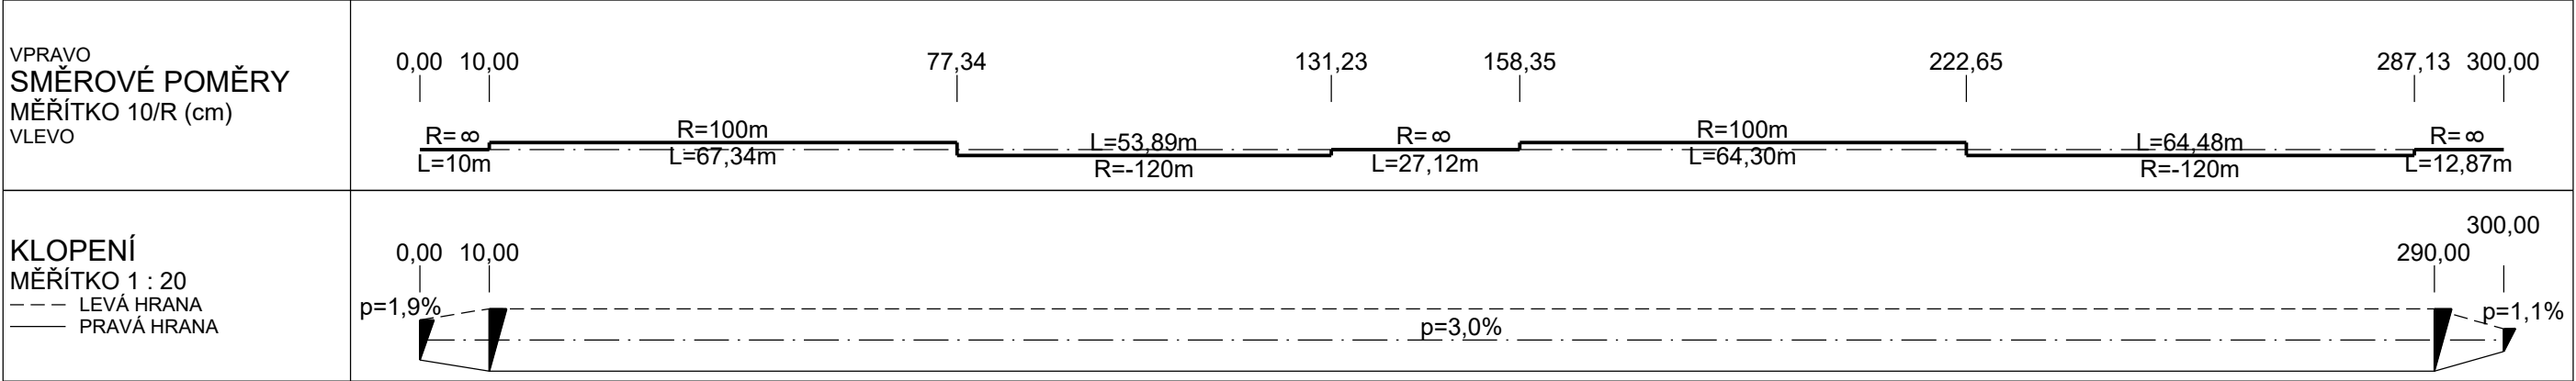

Výškový systém: Bpv

SO 154 Přeložka polní cesty v km 6,700

Objednatel:

**ŘEDITELSTVÍ
SILNIC
A DÁLNIC**

Ředitelství silnic a dálnic s. p.
Čerčanská 2023/12, Krč, 140 00 Praha 4

Zhotovitel:

**Valbek**

Valbek, spol. s r.o.
Vaňurova 505/17
460 07 Liberec 3

HIP:

ING. T. KLIMENT

	Vypracoval	P. BARTUSEK	Zak. číslo	21-LI13-001
	Zodp. projektant	ING. T. KLIMENT	Datum	02/2025
	Tech. kontrola	ING. M. HANŽL	Stupeň	PDPS
	Akce I/16 MLADÁ BOLESLAV - MARTINOVICE		Počet formátů	6 x A4
			Měřitko	1:1 000/100
Zhotovitel: Valbek, spol. s r.o. Vaňurova 505/17 460 07 Liberec 3	Příloha	PODÉLNÝ PROFIL		Č. přílohy 3 Paré