


SO 154 - PŘELOŽKA POLNÍ CESTY V km 6,700


VZOROVÉ PŘÍČNÉ ŘEZY, M 1 : 50

KATEGORIE P 4,0/30
JEDNOPRUHOVÁ, OBOUSMĚRNÁ

TŘÍDA DOPRAVNÍHO ZATÍŽENÍ VI
NÁVRHOVÁ ÚROVEŇ PORUŠENÍ D2
TYP PODLOŽÍ PII (PN 6-5)

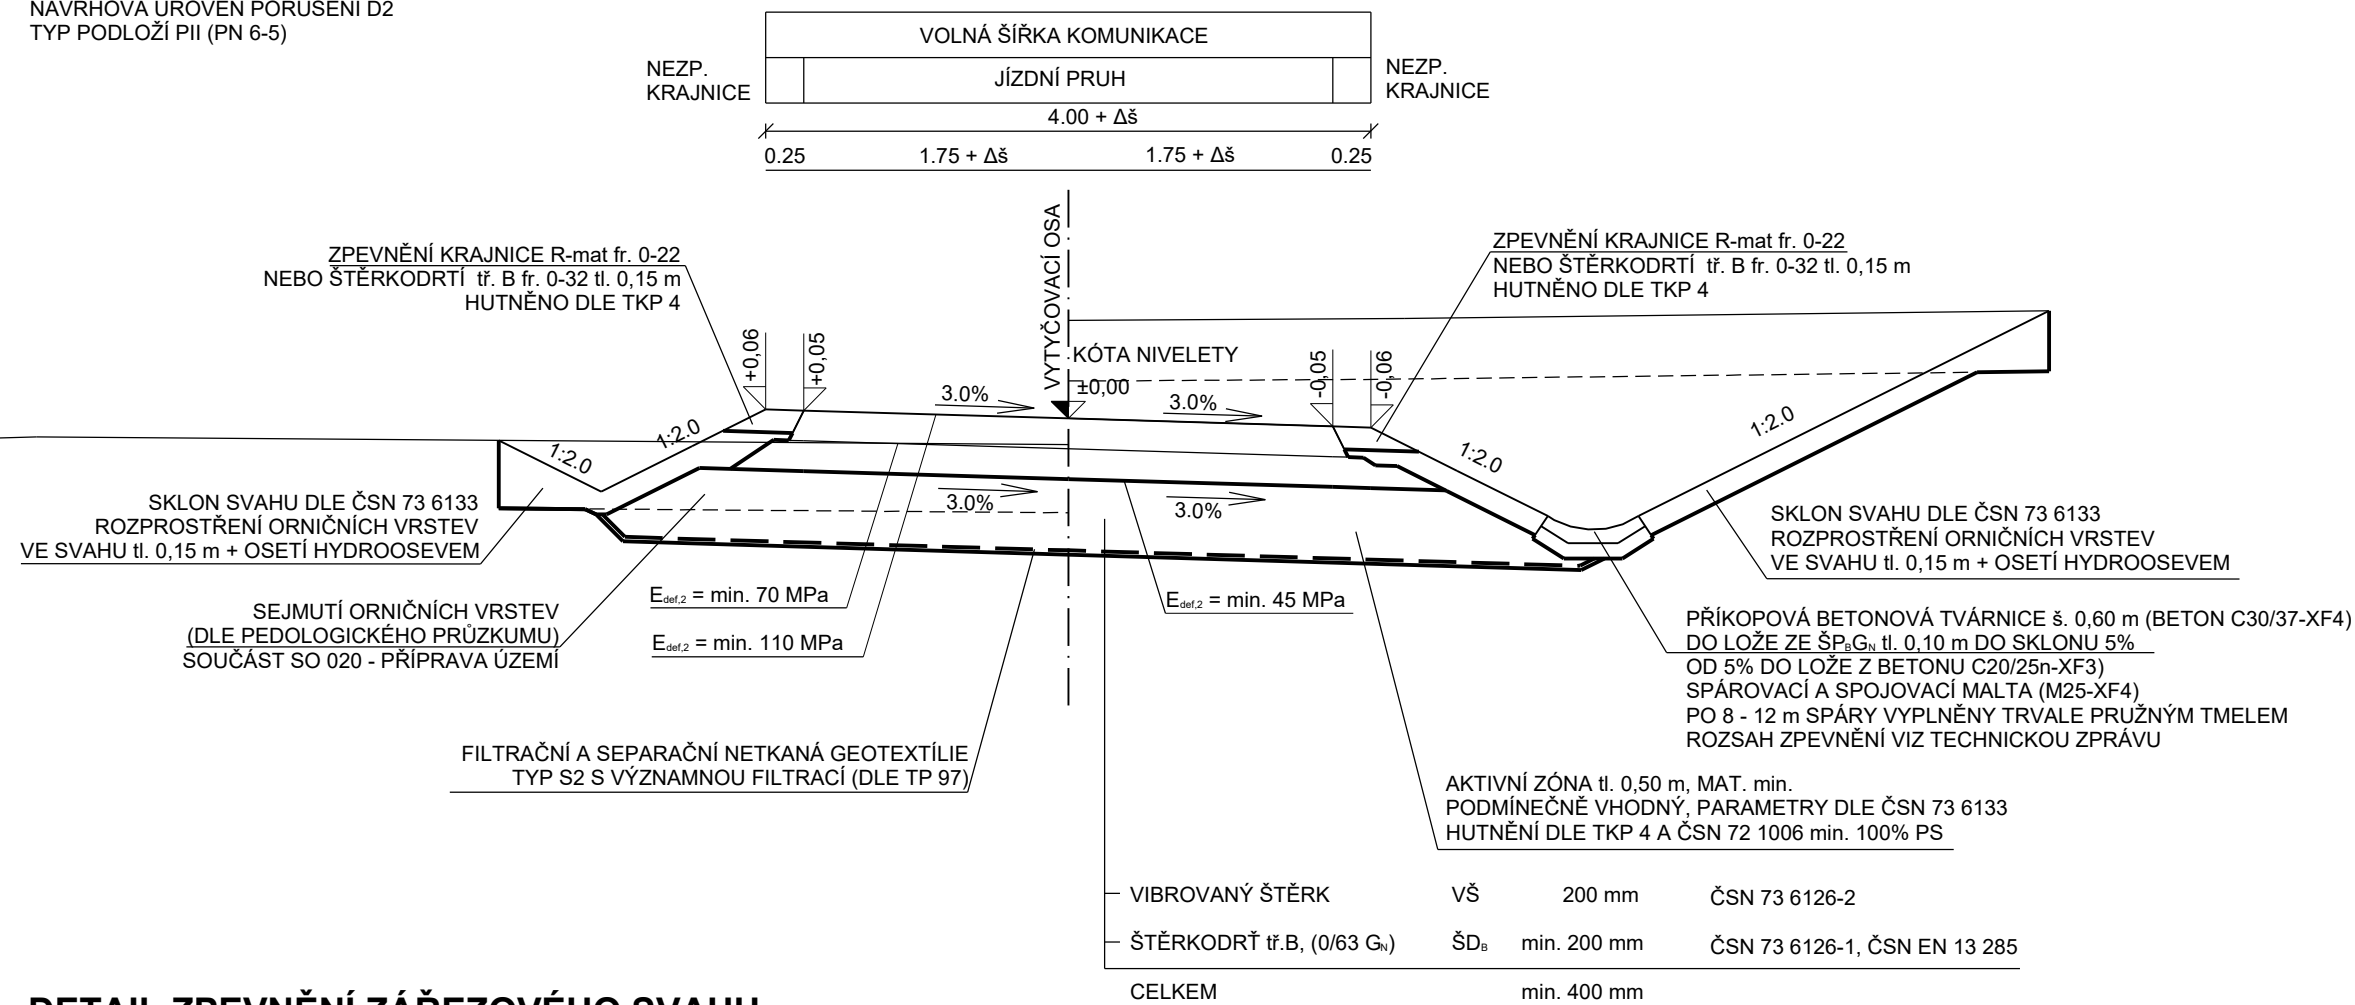

DETAIL ZPEVNĚNÍ ZÁŘEZOVÉHO SVAHU

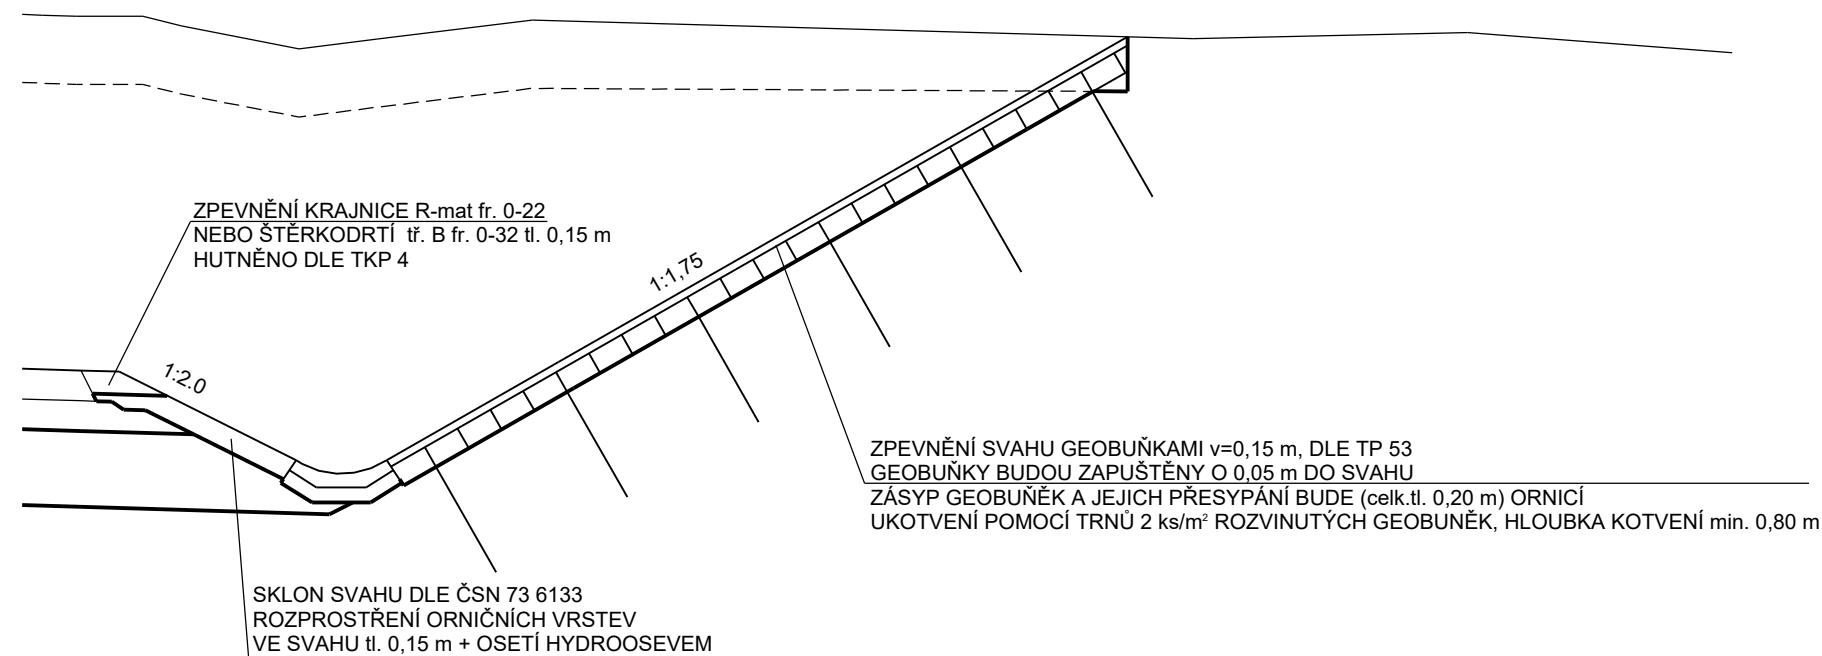

Výškový systém: Bpv

SO 154	Přeložka polní cesty v km 6,700
---------------	---------------------------------

Objednatel:

ŘEDITELSTVÍ SILNIC A DÁLNIC

Ředitelství silnic a dálnic s. p.

Čerčanská 2023/12, Krč, 140 00 Praha 4

Zhotovitel:

**Valbek, spol. s r.o.**

Vaňurova 505/17

460 07 Liberec 3

	Vypracoval	P. BARTUSEK	Zak. číslo	21-LI13-001
	Zodp. projektant	ING. T. KLIMENT	Datum	02/2025
	Tech. kontrola	ING. M. HANŽL	Stupeň	PDPS
	Akce I/16 MLADÁ BOLESLAV - MARTINOVICE		Počet formátů	3 x A4
			Měřítko	1 : 50
Zhotovitel: Valbek, spol. s r.o. Vaňurova 505/17 460 07 Liberec 3	Příloha VZOROVÉ PŘÍČNÉ ŘEZY		Č. přílohy 4	Paré