




SO 154 - PŘELOŽKA PNÍ CESTY V km 6,700
PŘÍČNÉ ŘEZY, M 1 : 100

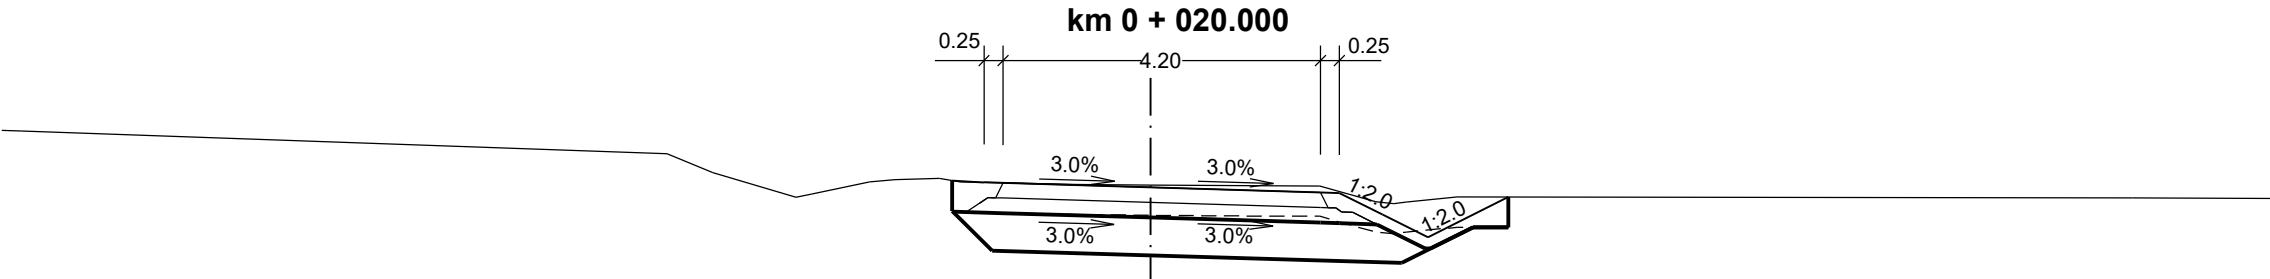


PROJEKTOVANÝ STAV	
ODSAZENÍ OD OSY	
STÁVAJÍCÍ TERÉN	12.89 229.88 -5.78 229.73 -4.48 229.40 -4.48 229.44 -3.72 229.60 -3.38 229.64 -2.78 229.65 -2.38 229.61 -1.98 229.58 -0.88 229.57 0.00 229.54 1.47 229.55 2.24 229.55 2.50 229.46 3.07 229.17 3.07 228.87 4.73 229.41
ODSAZENÍ OD OSY	

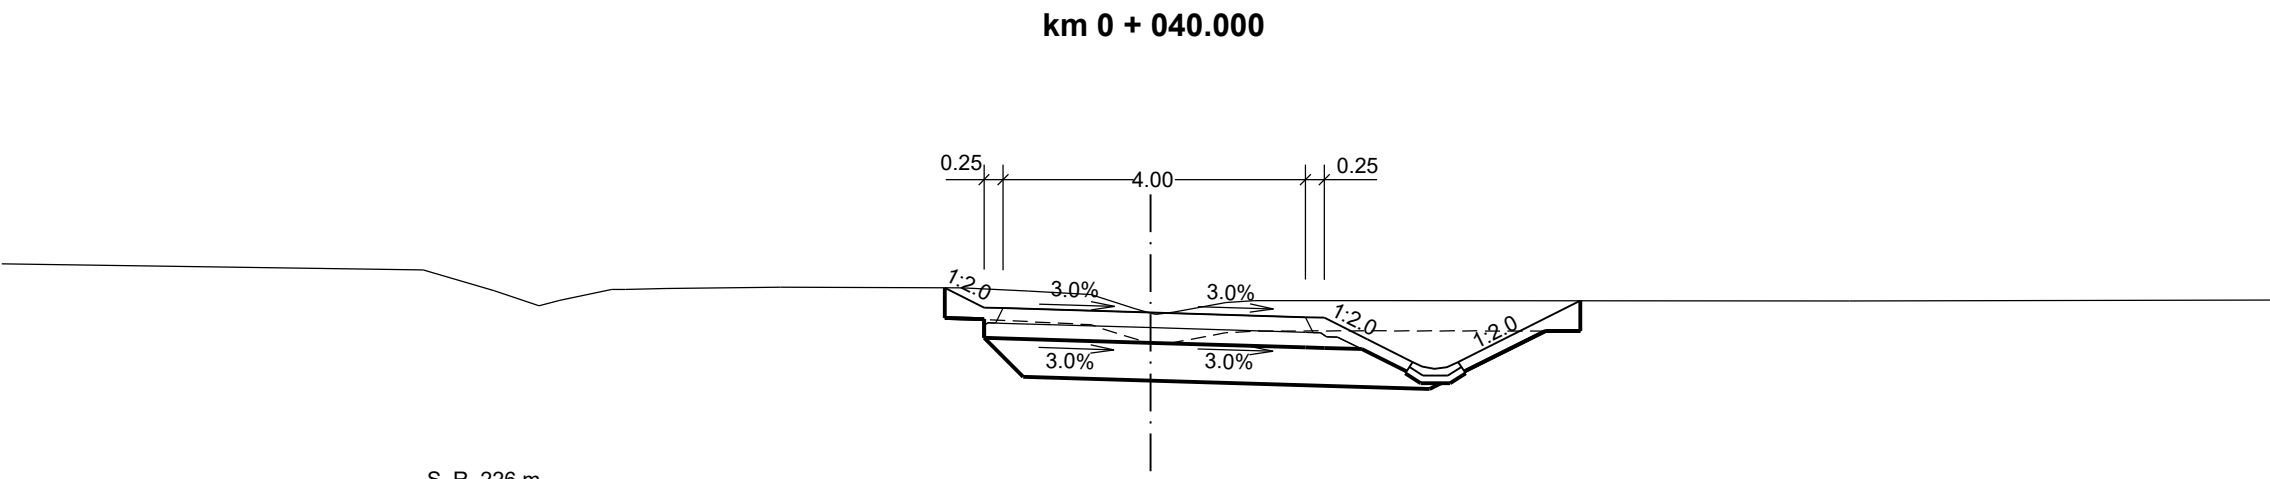


PROJEKTOVANÝ STAV	
ODSAZENÍ OD OSY	
STÁVAJÍCÍ TERÉN	-9.62 229.45 -8.68 229.17 -7.81 229.04 -7.13 229.19 -6.95 229.19 -6.41 229.20 -4.89 229.22
ODSAZENÍ OD OSY	

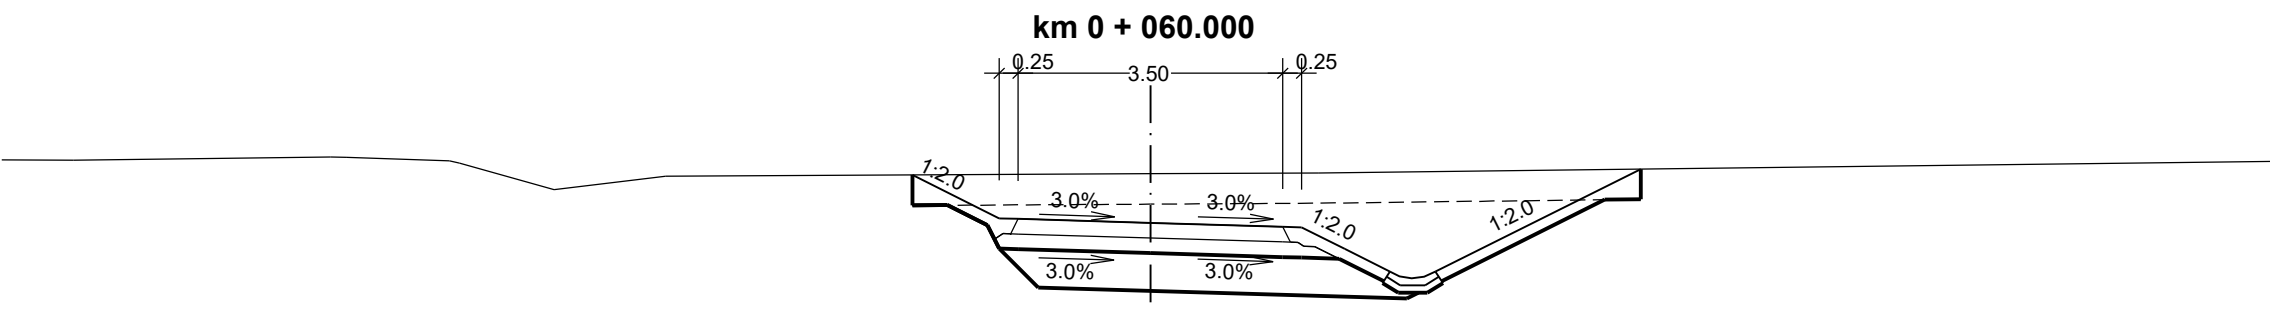


PROJEKTOVANÝ STAV	
ODSAZENÍ OD OSY	
STÁVAJÍCÍ TERÉN	-9.27 228.78 -5.14 228.75 -7.89 228.40 -6.41 228.58
ODSAZENÍ OD OSY	

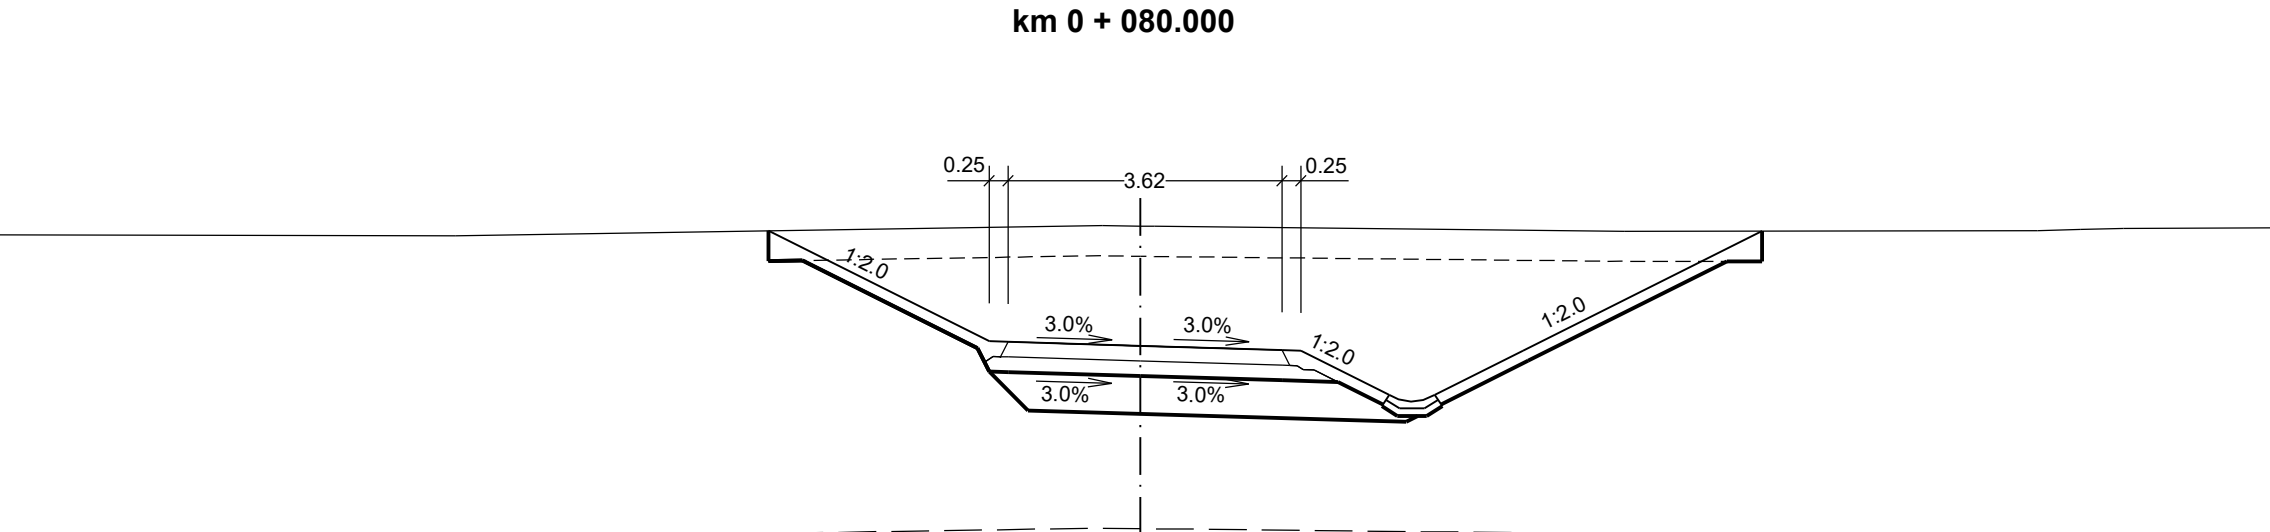


PROJEKTOVANÝ STAV	
ODSAZENÍ OD OSY	
STÁVAJÍCÍ TERÉN	11.87 228.31 12.44 228.32 13.00 228.34
ODSAZENÍ OD OSY	

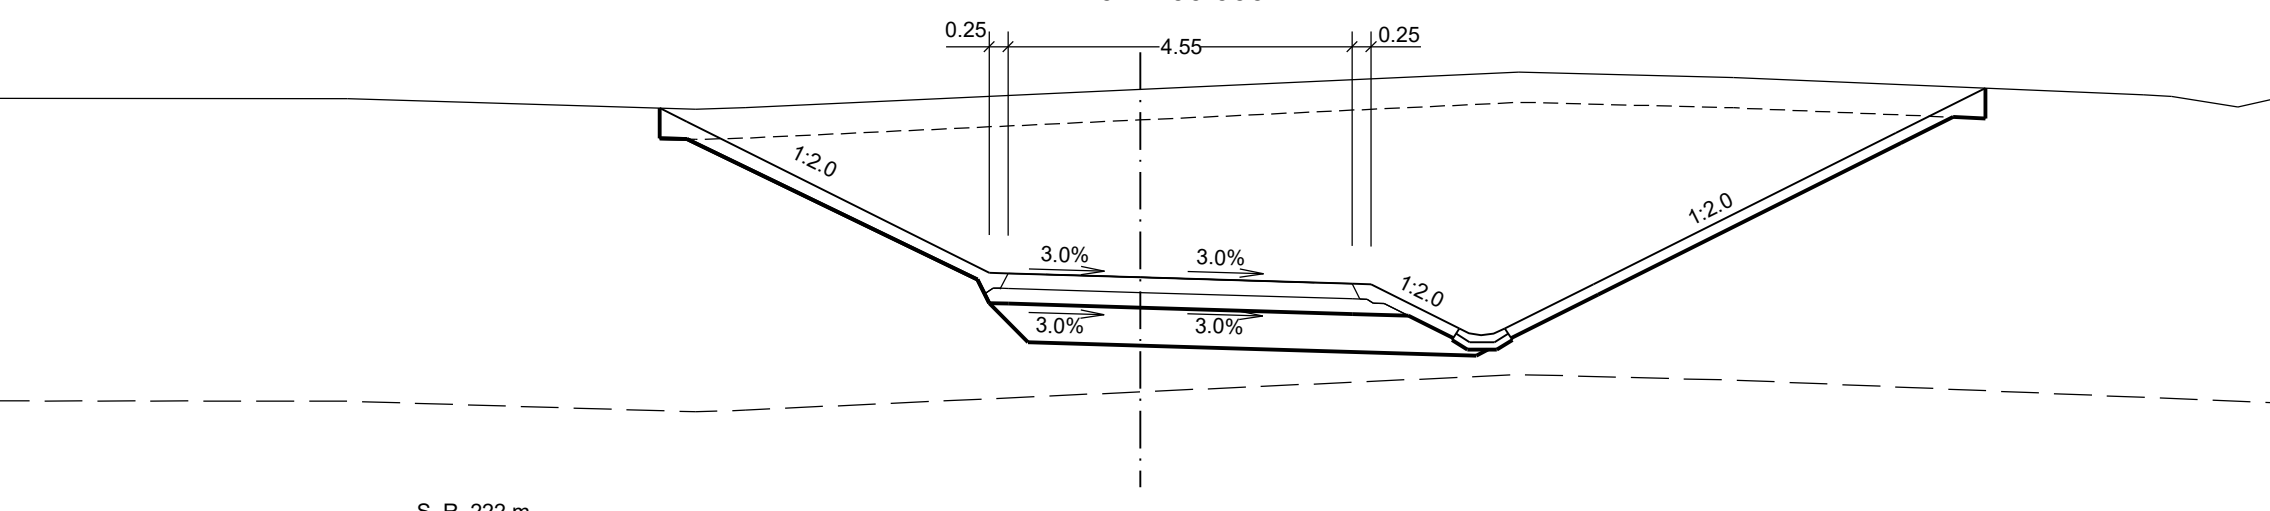


PROJEKTOVANÝ STAV	
ODSAZENÍ OD OSY	
STÁVAJÍCÍ TERÉN	13.39 229.18 13.84 229.17 14.62 229.02
ODSAZENÍ OD OSY	

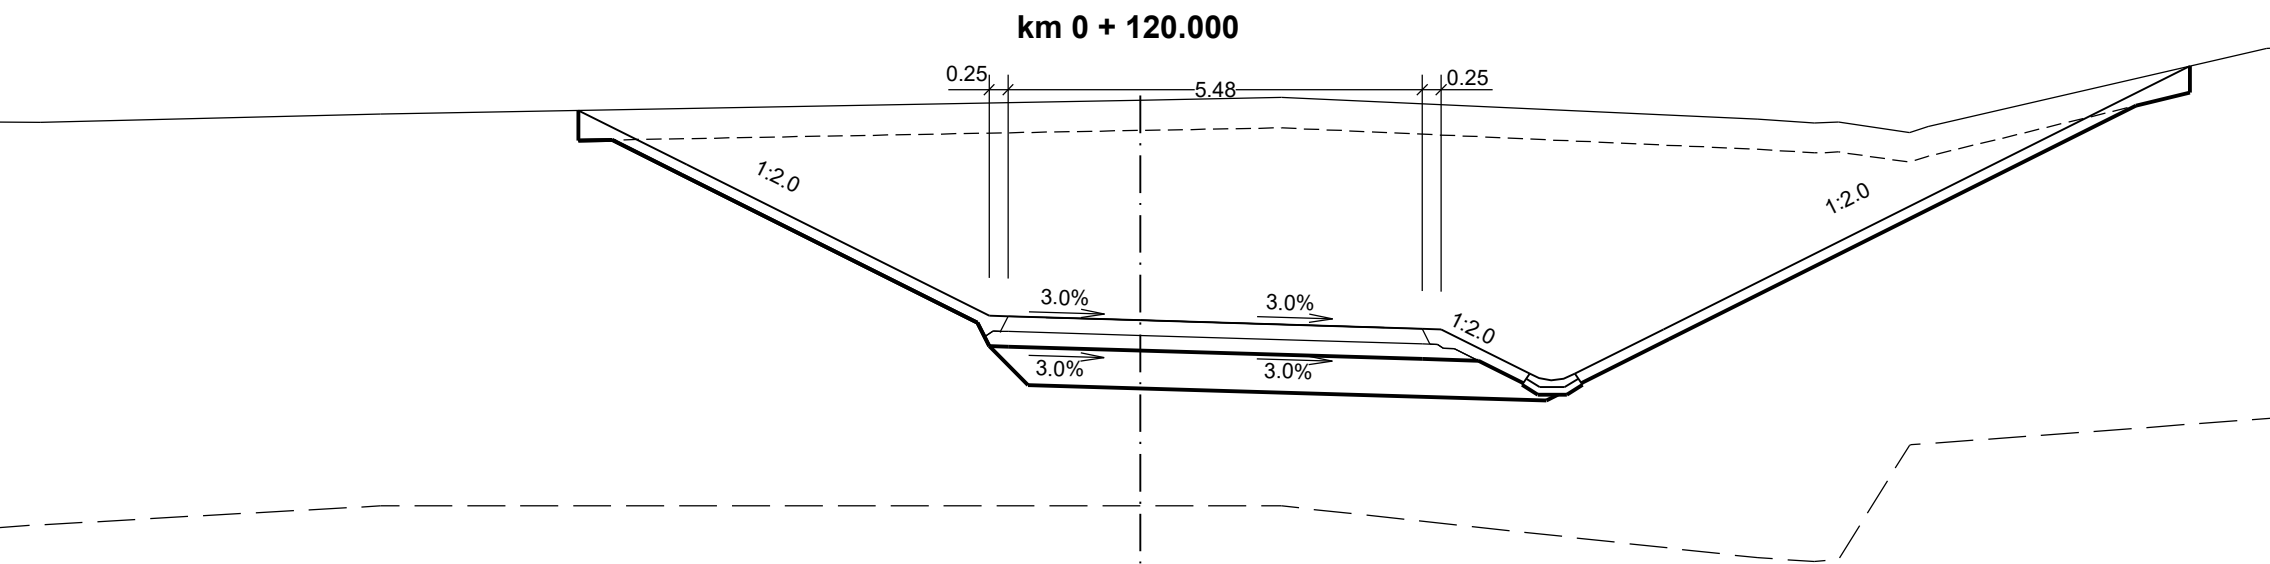


PROJEKTOVANÝ STAV	
ODSAZENÍ OD OSY	
STÁVAJÍCÍ TERÉN	13.86 228.56 14.95 228.80
ODSAZENÍ OD OSY	

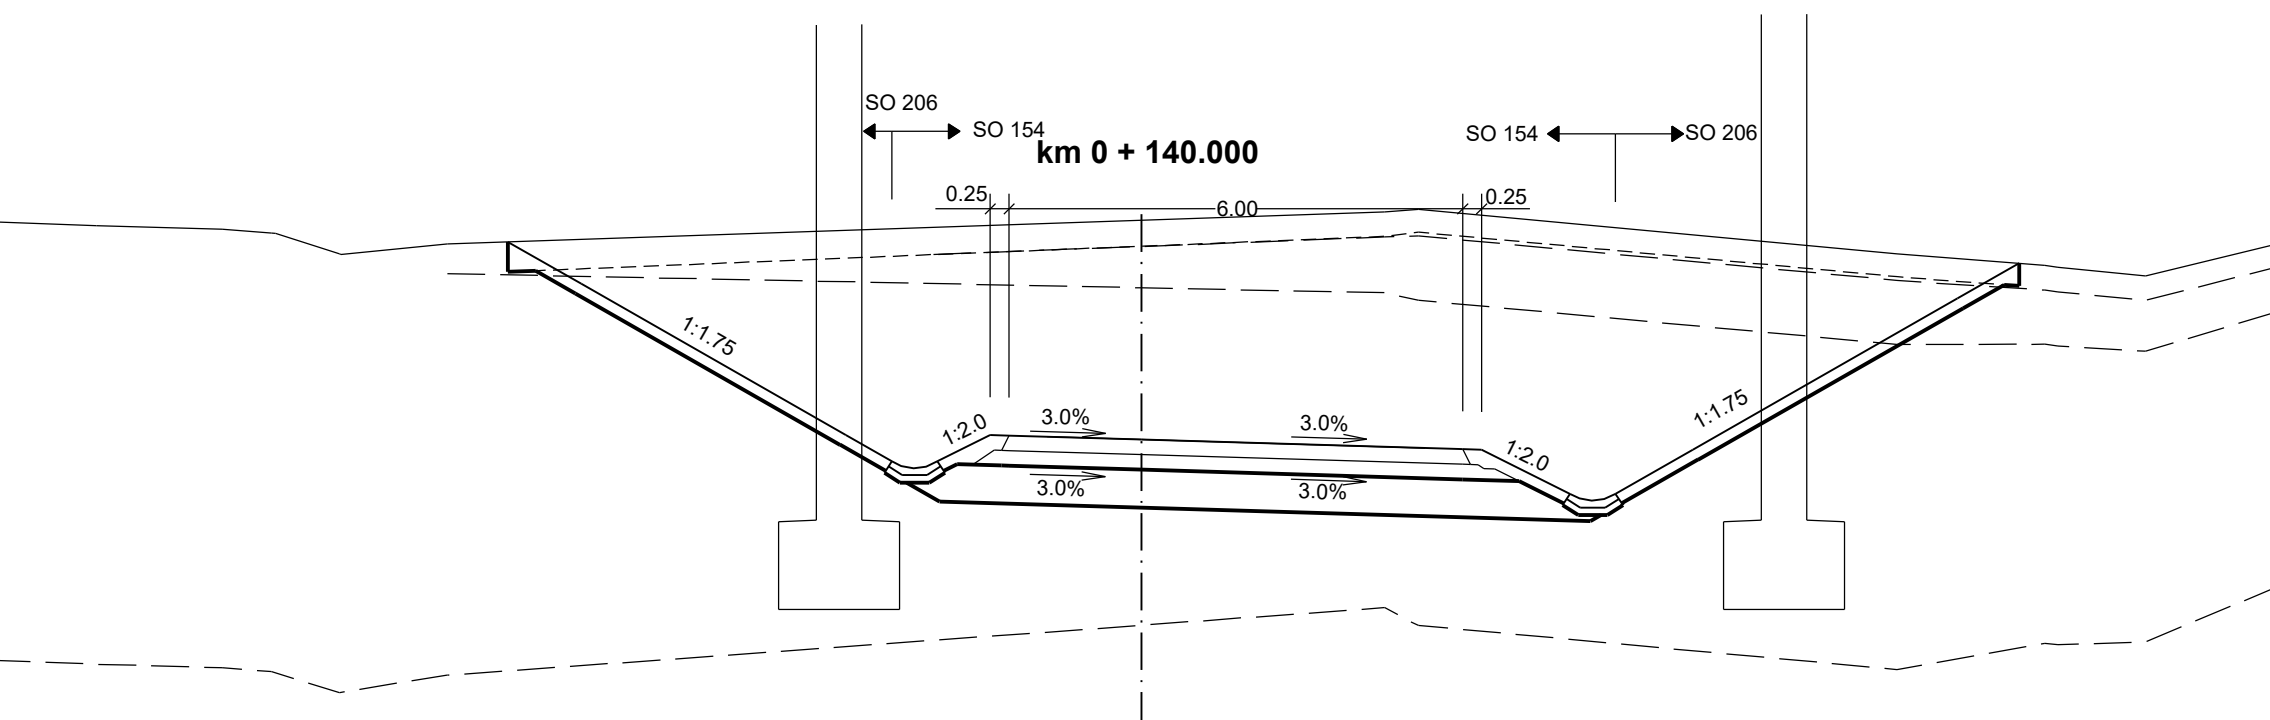


PROJEKTOVANÝ STAV	
ODSAZENÍ OD OSY	
STÁVAJÍCÍ TERÉN	11.87 228.31 12.44 228.32 13.00 228.34
ODSAZENÍ OD OSY	

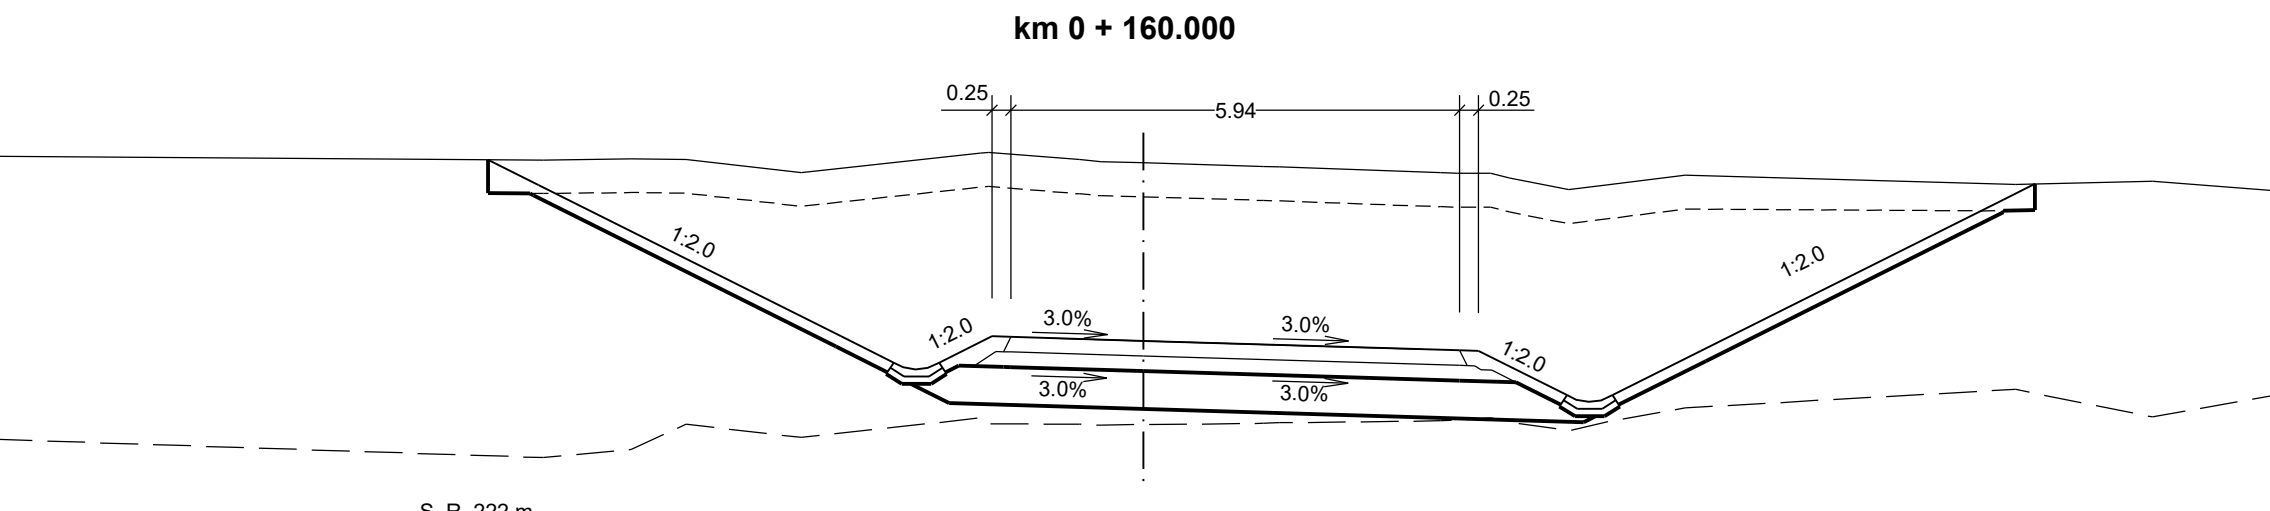


PROJEKTOVANÝ STAV	
ODSAZENÍ OD OSY	
STÁVAJÍCÍ TERÉN	13.35 227.04 13.84 227.03 14.62 226.80
ODSAZENÍ OD OSY	

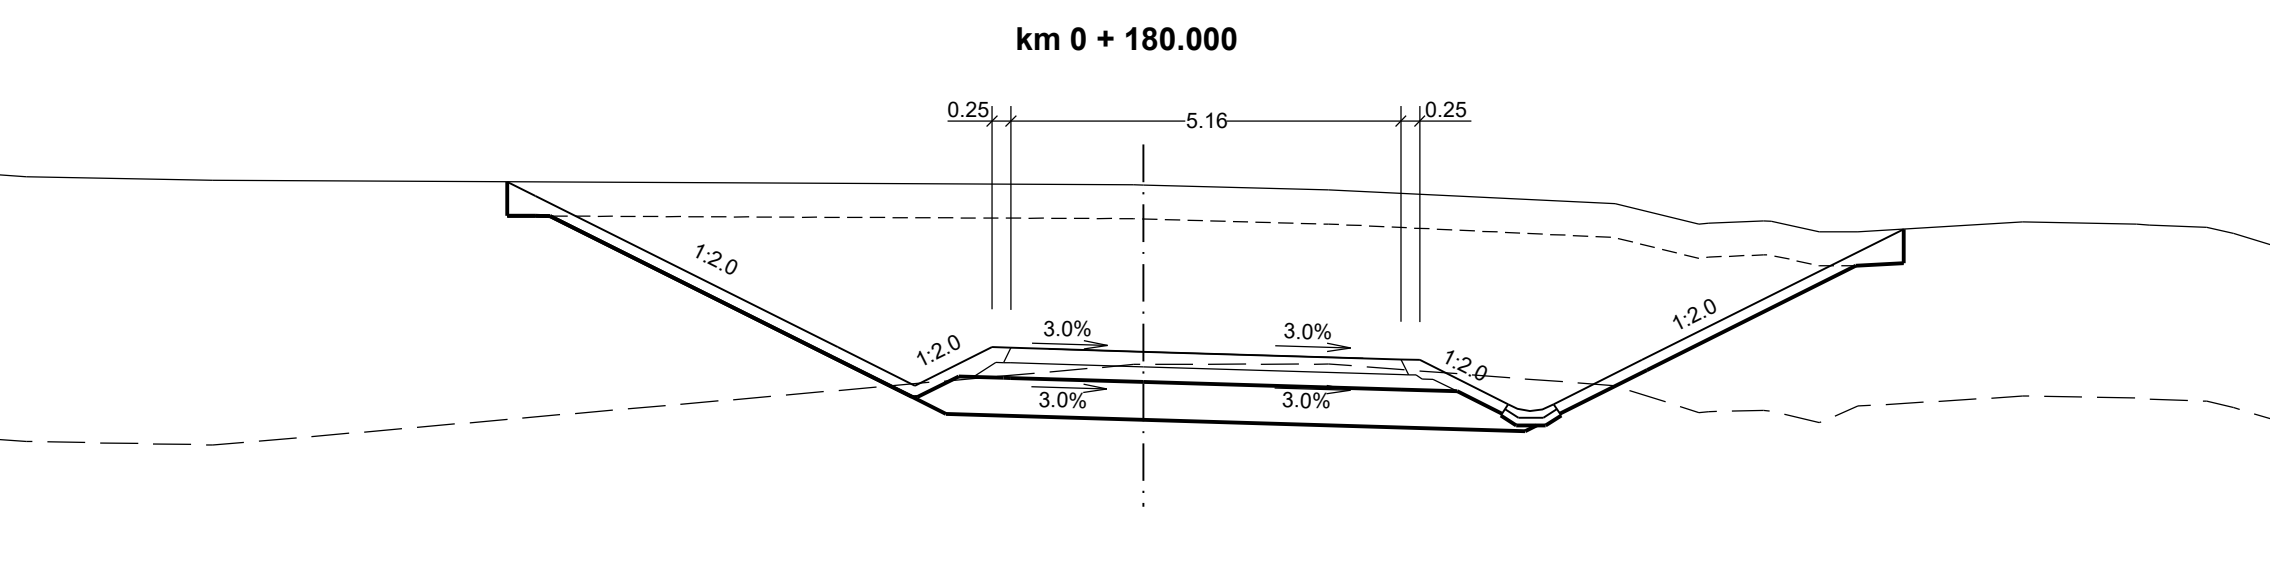


PROJEKTOVANÝ STAV	
ODSAZENÍ OD OSY	
STÁVAJÍCÍ TERÉN	11.83 226.50 12.44 226.51 13.00 226.52 13.31 226.47 14.07 226.43 14.42 226.35
ODSAZENÍ OD OSY	

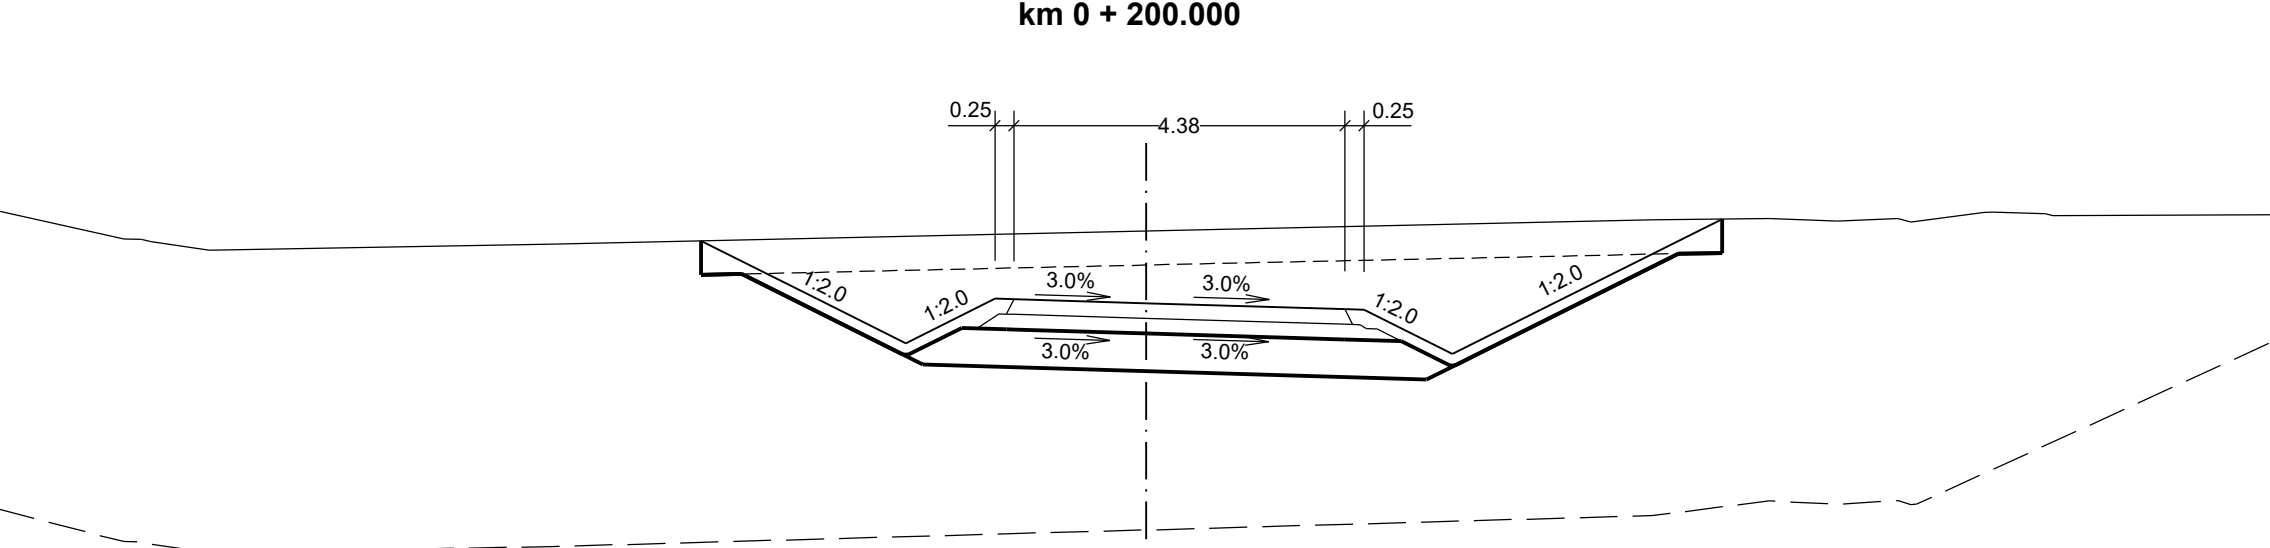


PROJEKTOVANÝ STAV	
ODSAZENÍ OD OSY	
STÁVAJÍCÍ TERÉN	11.87 228.31 12.44 228.32 13.00 228.34
ODSAZENÍ OD OSY	

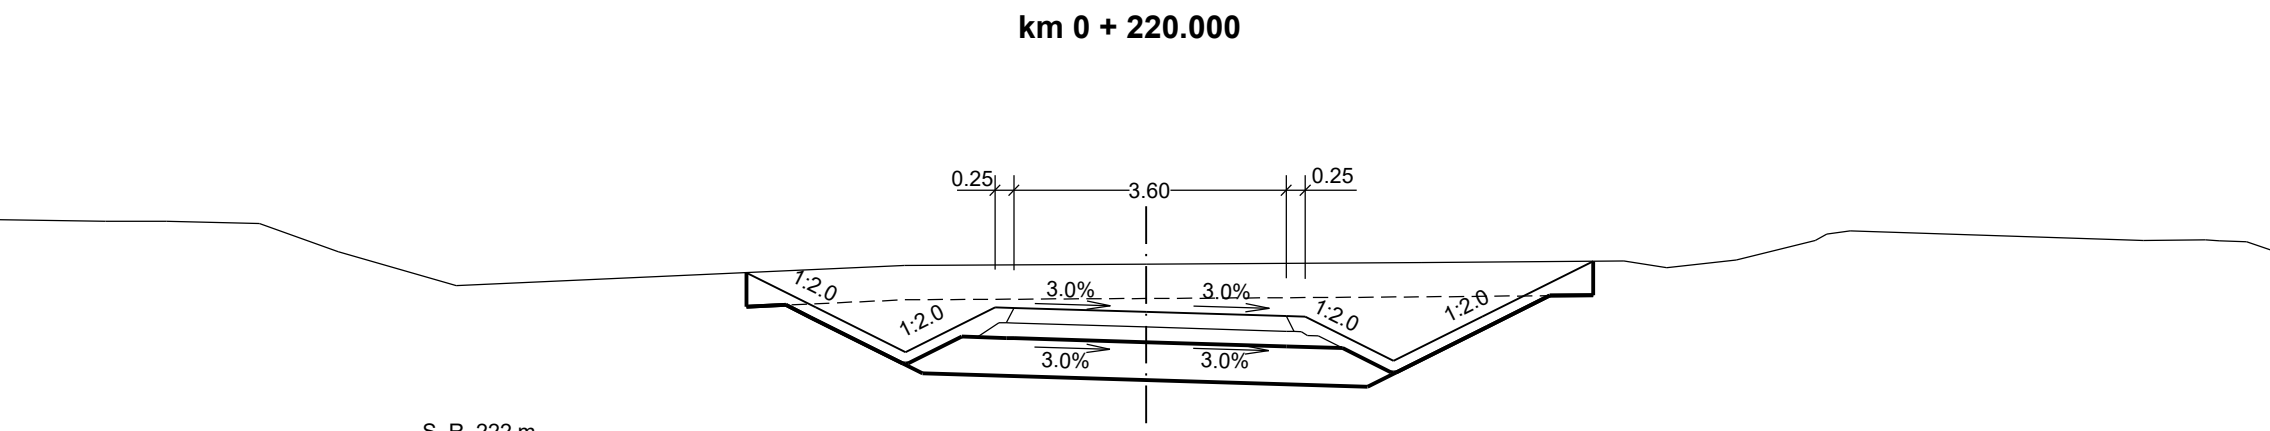


PROJEKTOVANÝ STAV	
ODSAZENÍ OD OSY	
STÁVAJÍCÍ TERÉN	13.19 225.20 14.51 225.21 14.50 225.20 14.56 225.18
ODSAZENÍ OD OSY	

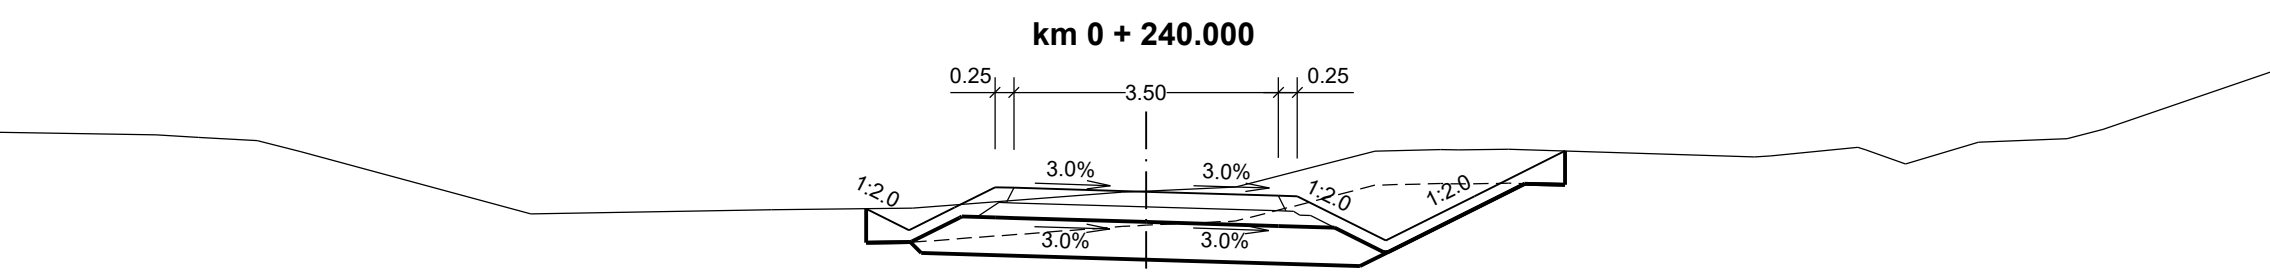

PROJEKTOVANÝ STAV	
ODSAZENÍ OD OSY	
STÁVAJÍCÍ TERÉN	11.87 228.31 12.44 228.32 13.00 228.34
ODSAZENÍ OD OSY	

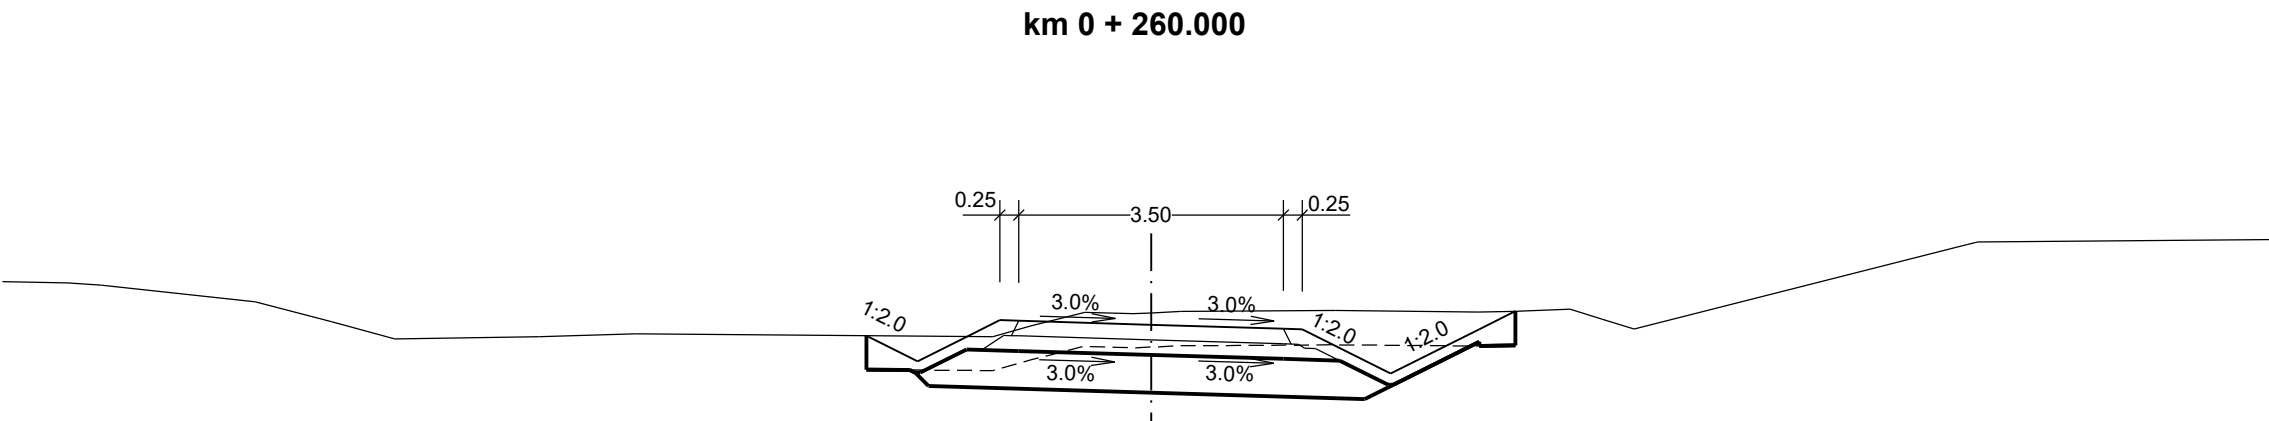

PROJEKTOVANÝ STAV	
ODSAZENÍ OD OSY	
STÁVAJÍCÍ TERÉN	11.87 228.31 12.44 228.32 13.00 228.34
ODSAZENÍ OD OSY	

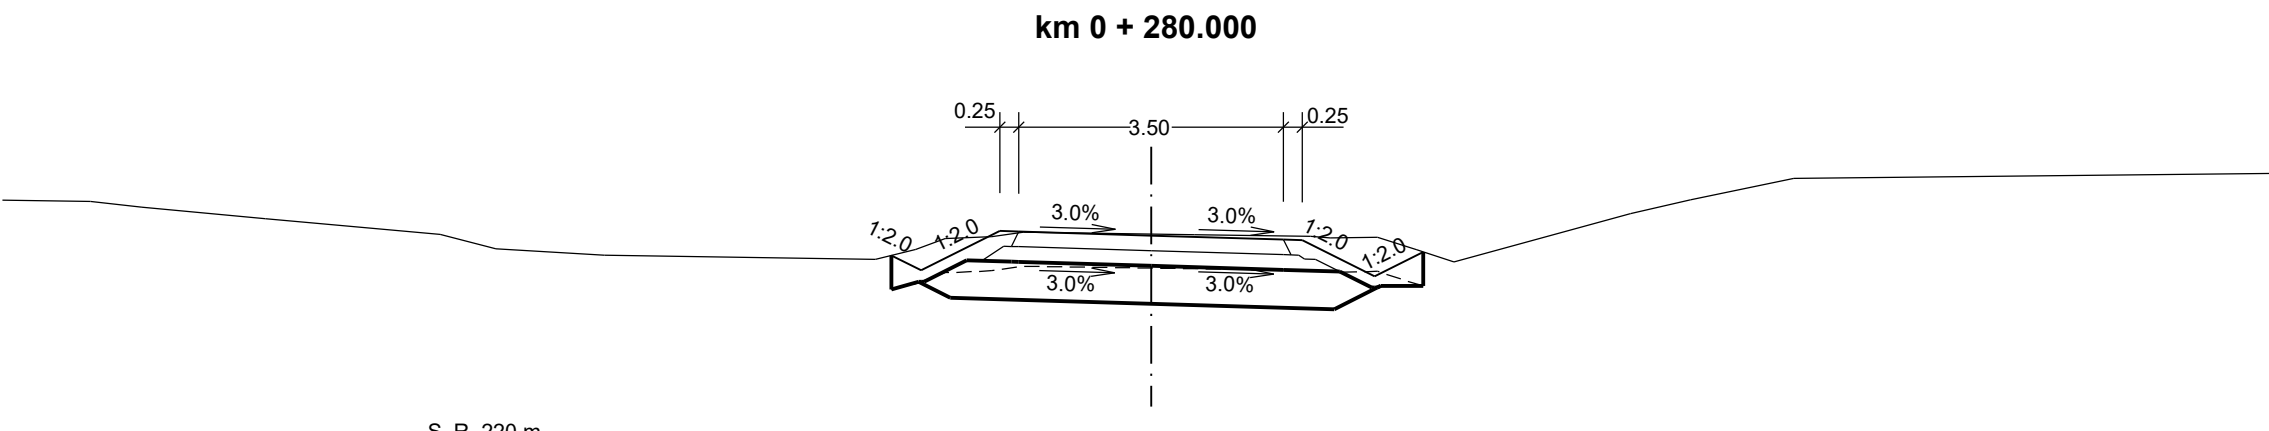

PROJEKTOVANÝ STAV	
ODSAZENÍ OD OSY	
STÁVAJÍCÍ TERÉN	11.87 228.31 12.44 228.32 13.00 228.34
ODSAZENÍ OD OSY	

Výškový systém: Bpv

SO 154 Přeložka polní cesty v km 6,700

Objednatel:
**ŘEDITELSTVÍ
SILNIC
A DÁLNIC**

Ředitelství silnic a dálnic s. p.
Čertánská 2023/12, Krč, 140 00 Praha 4

Zhotovitel:
**Valbek**

Valbek, spol. s r.o.
Vaňurova 505/17
460 07 Liberec 3

 Valbek	Vypracoval	P. BARTUSEK	Zak. číslo	21-L113-001
	Zodp. projektant	ING. T. KLIMENT	Datum	02/2025
	Tech. kontrola	ING. M. HANŽL	Stupeň	PDPS
	Akce	I/16 MLADÁ BOLESLAV - MARTINOVICE	Počet formátů	18 x A4
Zhotovitel: Valbek, spol. s r.o. Vaňurova 505/17 460 07 Liberec 3	Příloha	PŘÍČNÉ ŘEZY	Měřítko	1 : 100
			Č. přílohy	5