


SO 171 - PROVIZORNÍ PŘELOŽKA I/16
SITUACE, M 1 : 1 000

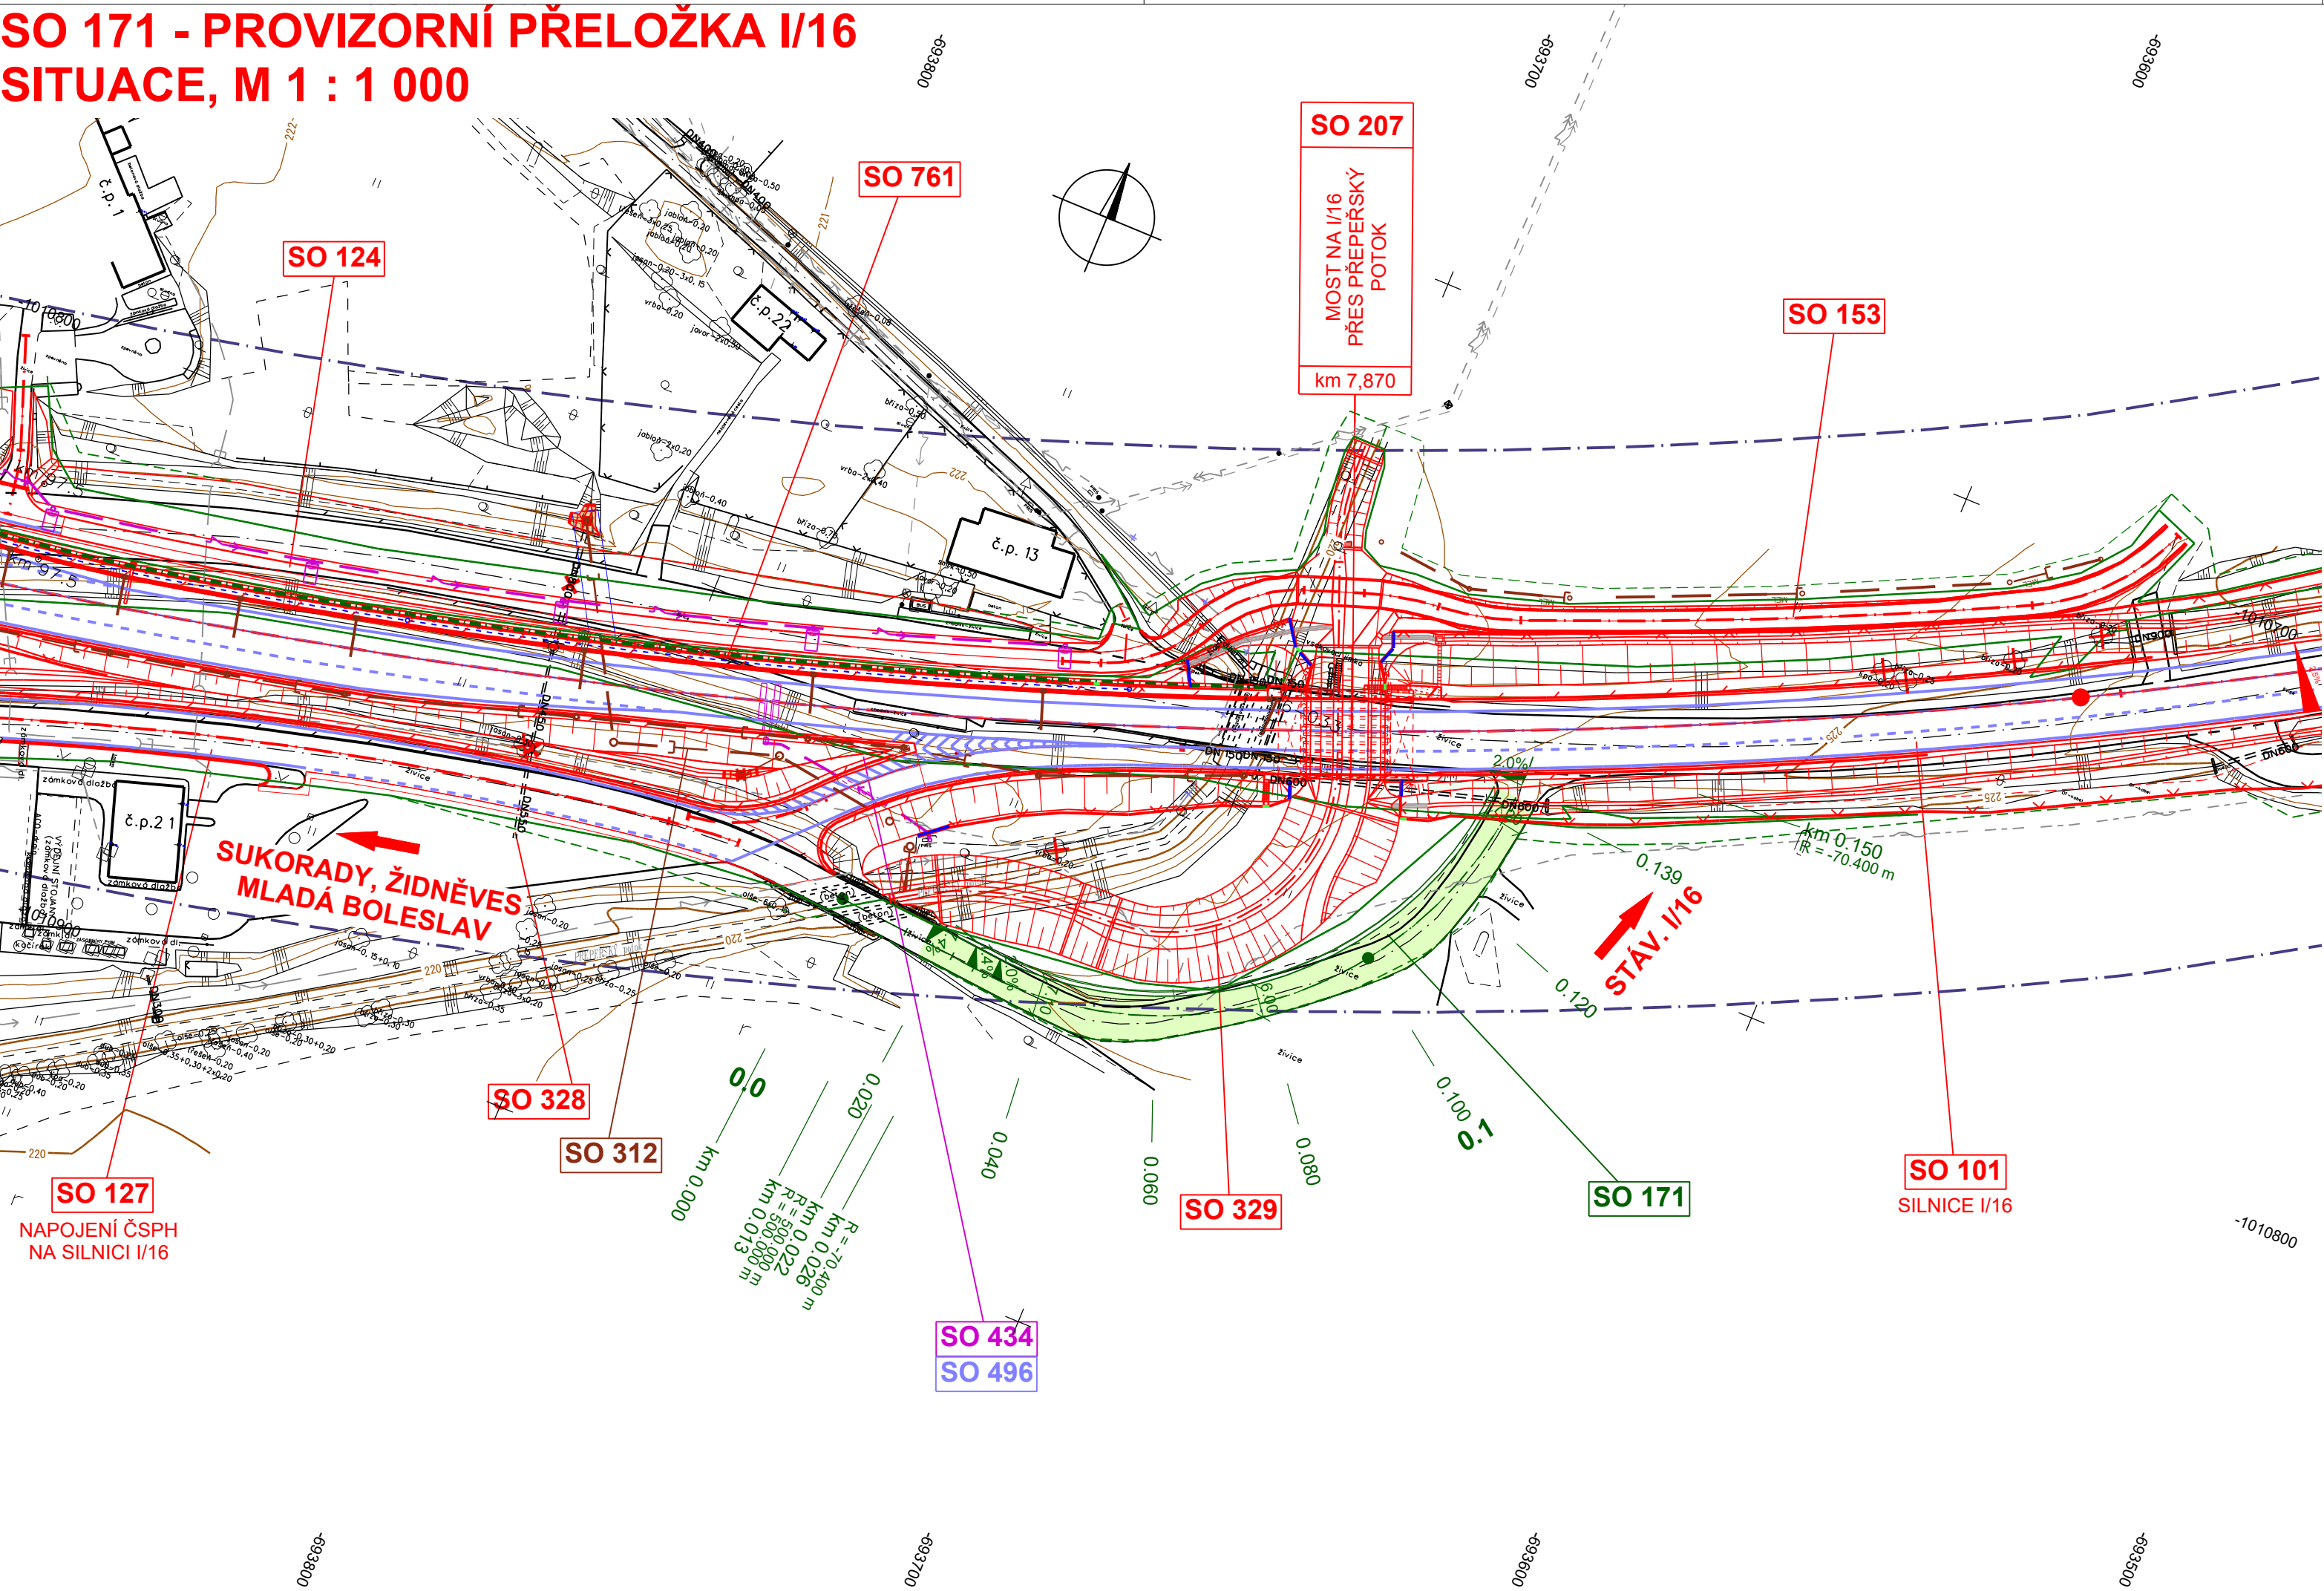

LEGENDA:

PLOCHY

- DS_PROVIZORNI-VOZOVKA
- SVAHY VÝKOPU

NOVÉ IS

- DEŠŤOVÁ KANALIZACE
- MELIORACE
- VÝTLAK
- VODOVOD
- NADZEMNÍ VEDENÍ NN
- NADZEMNÍ VEDENÍ VN
- PODZEMNÍ VEDENÍ NN
- PODZEMNÍ SDĚLOVACÍ VEDENÍ
- PLYNOVOD - STL

STÁVAJÍCÍ IS - INFORMATIVNÍ ZÁKRES

- PODZEMNÍ VEDENÍ NN
- PODZEMNÍ VEDENÍ VN
- NADZEMNÍ VEDENÍ NN
- NADZEMNÍ VEDENÍ VN
- NADZEMNÍ VEDENÍ VVN
- DEŠŤOVÁ KANALIZACE
- PLYNOVOD - STL
- PODZEMNÍ SDĚLOVACÍ VEDENÍ
- VODOVOD

Souřadnicový systém: S-JTSK
Výškový systém: BpV

SO 171 Provizorní přeložka I/16

Objednatel:



ŘEDITELSTVÍ
SILNIC
A DÁLNIC

Ředitelství silnic a dálnic s. p.
Čerčanská 2023/12, Krč, 140 00 Praha 4

Zhotovitel:



Valbek, spol. s r.o.
Vaňurova 505/17
460 07 Liberec 3



Vypracoval P. MATYS
Zodp. projektant ING. T. KLIMENT
Tech. kontrola ING. M. HANŽL

Akce
I/16 MLADÁ BOLESLAV - MARTINOVICE

Příloha
SITUACE

Zak. číslo 21-LI13-001
Datum 02 / 2025
Stupeň PDPS
Počet formátů 3 x A4
Měřítko 1 : 1 000
Č. přílohy Paré

2

Zhotovitel:
Valbek, spol. s r.o.
Vaňurova 505/17
460 07 Liberec 3