


SO 171 - PROVIZORNÍ PŘELOŽKA I/16

PODÉLNÝ PROFIL, M 1 : 1000 / 100

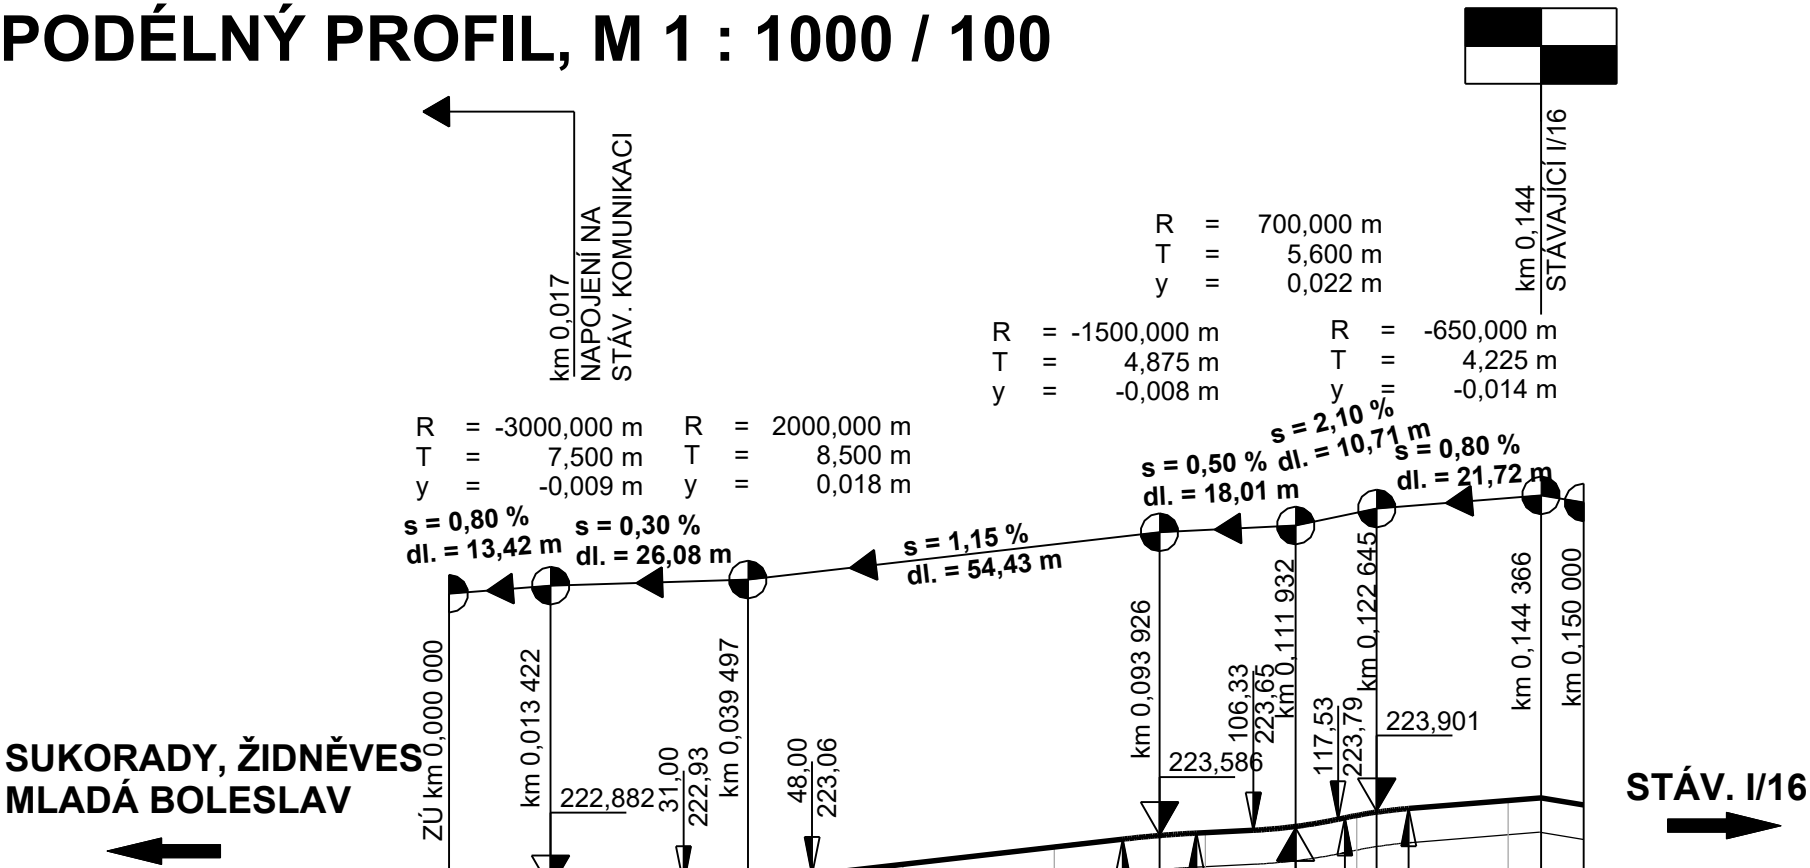


SUKORADY, ŽIDNĚVES
MLADÁ BOLESLAV

STÁV. I/16

Bpv 219 m

KÓTY NIVELETY	222,77	222,87	222,90	222,98	222,98	223,20	223,43	223,58	223,62	223,70	223,84	223,89	224,04	224,07	223,98
KÓTY TERÉNU	222,77	222,87	222,91	222,98	222,98	223,20	223,42	223,57	223,61	223,70	223,85	223,88	224,04	224,07	223,98
STANIČENÍ	0,00	13,42	20,00	39,50	40,00	60,00	80,00	93,93	100,00	111,93	120,00	122,64	140,00	144,37	150,00

km 0+000 0+100

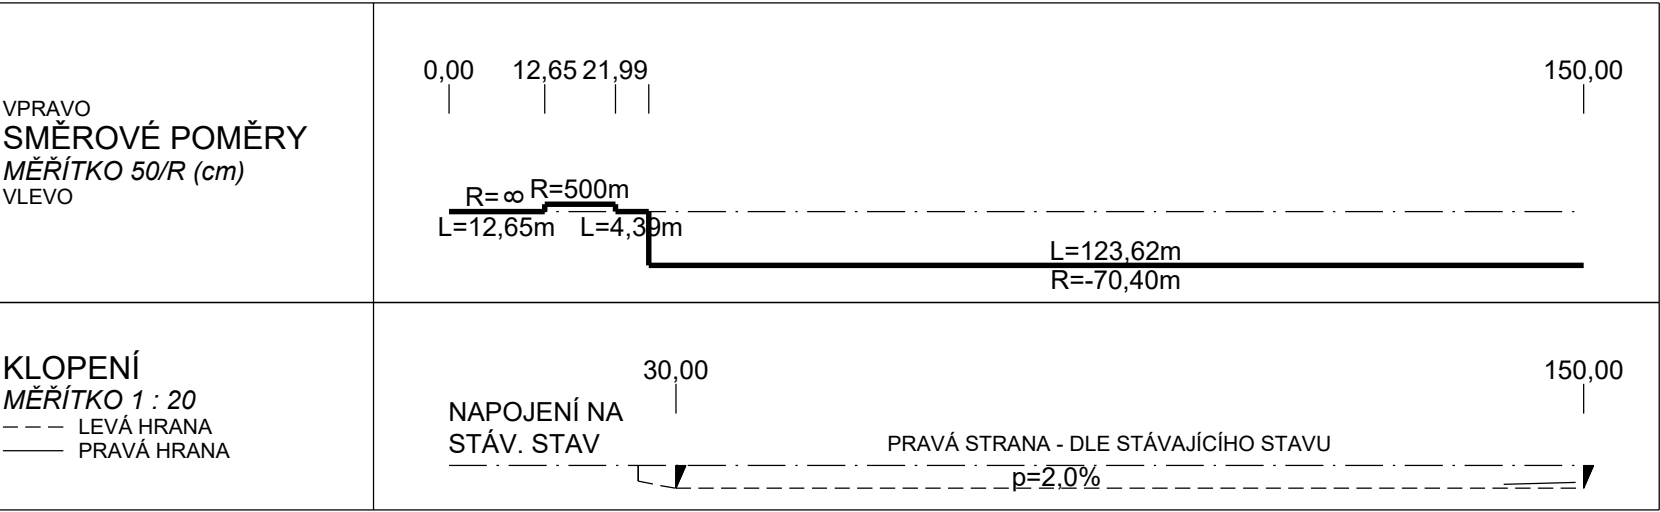

VPRAVO
SMĚROVÉ POMĚRY
MĚŘÍTKO 50/R (cm)
VLEVO

KLOPENÍ
MĚŘÍTKO 1 : 20
--- LEVÁ HRANA
—— PRAVÁ HRANA

Výškový systém Bpv

SO 171 Provizorní přeložka I/16

Objednatel:



ŘEDITELSTVÍ
SILNIC
A DÁLNIC

Ředitelství silnic a dálnic s. p.
Čerčanská 2023/12, Krč, 140 00 Praha 4

Zhotovitel:



Valbek

Valbek, spol. s r.o.
Vaňurova 505/17
460 07 Liberec 3

	Vypracoval	P. MATYS		Zak. číslo	21-LI13-001
	Zodp. projektant	ING. T. KLIMENT		Datum	02 / 2025
	Tech. kontrola	ING. M. HANŽL		Stupeň	PDPS
	Akce I/16 MLADÁ BOLESLAV - MARTINOVICE			Počet formátů	2 x A4
				Měřítko	1 : 1 000 / 100
Zhotovitel: Valbek, spol. s r.o. Vaňurova 505/17 460 07 Liberec 3	Příloha PODÉLNÝ PROFIL			Č. přílohy 3	Paré