


SO 171 - PROVIZORNÍ PŘELOŽKA I/16

VZOROVÝ PŘÍČNÝ ŘEZ, M 1 : 50

PROVIZORNÍ PŘELOŽKA

TŘÍDA DOPRAVNÍHO ZATÍŽENÍ IV
NÁVRHOVÁ ÚROVEŇ PORUŠENÍ D1
TYP PODLOŽÍ PIII (D1-A-2)

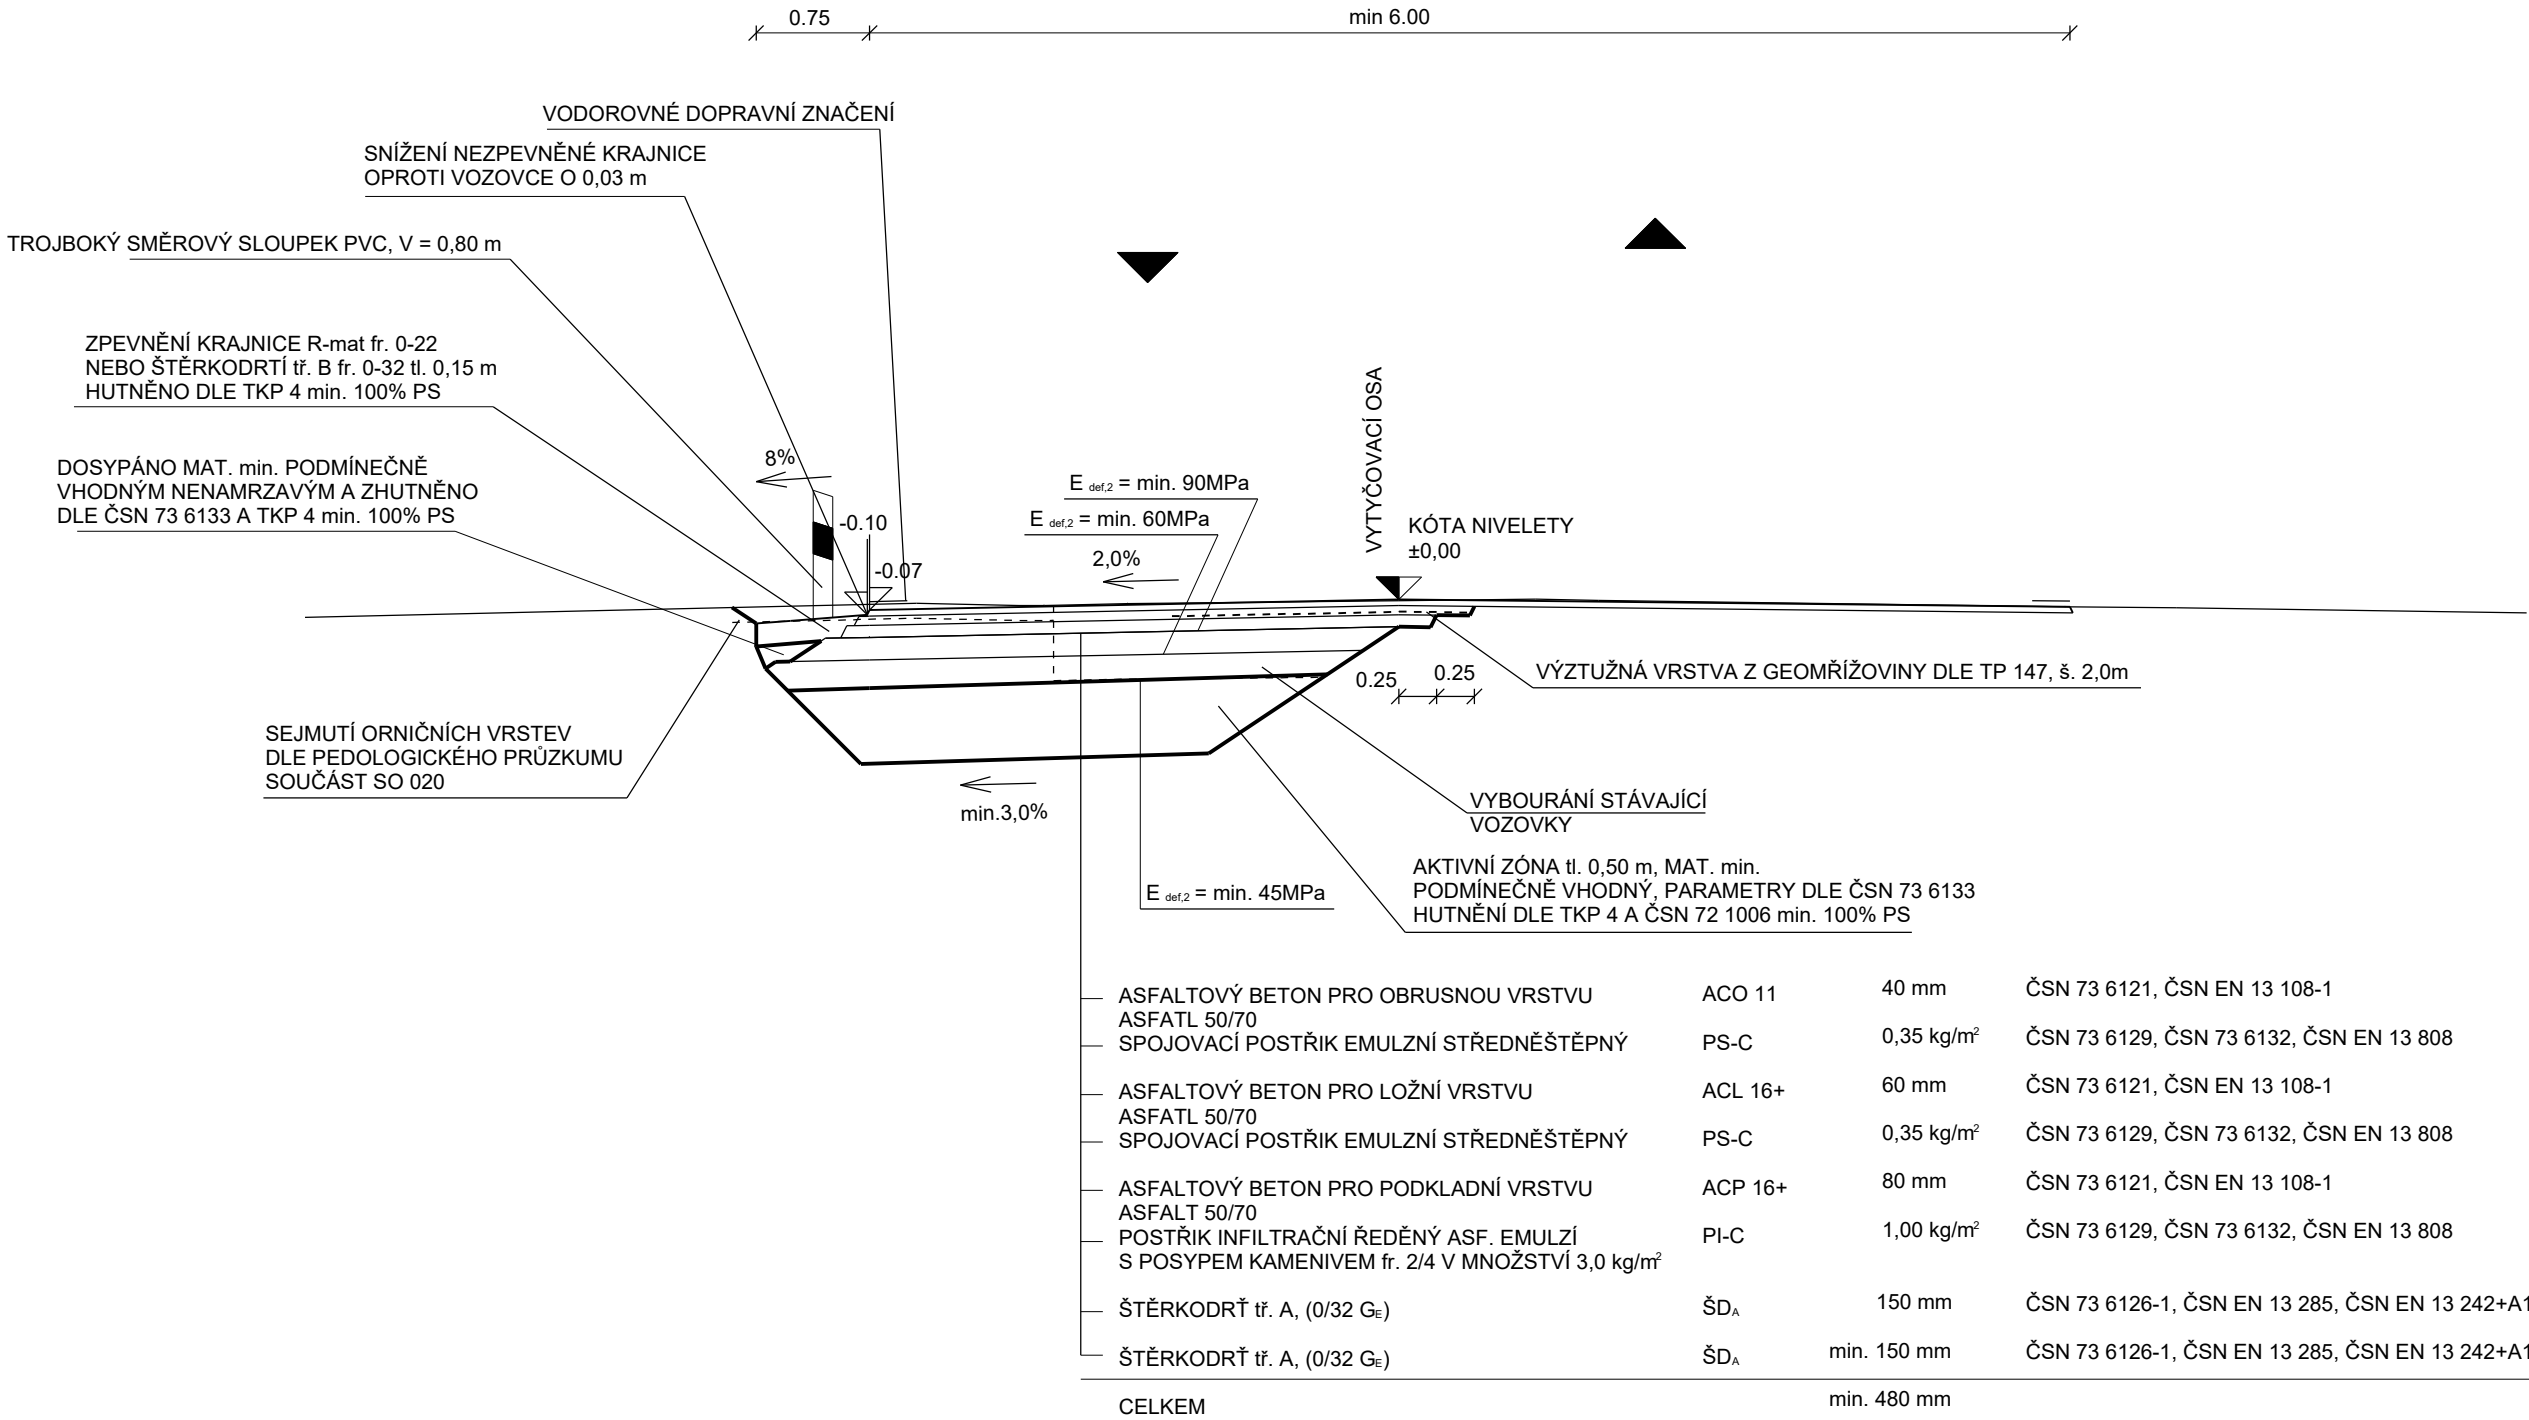

SO 171 Provizorní přeložka I/16

Objednatel:



ŘEDITELSTVÍ
SILNIC
A DÁLNIC

Ředitelství silnic a dálnic s. p.

Čerčanská 2023/12, Krč, 140 00 Praha 4

Zhotovitel:



Valbek, spol. s r.o.

Vaňurova 505/17
460 07 Liberec 3



Vypracoval P. MATYS
Zodp. projektant ING. T. KLIMENT
Tech. kontrola ING. M. HANŽL

I/16 MLADÁ BOLESLAV - MARTINOVICE

Zhotovitel:
Valbek, spol. s r.o.
Vaňurova 505/17
460 07 Liberec 3

Příloha
VZOROVÝ PŘÍČNÝ ŘEZ

Zak. číslo 21-LI13-001
Datum 02 / 2025
Stupeň PDPS
Počet formátů 3 x A4
Měřítko 1 : 50
Č. přílohy Paré

4