

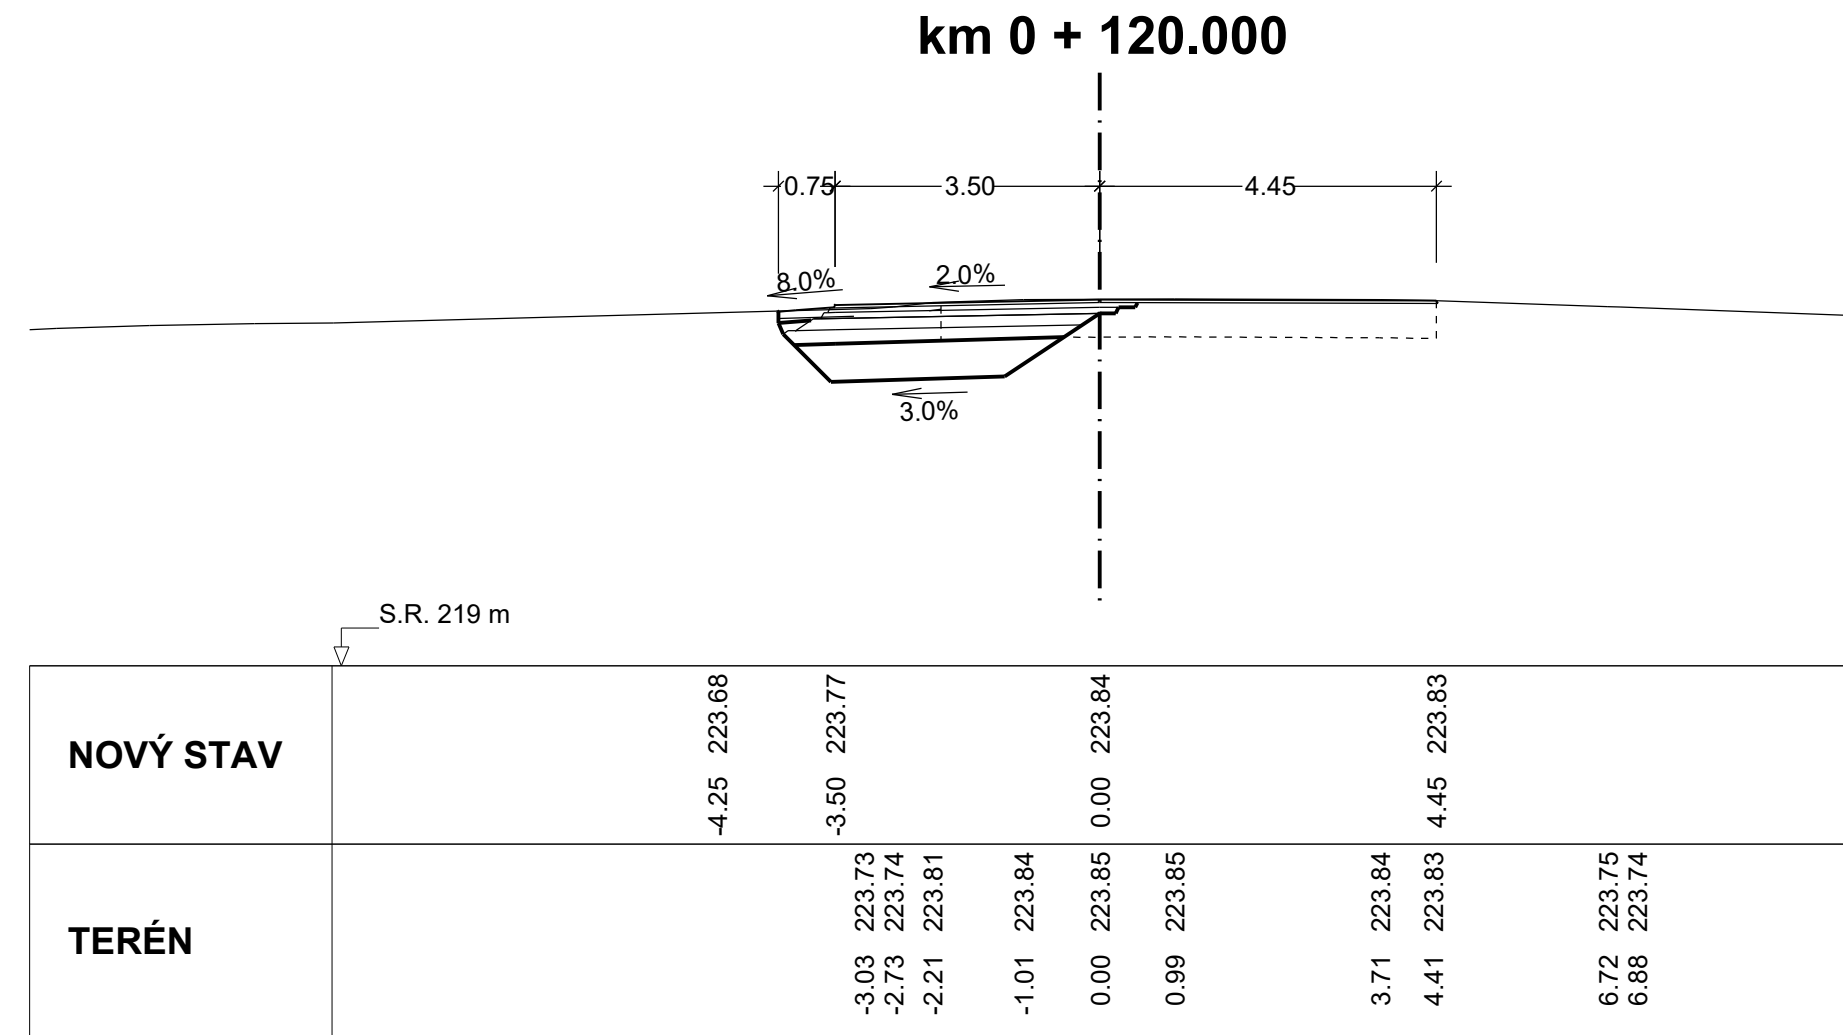


PŘÍČNÉ ŘEZY, M 1 : 100

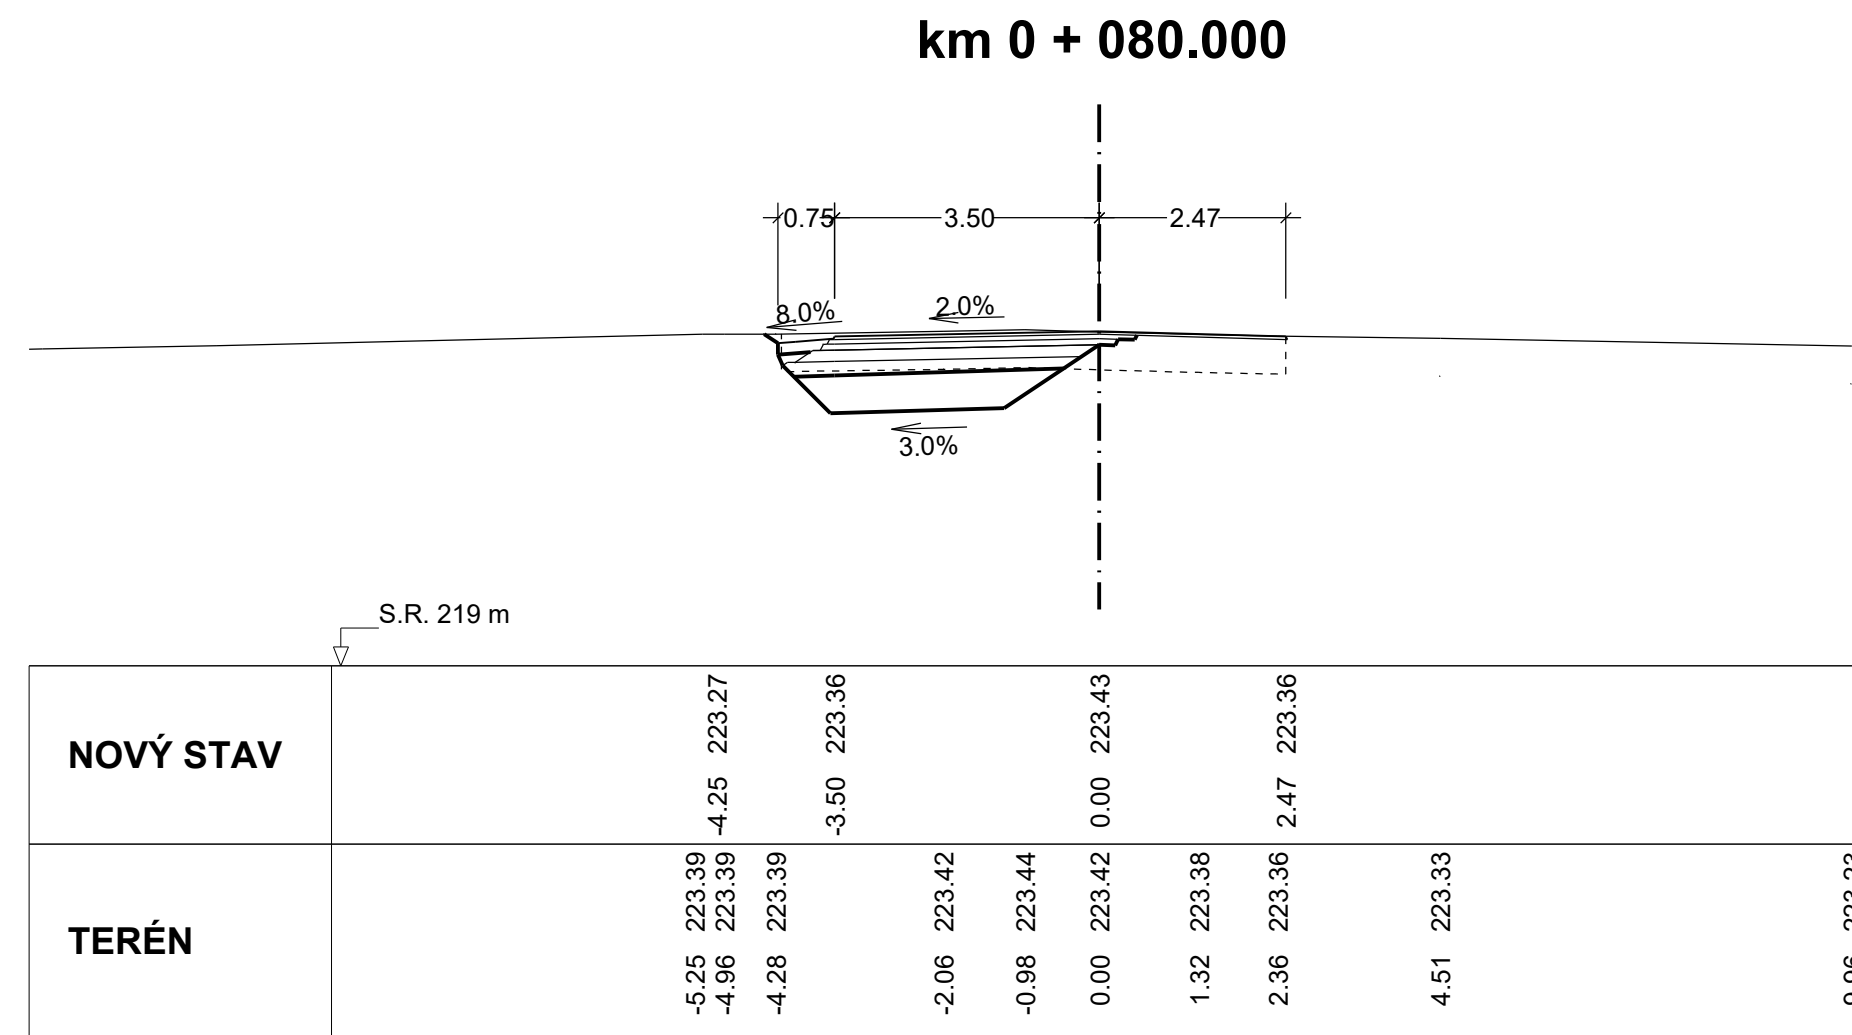

SO 171 Provizorní přeložka I/16

Ředitelství silnic a dálnic s. p.
Čerčanská 2023/12, Krč, 140 00 Praha 4

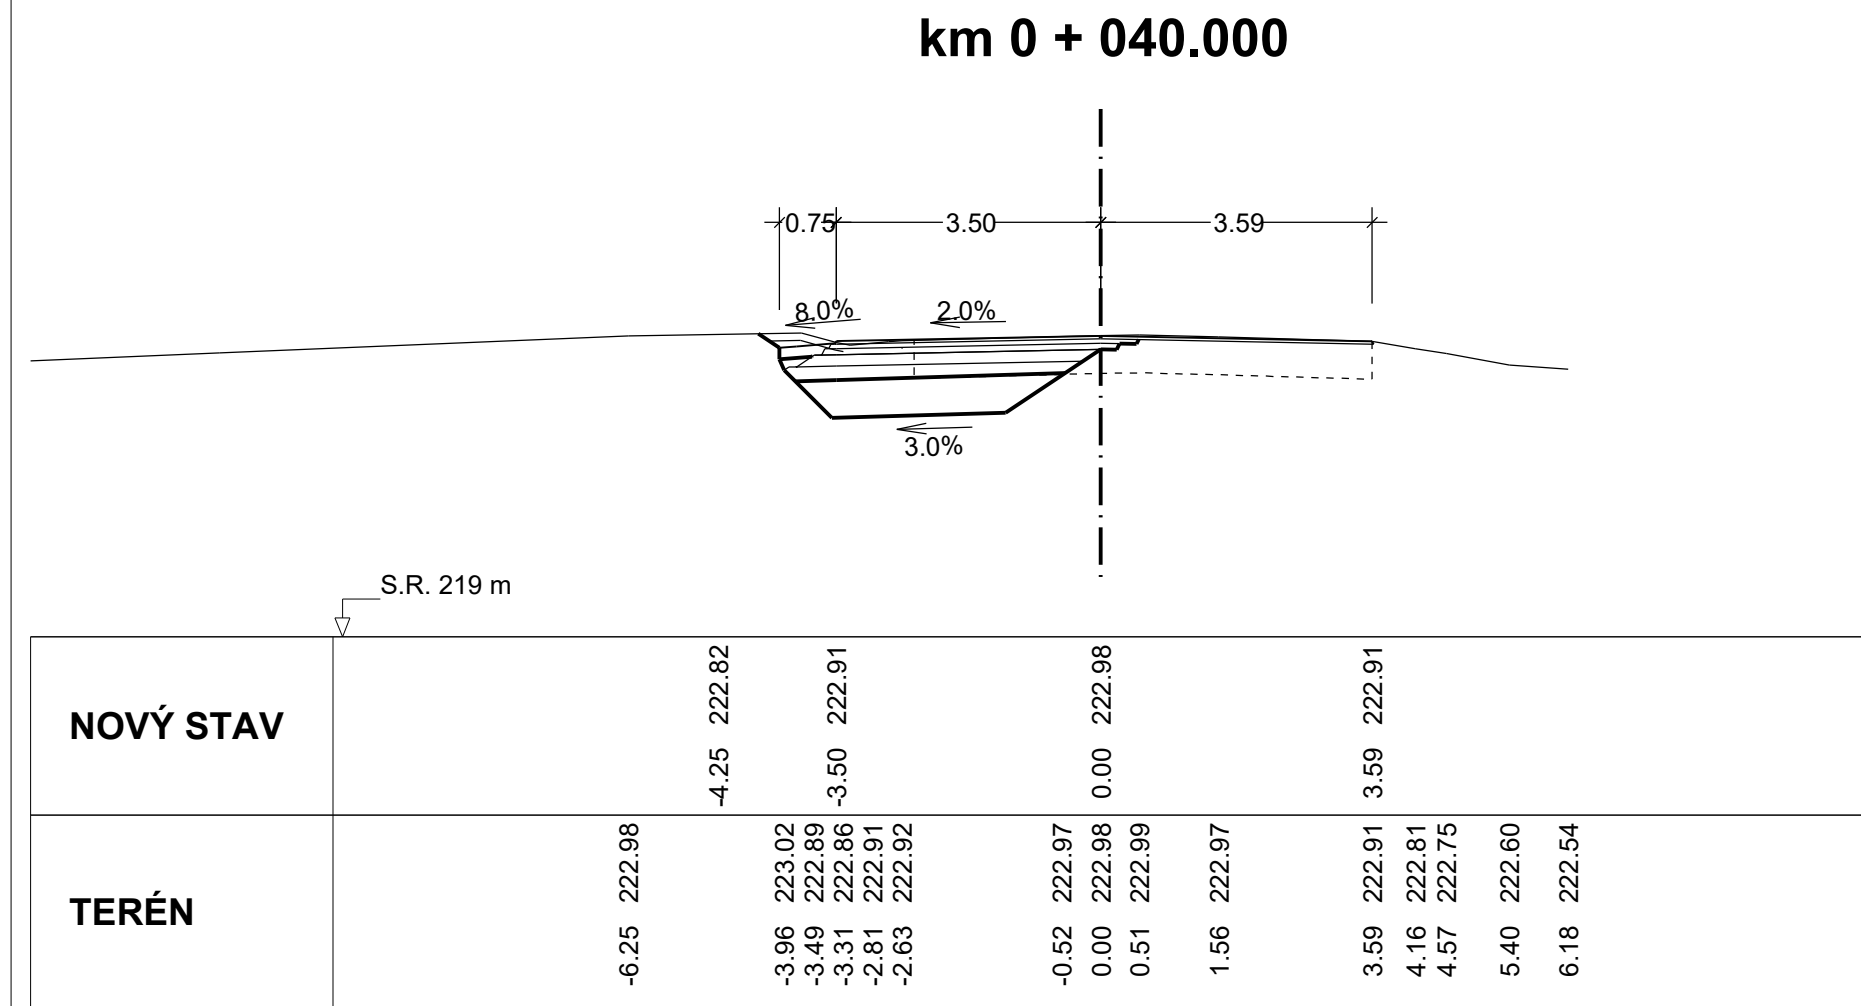

Valbek, spol. s r.o.
Vaňurova 505/17
460 07 Liberec 3

	Vypracoval	P. MATYS	Zak. číslo	21-L113-001
	Zodp. projektant	ING. T. KLIMENT	Datum	02 / 2025
	Tech. kontrola	ING. M. HANŽL	Stupeň	PDPS
	Akce		Počet formátů	6 x A4
I/16 MLADÁ BOLESLAV - MARTINOVICE			Měřítko	1 : 100
			Č. přílohy	Paré
			5	
Zhotovitel: Valbek, spol. s r.o. Vaňurova 505/17 460 07 Liberec 3	Příloha PŘÍČNÉ ŘEZY			