




LEGENDA:

- Dopravní značení Správce-ŘSD s.p.
- Dopravní značení Správce-KSÚS Středočeského kraje
- Dopravní značení Správce-Město Kosmonosy
- Dopravní značení Správce-Obec Sukorady
- Dopravní značení Správce-Obec Plazy
- Dopravní značení Správce-Obec Židněves

Souřadnicový systém: S-JTSK
Výškový systém: BpV

SO 190 Dopravní značení

Objednatel:
ŘEDITELSTVÍ SILNIC A DÁLNIC
Ředitelství silnic a dálnic s.p.
Čerčanská 2023/12, Křt, 140 00 Praha 4

Zhotovitel:
Valbek, spol. s r.o.
Vahurova 505/17
460 07 Liberec 3

Výpracovní Zpracovatel Tech. kontrola Akce	STANISLAV VRUPČKA ING. PETER HALD ANTONÍN SEIDL	Zak. číslo Datum Stupeň Počet formátů Měřítko C. přílohy	104-24 02/2025 PDPS 17 x A4 1 : 1000 Pare
	I/16 MLADÁ BOLESLAV - MARTINOVICE		
Zhotovitel: Kopie Merkurium 1250/10 100 00 Praha 6	Příloha SITUACE KM 1,500 - 3,000	2.2	