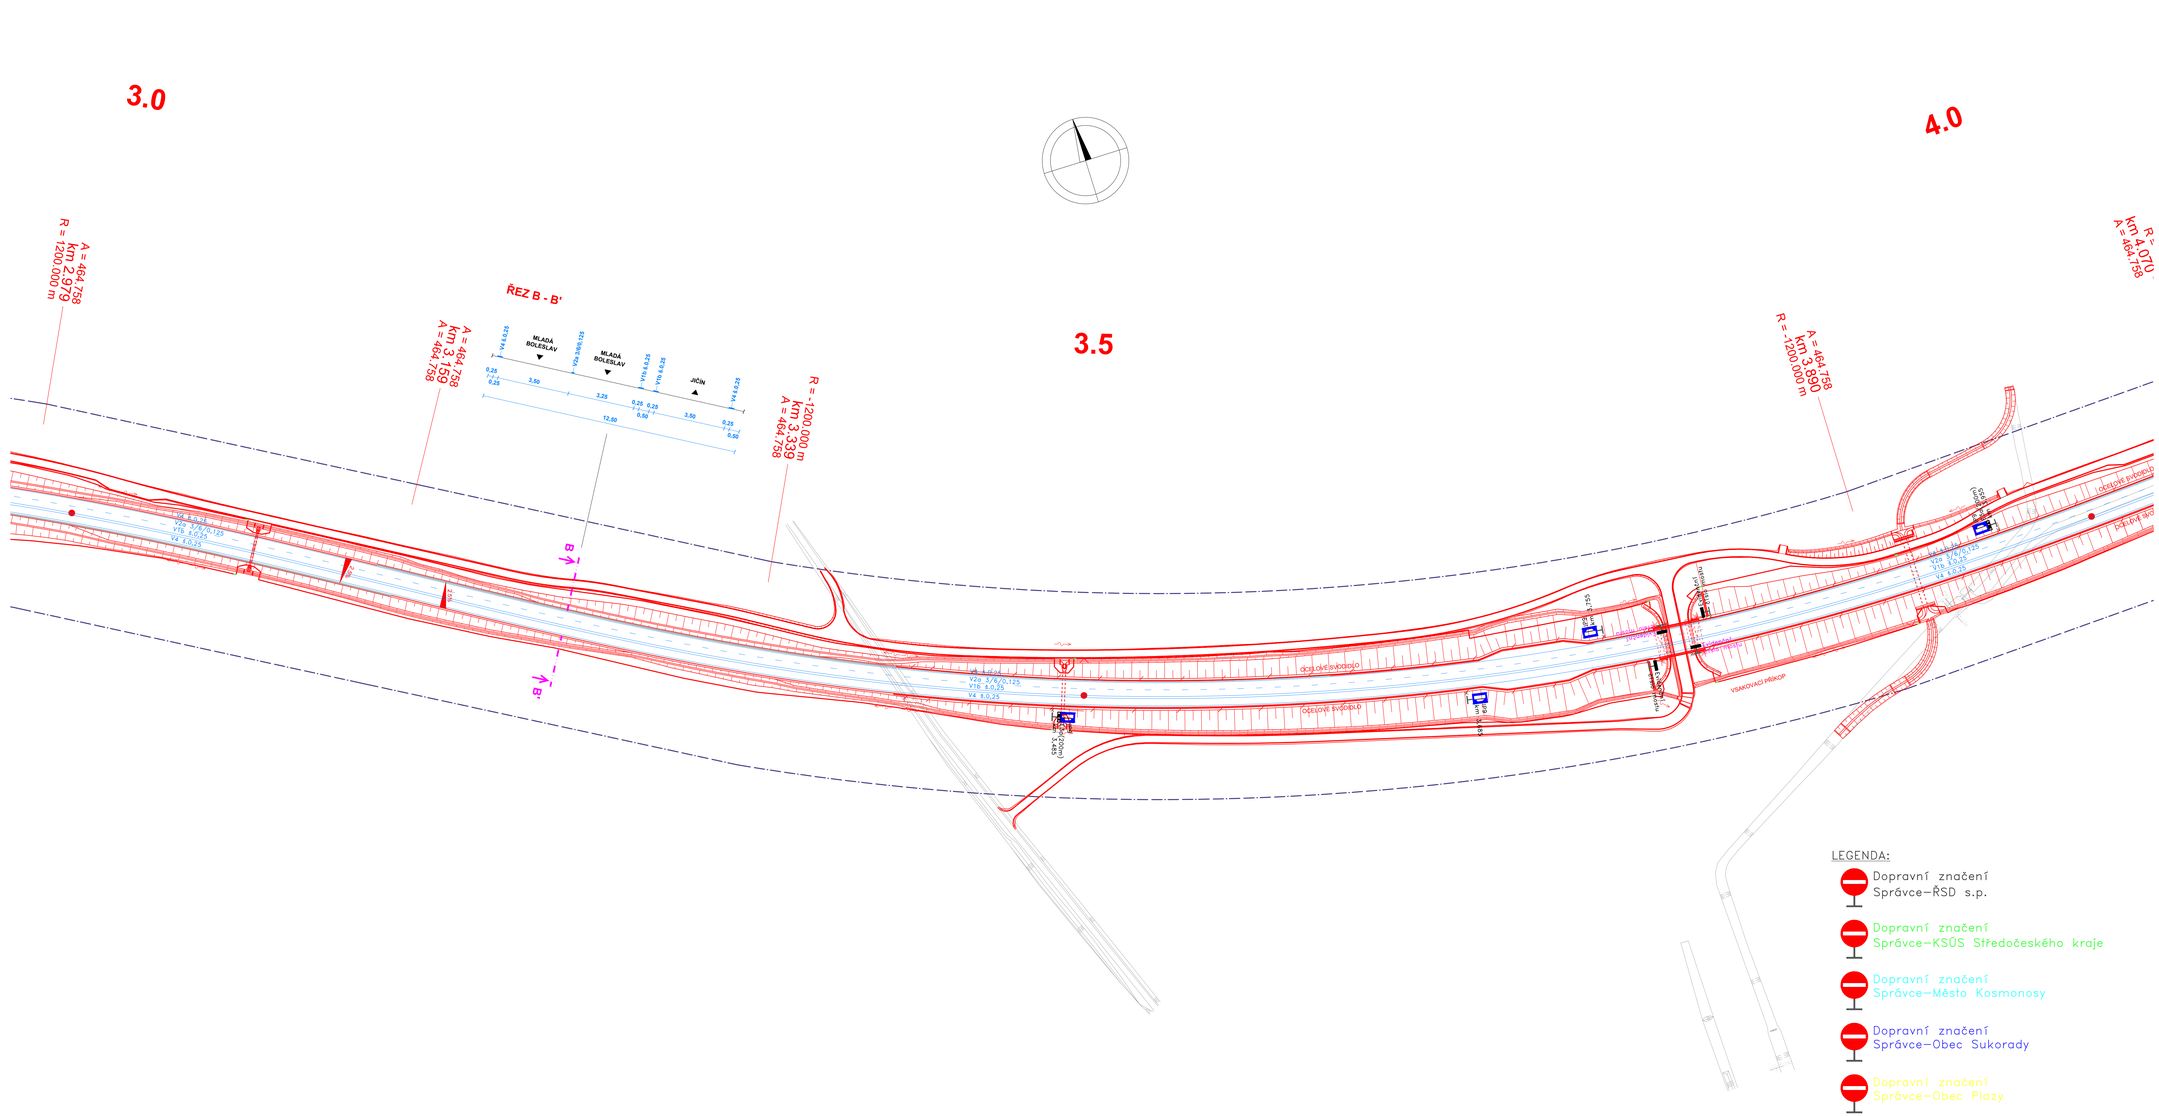

3.0
3.5
4.0
A = 464.758
km 2.979
R = 1200.000 m
A = 464.758
km 3.159
A = 464.758
R = -1200.000 m
km 3.339
A = 464.758
A = 464.758
km 3.890
R = -1200.000 m
R =
km 4.070
A = 464.758
ŘEZ B - B'
V4 š.0,25
MLADÁ BOLESLAV
V2a 3/6/0,125
MLADÁ BOLESLAV
V1b š.0,25
V1b š.0,25
JIČÍN
V4 š.0,25
0,25
0,25
3,50
3,25
0,25
0,25
0,50
3,50
0,25
0,50
12,50
B
B'
V4 š.0,25
V2a 3/6/0,125
V1b š.0,25
V4 š.0,25
2,5%
2,5%
OCELOVÉ SVODIDLO
OCELOVÉ SVODIDLO
IP9
E3a (200m)
km 3,485
IP9
km 3,685
IP9
km 3,755
Evidenční číslo mostu
Evidenční číslo mostu
Evidenční číslo mostu
Evidenční číslo mostu
VSAKOVACÍ PŘÍKOP
IP9
E3a (200m)
km 3,955
OCELOVÉ SVODIDLO
OCELOVÉ SVODIDLO

LEGENDA:

- ⛔ Dopravní značení Správce–ŘSD s.p.
- ⛔ Dopravní značení Správce–KSÚS Středočeského kraje
- ⛔ Dopravní značení Správce–Město Kosmonosy
- ⛔ Dopravní značení Správce–Obec Sukorady
- ⛔ Dopravní značení Správce–Obec Plazy
- ⛔ Dopravní značení Správce–Obec Židněves

Souřadnicový systém: S-JTSK
Výškový systém: Bpv

SO 190 Dopravní značení

Objednatel:
ŘEDITELSTVÍ SILNIC A DÁLNIC
Ředitelství silnic a dálnic s. p.
Čerčanská 2023/12, Krč, 140 00 Praha 4

Zhotovitel:
Valbek
Valbek, spol. s r.o.
Vaňurova 505/17
460 07 Liberec 3

DISK DOPRAVNÍ ZNAČENÍ

Vypracoval	STANISLAV KRUPIČKA	Krupička	Zak. číslo	024-24
Zodp. projektant	ING. PETER HAJOŠ		Datum	02/2025
Tech. kontrola	ANTONÍN SEIDL		Stupeň	PDPS
Akce	I/16 MLADÁ BOLESLAV - MARTINOVICE		Počet formátů	12 x A4
			Měřítko	1 : 1000
			Č. přílohy	Paré
Příloha	SITUACE KM 3,000 - 4,000		2.3	

Zhotovitel:
DISK s.r.o.
Menšíkovská 1239/10
160 00 Praha 6