




- LEGENDA:
- Dopravní značení Správce-ŘSD s.p.
 - Dopravní značení Správce-KSÚS Středočeského kraje
 - Dopravní značení Správce-Město Kosmonosy
 - Dopravní značení Správce-Obec Sukorady
 - Dopravní značení Správce-Obec Plazy
 - Dopravní značení Správce-Obec Židněves

Souřadnicový systém: S-JTSK Výškový systém: Bpv				
SO 190 Dopravní značení				
Objednatel:				
		Ředitelství silnic a dálnic s. p. Čerčanská 2023/12, Krč, 140 00 Praha 4		
Zhotovitel:		Valbek, spol. s r.o. Vaňurova 505/17 460 07 Liberec 3		
				
	Vypracoval	STANISLAV KRUPČKA	Zak. číslo	024-24
	Zodp. projektant	ING. PETER HAJOŠ	Datum	02/2025
	Tech. kontrola	ANTONÍN SEIDL	Stupeň	PDP5
	Akce		Podet formátů	15 x A4
I/16 MLADÁ BOLESLAV - MARTINOVICE				
Zhotovitel:	Příloha	Měřítko	1: 1000	
		C. přílohy	Page	
DISKY s.r.o. Machovičkova 1229/15 160 00 Praha 6		SITUACE KM 4,000 - 5,500		2.4