




LEGENDA:	
	Dopravní značení Správce—ŘSD s.p.
	Dopravní značení Správce—KSÚS Středočeského kraje
	Dopravní značení Správce—Město Kosmonosy
	Dopravní značení Správce—Obec Sukorady
	Dopravní značení Správce—Obec Plazy
	Dopravní značení Správce—Obec Židněves

Souřadnicový systém: S-JTSK Výškový systém: BpV			
SO 190 Dopravní značení			
Objednatel:  ŘEDITELSTVÍ SILNIC A DÁLNIC		Ředitelství silnic a dálnic s. p. Čerčanská 2023/12, Křt, 140 00 Praha 4	
Zhotovitel:  Valbek		Valbek, spol. s r.o. Vahurova 505/17 460 07 Liberec 3	
 DISKO PROJEKTOVACÍ KANCELÁŘ	Výpracovní: Zodp. projektant Tech. kontrola Akce	STANISLAV VRUPČKA ING. PETER HALDOS ANTONÍN SEIDL I/16 MLADÁ BOLESLAV - MARTINOVICE	Zak. číslo Datum Stupeň Počet formátů Měřítko C. přílohy
		 	1234-34 02/2025 PDPS 17 x A4 1 : 1000
	Zhotovitel: Zodp. inženýr Město Kosmonosy (120/10) 160 00 Praha 6	Příloha: SITUACE KM 5,500 - 7,000	2.5