




LEGENDA:

-  Dopravní značení
Správce-ŘSD s.p.
-  Dopravní značení
Správce-KSÚS Středočeského kraje
-  Dopravní značení
Správce-Město Kosmonosy
-  Dopravní značení
Správce-Obec Sukorady
-  Dopravní značení
Správce-Obec Plazy
-  Dopravní značení
Správce-Obec Židněves

Souřadnicový systém: S-JTSK
Výškový systém: Bpv

SO 190 Dopravní značení

Objednatel:
 **ŘEDITELSTVÍ
SILNIC
A DÁLNIC** Ředitelství silnic a dálnic s. p.
Čerčanská 2023/12, Křč, 140 00 Praha 4

Zhotovitel:
 **Valbek, spol. s r.o.**
Vaňurova 505/17
460 07 Liberec 3

	Vypracoval	STANISLAV KRUPČKA	Zak. číslo	024-24
	Zodp. projektant	ING. PETER HAJOŠ	Datum	02/2025
	Tech. kontrola	ANTONÍN SEDL	Stupeň	PDP-9
	Akce		Podací formát	14 x A4
I/16 MLADÁ BOLESLAV - MARTINOVICE				
Měřítko			1:1000	
Č. přílohy			Paré	
Zhotovitel: DISK s.r.o. Měřičova 1230/10 190 00 Praha 9	Příloha	SITUACE KM 7,000 - KÚ		
		2.6		