

Souřadnicový systém: S-JTSK
Výškový systém: Bpv

SO 190 Dopravní značení

Objednatel:



**ŘEDITELSTVÍ
SILNIC
A DÁLNIC**

Ředitelství silnic a dálnic s. p.
Čerčanská 2023/12, Krč, 140 00 Praha 4

Zhotovitel:




Valbek, spol. s r.o.

Vaňurova 505/17
460 07 Liberec 3

	Vypracoval	STANISLAV KRUPÍČKA		Zak. číslo	024-24
	Zodp. projektant	ING. PETER HAJOŠ		Datum	02/2025
	Tech. kontrola	ANTONÍN SEIDL		Stupeň	PDPS
	Akce I/16 MLADÁ BOLESLAV - MARTINOVICE			Počet formátů	24 x A4
				Měřítko	1 : 50, 1 : 100
Zhotovitel: DISK s.r.o. Menšíkovská 1239/10 160 00 Praha 6	Příloha VELKOPLOŠNÉ DOPRAVNÍ ZNAČKY			Č. přílohy	Paré
				3	




Kreslil: K. Kalová	Kontroloval: A. Seidl	Schváleno - datum: A. Seidl - 27/11/24	Název souboru: Disk_2024/Projekty/024-24-se_I-16_Mladá_Boleslav-Martinovice-PDPS/ Projektová dokumentace/SO 190 Dopravní značení/VLKP/024-24-001	Stupeň: PDPS	Datum: 27/11/24
			I/16 Mladá Boleslav - Martinovice SO 190 Dopravní značení - Velkoplošné dopravní značky		
			024-24-001	Měřítko: 1:50	Výtisk: List: 1/23

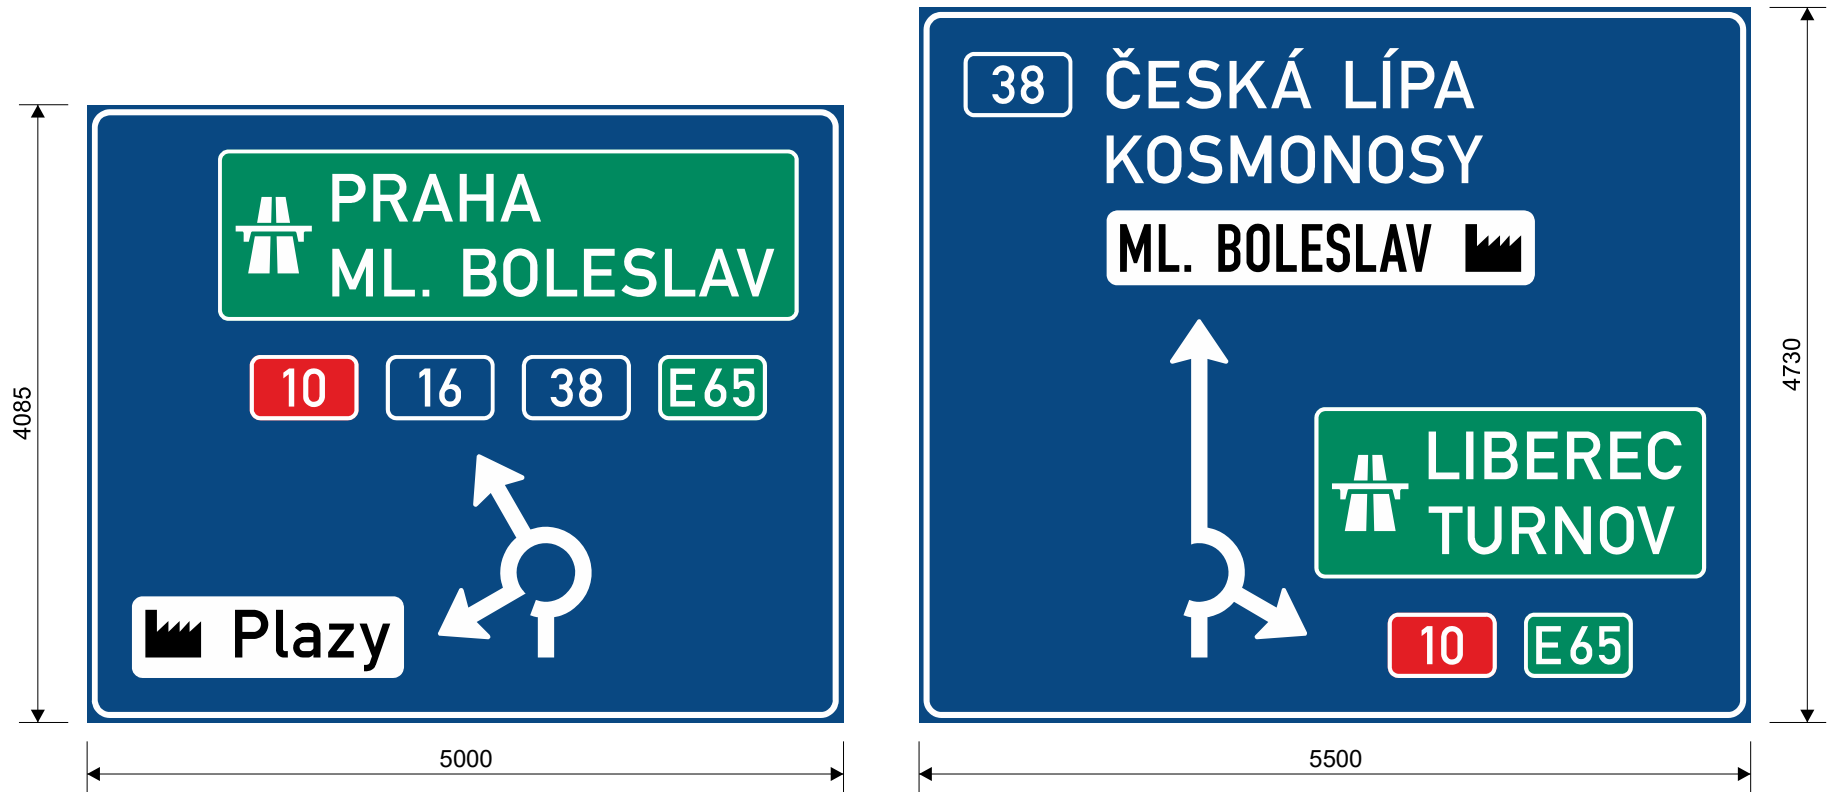


Kreslil: K. Kalová	Kontroloval: A. Seidl	Schváleno - datum: A. Seidl - 27/11/24	Název souboru: Disk_2024/Projekty/024-24-se_l-16_Mladá_Boleslav-Martinovice-PDPS/ Projektová dokumentace/SO 190 Dopravní značení/VLKP/024-24-001	Stupeň: PDPS	Datum: 27/11/24
 DOPRAVNÍ ZNAČENÍ			I/16 Mladá Boleslav - Martinovice SO 190 Dopravní značení - Velkoplošné dopravní značky		
			024-24-001	Měřítko: 1:50	Výtisk: List: 2/23

č. 016-03
IS 9b
Výška písma - 210 mm

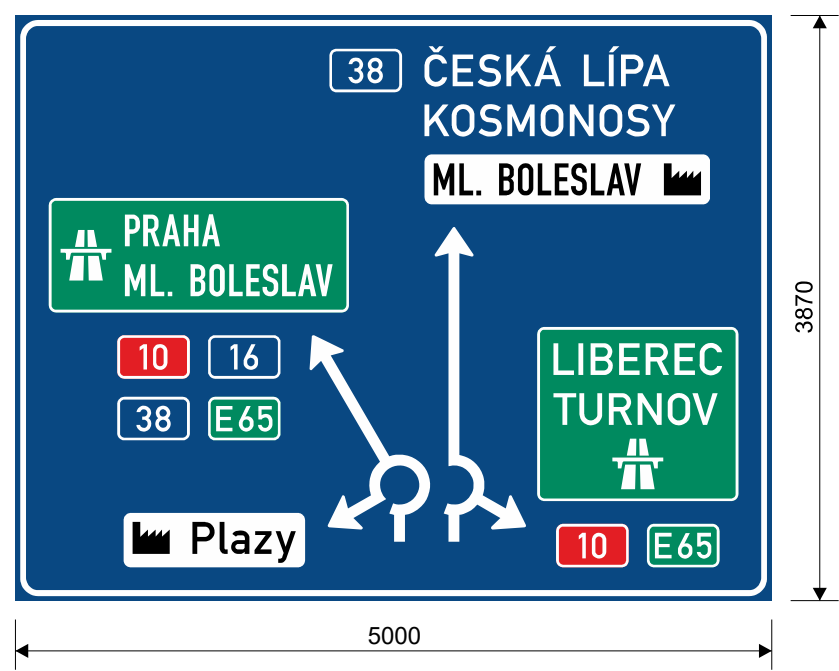


č. 016-04
IS 6b (300 m)
Výška písma - 210 mm

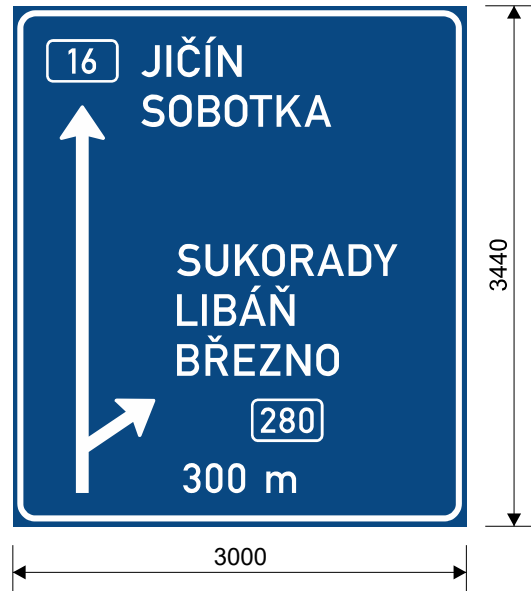


Kreslil: K. Kalová	Kontroloval: A. Seidl	Schváleno - datum: A. Seidl - 27/11/24	Název souboru: Disk_2024/Projekty/024-24-se_I-16_Mladá_Boleslav-Martinovice-PDPS/ Projektová dokumentace/SO 190 Dopravní značení/VLK/P/024-24-001	Stupeň: PDPS	Datum: 27/11/24
 DOPRAVNÍ ZNAČENÍ			I/16 Mladá Boleslav - Martinovice SO 190 Dopravní značení - Velkoplošné dopravní značky		
024-24-001			Měřítko: 1:50	Výtisk:	List: 3/23


č. 016-05
IS 6g
Výška písma - 210 mm

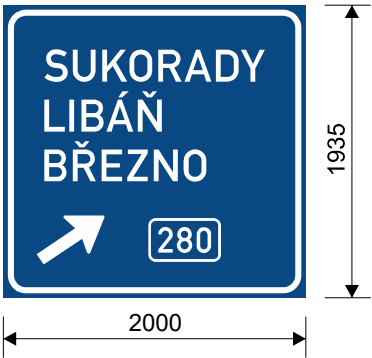

č. 016-06
IS 6b (300 m)
Výška písma - 210 mm

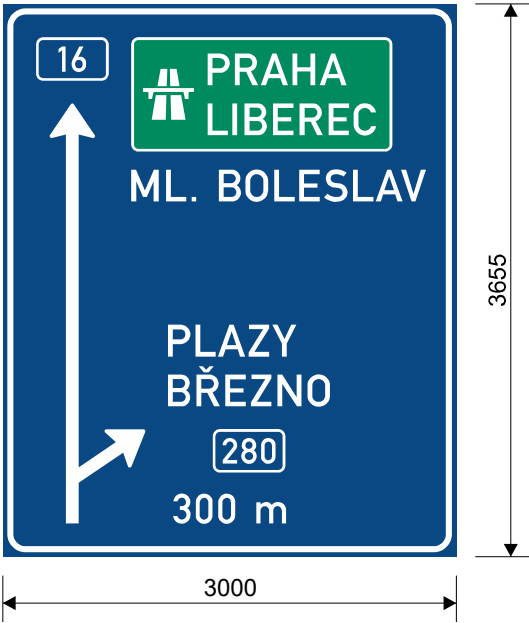


č. 016-07
IS 6g
Výška písma - 210 mm

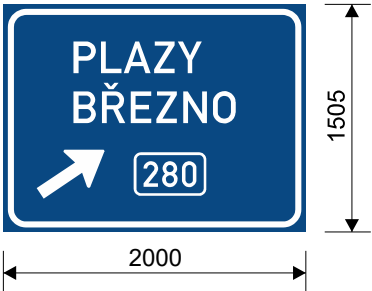


Kreslil: K. Kalová	Kontroloval: A. Seidl	Schváleno - datum: A. Seidl - 27/11/24	Název souboru: Disk_2024/Projekty/024-24-se_I-16_Mladá_Boleslav-Martinovice-PDPS/ Projektová dokumentace/SO 190 Dopravní značení/VLKP/024-24-001	Stupeň: PDPS	Datum: 27/11/24
 DOPRAVNÍ ZNAČENÍ			I/16 Mladá Boleslav - Martinovice SO 190 Dopravní značení - Velkoplošné dopravní značky		
			024-24-001	Měřítko: 1:50	Výtisk: List: 4/23

č. 016-08
IS 9b
Výška písma - 210 mm

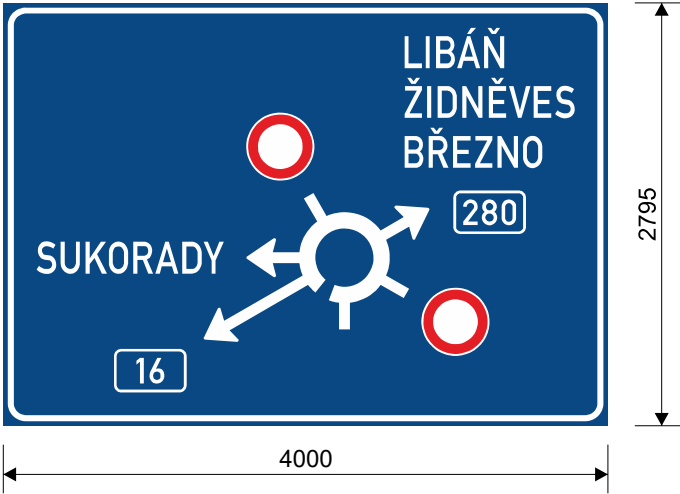


U cílů „LIBÁŇ“, „ŽIDNĚVES“, „BŘEZNO“ a „SUKORADY“ použita komprese 85 %.

č. 016-09
IS 9b
Výška písma - 210 mm

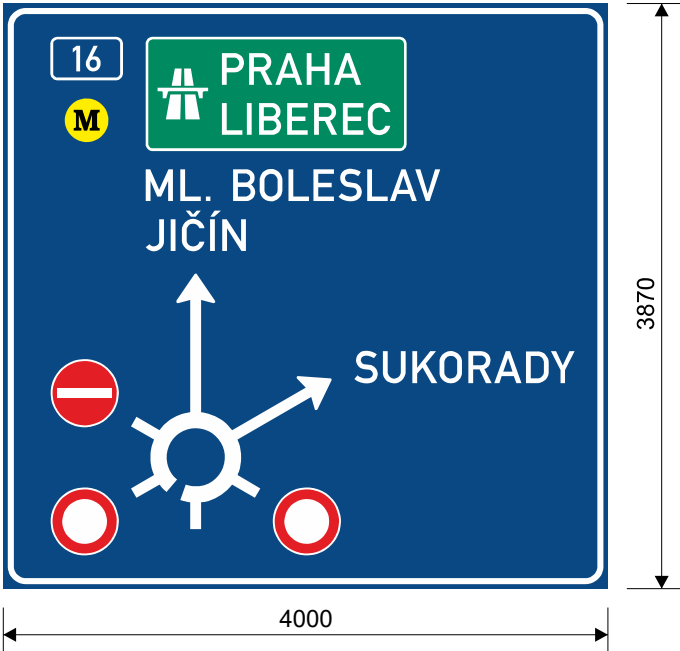


Kreslil: K. Kalová	Kontroloval: A. Seidl	Schváleno - datum: A. Seidl - 27/11/24	Název souboru: Disk_2024/Projekty/024-24-se_I-16_Mladá_Boleslav-Martinovice-PDPS/ Projektová dokumentace/SO 190 Dopravní značení/VLKP/024-24-001	Stupeň: PDPS	Datum: 27/11/24
DISK DOPRAVNÍ ZNAČENÍ			I/16 Mladá Boleslav - Martinovice SO 190 Dopravní značení - Velkoplošné dopravní značky		
024-24-001			Měřítko: 1:50	Výtisk:	List: 5/23

č. 016-10
IS 9b
Výška písma - 210 mm

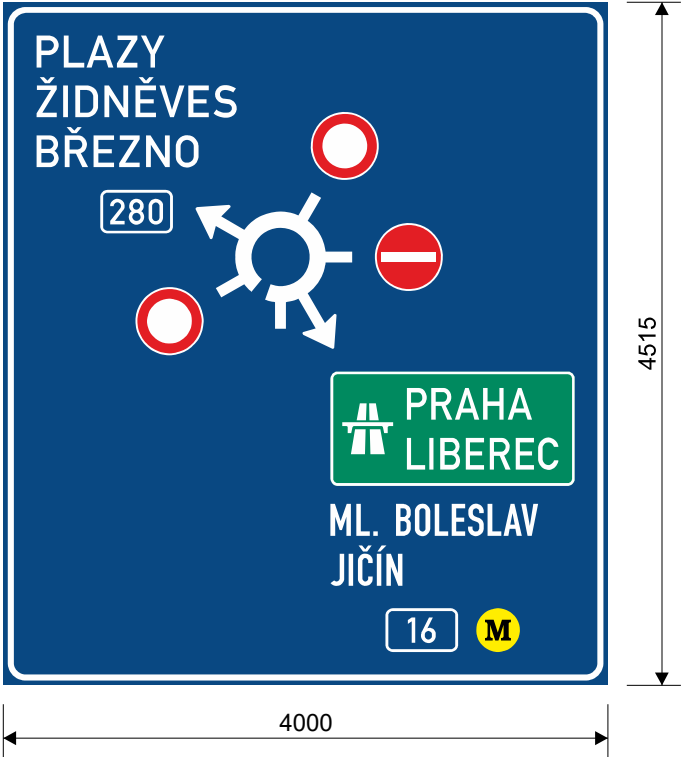

U cílů „PRAHA” a „LIBEREC” použita komprese 90 %.


č. 016-11
IS 9b
Výška písma - 210 mm

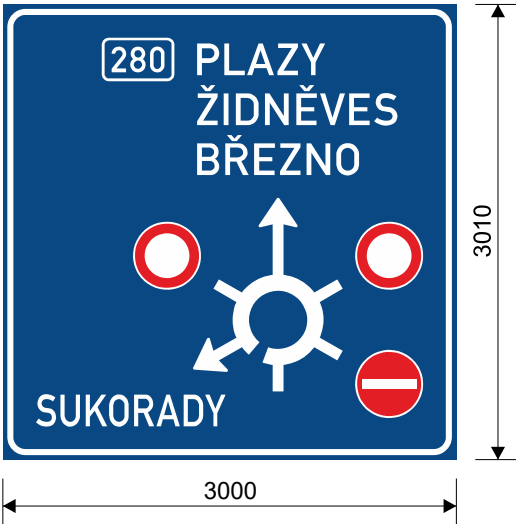


U cíle „SUKORADY” použita komprese 86 %.

Kreslil: K. Kalová	Kontroloval: A. Seidl	Schváleno - datum: A. Seidl - 27/11/24	Název souboru: Disk_2024/Projekty/024-24-se_I-16_Mladá_Boleslav-Martinovice-PDPS/ Projektová dokumentace/SO 190 Dopravní značení/VLKP/024-24-001	Stupeň: PDPS	Datum: 27/11/24
DISK DOPRAVNÍ ZNAČENÍ			I/16 Mladá Boleslav - Martinovice SO 190 Dopravní značení - Velkoplošné dopravní značky		
024-24-001			Měřítko: 1:50	Výtisk:	List: 6/23

č. 016-12
IS 6b (250 m)
Výška písma - 210 mm

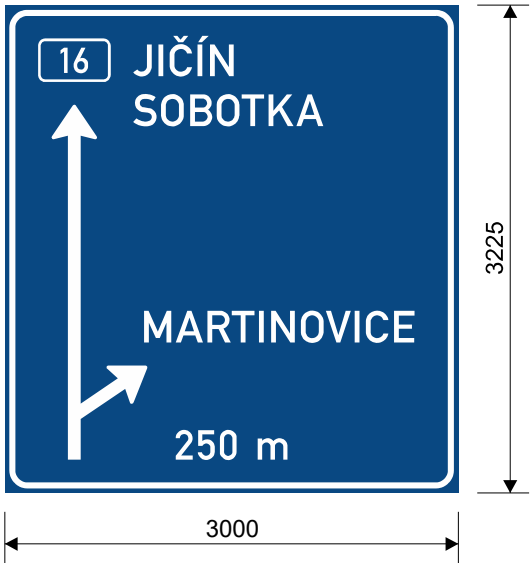


č. 016-13
IS 6g
Výška písma - 210 mm

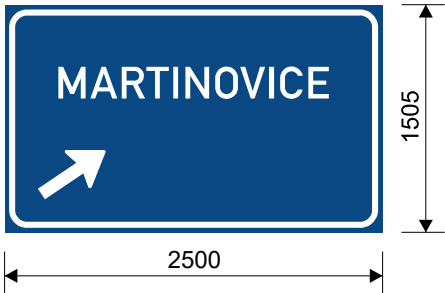

Kreslil: K. Kalová	Kontroloval: A. Seidl	Schváleno - datum: A. Seidl - 27/11/24	Název souboru: Disk_2024/Projekty/024-24-se_I-16_Mladá_Boleslav-Martinovice-PDPS/ Projektová dokumentace/SO 190 Dopravní značení/VLKP/024-24-001	Stupeň: PDPS	Datum: 27/11/24
 DOPRAVNÍ ZNAČENÍ			I/16 Mladá Boleslav - Martinovice SO 190 Dopravní značení - Velkoplošné dopravní značky		
			024-24-001	Měřítko: 1:50	Výtisk: List: 7/23

č. 016-14
IS 6b (300 m)
Výška písma - 210 mm

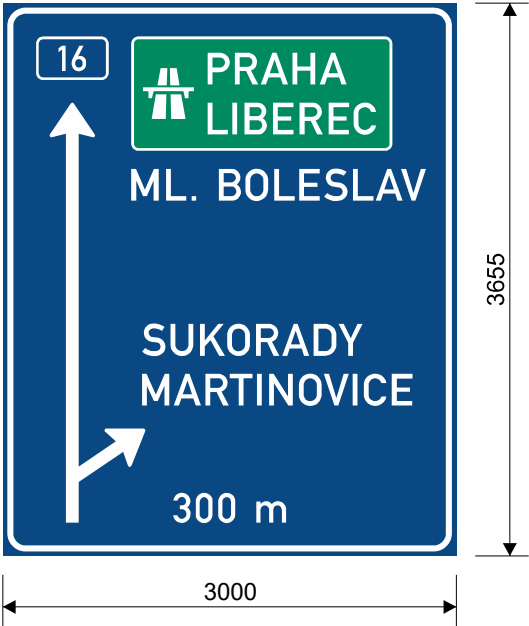


č. 016-15
IS 6g - poloportál
Výška písma - 315 mm




Kreslil: K. Kalová	Kontroloval: A. Seidl	Schváleno - datum: A. Seidl - 27/11/24	Název souboru: Disk_2024/Projekty/024-24-se_I-16_Mladá_Boleslav-Martinovice-PDPS/ Projektová dokumentace/SO 190 Dopravní značení/VLKP/024-24-001	Stupeň: PDPS	Datum: 27/11/24
 DOPRAVNÍ ZNAČENÍ			I/16 Mladá Boleslav - Martinovice SO 190 Dopravní značení - Velkoplošné dopravní značky		
			024-24-001	Měřítko: 1:50	Výtisk: List: 8/23

č. 016-16
IS 9b
Výška písma - 210 mm

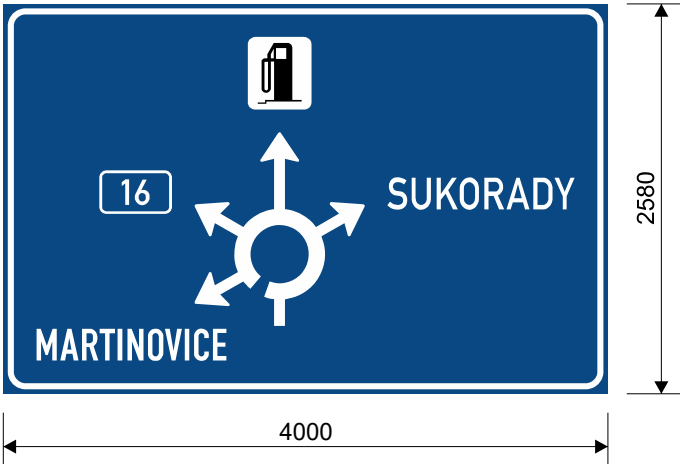

U cíle „SUKORADY” použita komprese 85 %.


č. 016-17
IS 9b
Výška písma - 210 mm

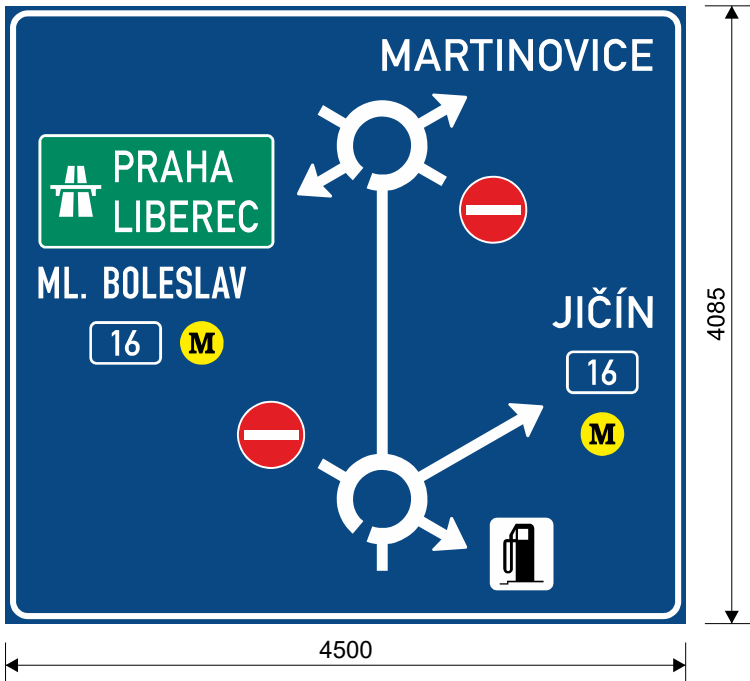


U cílů „PRAHA” a „LIBEREC” použita komprese 85 %.

Kreslil: K. Kalová	Kontroloval: A. Seidl	Schváleno - datum: A. Seidl - 27/11/24	Název souboru: Disk_2024/Projekty/024-24-se_I-16_Mladá_Boleslav-Martinovice-PDPS/ Projektová dokumentace/SO 190 Dopravní značení/VLKP/024-24-001	Stupeň: PDPS	Datum: 27/11/24
			I/16 Mladá Boleslav - Martinovice SO 190 Dopravní značení - Velkoplošné dopravní značky		
024-24-001			Měřítko: 1:50	Výtisk:	List: 9/23


č. 016-18
IS 9b
Výška písma - 210 mm

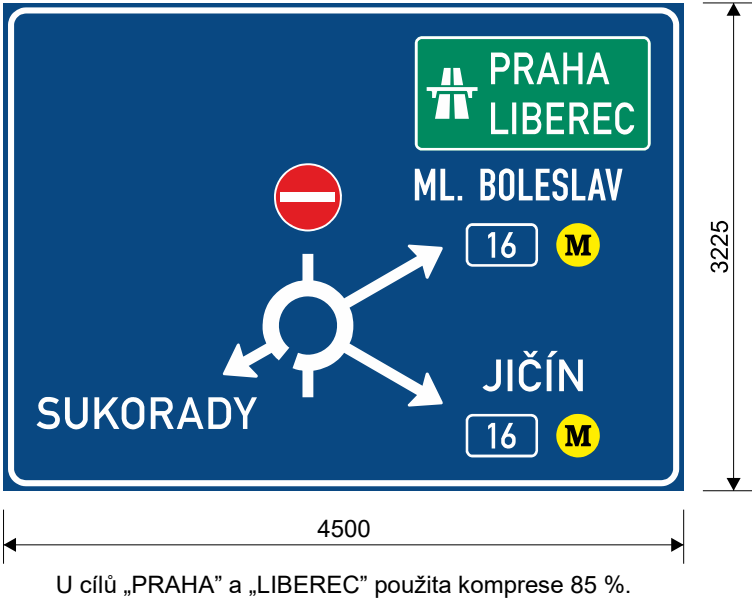

č. 016-19
IS 9b
Výška písma - 210 mm

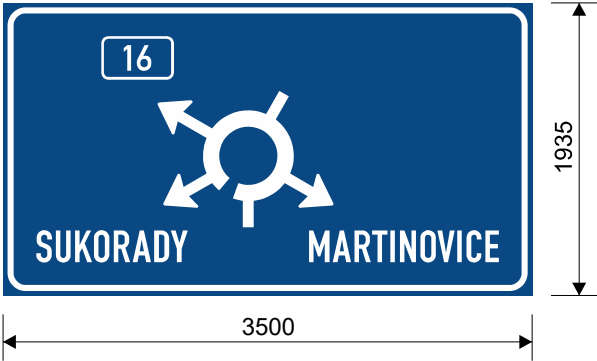


č. 016-20
IS 9b
Výška písma - 210 mm

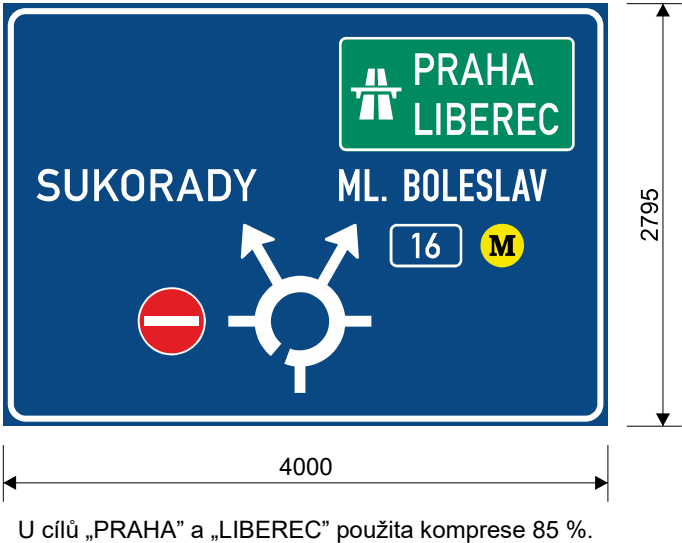


Kreslil: K. Kalová	Kontroloval: A. Seidl	Schváleno - datum: A. Seidl - 27/11/24	Název souboru: Disk_2024/Projekty/024-24-se_I-16_Mladá_Boleslav-Martinovice-PDPS/Projektová dokumentace/SO 190 Dopravní značení/VLKP/024-24-001	Stupeň: PDPS	Datum: 27/11/24
 DOPRAVNÍ ZNAČENÍ			I/16 Mladá Boleslav - Martinovice SO 190 Dopravní značení - Velkoplošné dopravní značky		
			024-24-001	Měřítko: 1:50	Výtisk: List: 10/23

č. 016-21
IS 9b
Výška písma - 210 mm

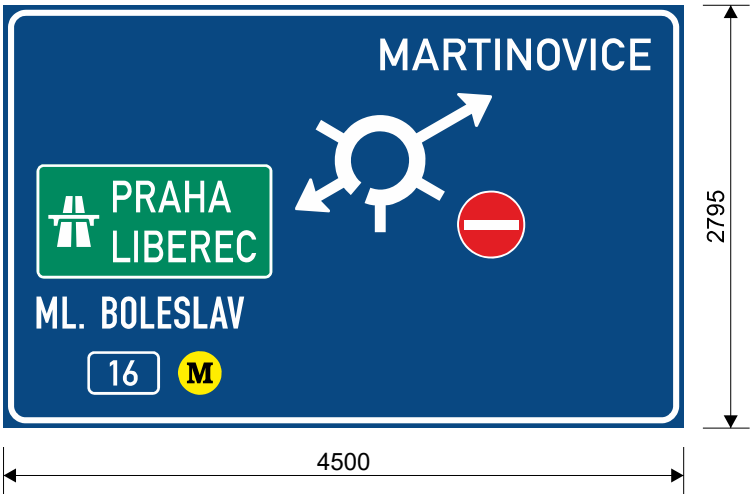


U cílů „PRAHA“ a „LIBEREC“ použita komprese 85 %.

č. 016-22
IS 9b
Výška písma - 210 mm

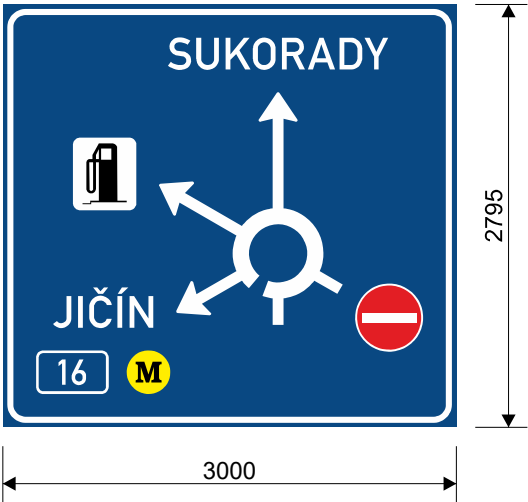


Kreslil: K. Kalová	Kontroloval: A. Seidl	Schváleno - datum: A. Seidl - 27/11/24	Název souboru: Disk_2024/Projekty/024-24-se_I-16_Mladá_Boleslav-Martinovice-PDPS/ Projektová dokumentace/SO 190 Dopravní značení/VLKP/024-24-001	Stupeň: PDPS	Datum: 27/11/24
 DOPRAVNÍ ZNAČENÍ			I/16 Mladá Boleslav - Martinovice SO 190 Dopravní značení - Velkoplošné dopravní značky		
			024-24-001	Měřítko: 1:50	Výtisk: List: 11/23

č. D10-04602
IS 6e + IS 6f (500 m) - portál
Výška písma - 420 mm

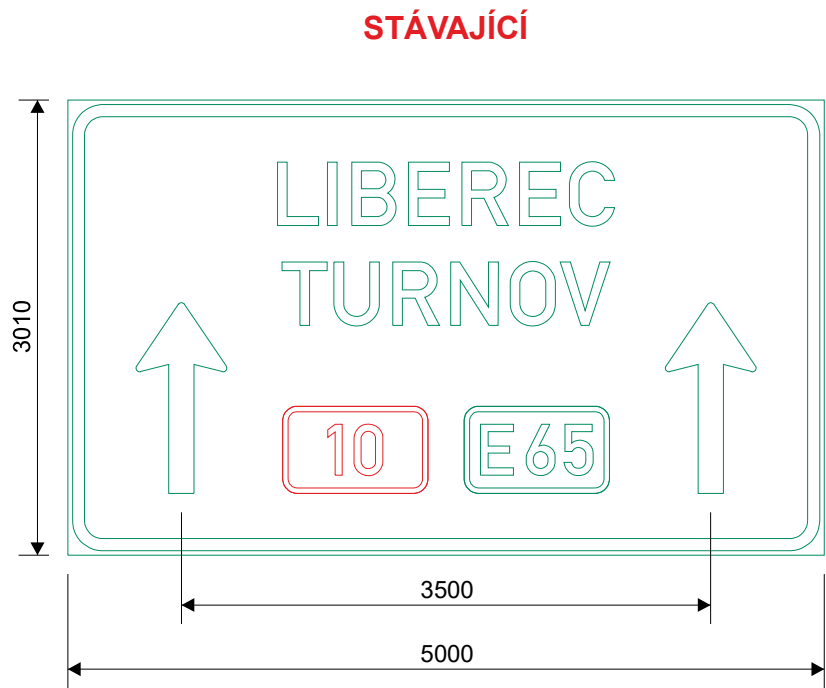


Kreslil: K. Kalová	Kontroloval: A. Seidl	Schváleno - datum: A. Seidl - 27/11/24	Název souboru: Disk_2024/Projekty/024-24-se_l-16_Mladá_Boleslav-Martinovice-PDPS/ Projektová dokumentace/SO 190 Dopravní značení/VLKP/024-24-001	Stupeň: PDPS	Datum: 27/11/24
			I/16 Mladá Boleslav - Martinovice SO 190 Dopravní značení - Velkoplošné dopravní značky		
			024-24-001	Měřítko: 1:50	Výtisk: List: 12/23

č. D10-04603
IS 6e + IS 6f - portál
Výška písma - 420 mm

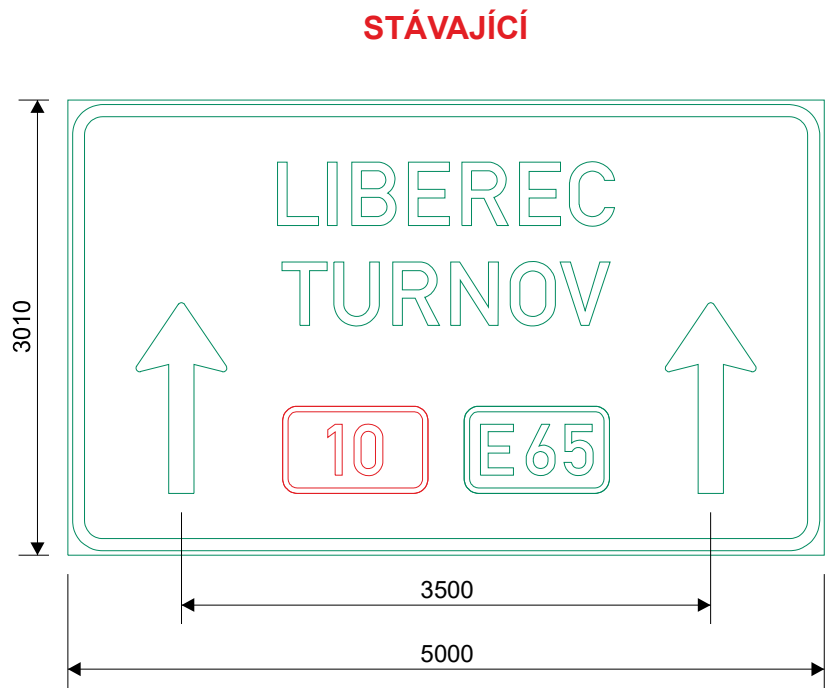


Kreslil: K. Kalová	Kontroloval: A. Seidl	Schváleno - datum: A. Seidl - 27/11/24	Název souboru: Disk_2024/Projekty/024-24-se_l-16_Mladá_Boleslav-Martinovice-PDPS/ Projektová dokumentace/SO 190 Dopravní značení/VLKP/024-24-001	Stupeň: PDPS	Datum: 27/11/24
			I/16 Mladá Boleslav - Martinovice SO 190 Dopravní značení - Velkoplošné dopravní značky		
			024-24-001	Měřítko: 1:50	Výtisk: List: 13/23

č. D10-04604
IS 6e + IS 6f + IS 6f - portál
Výška písma - 420 mm


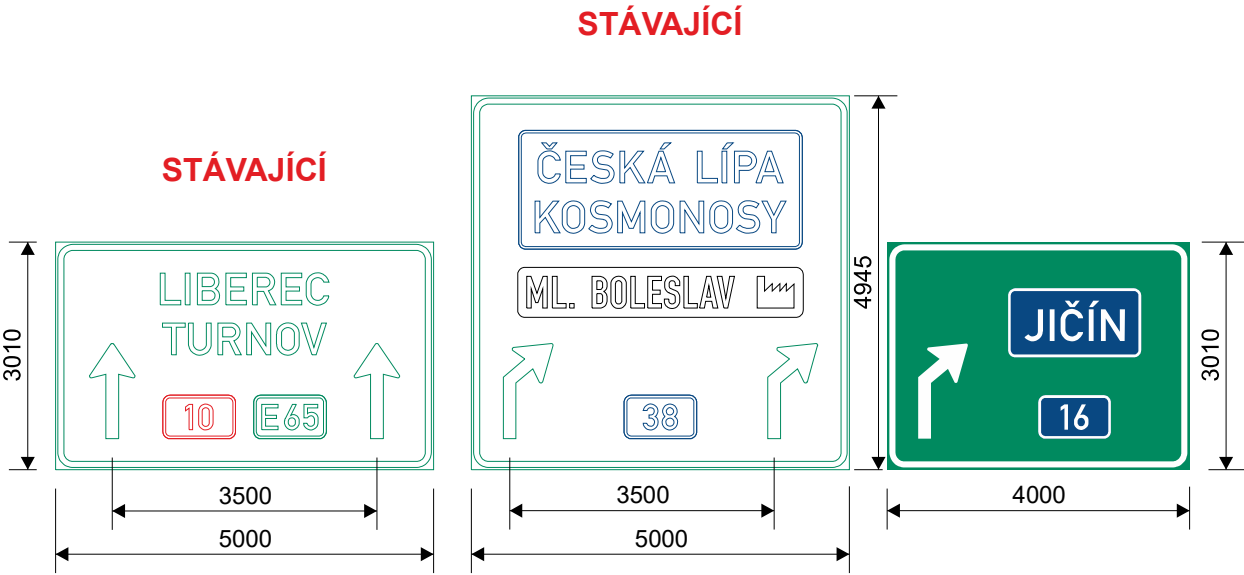


č. D10-04605
IS 6e + IS 6f + IS 6f - portál
Výška písma - 420 mm

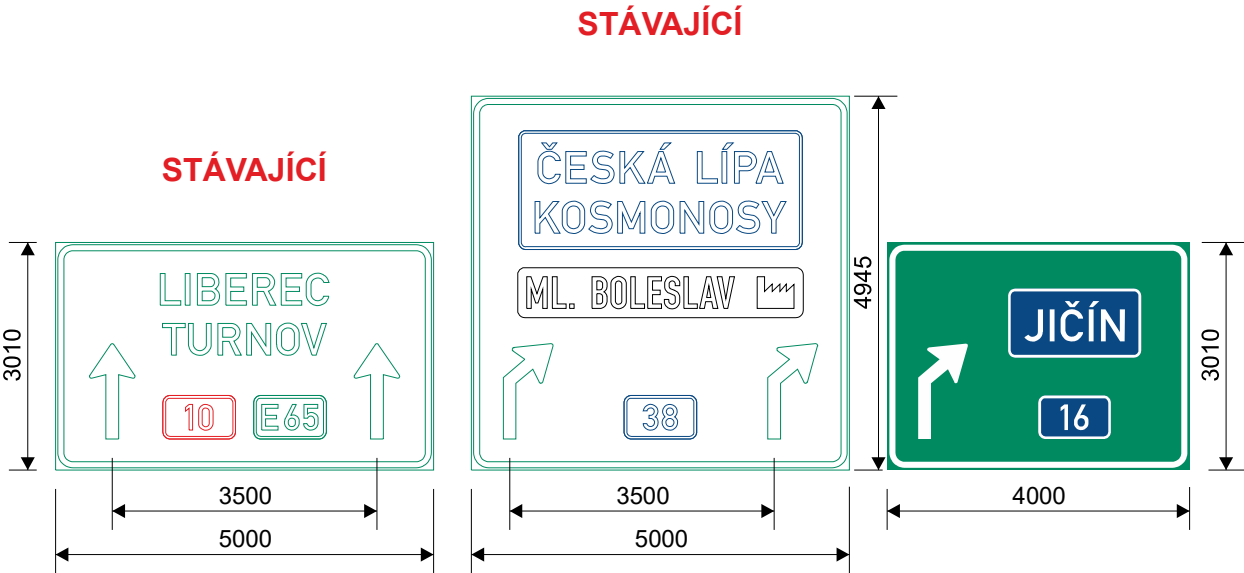

Kreslil: K. Kalová	Kontroloval: A. Seidl	Schváleno - datum: A. Seidl - 27/11/24	Název souboru: Disk_2024/Projekty/024-24-se_I-16_Mladá_Boleslav-Martinovice-PDPS/ Projektová dokumentace/SO 190 Dopravní značení/VLKP/024-24-001	Stupeň: PDPS	Datum: 27/11/24
 DOPRAVNÍ ZNAČENÍ			I/16 Mladá Boleslav - Martinovice SO 190 Dopravní značení - Velkoplošné dopravní značky		
			024-24-001	Měřítko: 1:100	Výtisk: List: 14/23

STÁVAJÍCÍ

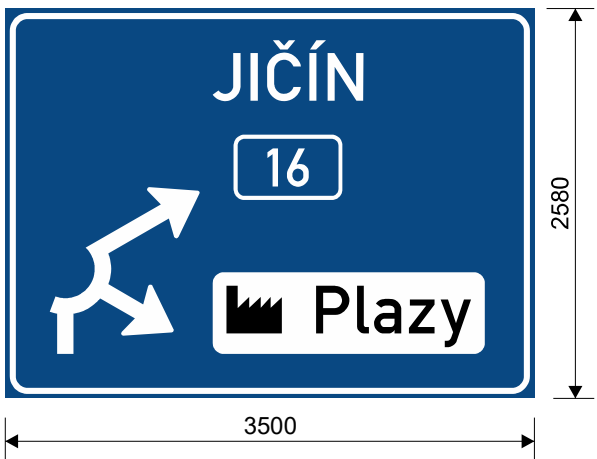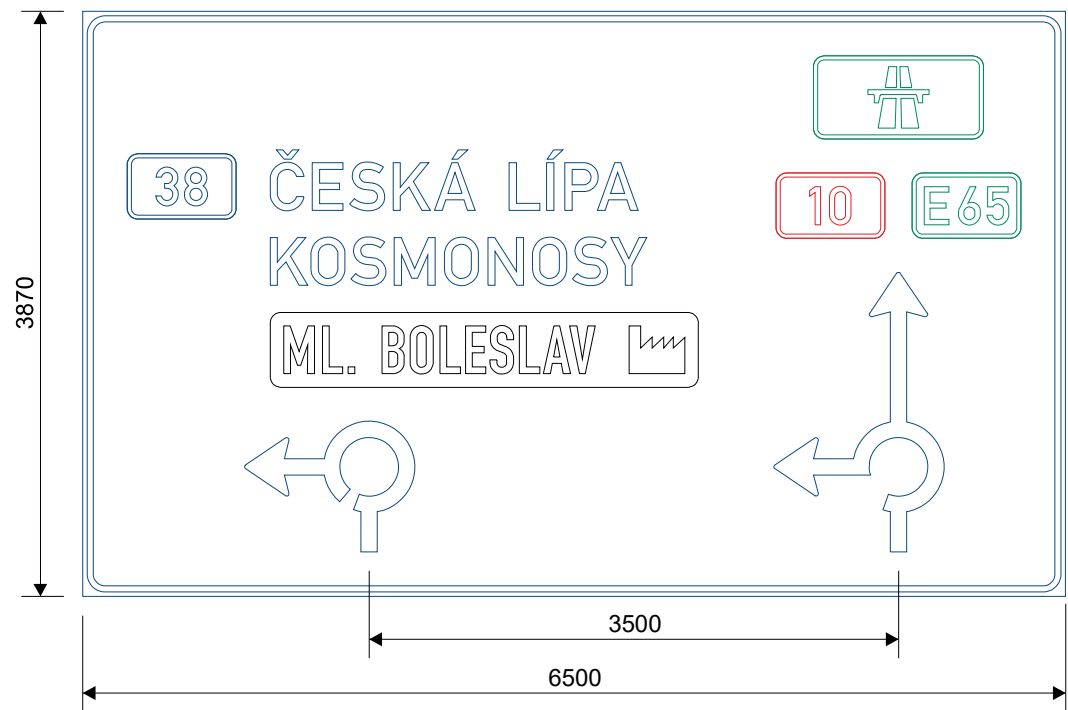


Kreslil: K. Kalová	Kontroloval: A. Seidl	Schváleno - datum: A. Seidl - 27/11/24	Název souboru: Disk_2024/Projekty/024-24-se_i-16_Mladá_Boleslav-Martinovice-PDPS/ Projektová dokumentace/SO 190 Dopravní značení/VLKP/024-24-001	Stupeň: PDPS	Datum: 27/11/24
			I/16 Mladá Boleslav - Martinovice SO 190 Dopravní značení - Velkoplošné dopravní značky		
			024-24-001	Měřítko: 1:50	Výtisk: List: 15/23

č. D10-04609
IS 6b (500 m) - portál
Výška písma - 420 mm



U cíle „ML. BOLESLAV” použita komprese 90%.

Kreslil: K. Kalová	Kontroloval: A. Seidl	Schváleno - datum: A. Seidl - 27/11/24	Název souboru: Disk_2024/Projekty/024-24-se_l-16_Mladá_Boleslav-Martinovice-PDPS/ Projektová dokumentace/SO 190 Dopravní značení/VLKP/024-24-001	Stupeň: PDPS	Datum: 27/11/24
			I/16 Mladá Boleslav - Martinovice SO 190 Dopravní značení - Velkoplošné dopravní značky		
			024-24-001	Měřítko: 1:50	Výtisk: List: 16/23

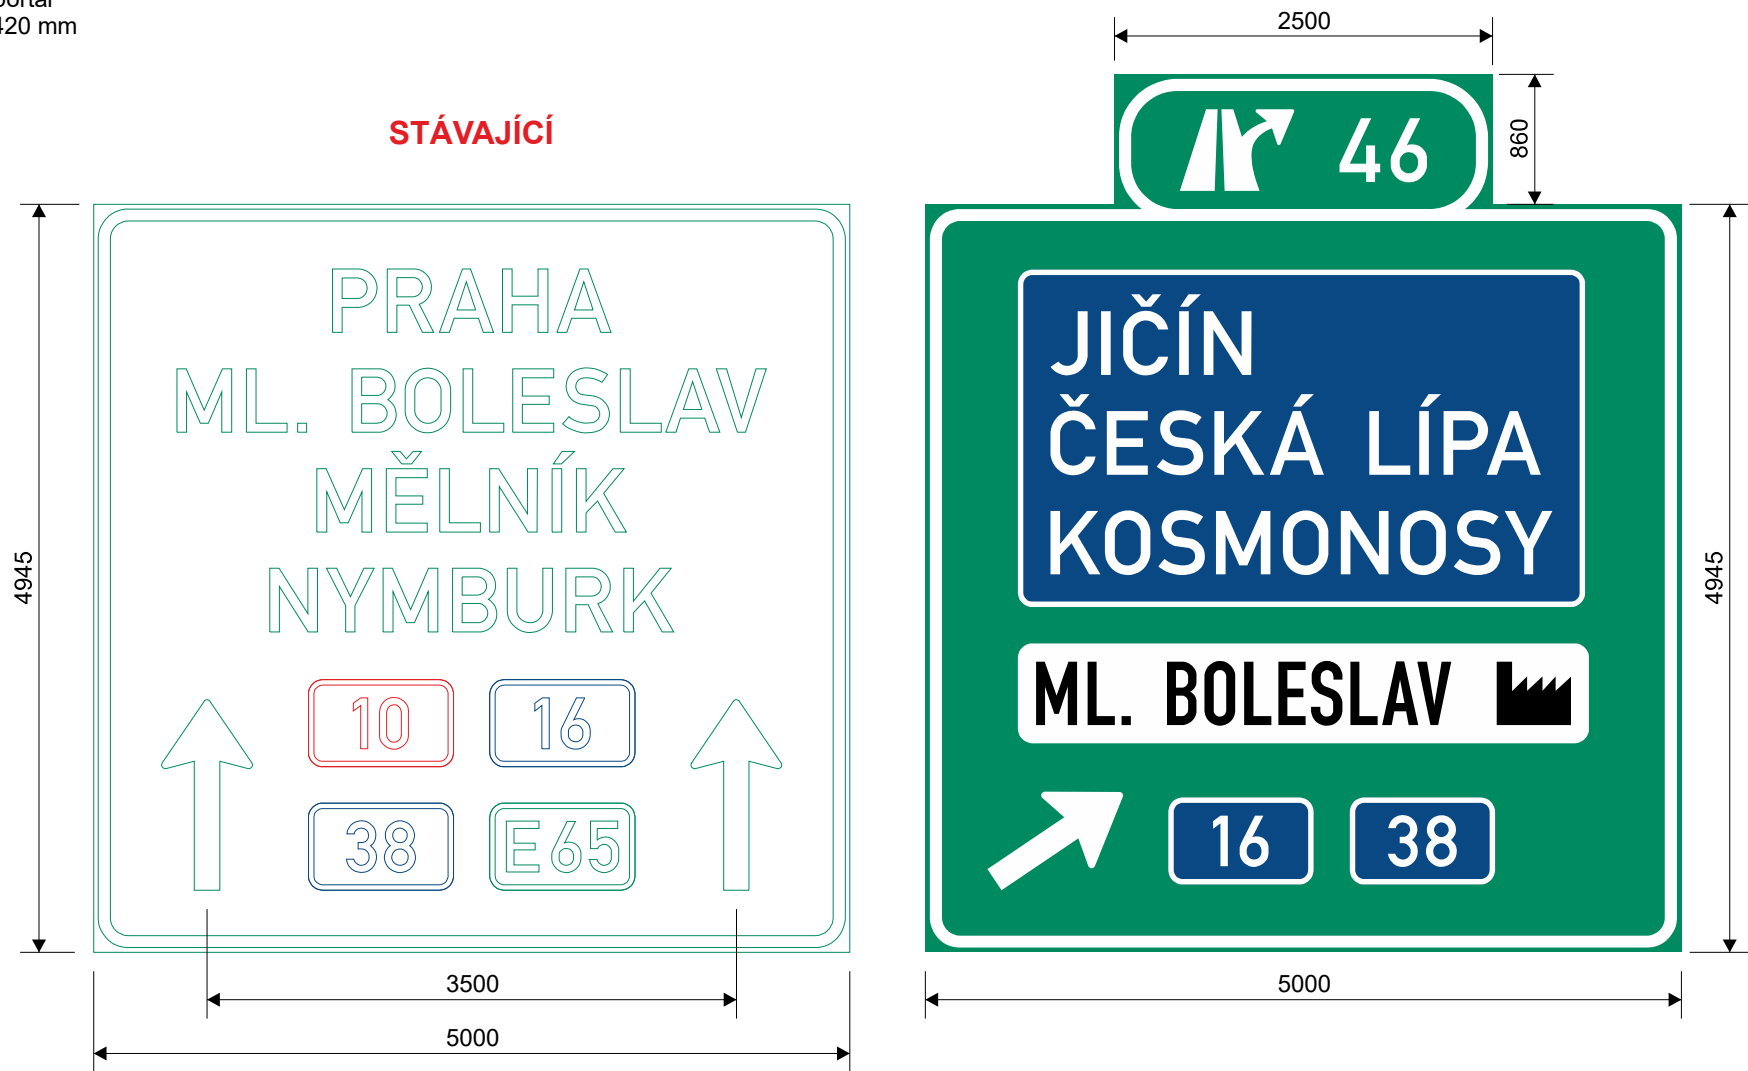


Kreslil: K. Kalová	Kontroloval: A. Seidl	Schváleno - datum: A. Seidl - 27/11/24	Název souboru: Disk_2024/Projekty/024-24-se_l-16_Mladá_Boleslav-Martinovice-PDPS/ Projektová dokumentace/SO 190 Dopravní značení/VLKP/024-24-001	Stupeň: PDPS	Datum: 27/11/24
			I/16 Mladá Boleslav - Martinovice SO 190 Dopravní značení - Velkoplošné dopravní značky		
			024-24-001	Měřítko: 1:50	Výtisk: List: 17/23

č. D10-04611
IS 7a - poloportál
Výška písma - 420 mm




č. D10-04612
IS 6e + IS 6f - portál
Výška písma - 315 mm

STÁVAJÍCÍ

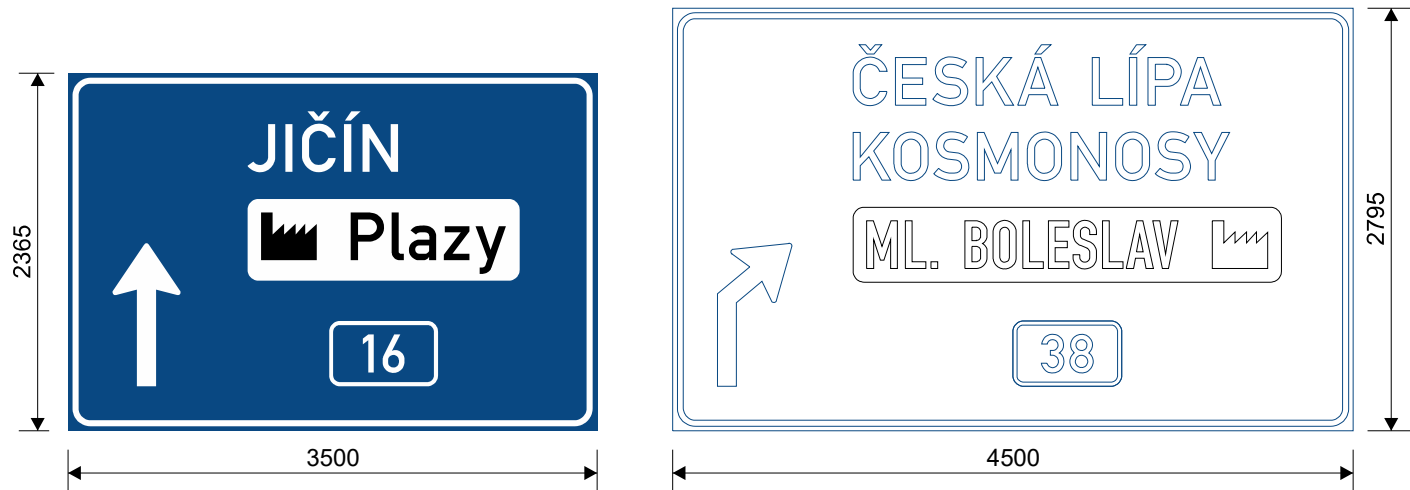


Kreslil: K. Kalová	Kontroloval: A. Seidl	Schváleno - datum: A. Seidl - 27/11/24	Název souboru: Disk_2024/Projekty/024-24-se_I-16_Mladá_Boleslav-Martinovice-PDPS/ Projektová dokumentace/SO 190 Dopravní značení/VLKP/024-24-001	Stupeň: PDPS	Datum: 27/11/24
DISK DOPRAVNÍ ZNAČENÍ			I/16 Mladá Boleslav - Martinovice SO 190 Dopravní značení - Velkoplošné dopravní značky		
024-24-001			Měřítko: 1:50	Výtisk:	List: 18/23

č. D10-04613
IS 6e + IS 7a - portál
Výška písma - 315 mm

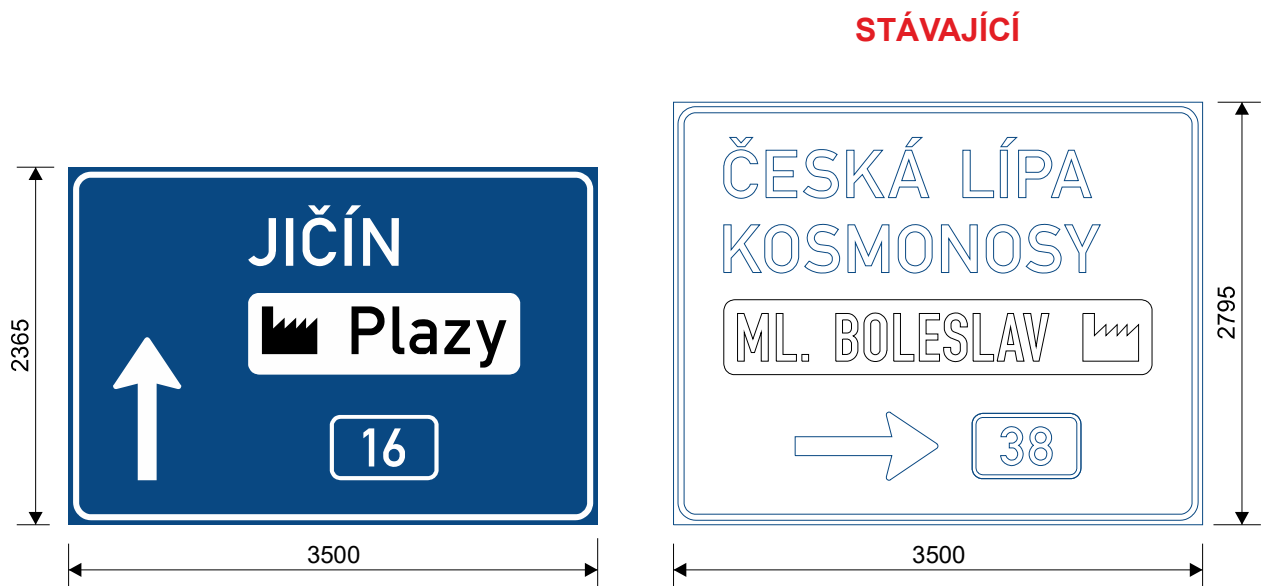


č. D10-04614
IS 9b - portál
Výška písma - 315 mm

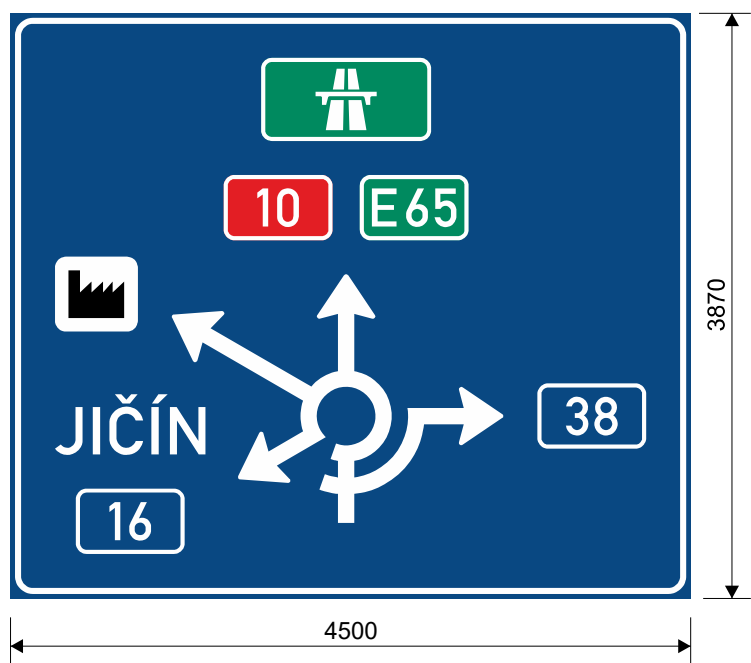


Kreslil: K. Kalová	Kontroloval: A. Seidl	Schváleno - datum: A. Seidl - 27/11/24	Název souboru: Disk_2024/Projekty/024-24-se_I-16_Mladá_Boleslav-Martinovice-PDPS/ Projektová dokumentace/SO 190 Dopravní značení/VLKP/024-24-001	Stupeň: PDPS	Datum: 27/11/24
 DOPRAVNÍ ZNAČENÍ			I/16 Mladá Boleslav - Martinovice SO 190 Dopravní značení - Velkoplošné dopravní značky		
			024-24-001	Měřítko: 1:50	Výtisk: List: 19/23

č. D10-04616
IS 7a - poloportál
Výška písma - 315 mm


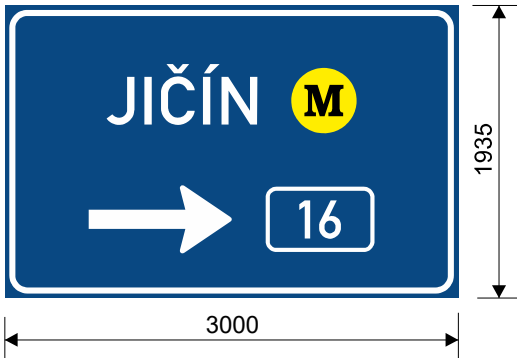


č. D10-04620
IS 9b
Výška písma - 210 mm

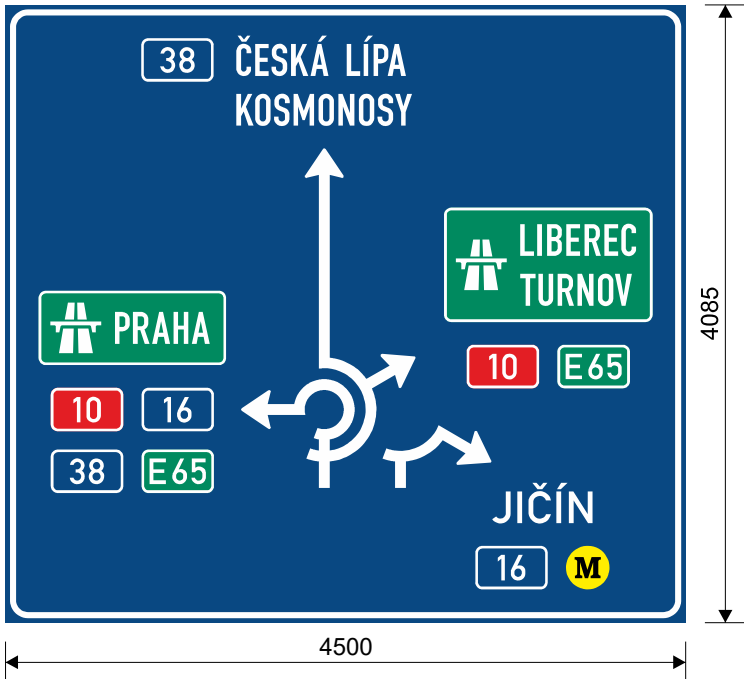

Kreslil: K. Kalová	Kontroloval: A. Seidl	Schváleno - datum: A. Seidl - 27/11/24	Název souboru: Disk_2024/Projekty/024-24-se_I-16_Mladá_Boleslav-Martinovice-PDPS/ Projektová dokumentace/SO 190 Dopravní značení/VLKP/024-24-001	Stupeň: PDPS	Datum: 27/11/24
			I/16 Mladá Boleslav - Martinovice SO 190 Dopravní značení - Velkoplošné dopravní značky		
			024-24-001	Měřítko: 1:50	Výtisk: List: 20/23



STÁVAJÍCÍ

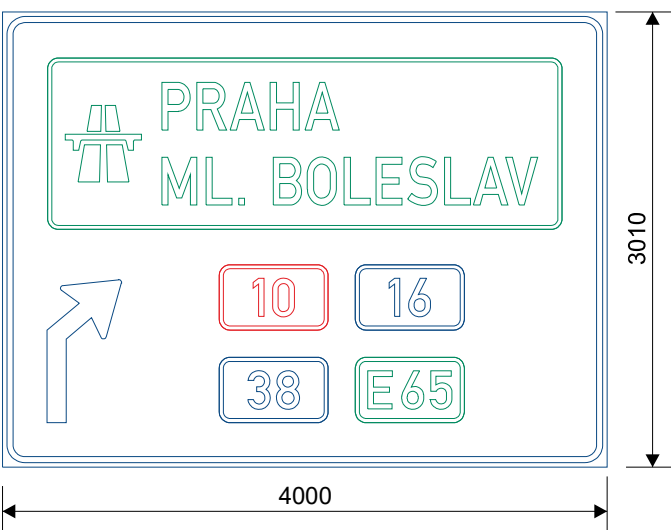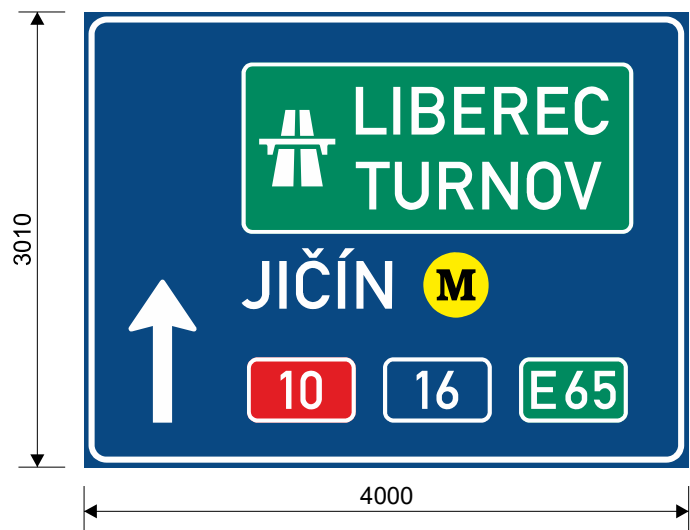


U cílů „PRAHA“ a „ML. BOLESLAV“ použita komprese 85 %.

Kreslil: K. Kalová	Kontroloval: A. Seidl	Schváleno - datum: A. Seidl - 27/11/24	Název souboru: Disk_2024/Projekty/024-24-se_I-16_Mladá_Boleslav-Martinovice-PDPS/ Projektová dokumentace/SO 190 Dopravní značení/VLKP/024-24-001	Stupeň: PDPS	Datum: 27/11/24
			I/16 Mladá Boleslav - Martinovice SO 190 Dopravní značení - Velkoplošné dopravní značky		
			024-24-001	Měřítko: 1:50	Výtisk: List: 21/23

STÁVAJÍCÍ

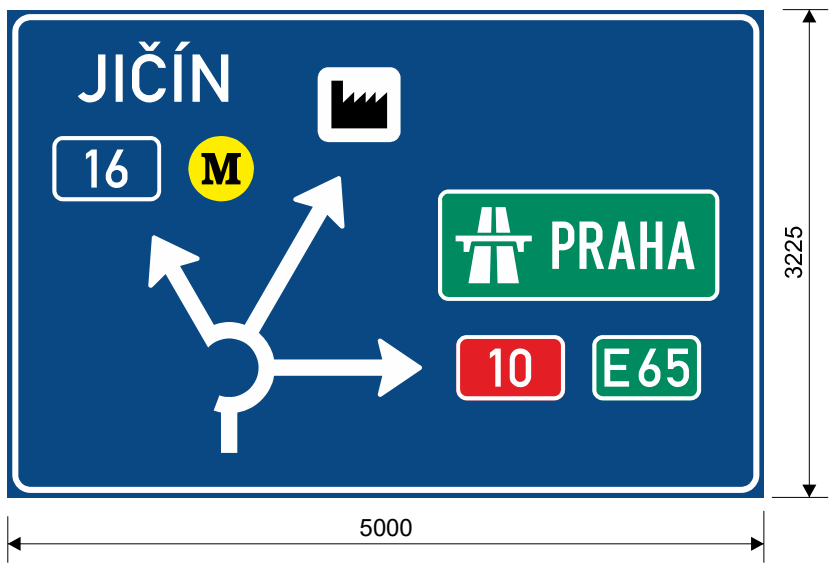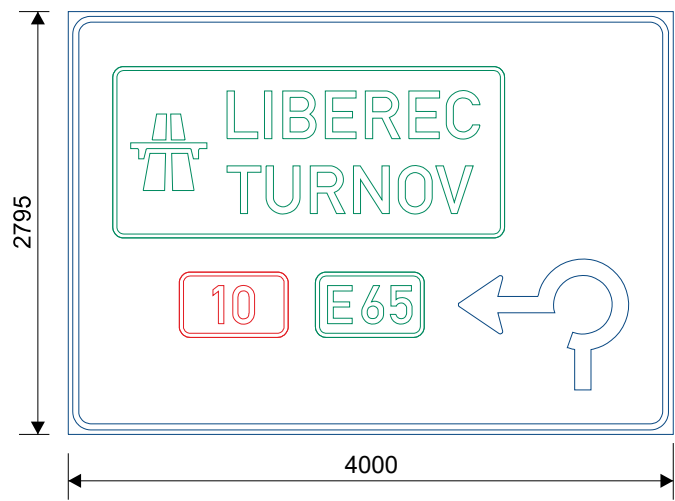

Kreslil: K. Kalová	Kontroloval: A. Seidl	Schváleno - datum: A. Seidl - 27/11/24	Název souboru: Disk_2024/Projekty/024-24-se_i-16_Mladá_Boleslav-Martinovice-PDPS/ Projektová dokumentace/SO 190 Dopravní značení/VLKP/024-24-001	Stupeň: PDPS	Datum: 27/11/24
			I/16 Mladá Boleslav - Martinovice SO 190 Dopravní značení - Velkoplošné dopravní značky		
			024-24-001	Měřítko: 1:50	Výtisk: List: 22/23

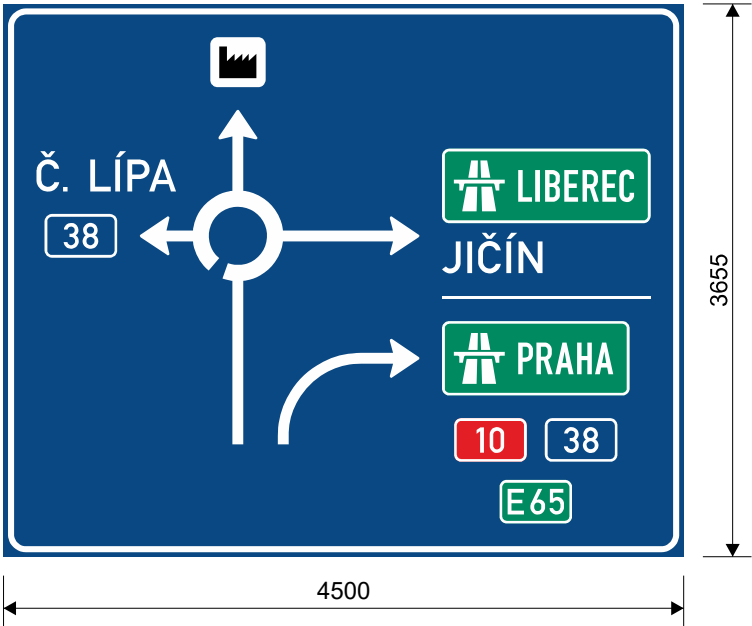

Značka neodpovídá VL 6.1.

Kreslil: K. Kalová	Kontroloval: A. Seidl	Schváleno - datum: A. Seidl - 27/11/24	Název souboru: Disk_2024/Projekty/024-24-se_I-16_Mladá_Boleslav-Martinovice-PDPS/ Projektová dokumentace/SO 190 Dopravní značení/VLKP/024-24-001	Stupeň: PDPS	Datum: 27/11/24
			I/16 Mladá Boleslav - Martinovice SO 190 Dopravní značení - Velkoplošné dopravní značky		
			024-24-001	Měřítko: 1:50	Výtisk: List: 23/23