



PORTÁL 1 P016-0001H-P1

0,100 km I/16
dvojnosiťový portál
značka č. IS9b+IS9b – IS8b
plocha 54,04 m²

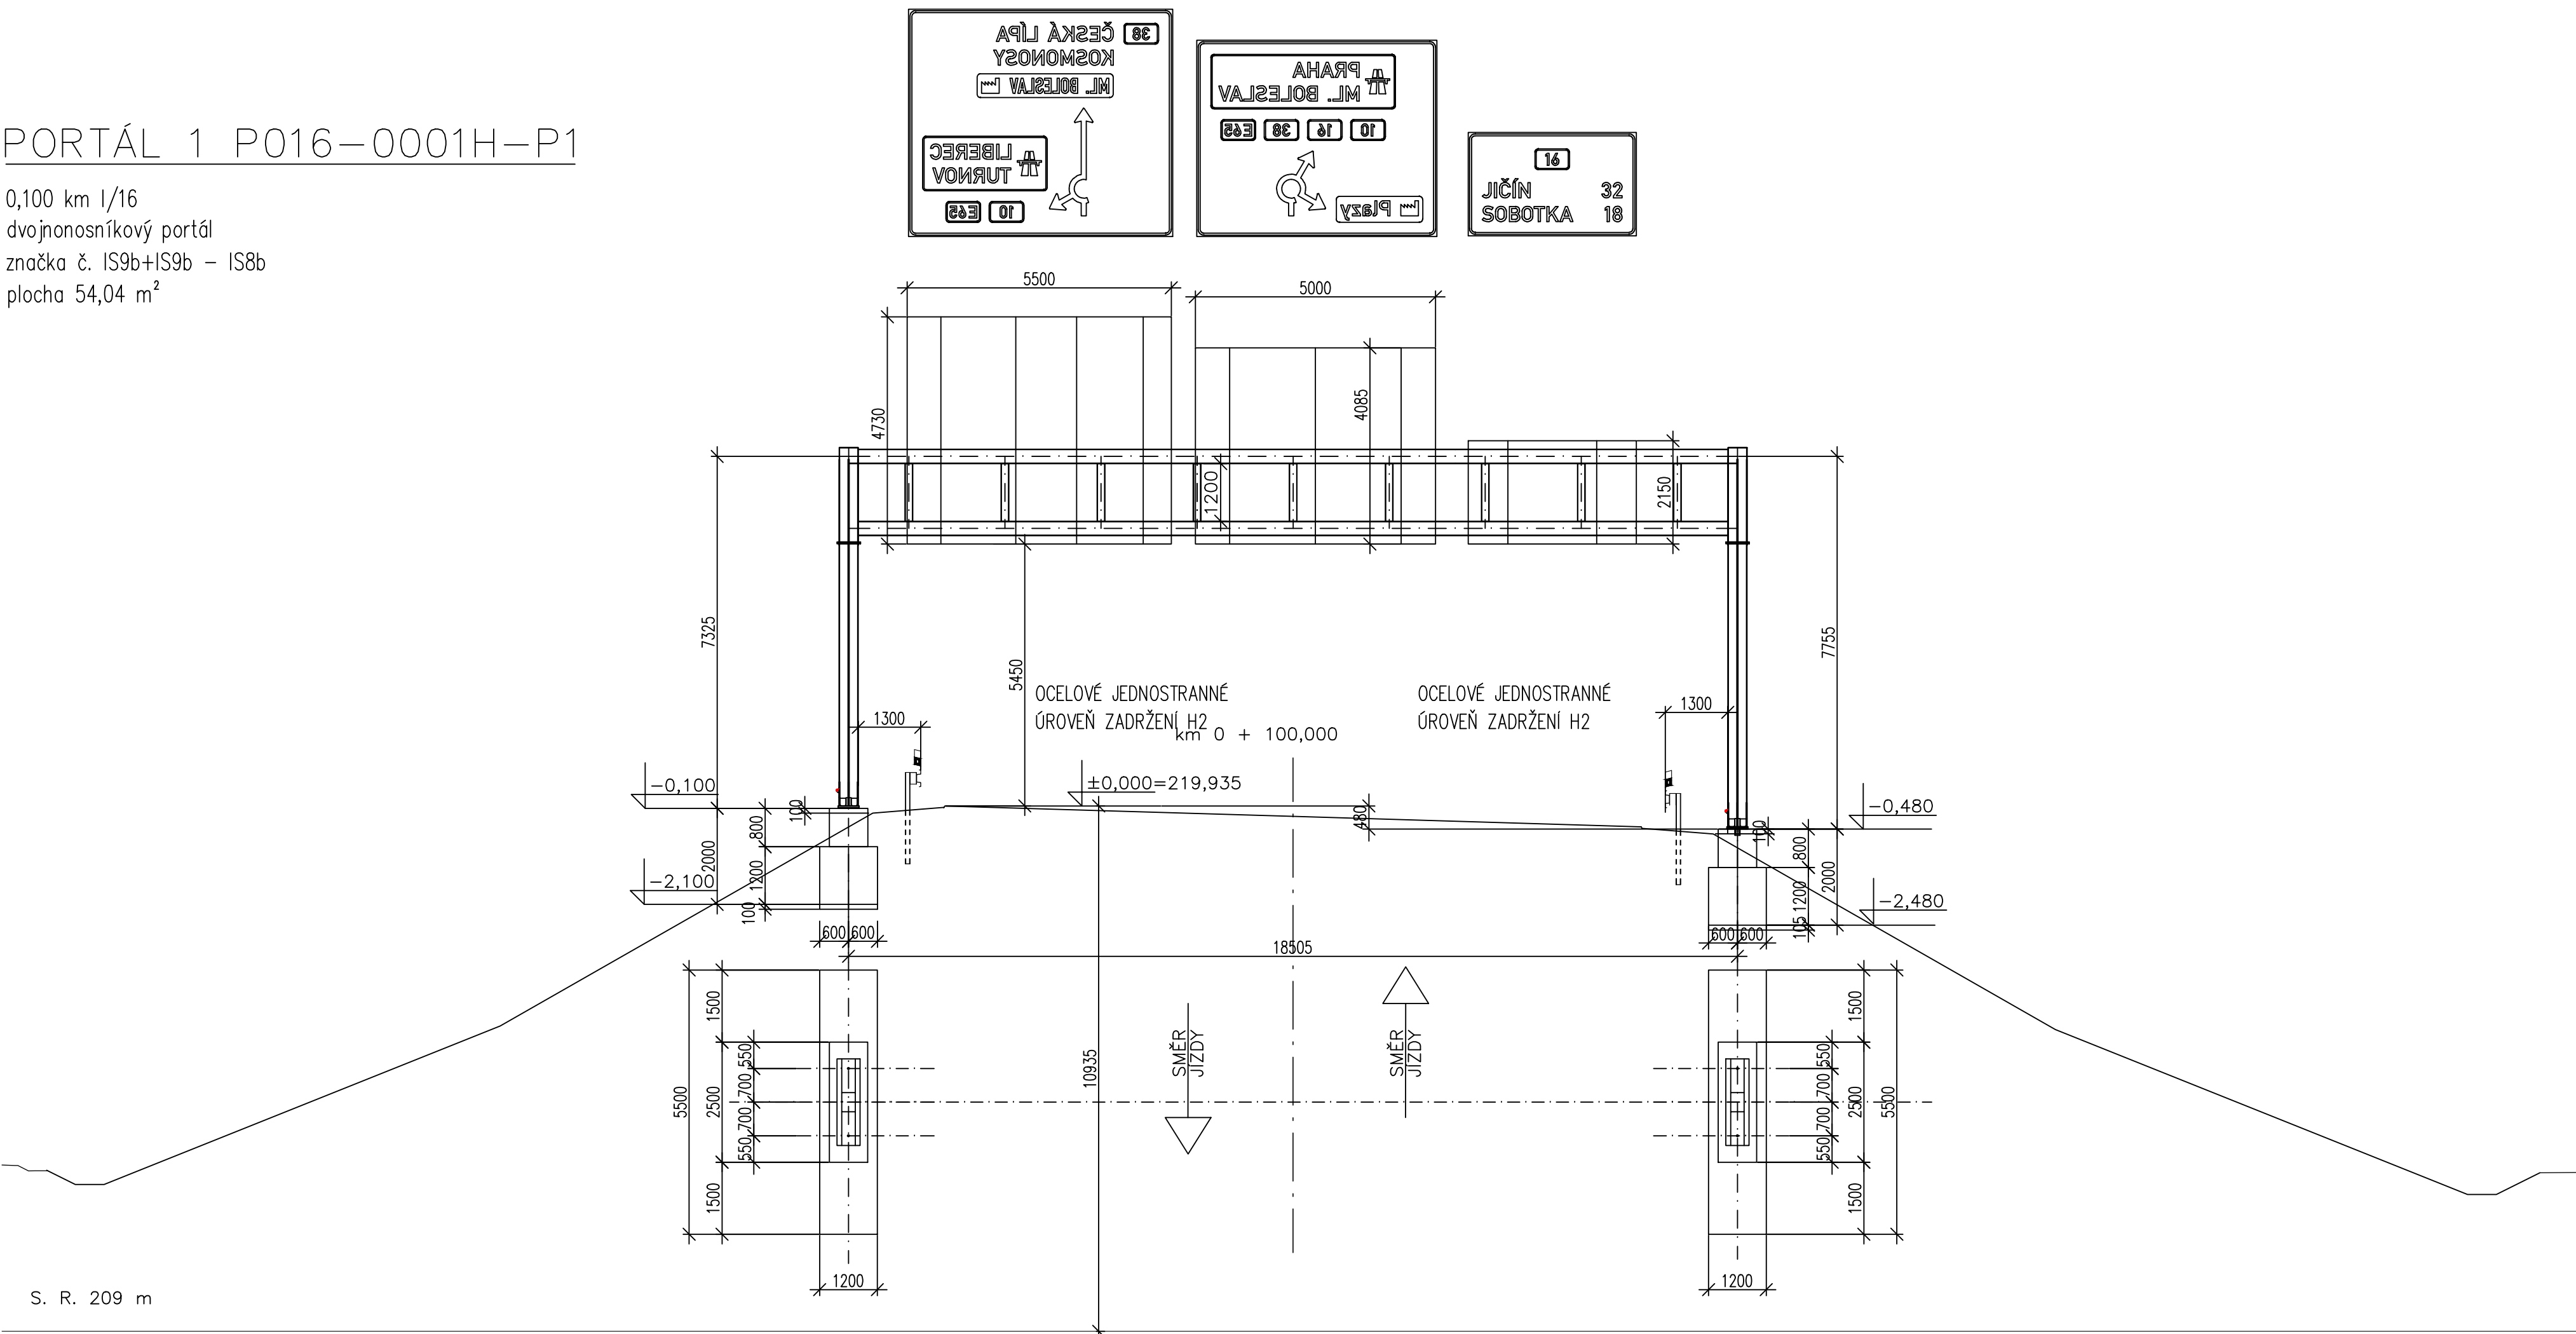

PORTÁL 2 P016-0076H-P1

7,650 km I/16
poloportál
značka č. IS6g
plocha 8,30 m²

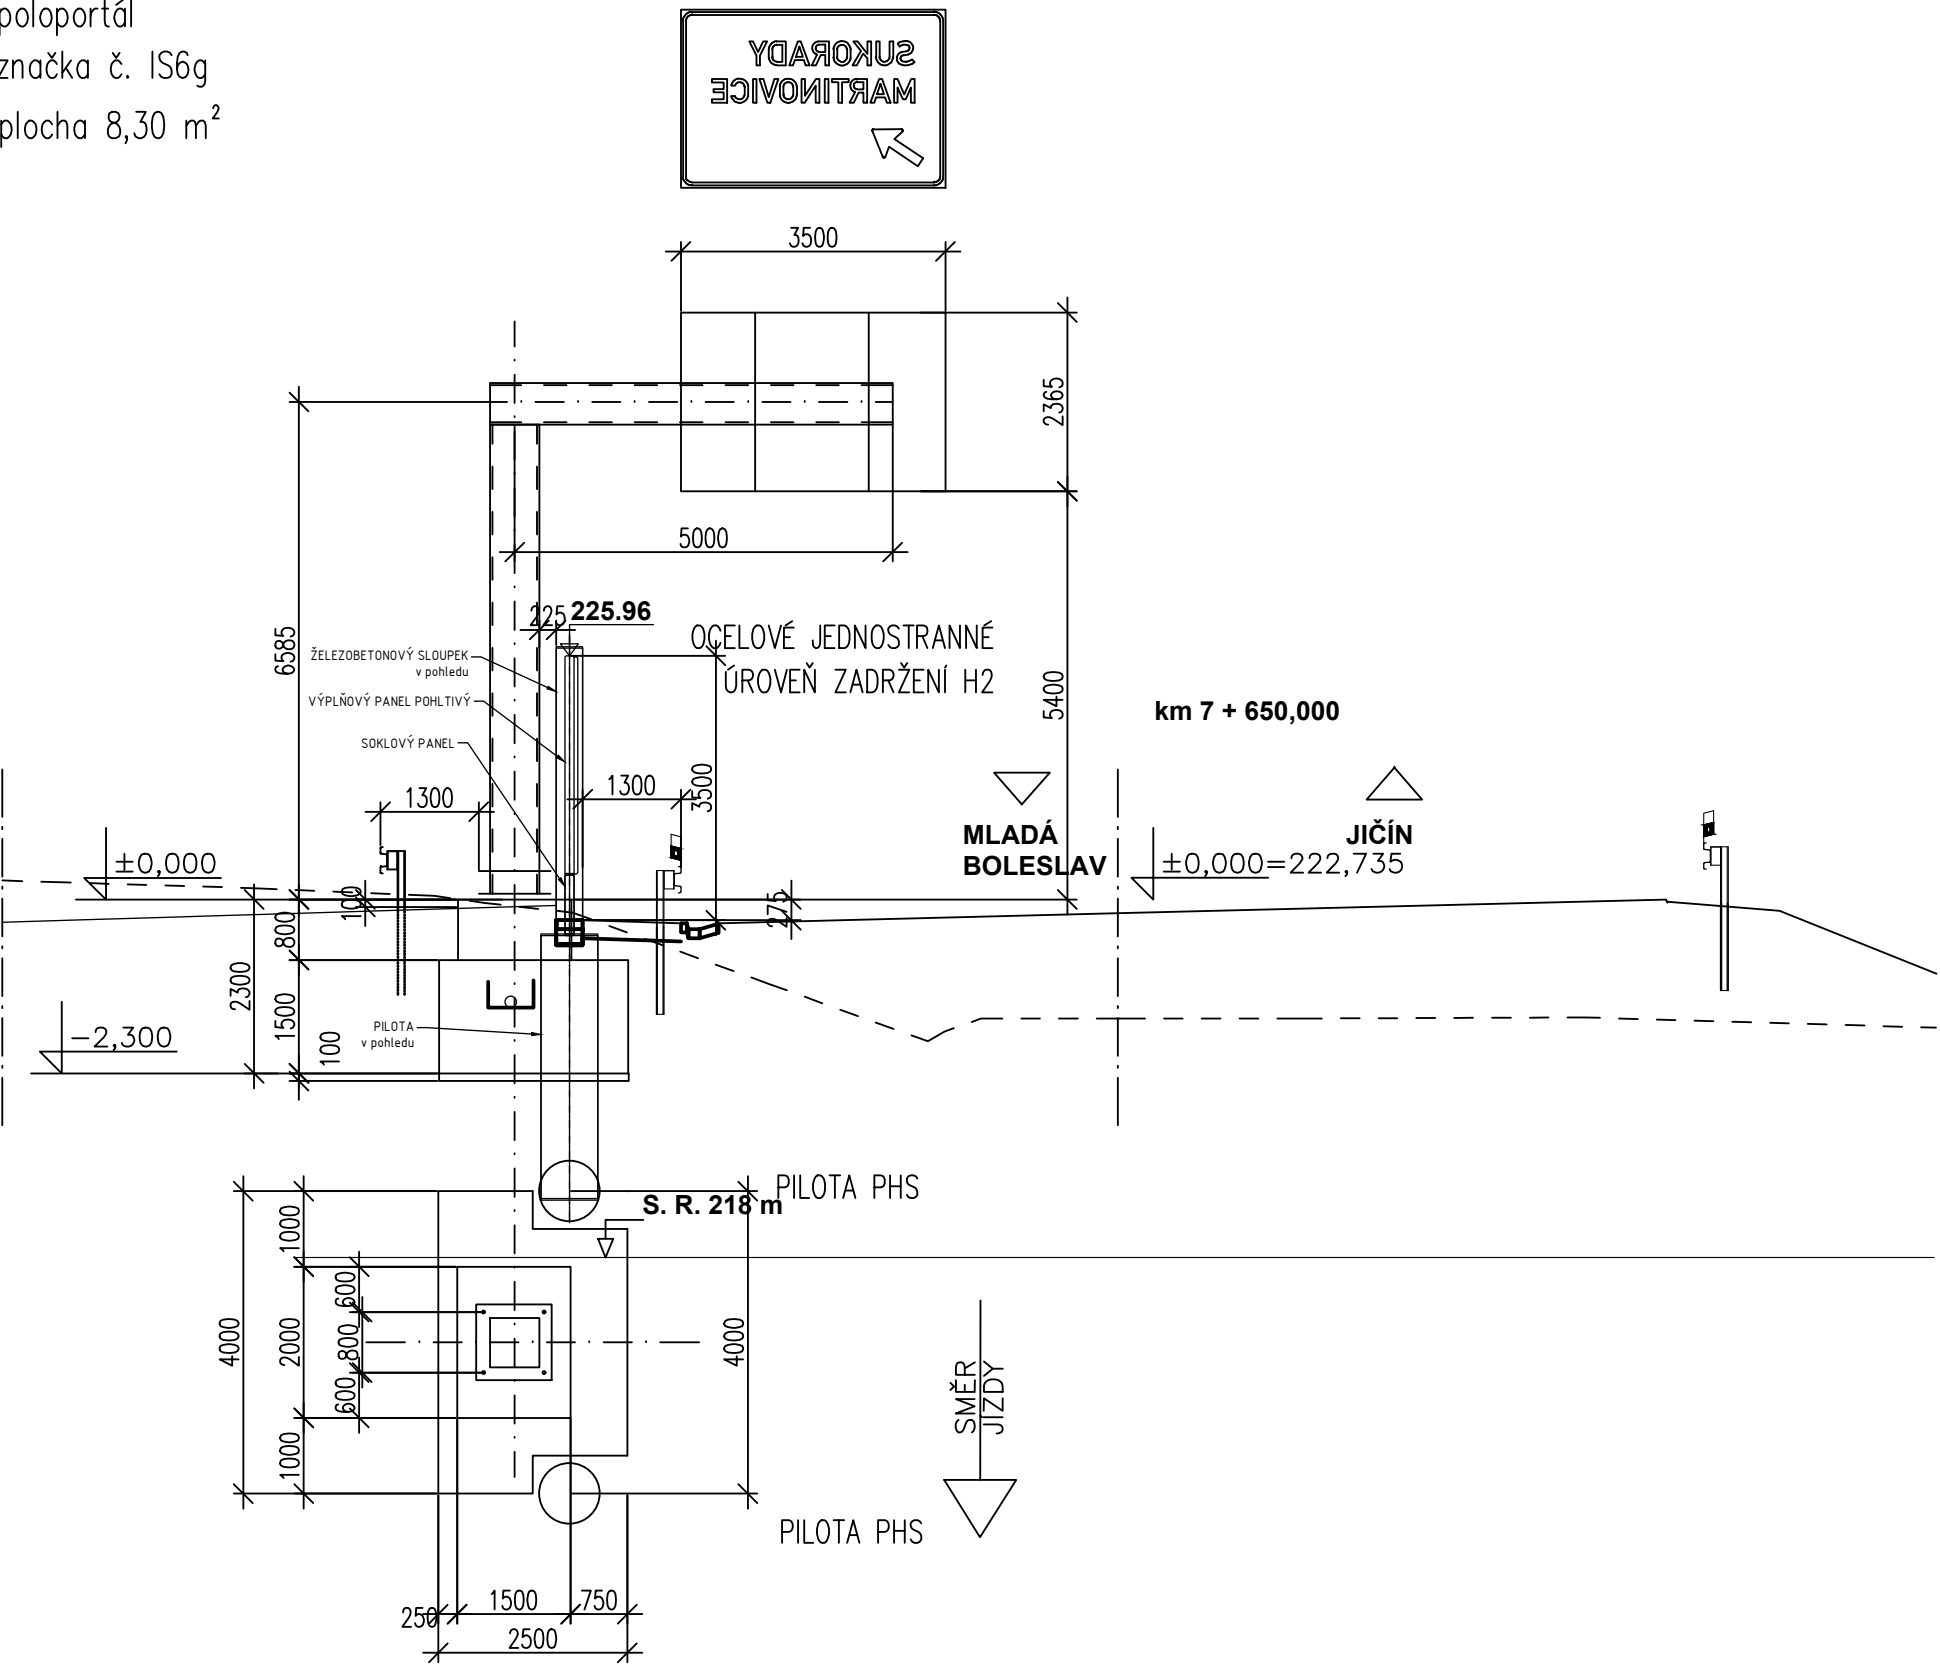

Souřadnicový systém: S-JTSK
Výškový systém: Bpv

DOD.21

SO 190 Dopravní značení

Objednatel:
**ŘEDITELSTVÍ SILNIC A DÁLNIC**
Ředitelství silnic a dálnic s. p.
Čerčanská 2023/12, Krč, 140 00 Praha 4

Zhotovitel:
**Valbek, spol. s r.o.**
Vaňurova 505/17
460 07 Liberec 3

	Vypracoval	STANISLAV KRUPÍČKA	Zak. číslo	024-24
	Zodp. projektant	ING. PETER HAJOŠ	Datum	02/2025
	Tech. kontrola	ANTONIN SEIDL	Stupeň	PDPS
	Akce	I/16 MLADÁ BOLESLAV - MARTINOVICE		
Zhotovitel: DISK s.r.o. Mentšikova 1239/10 160 00 Praha 6	Příloha PORTÁLY			Počet formátů 6 x A4
				Měřítko 1 : 100
			Č. přílohy	Paré
			4	