



ŘEZ A-A 1:100

OSOULUŽENÍ 01

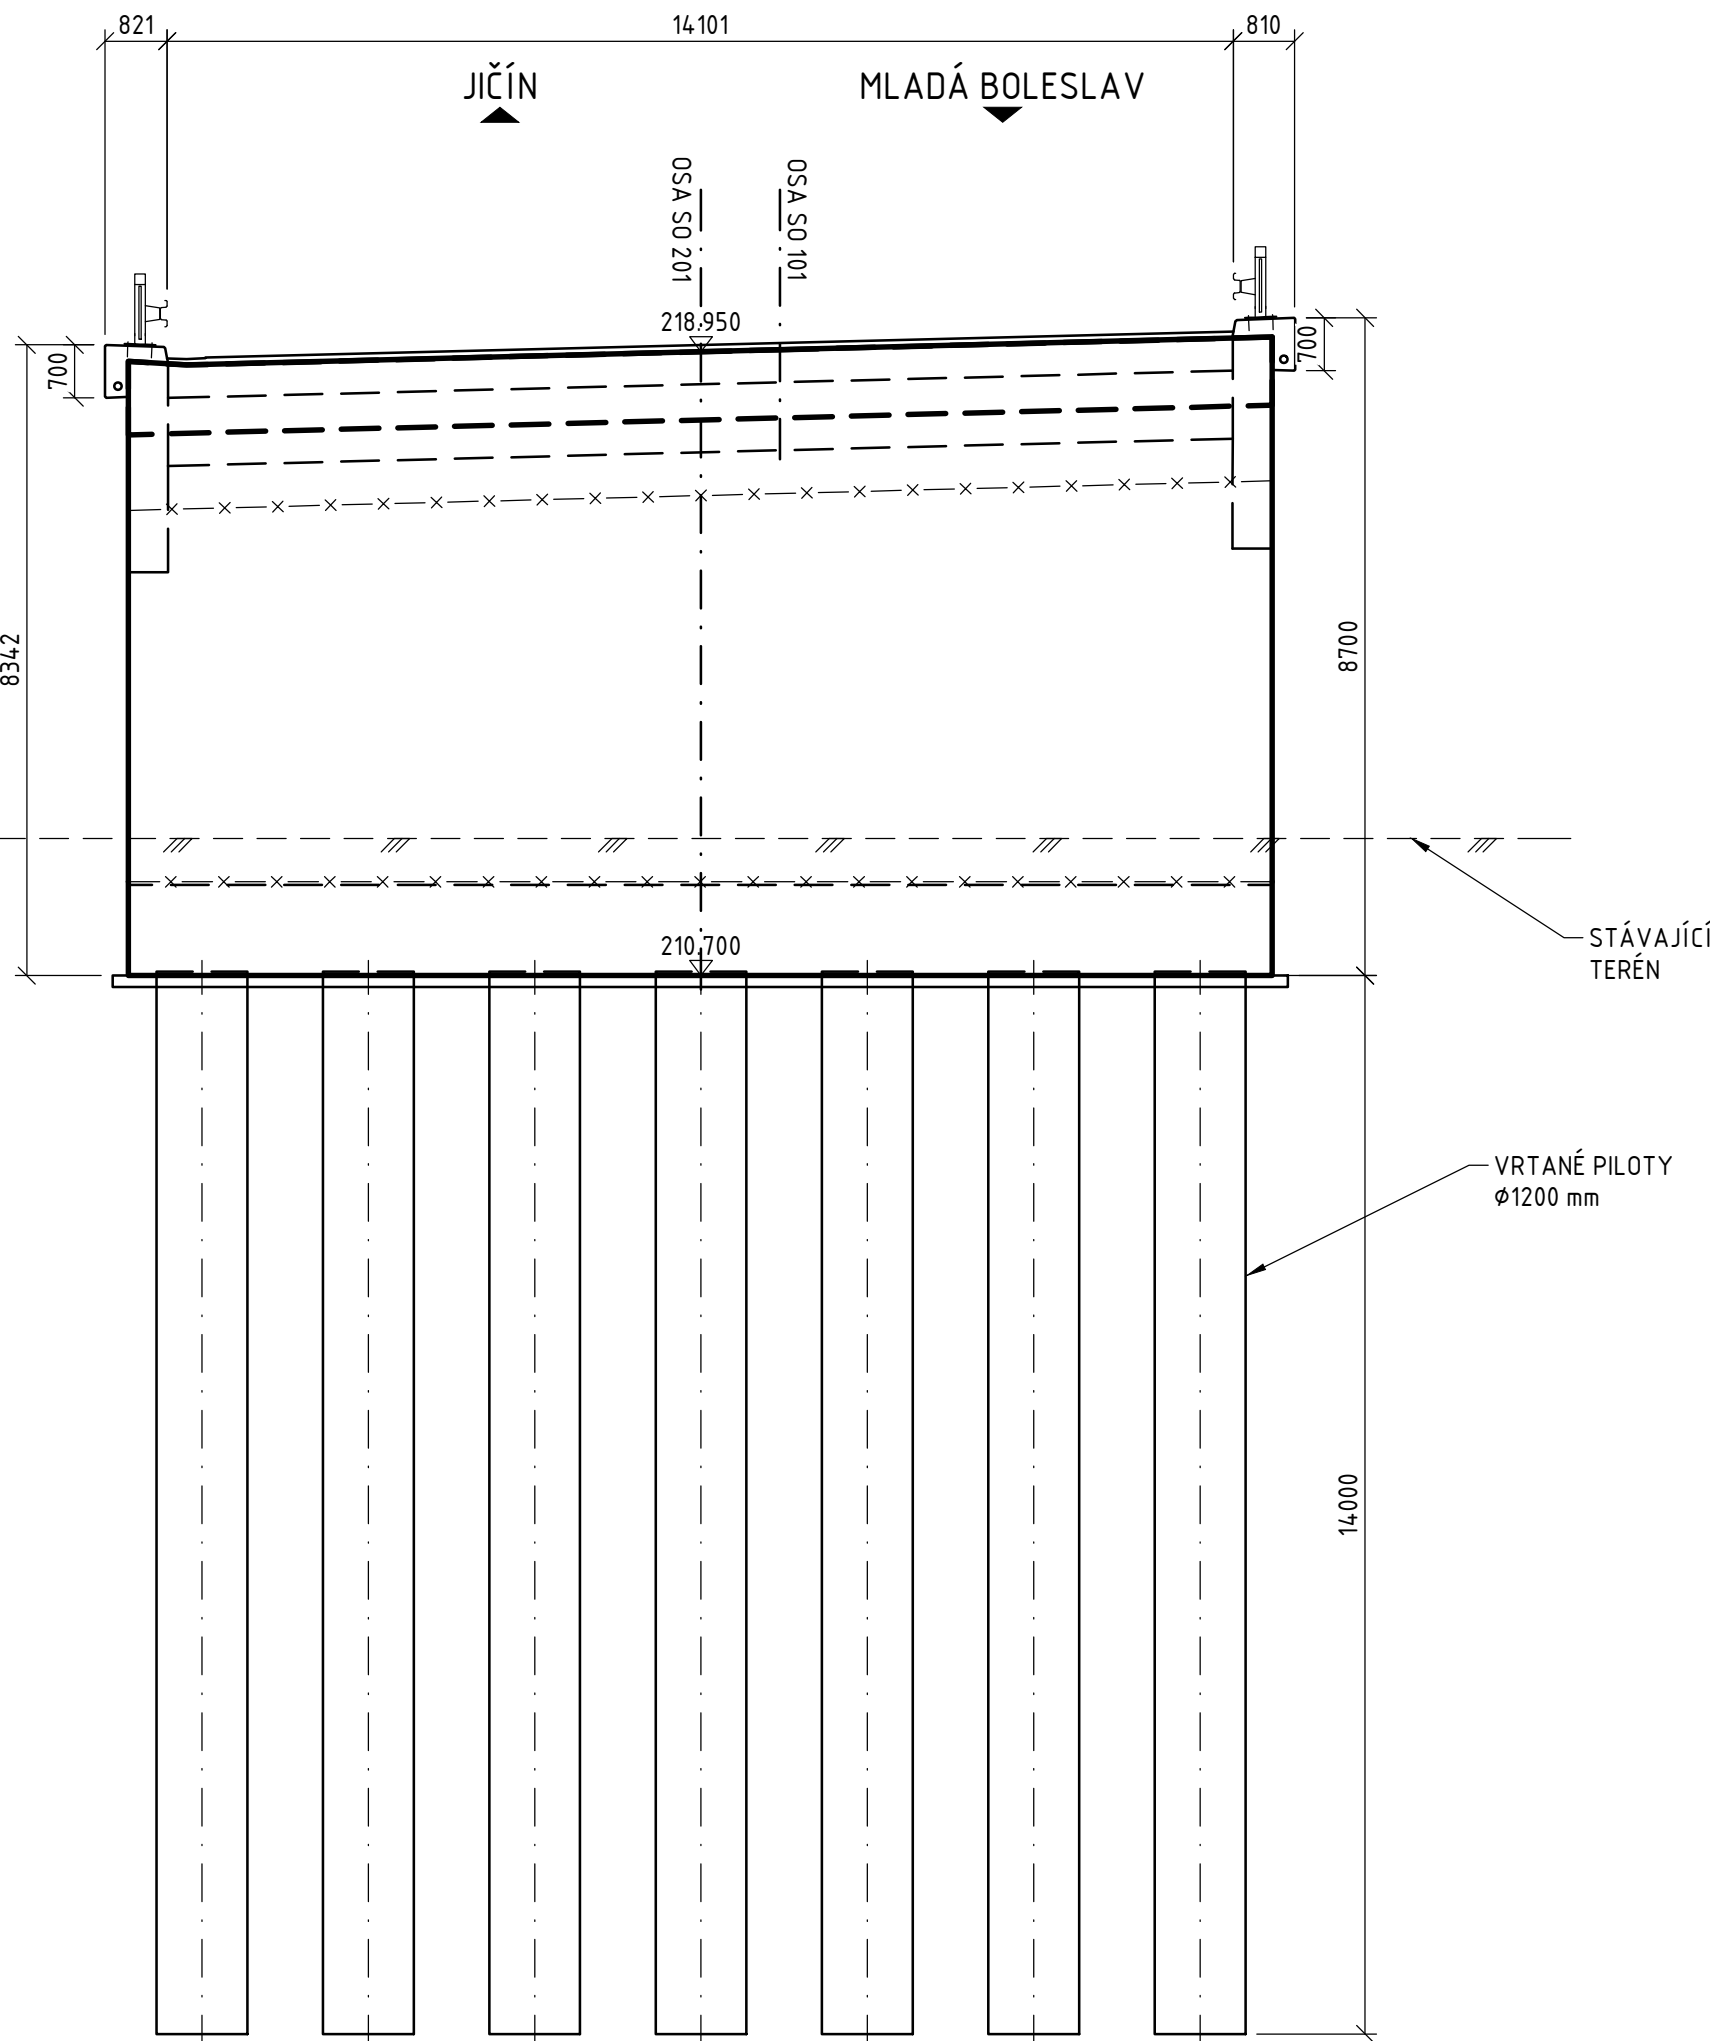


ŘEZ C-C 1:100

OSOULUŽENÍ 03

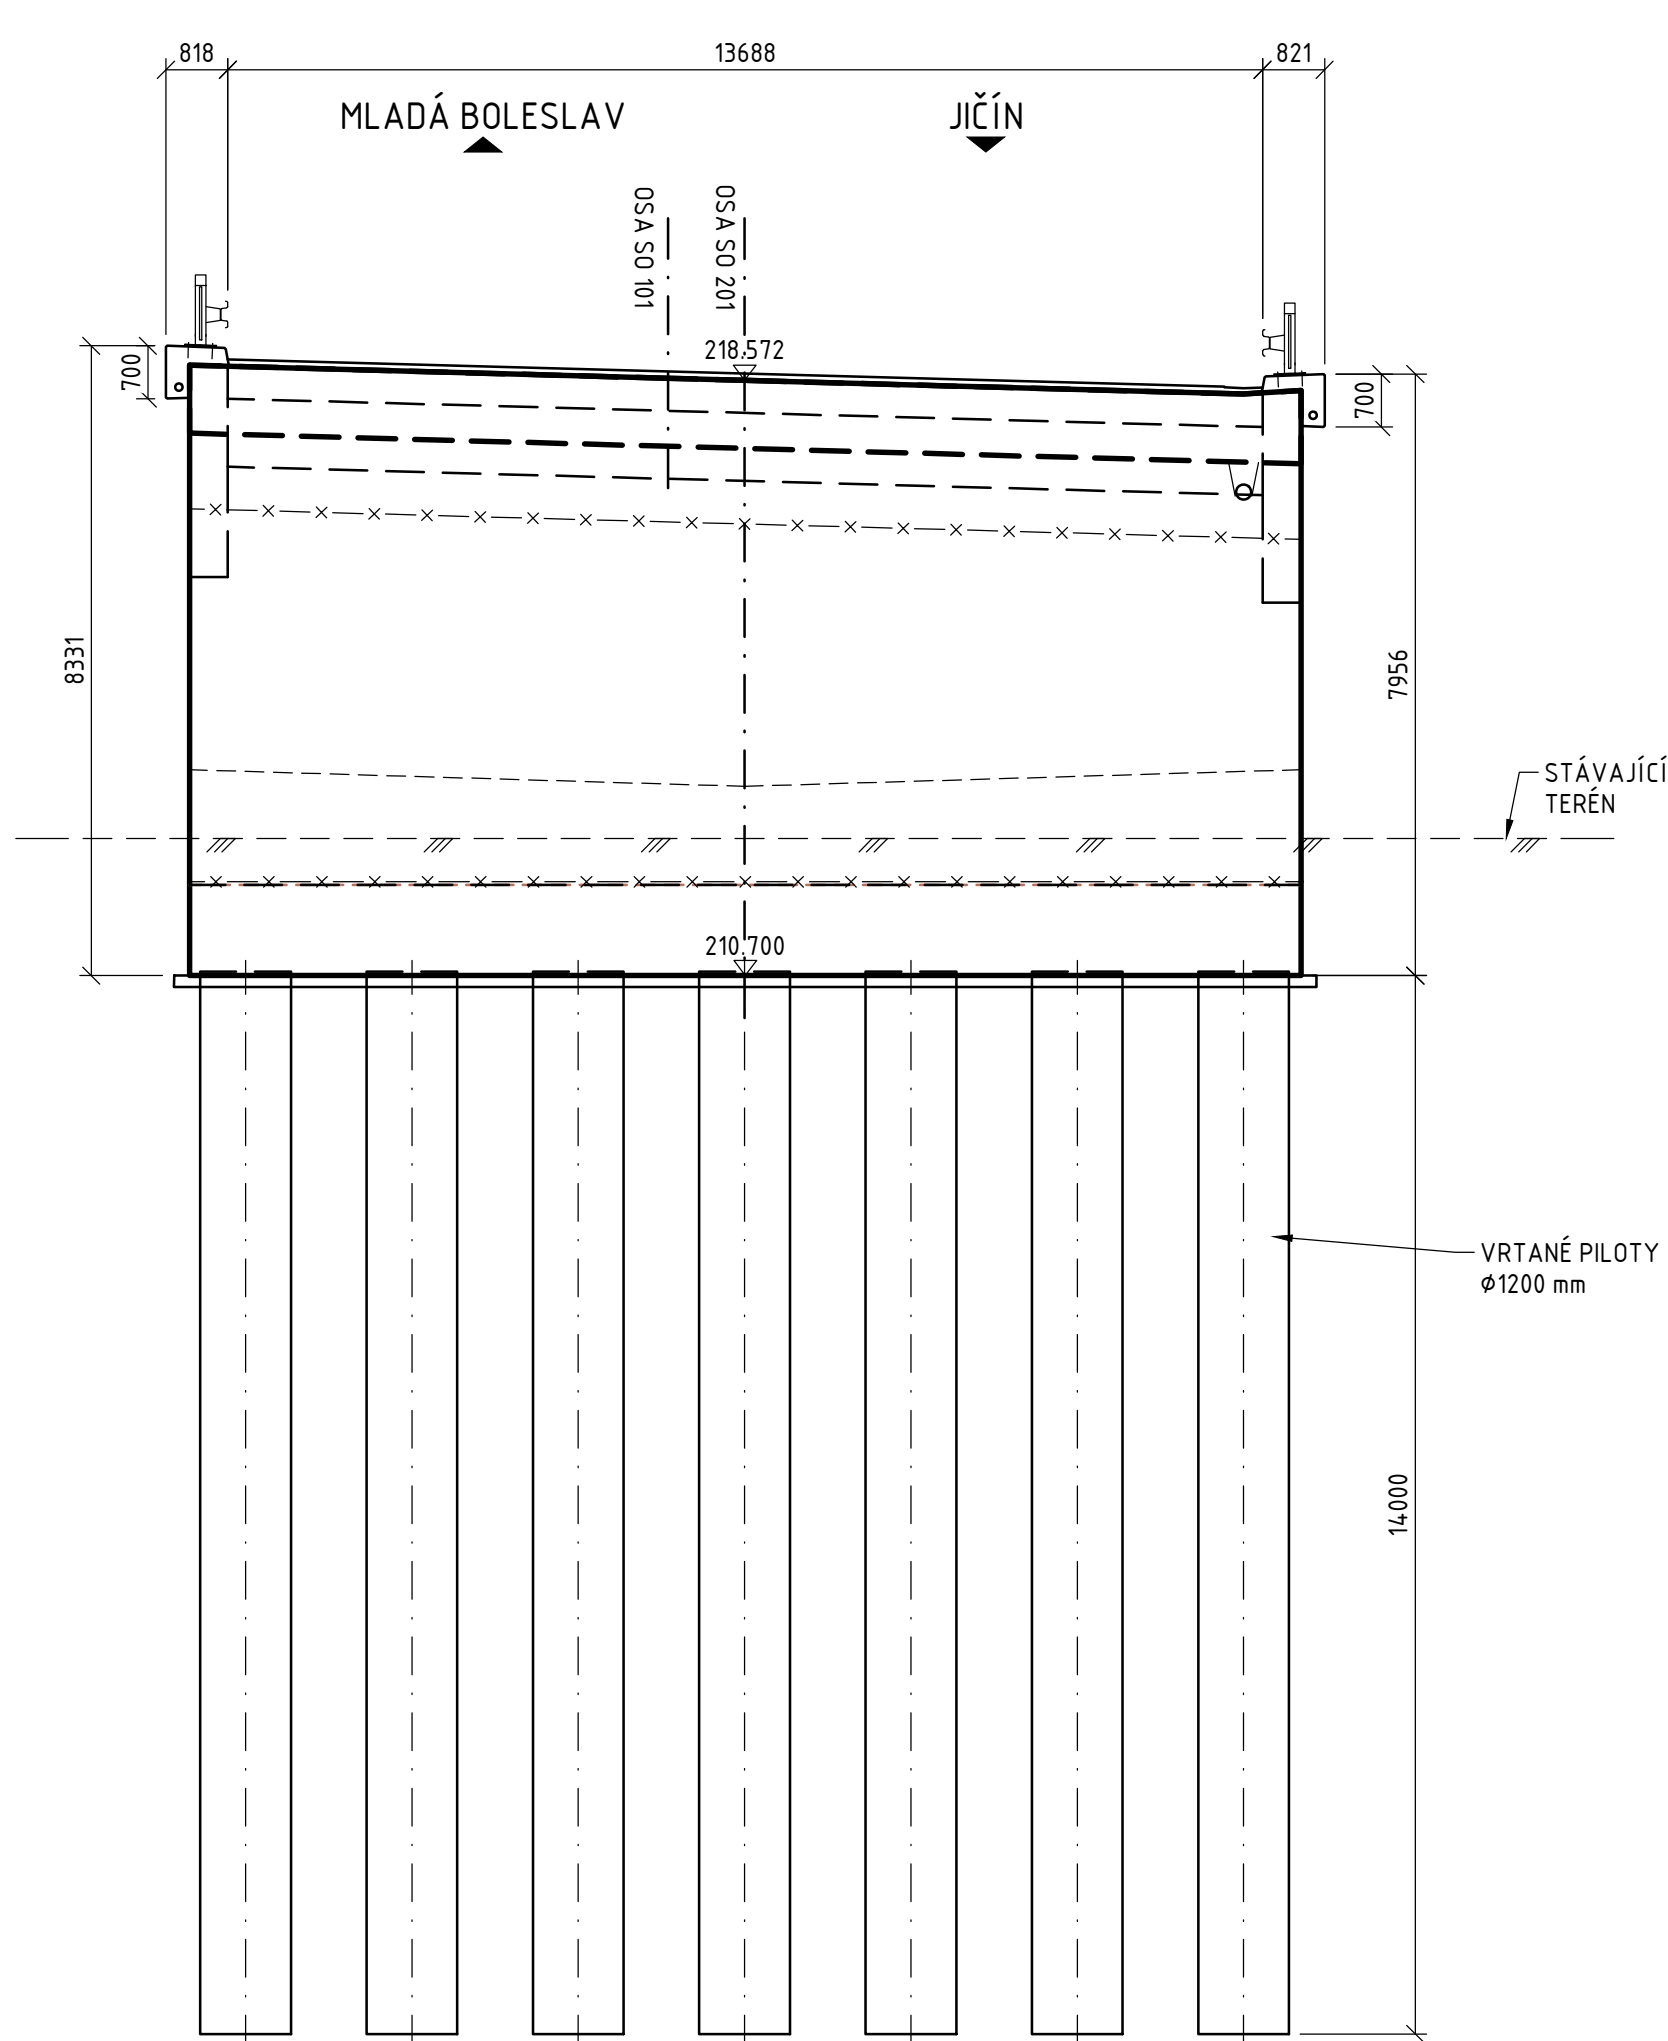


ŘEZ B-B 1:100

OSOULUŽENÍ P2

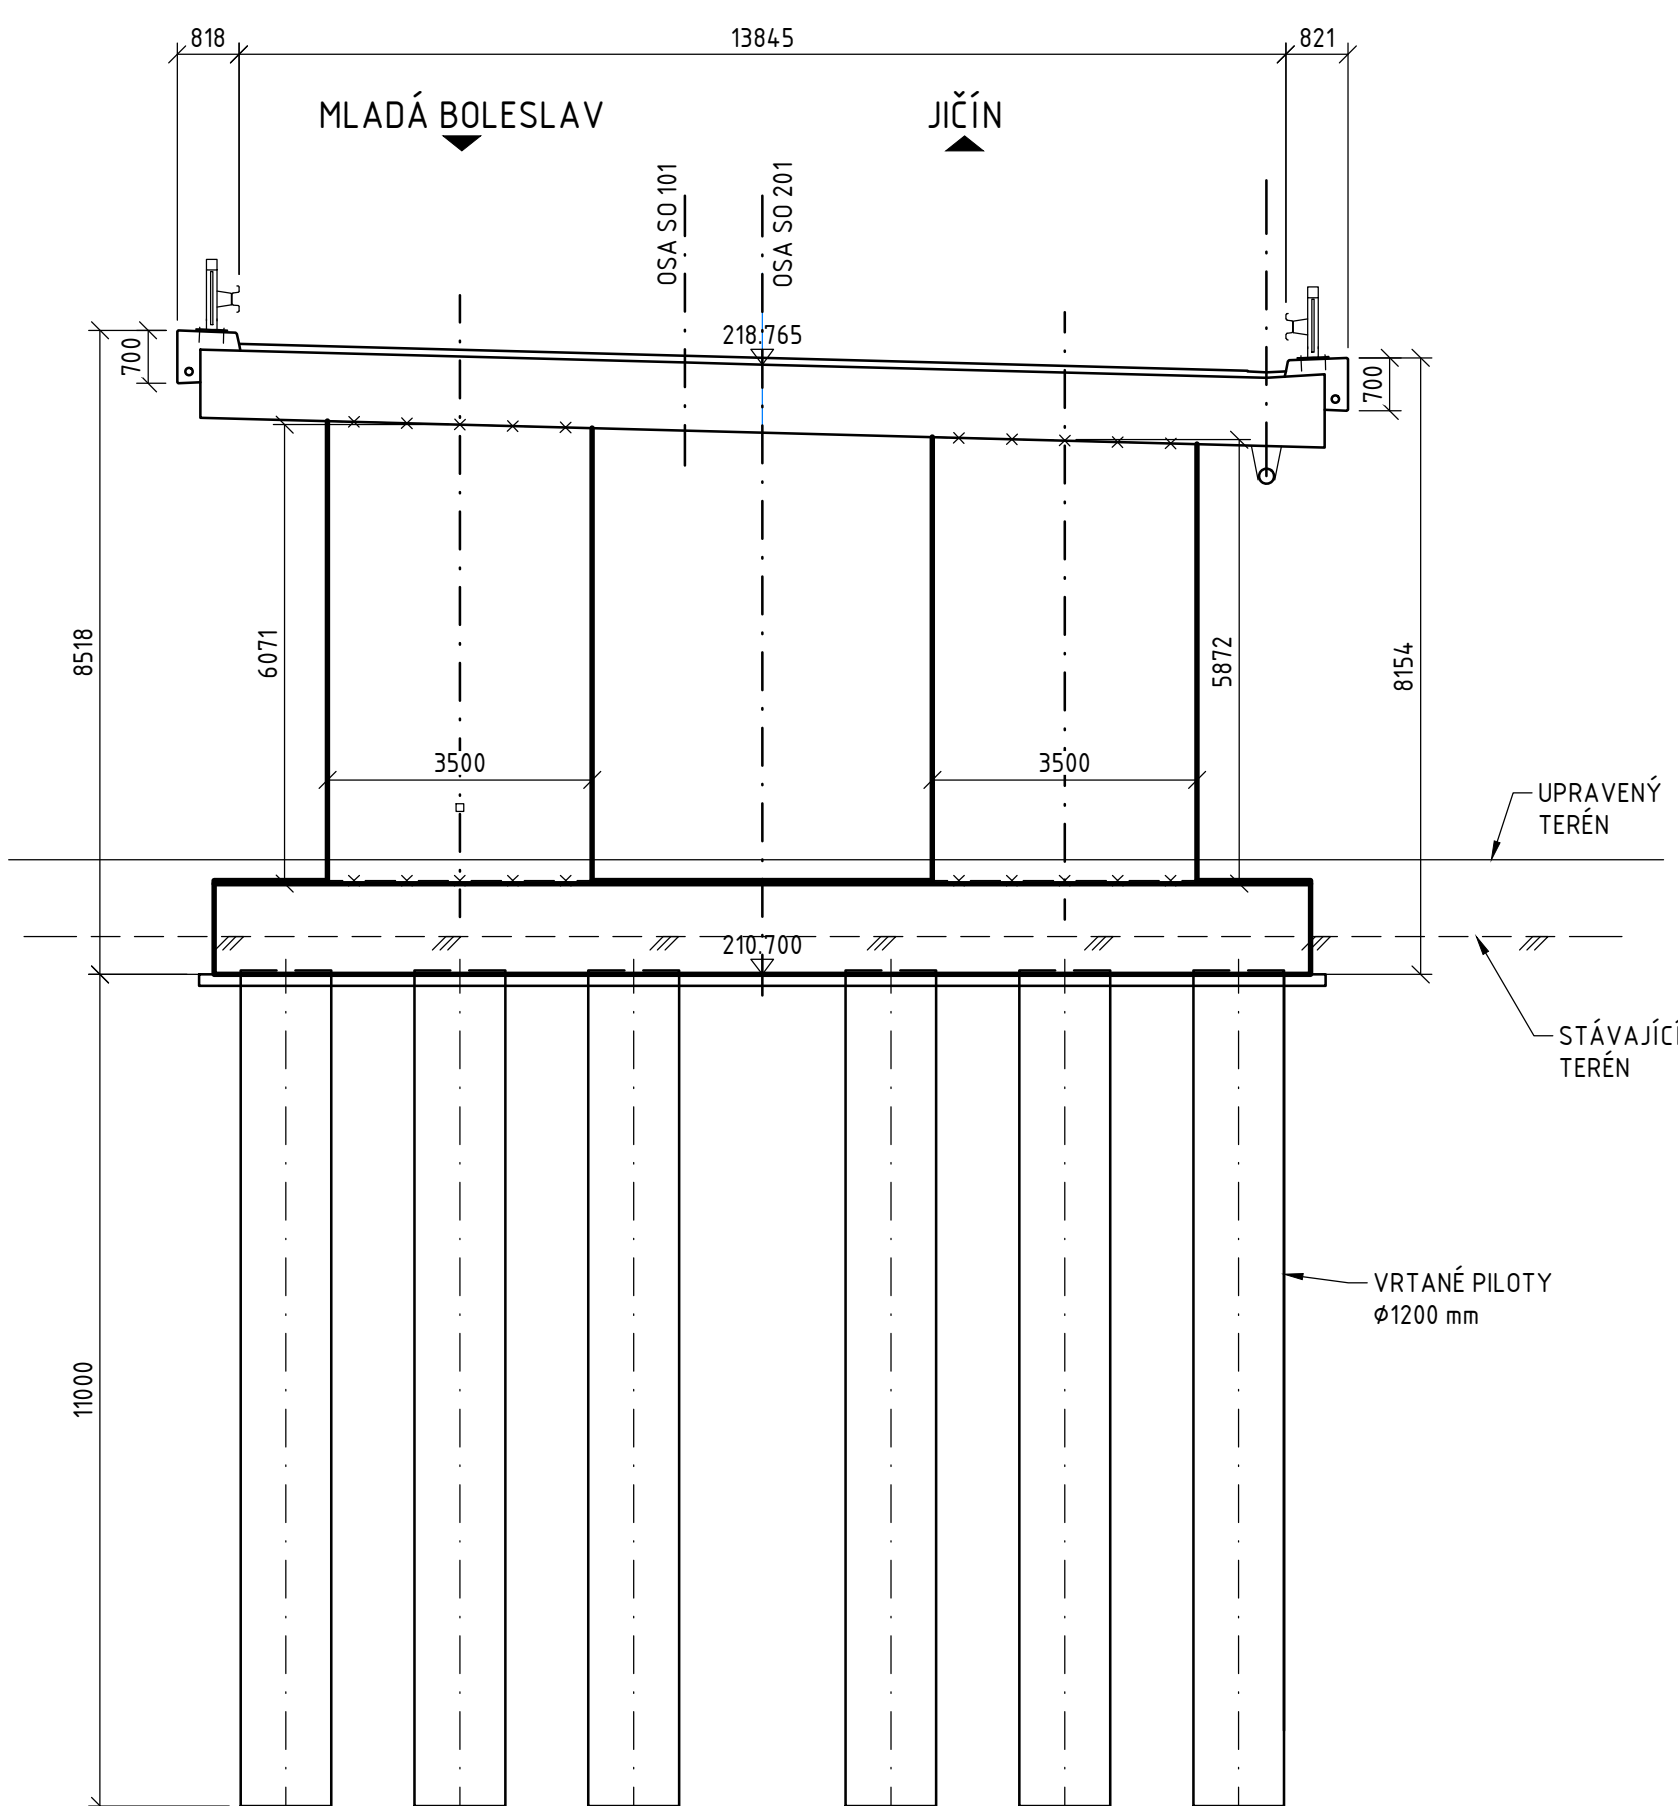

PŮDORYSNÉ SCHÉMA ŘEZŮ

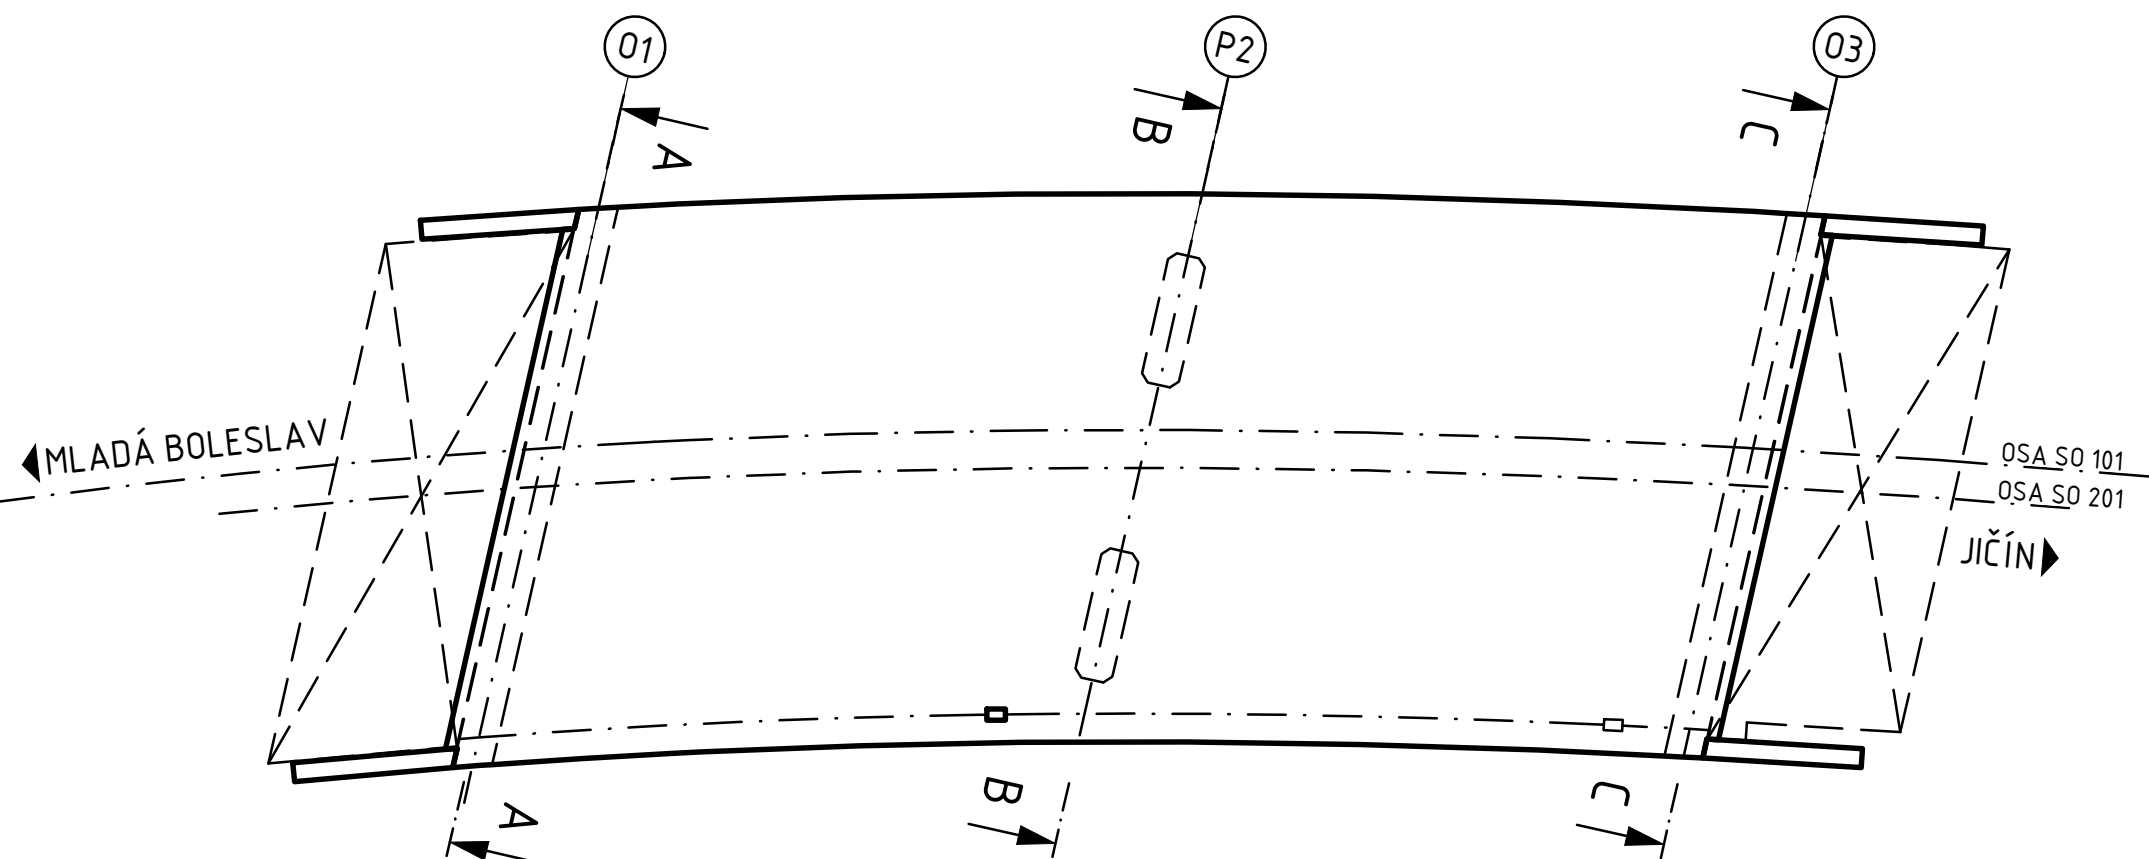

POZNÁMKY:

- NEDÍLNOU SOUČÁSTÍ VÝKRESU JSOU POZNÁMKY A SPECIFIKACE UVEDENÉ NA VÝKRESE POZNÁMEK A TECHNICKÝCH SPECIFIKACÍ

Souřadnicový systém: S-JTSK
Výškový systém: Bpv

SO 201 MOST NA I/16 PŘES MK A ZALUŽANSKOU VODOTEČ V KM 0,228

Objednatel:



Ředitelství silnic a dálnic s. p.
Čerčanská 2023/12, Krč, 140 00 Praha 4



Valbek, spol. s r.o.
Vaňurova 505/17
460 07 Liberec 3



Vypracoval	M. KNESPOVÁ	Zak. číslo	21-L113-001	
Zodp. projektant	ING. S. RUŽIČKA	Datum	02/2025	
Tech. kontrola	ING. I. BELDA	Stupeň	PDPS	
Akce	I/16 MLADÁ BOLES LAV - MARTINOVICE		Počet formátů	8x A4
			Měřítko	1:100
			Č. přílohy	Paré
Příloha	PŘÍČNÉ ŘEZY V MÍSTĚ PODPĚR		201	

PŘÍČNÉ ŘEZY V MÍSTĚ PODPĚR

MĚŘÍTKO 1:100
1 0 1 2 3 4 5 6 7 8 9 10m