




OPĚRA 01
ŘEZ A-A 1:100
OSOU ULOŽENÍ 01

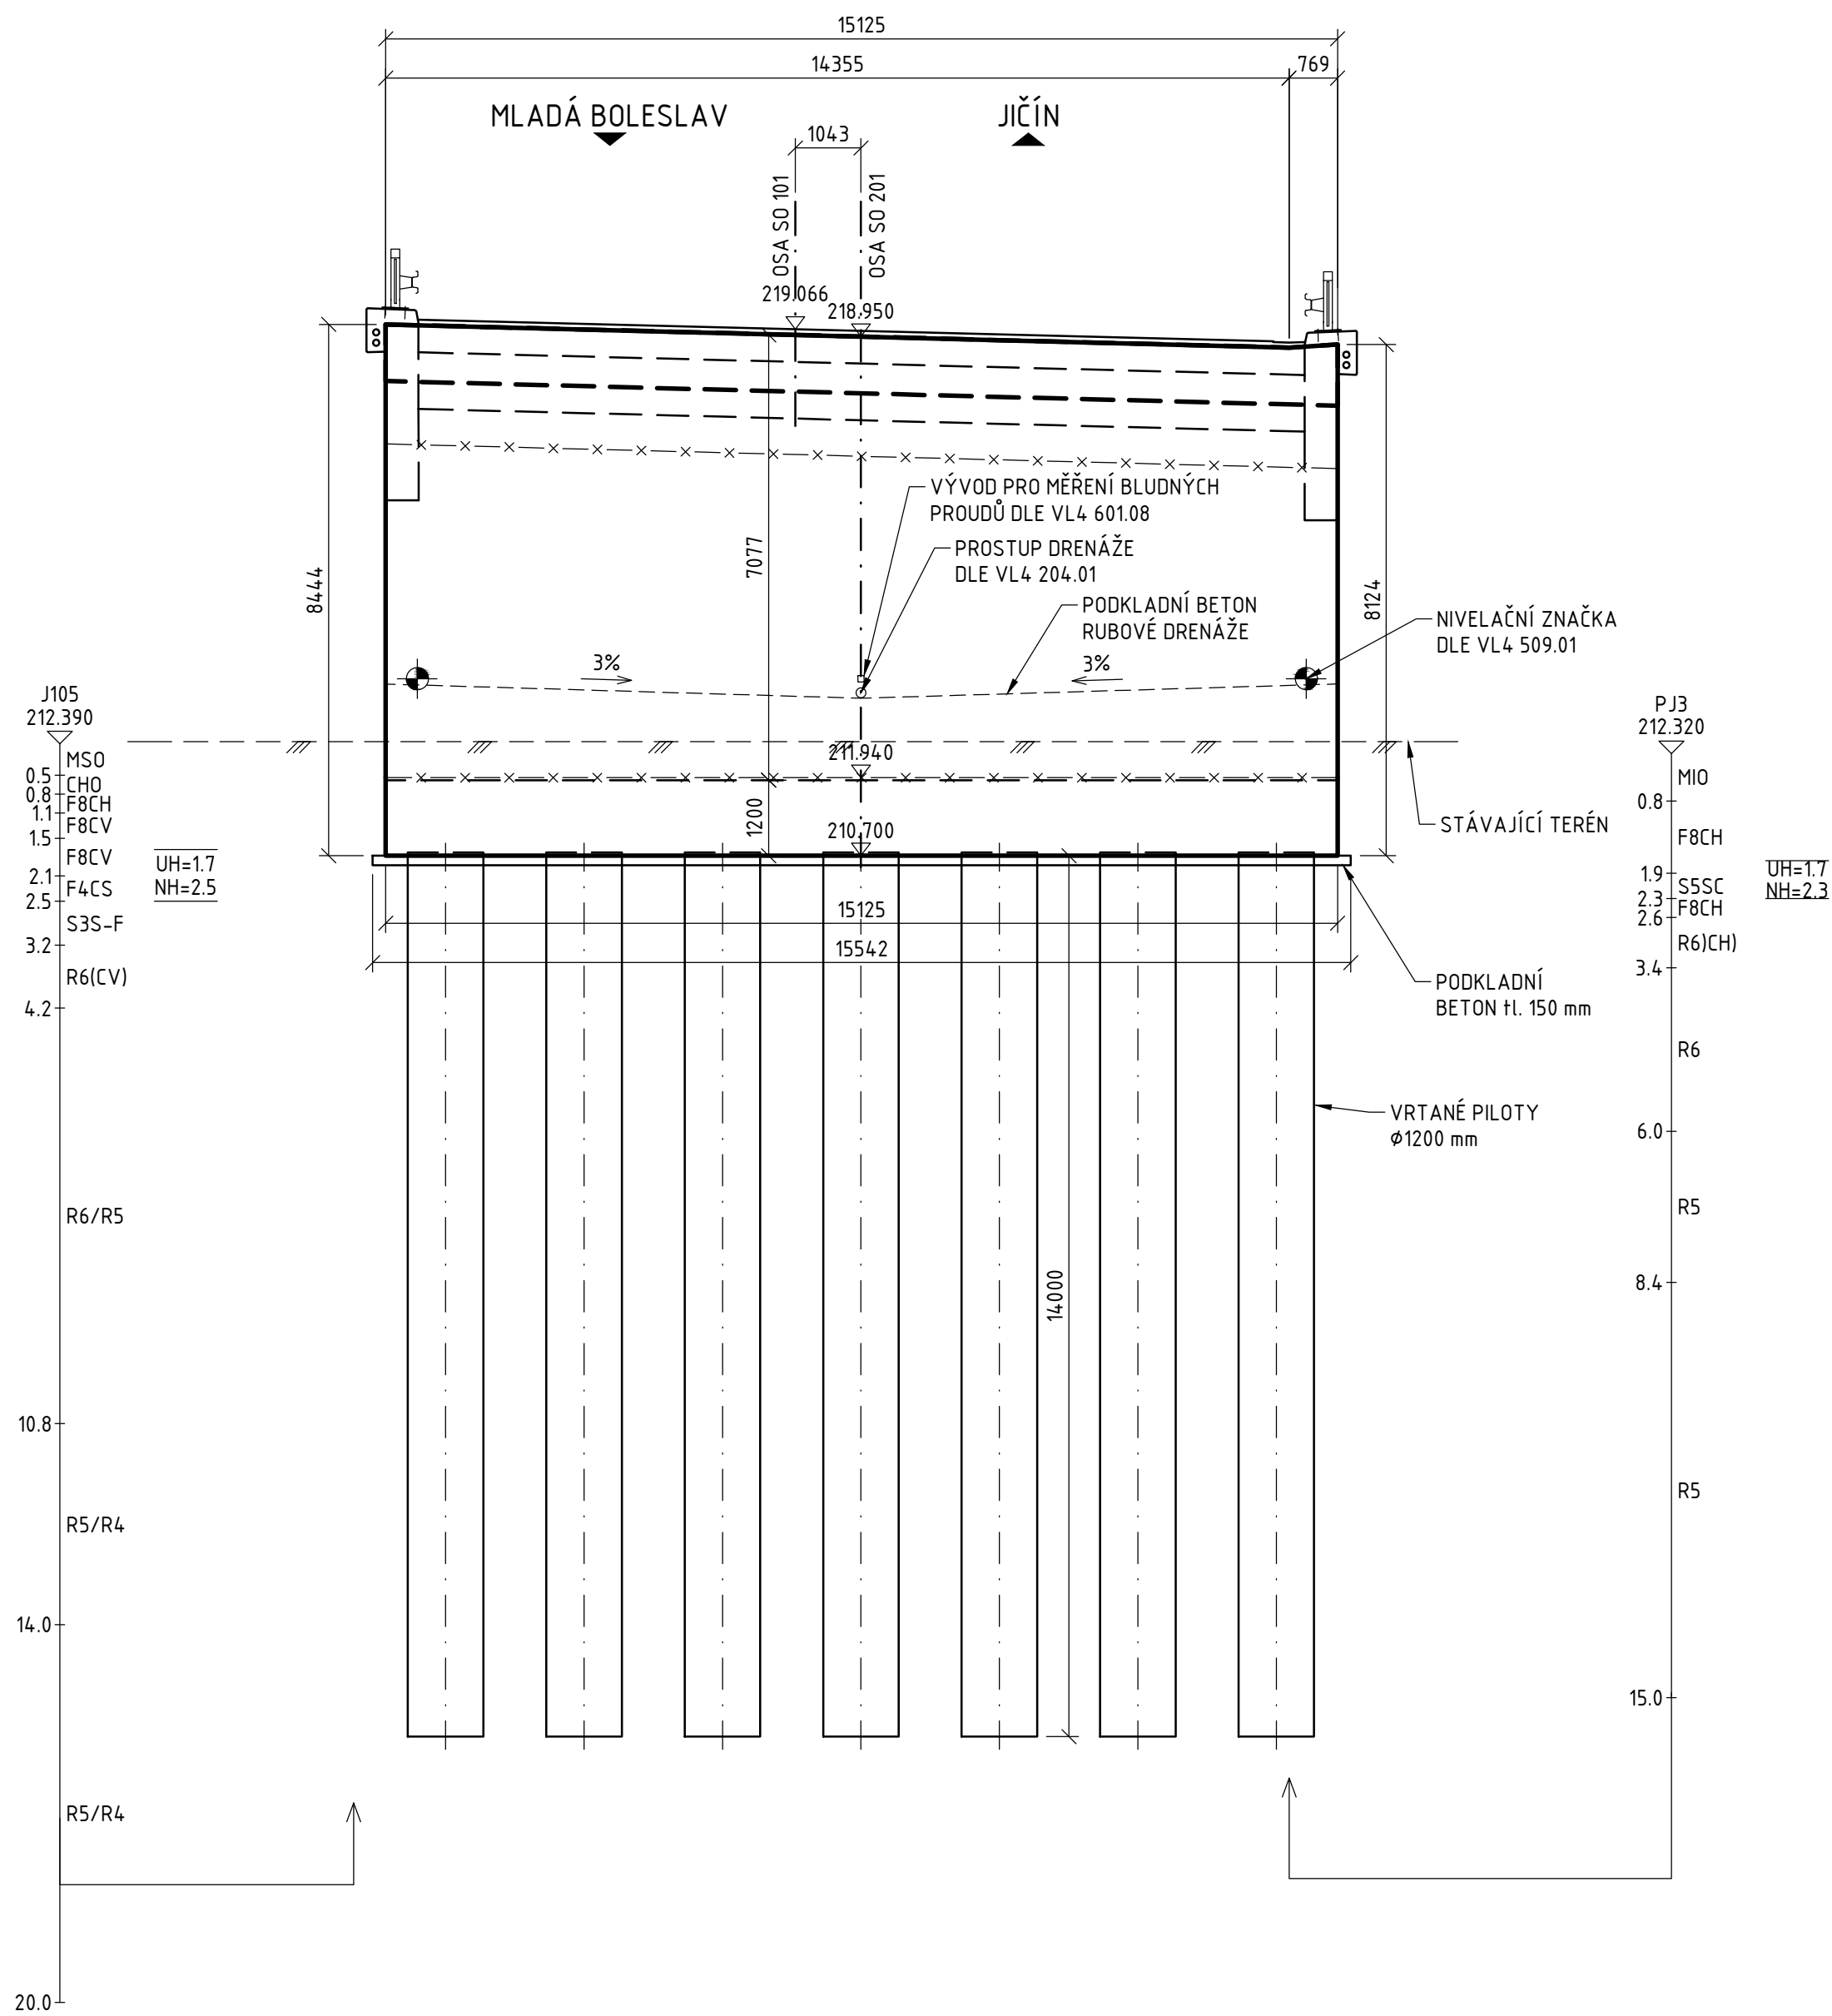


OPĚRA 01
PŮDORYS ZÁKLADU 1: 100

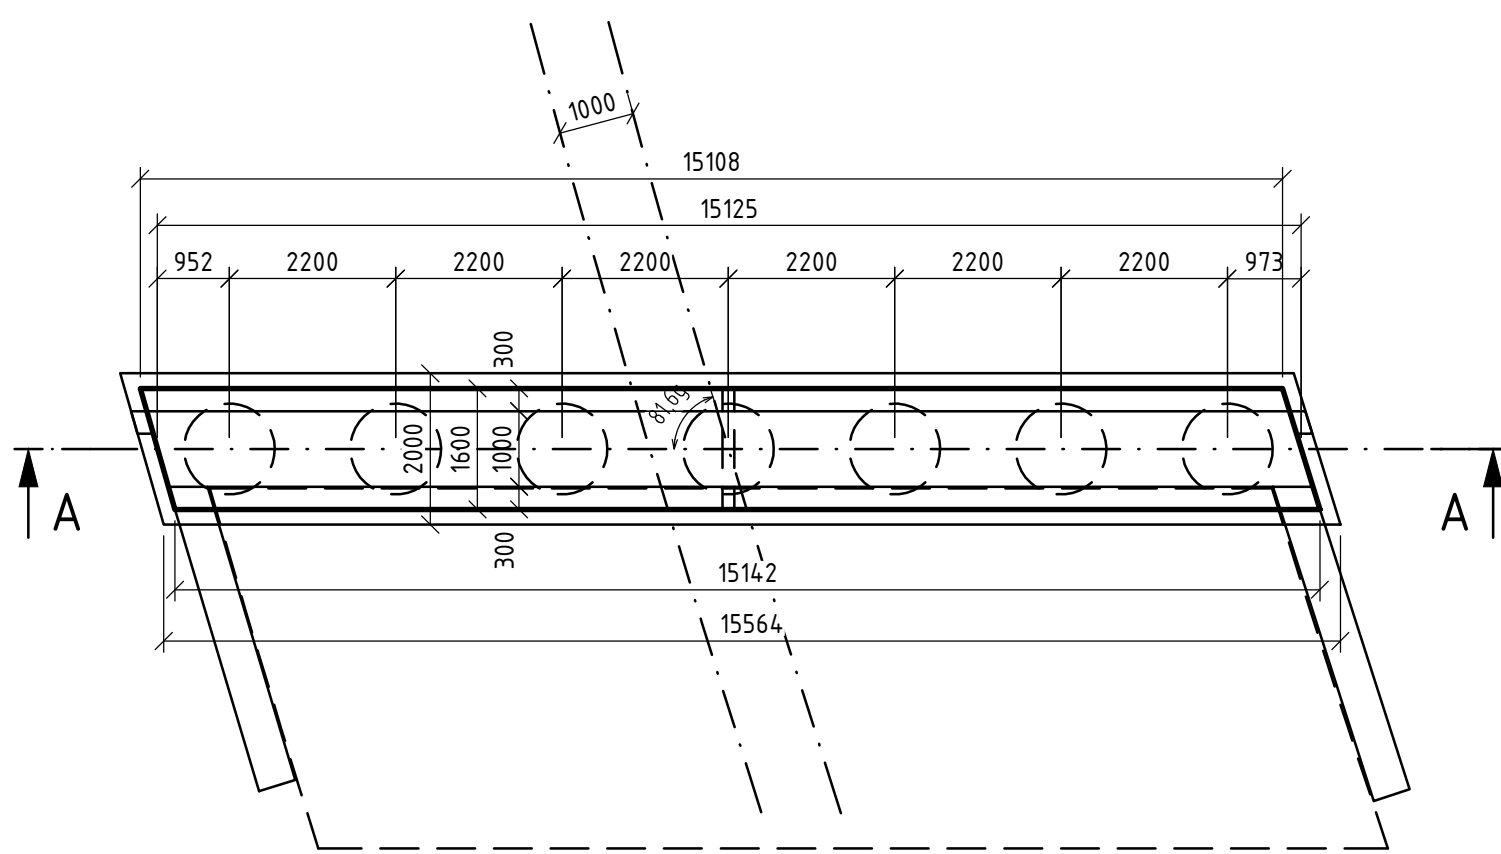

OPĚRA 03
ŘEZ B-B 1:100
OSOU ULOŽENÍ 03

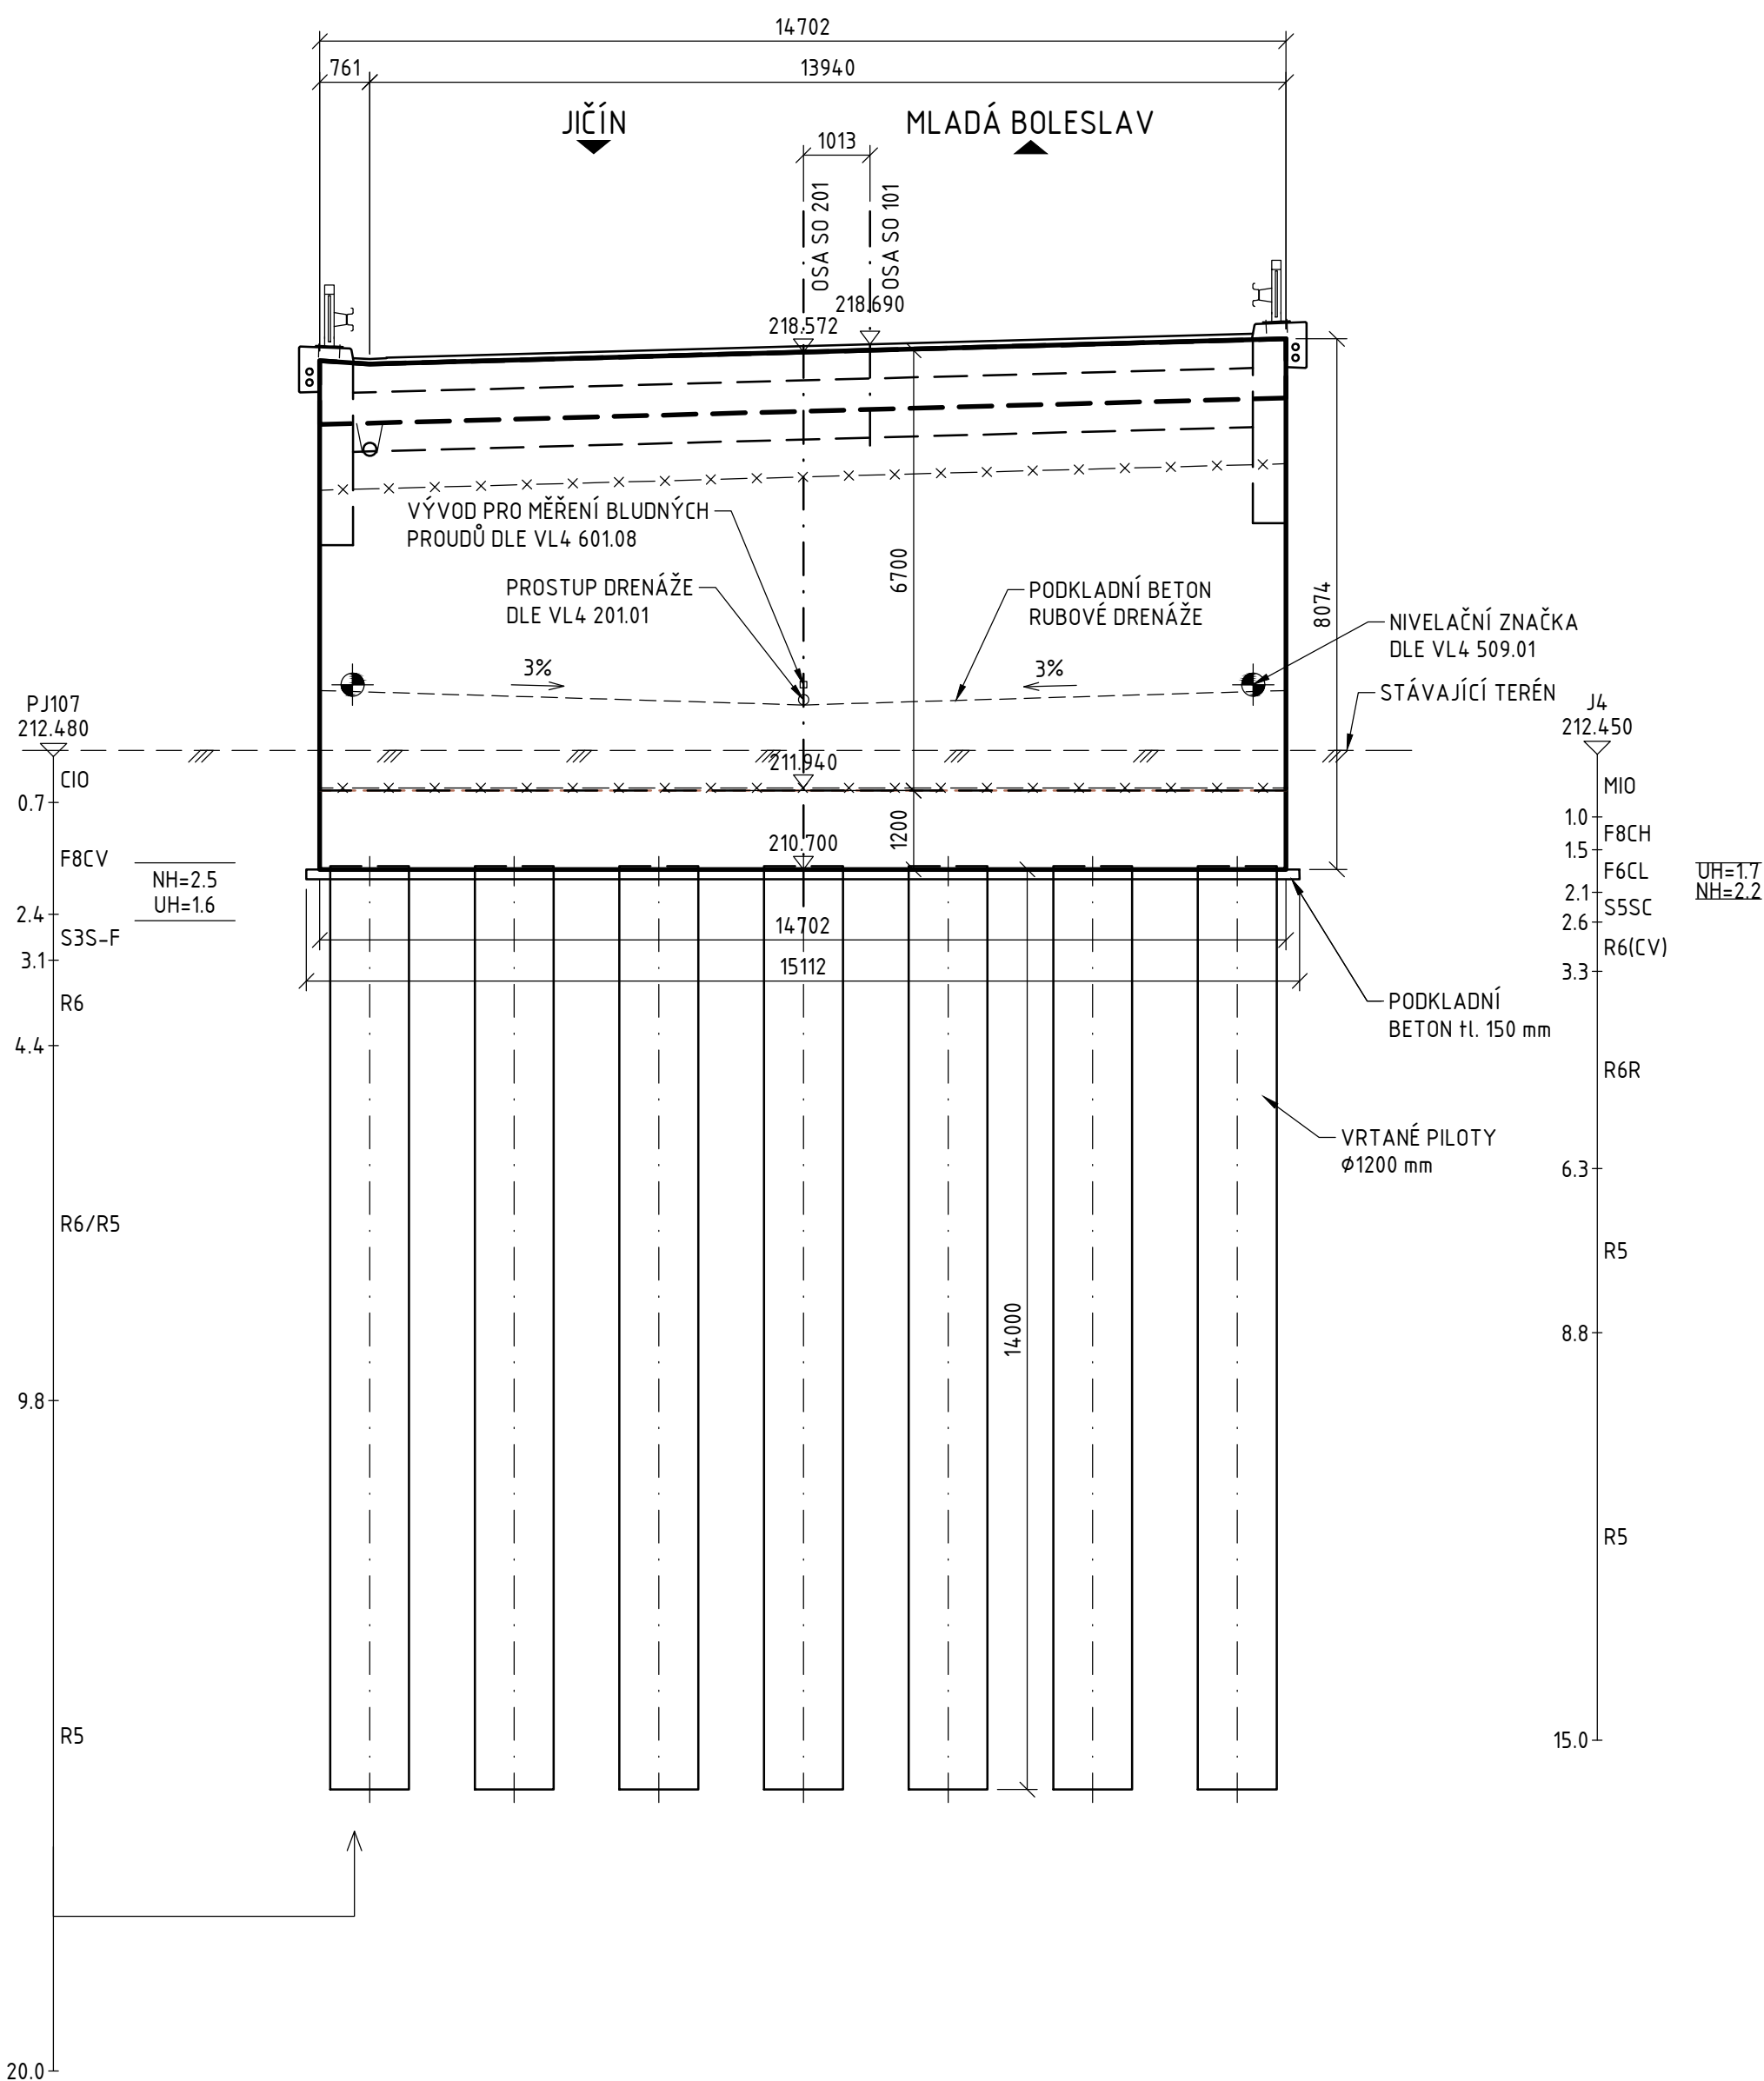

OPĚRA 03
PŮDORYS ZÁKLADU 1: 100

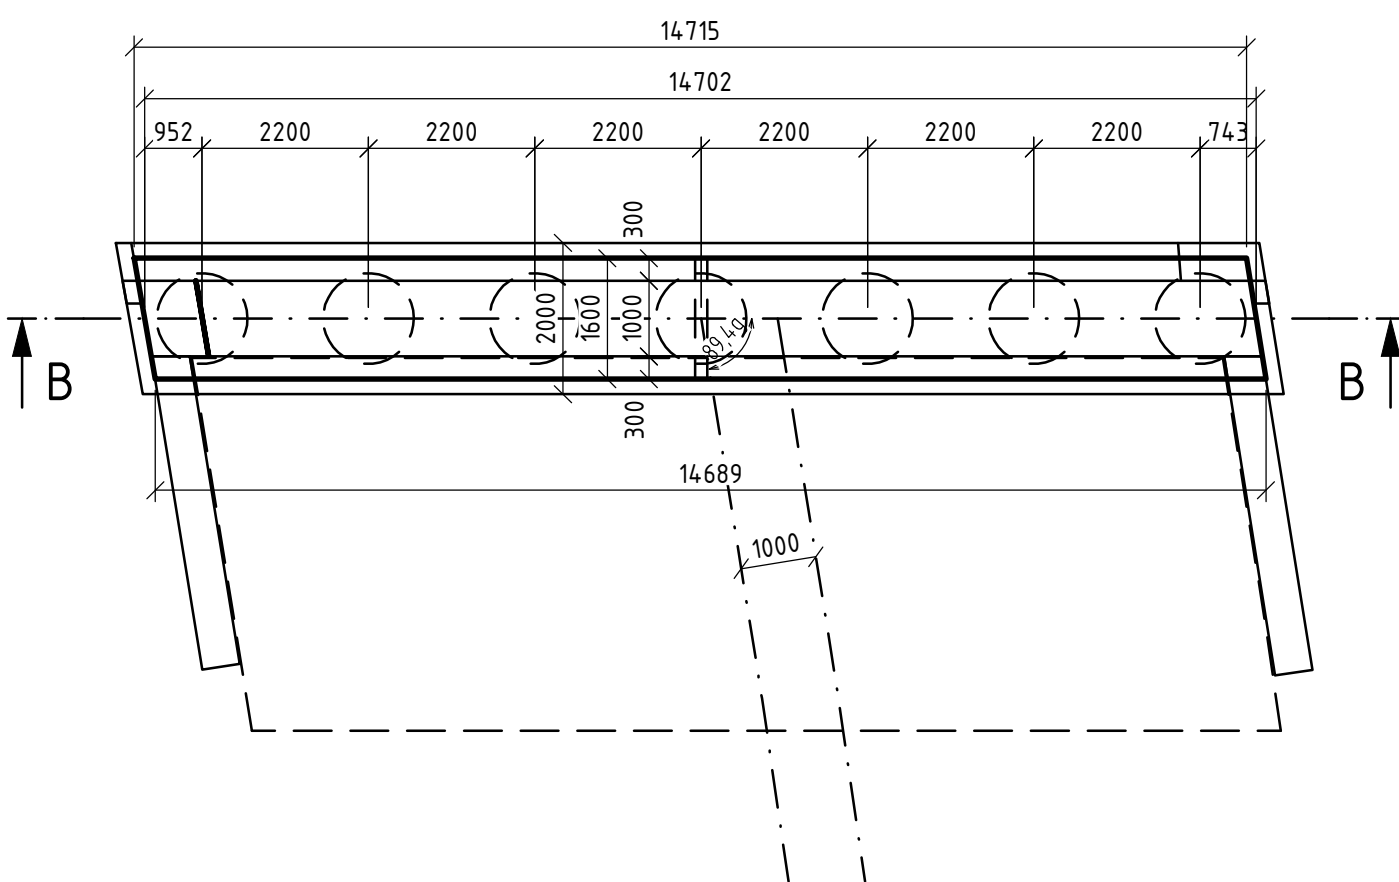

POZNÁMKY:
- NEDÍLNOU SOUČÁSTÍ VÝKRESU JSOU POZNÁMKY A SPECIFIKACE UVEDENÉ NA VÝKRESE POZNÁMEK A TECHNICKÝCH SPECIFIKACÍ

Souřadnicový systém: S-JTSK
Výškový systém: Bpv
SO 201 MOST NA I/16 PŘES MK A ZALUŽANSKOU VODOTEČ V KM 0,228

Objednatel:
ŘEDITELSTVÍ SILNIC A DÁLNIC
Ředitelství silnic a dálnic s. p.
Čerčanská 2023/12, Krč, 140 00 Praha 4

Valbek, spol. s r.o.
Vaňurova 505/17
460 07 Liberec 3

Valbek	Vypracoval	M. KNESPOVÁ	Zak. číslo	21-L113-001
	Zodp. projektant	ING. S. RUŽIČKA	Datum	02/2025
	Tech. kontrola	ING. I. BELDA	Stupeň	PDPS
	Akce	I/16 MLADÁ BOLESLAV - MARTINOVICE		Počet formátů
Zhotovitel:	Příloha		Měřítko	1:100
Valbek, spol. s r.o. Vaňurova 505/17 460 07 Liberec 3	HLUBINNÉ ZALOŽENÍ, TVAR OPĚRY 01,03		Č. přílohy	Paré
			202	

MĚŘÍTKO 1:100 1 0 1 2 3 4 5 6 7 8 9 10m