




PILÍŘ P2
ŘEZ A-A 1:100

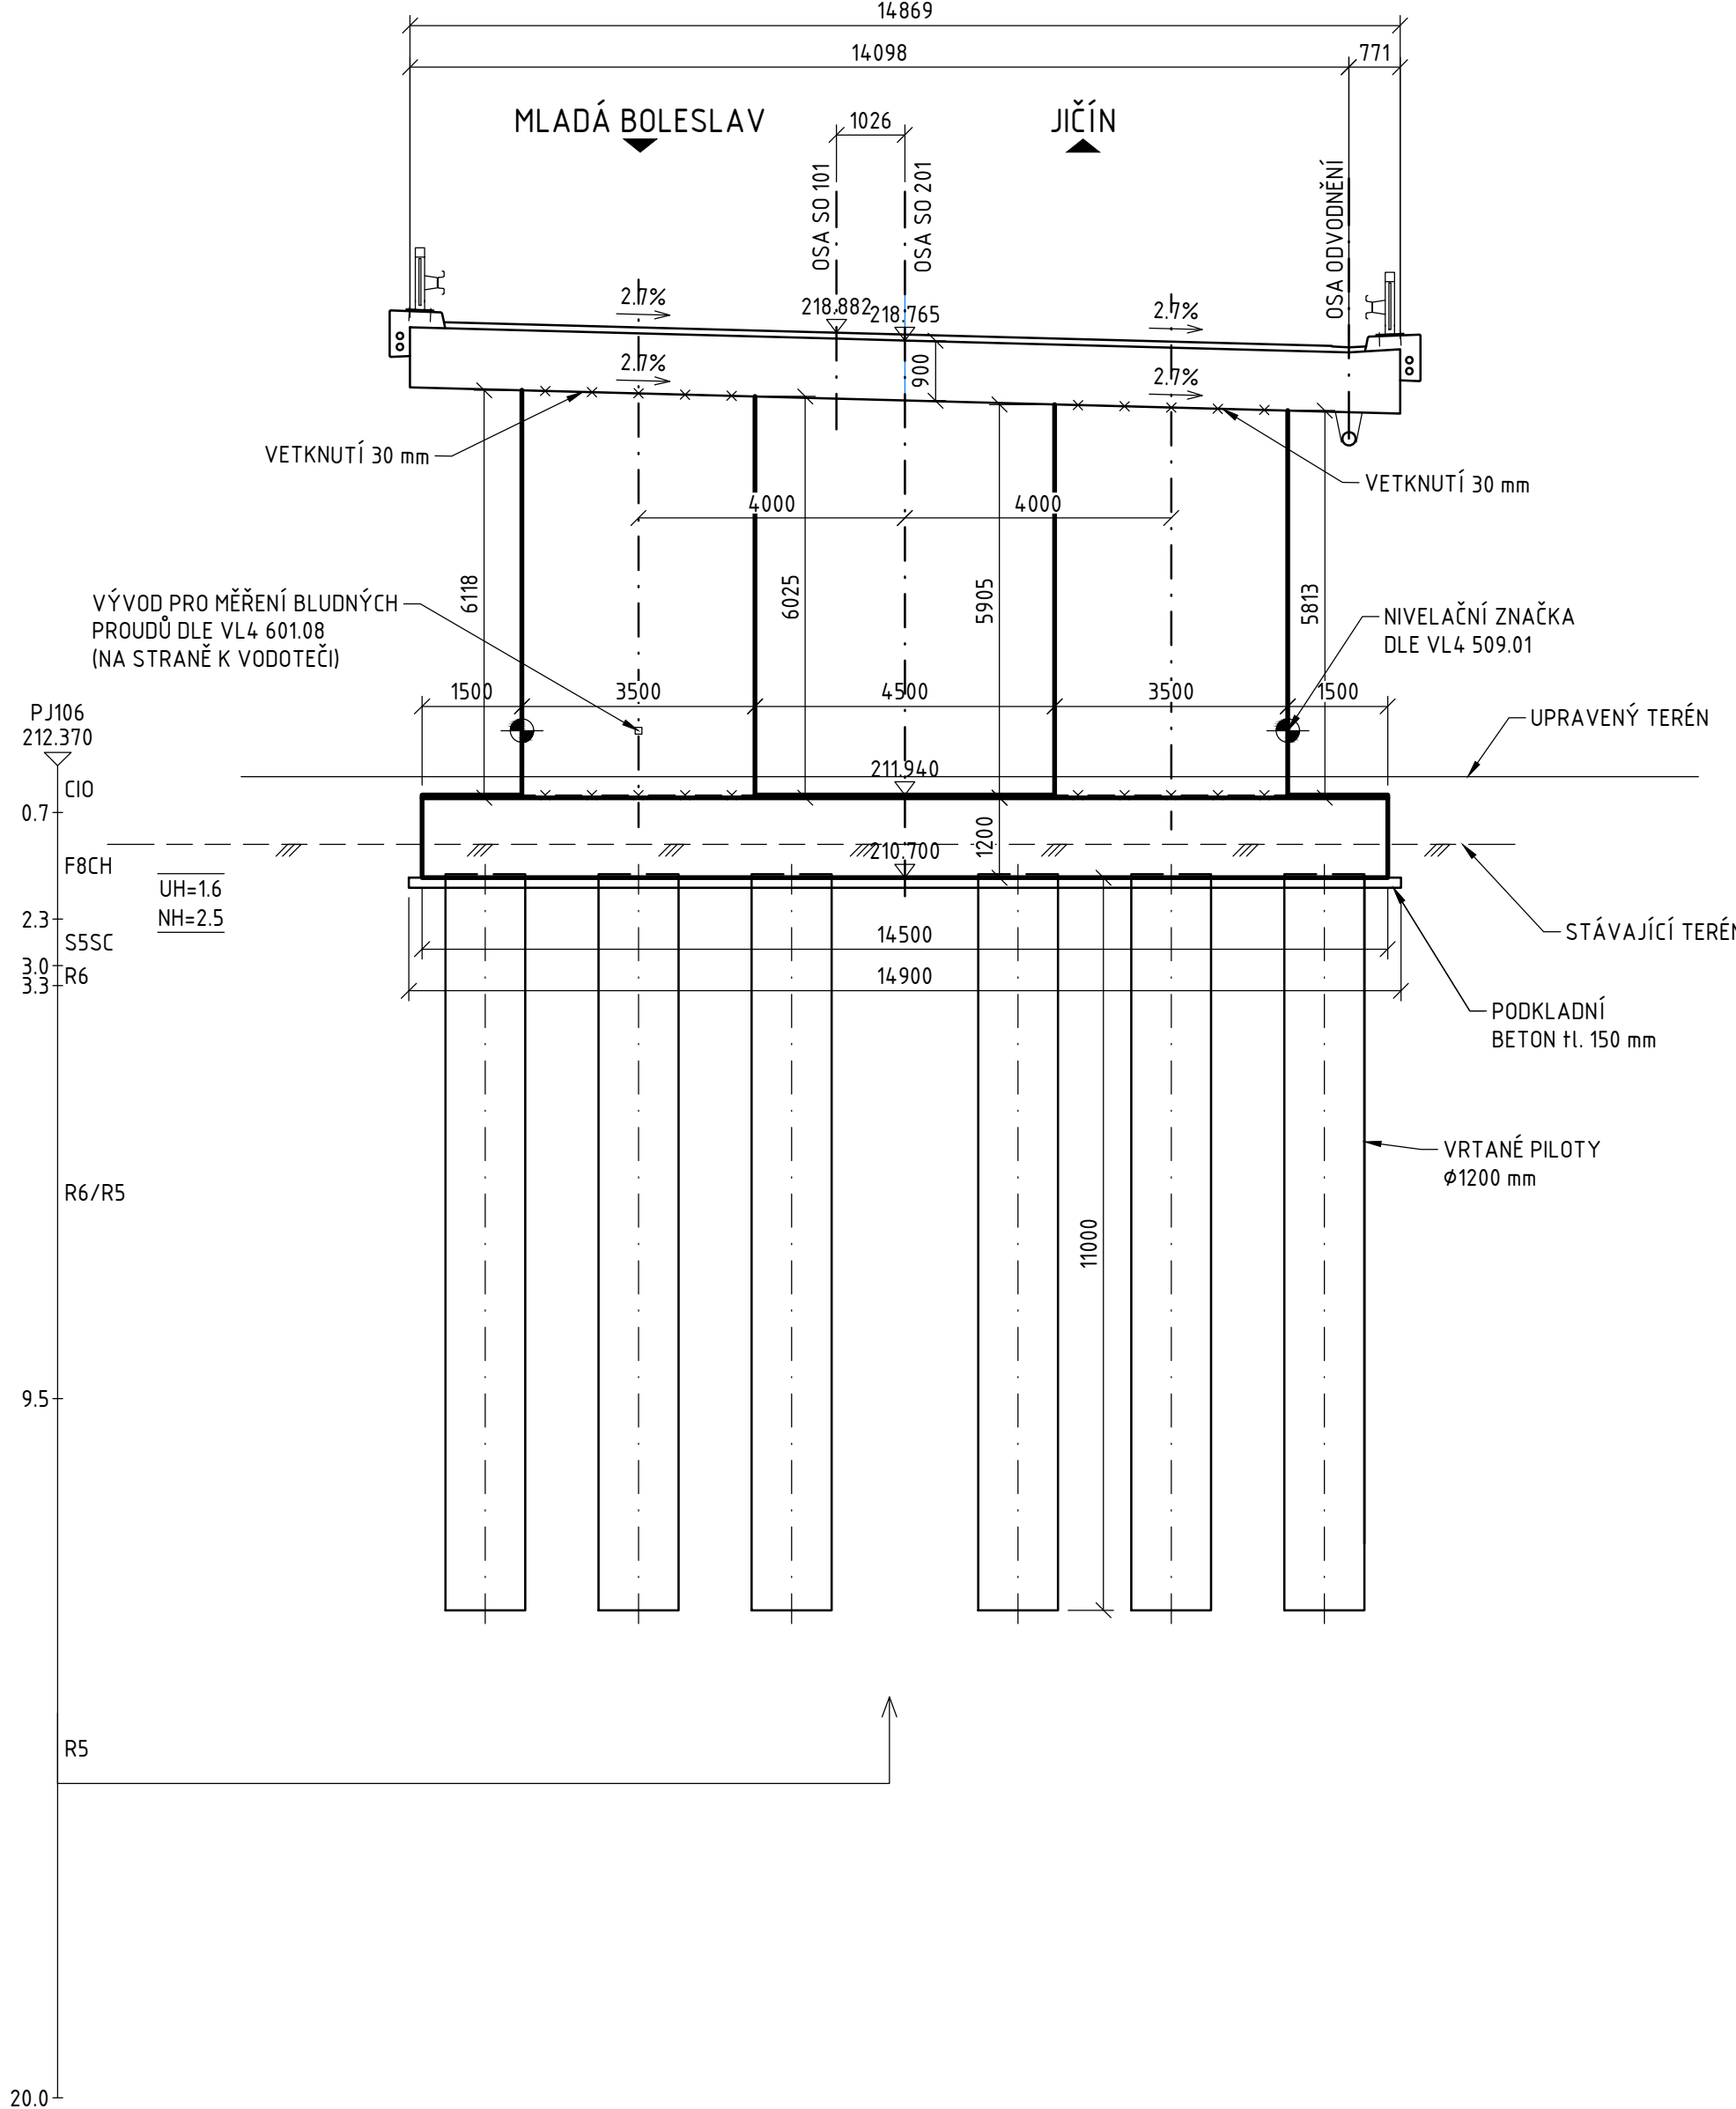


PŮDORYS ZÁKLADU 1:100

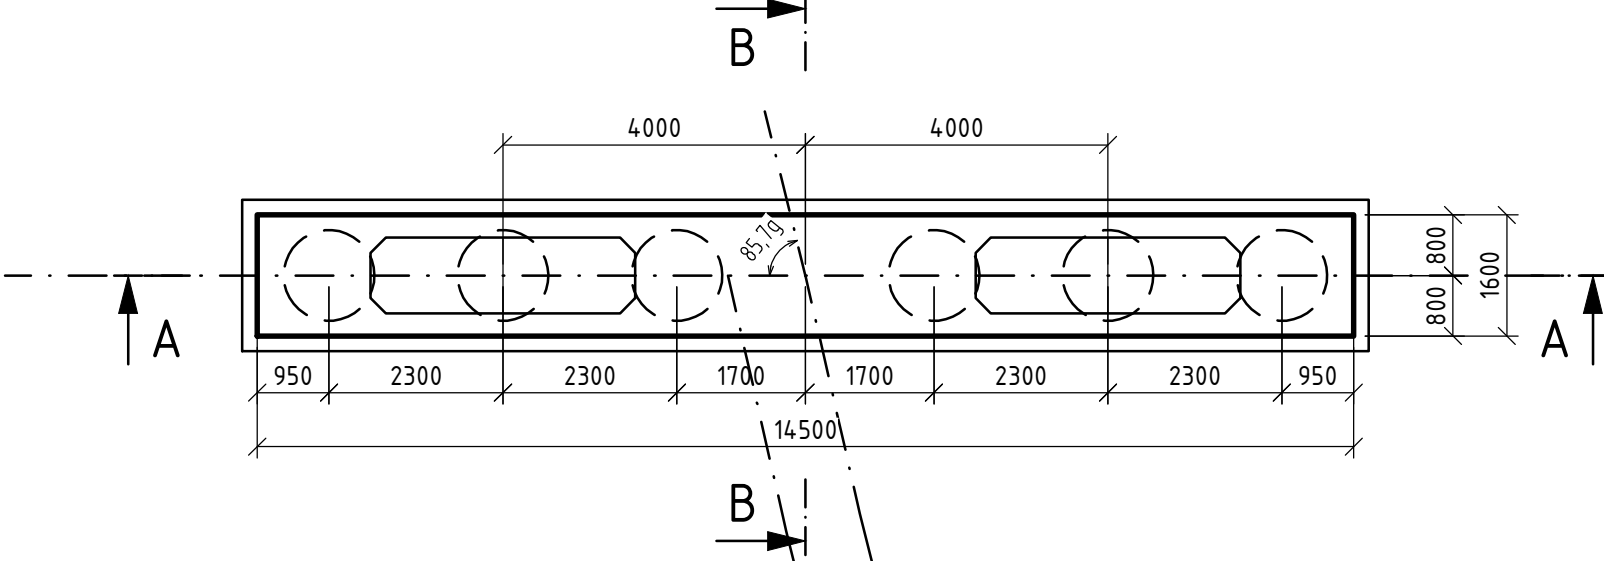

ŘEZ B-B 1 : 100

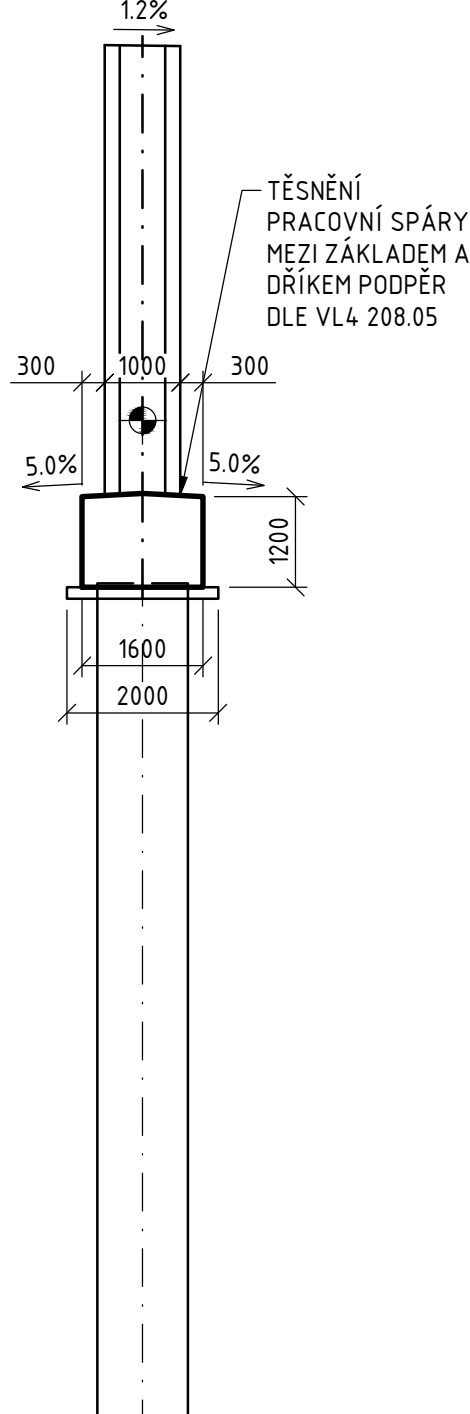

PILÍŘE
ŘEZ STOJKOU 1:50

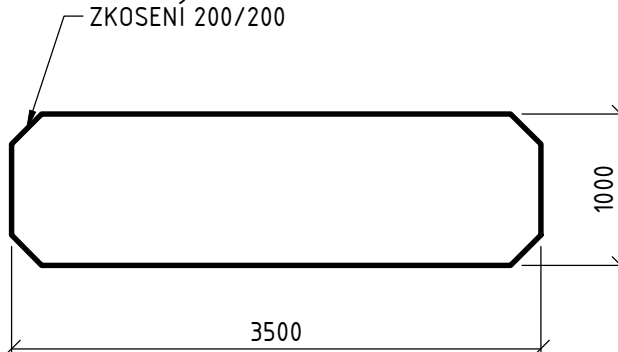

POZNÁMKY

- NEDÍLNOU SOUČÁSTÍ VÝKRESU JSOU POZNAMKY A SPECIFIKACE UVEDENÉ NA VÝKRESE POZNAMKY A TECHNICKÝCH SPECIFIKACÍ

Souřadnicový systém: S-JTSK
Výškový systém: Bpv

SO 201 MOST NA I/16 PŘES MK A ZALUŽANSKOU VODOTEČ V KM 0,228

Objednatel:



Ředitelství silnic a dálnic s. p.
Čerčanská 2023/12, Krč, 140 00 Praha 4



Valbek, spol. s r.o.
Vaňurova 505/17
460 07 Liberec 3



Vypracoval	M. KNESPOVÁ	<i>B. Hájek</i>	Dat. číslo	21-L113-001
Zodp. projektant	ING. S. RŮŽIČKA	<i>B. Hájek</i>	Zak.	02/2025
Tech. kontrola	ING. I. BELDA	<i>B. Hájek</i>	Posuň	PDPS
Akce			Počet formátů	8x A4
I/16 MLADÁ BOLESLAV - MARTINOVICE			Měřítko	1:100,50
			Č. přílohy	Paré
Příloha			203	
HLUBINNÉ ZALOŽENÍ, TVAR PILÍŘE P2				

