




PŮDORYS 1:150

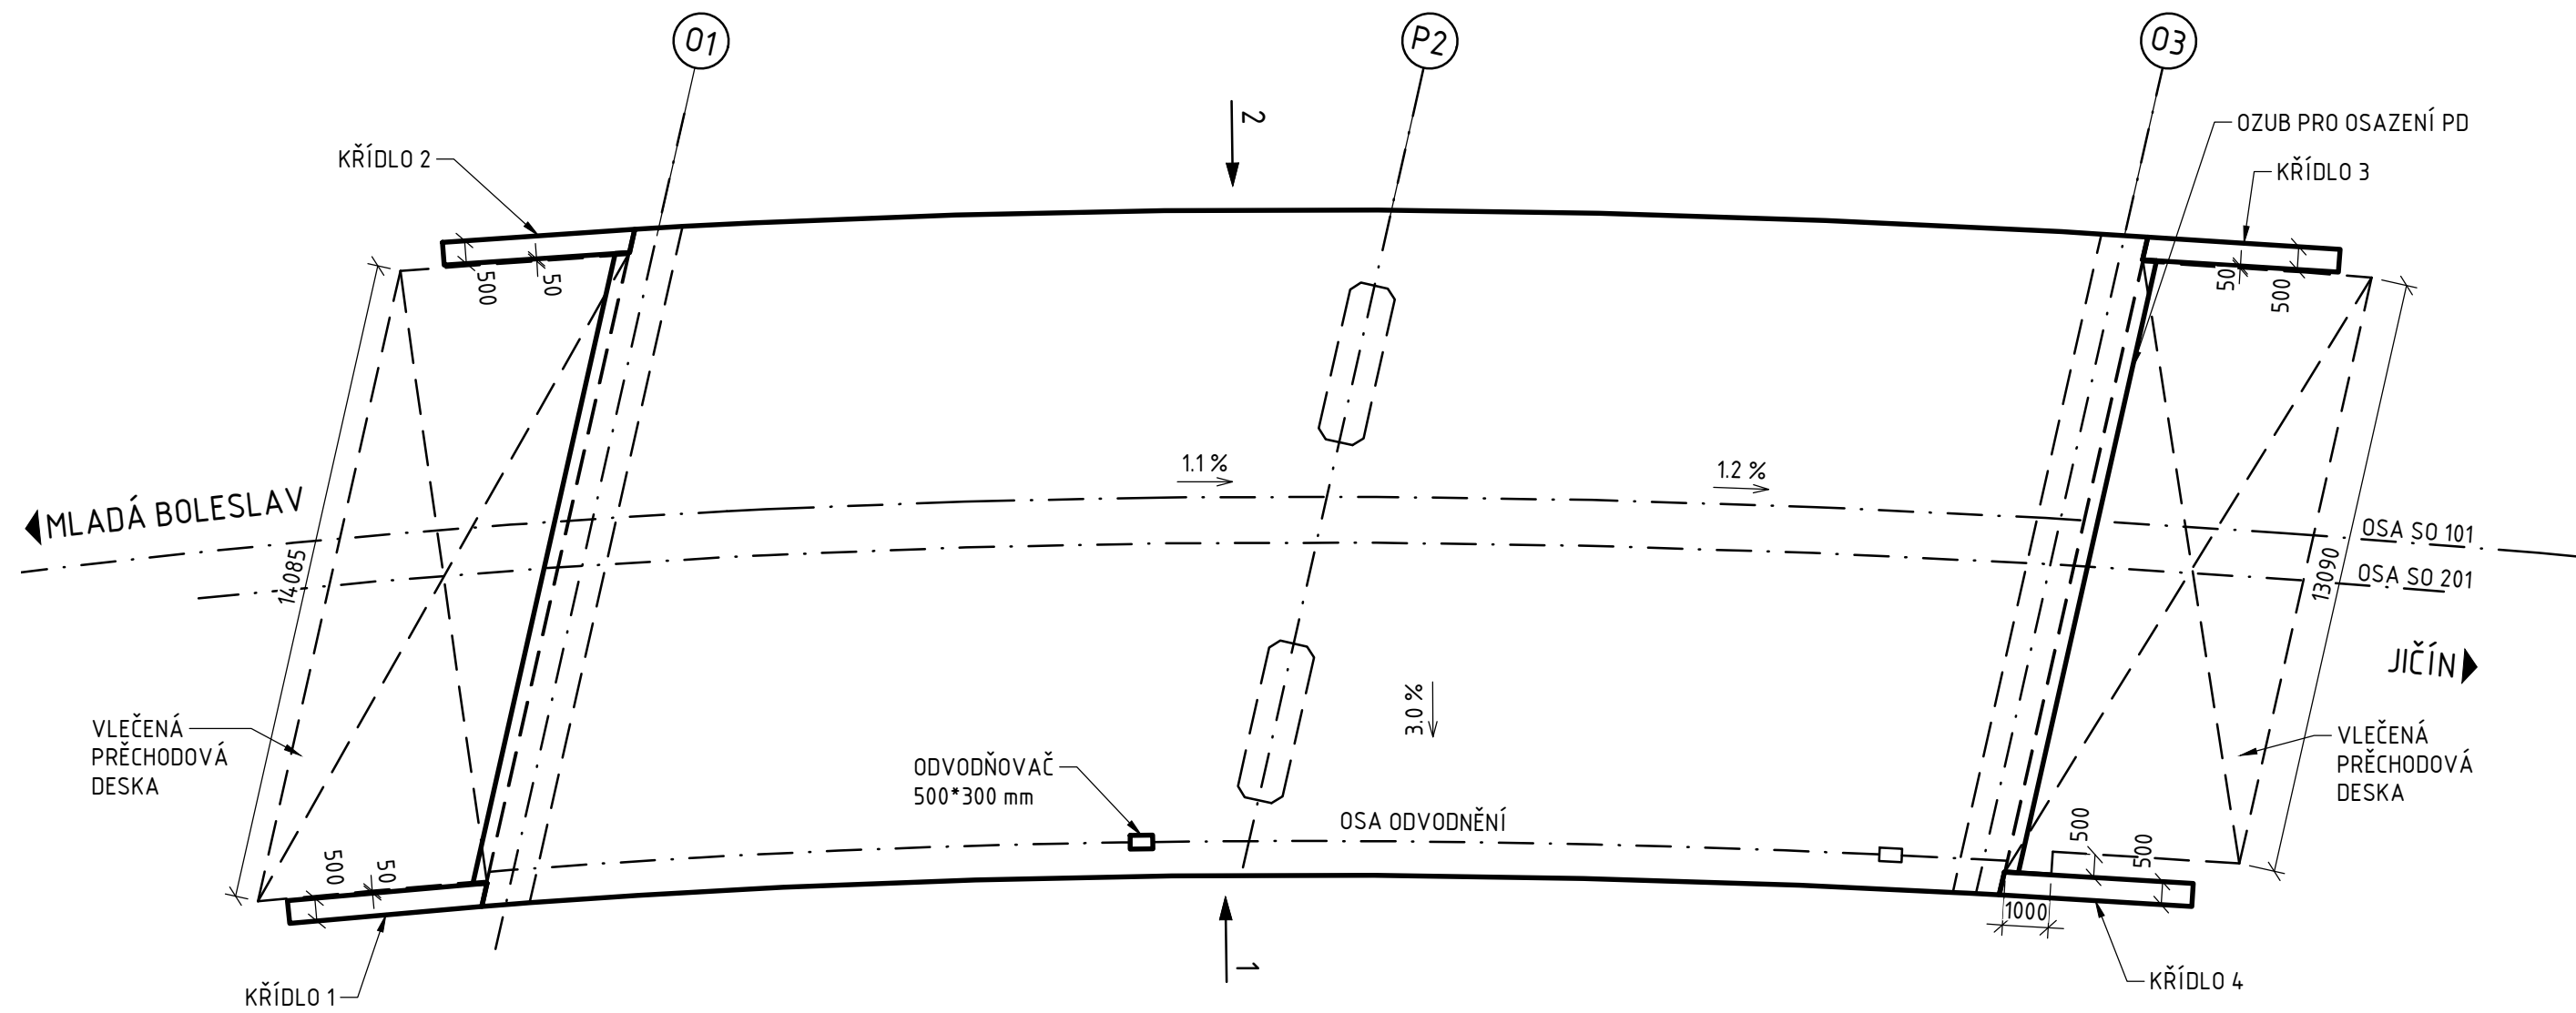


PODÉLNÝ ŘEZ 1:150
V OSE NIVELETY MOSTU

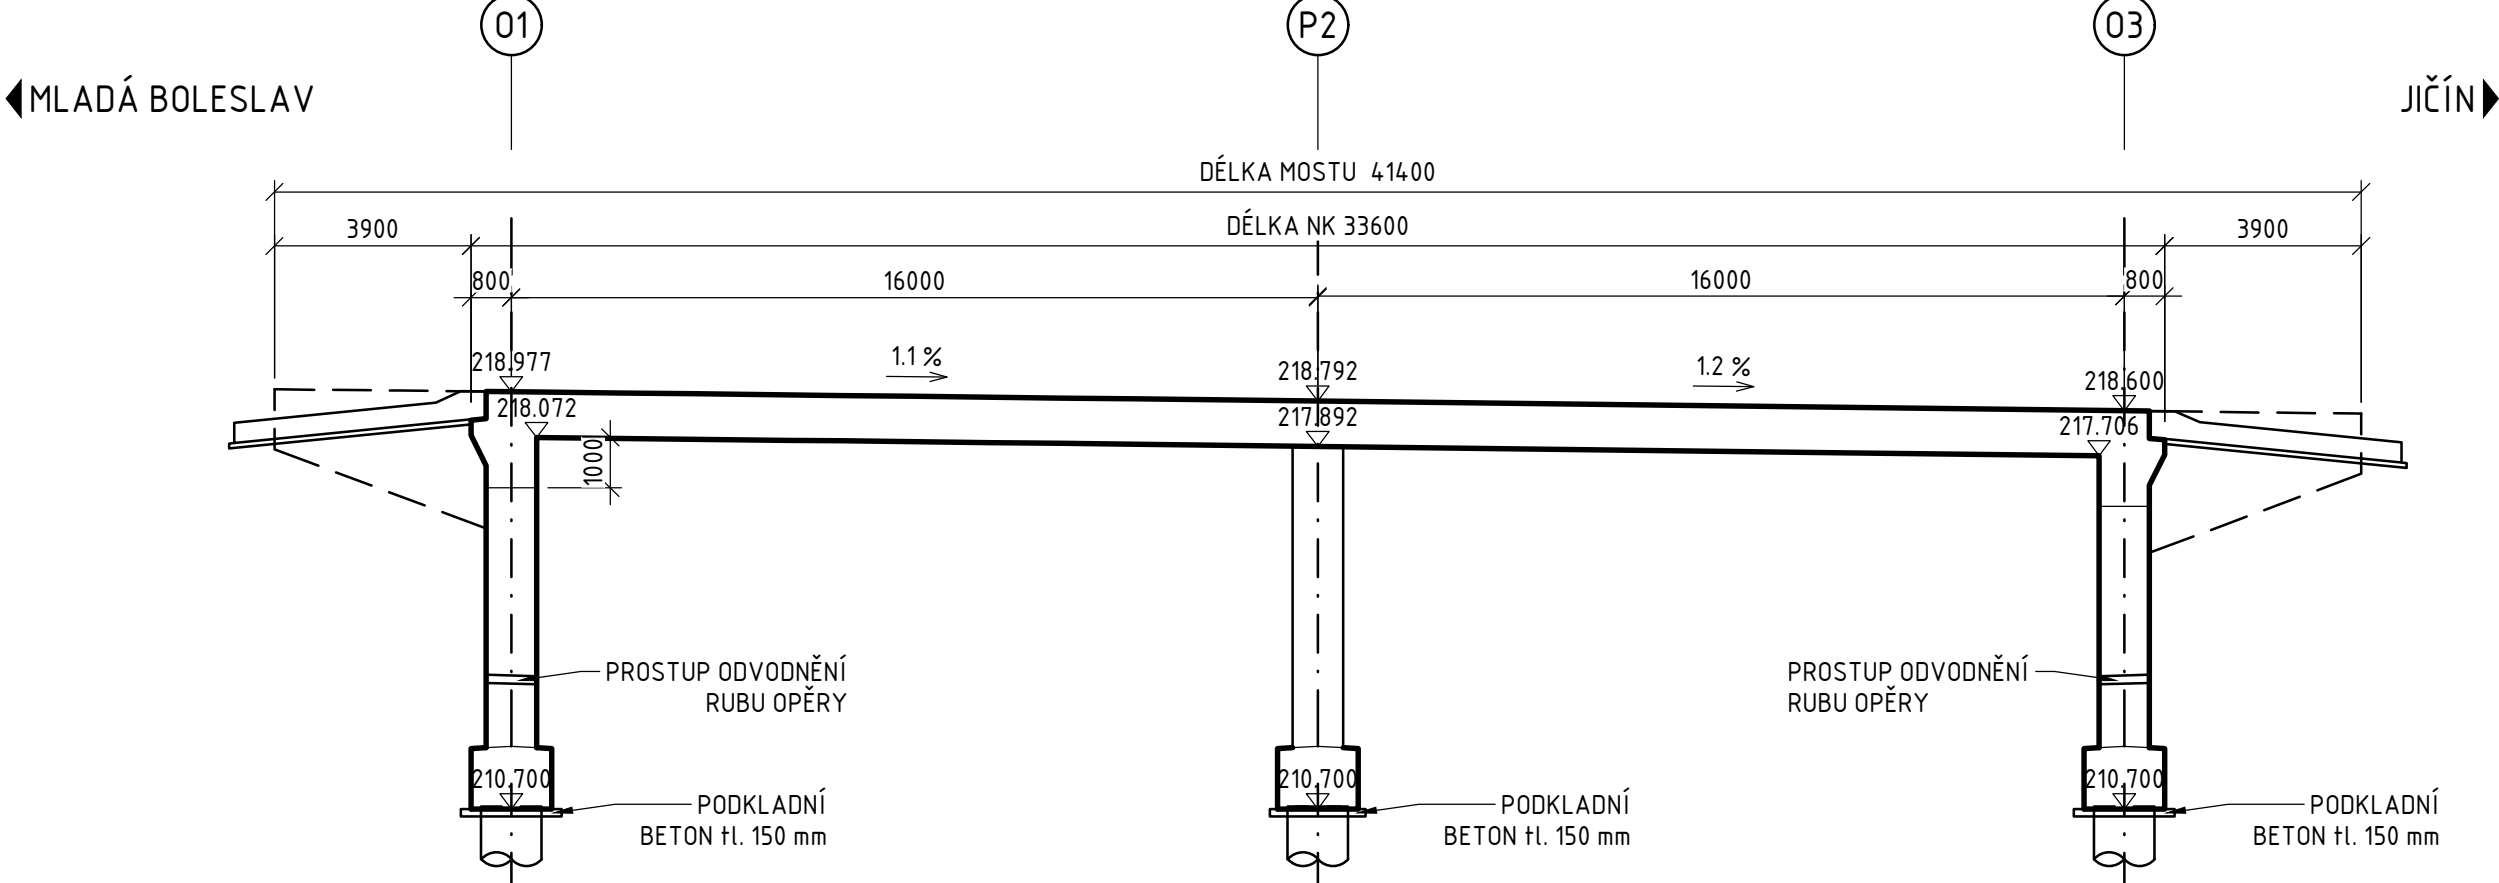


POHLED 1 1:150

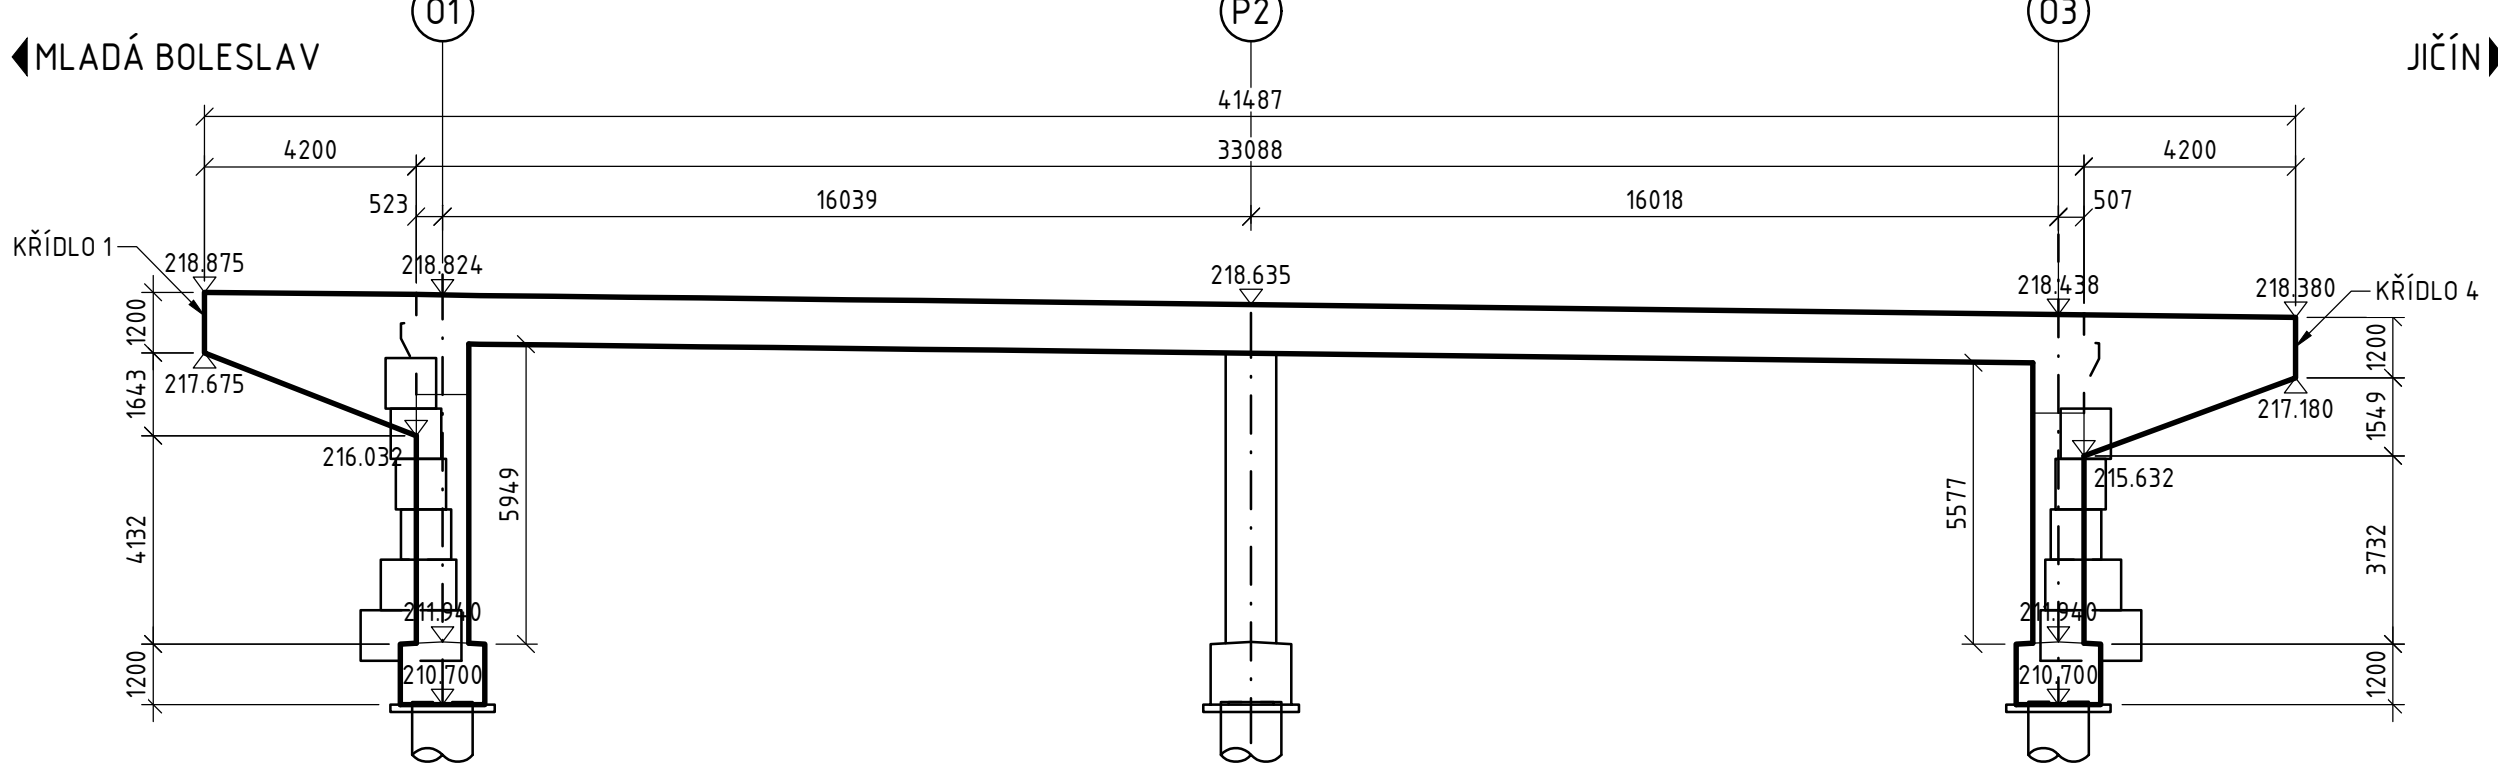

POHLED 2 1:150

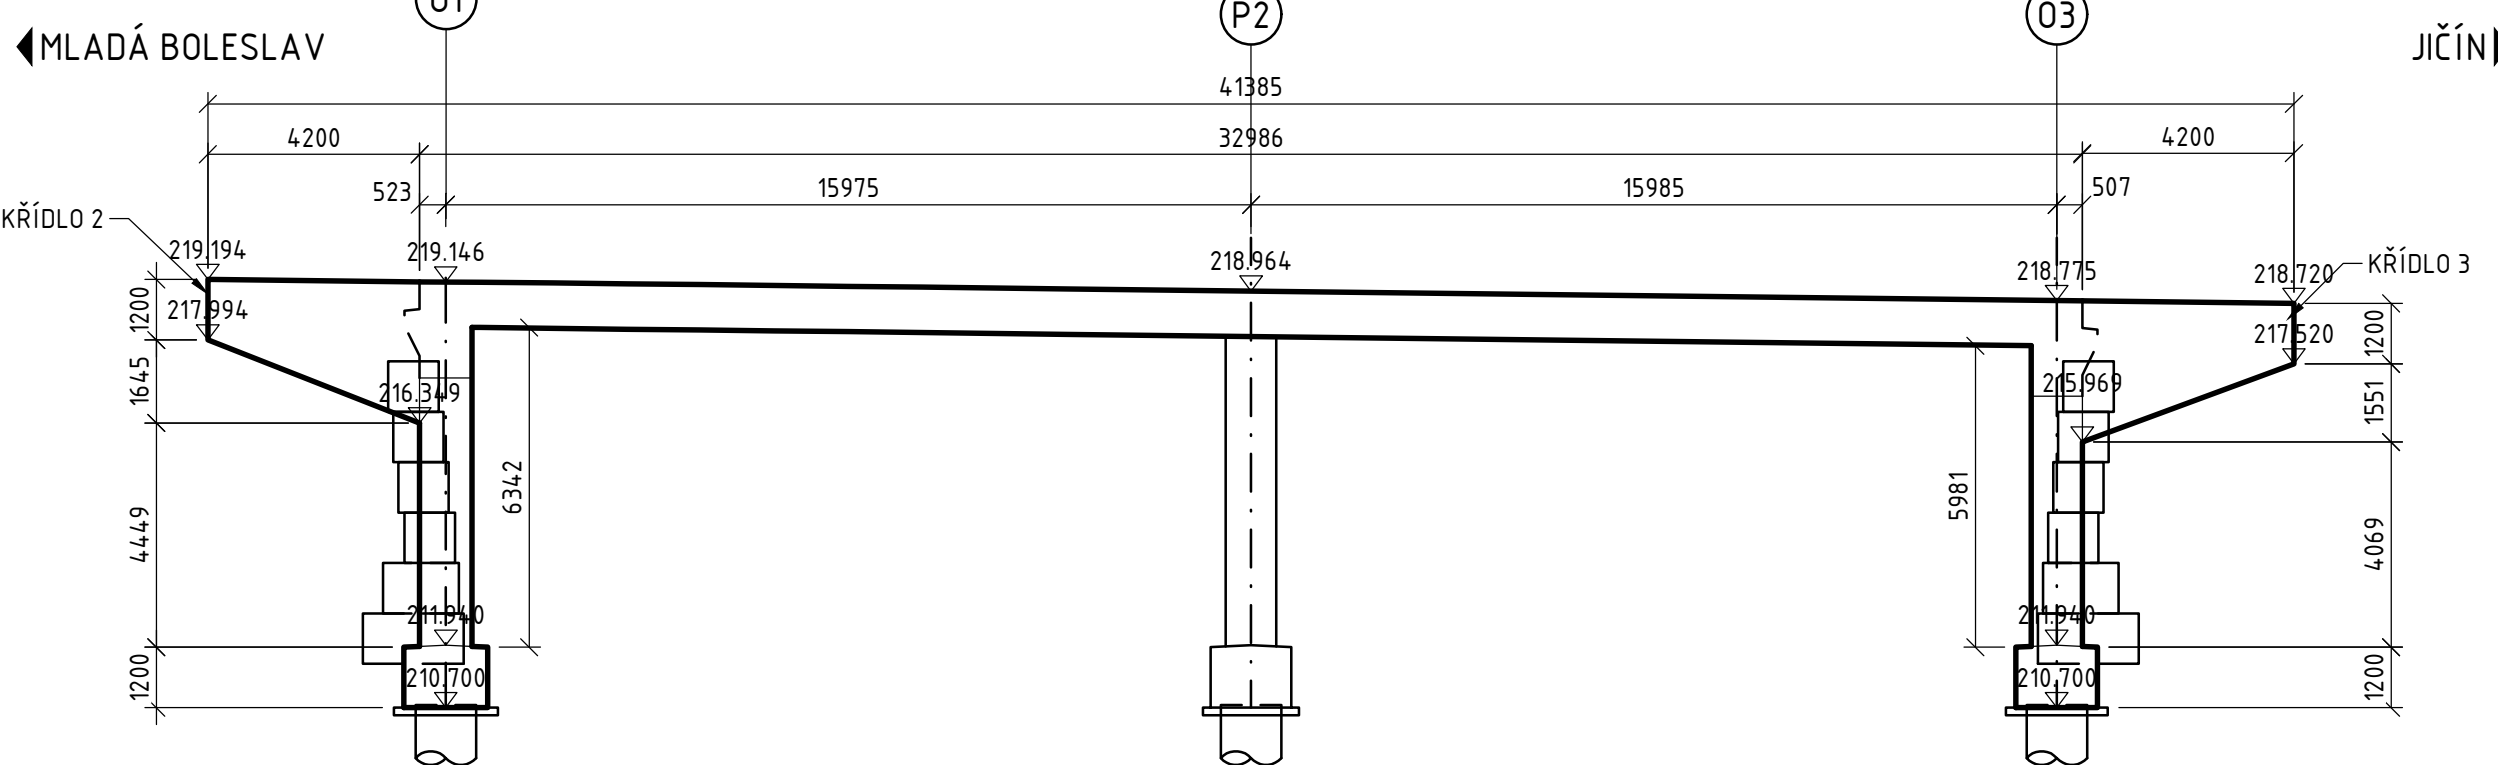

PŮDORYS VYTYČENÍ 1:150

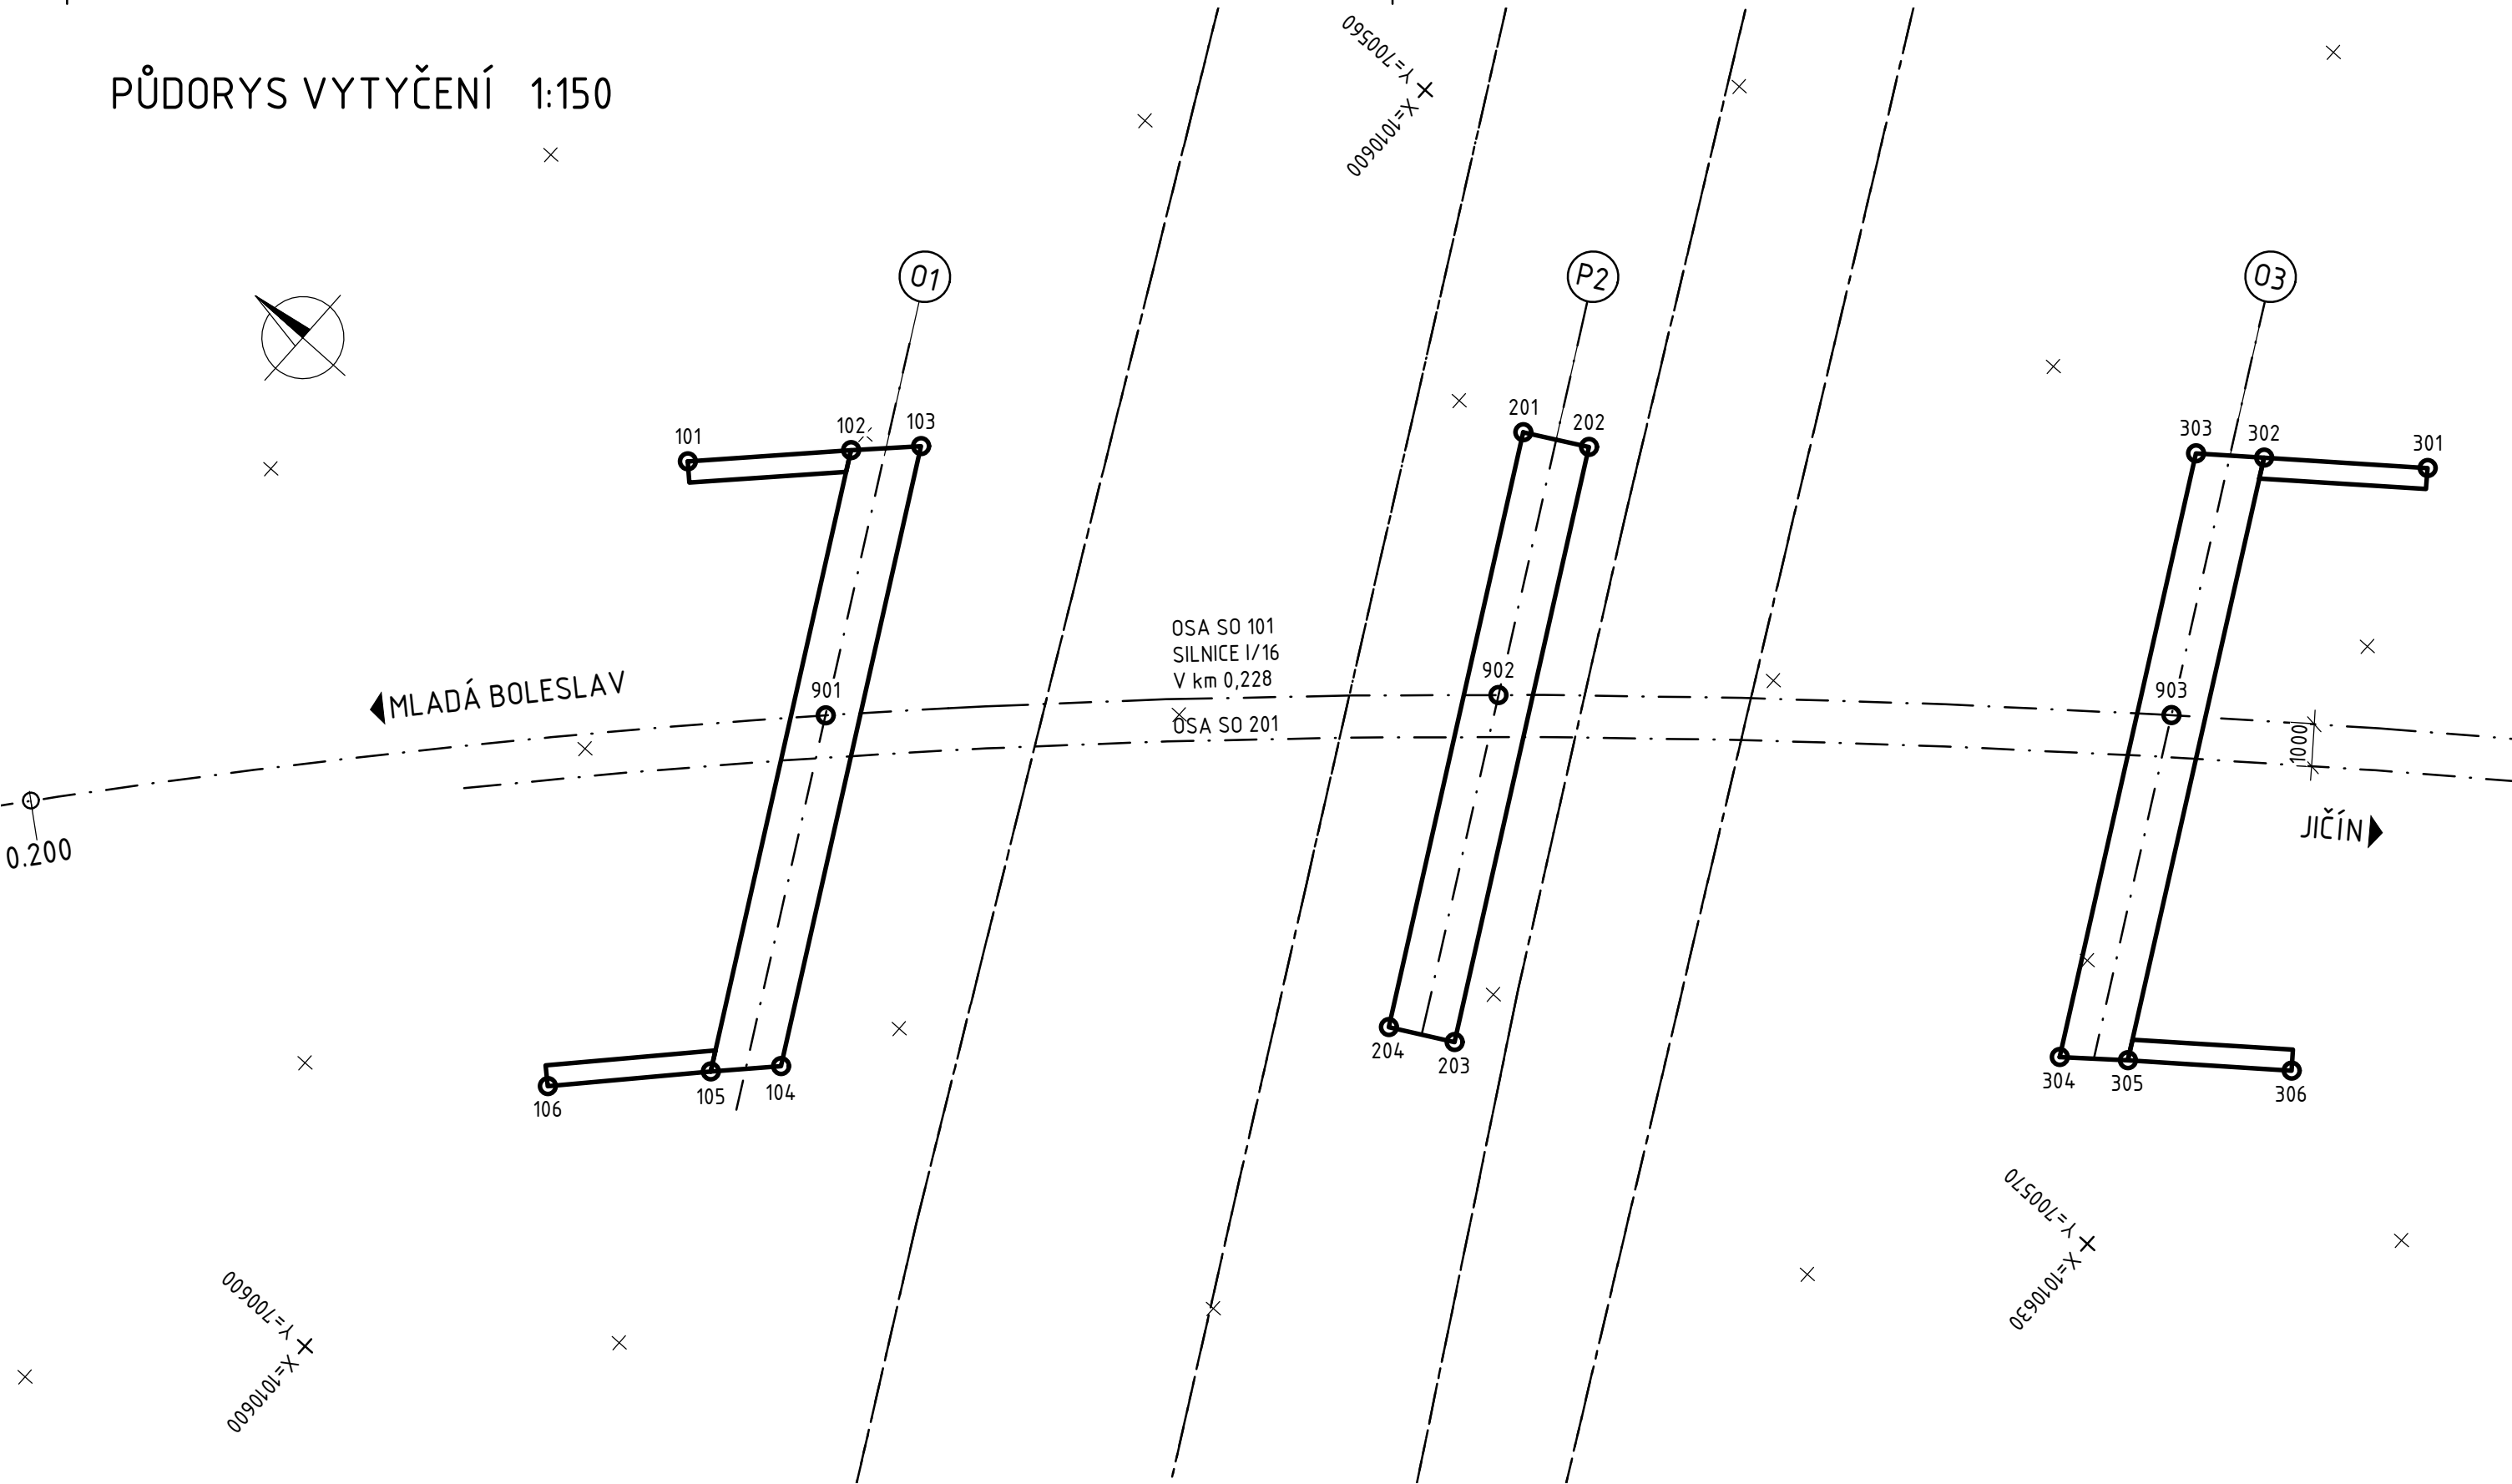

SOUŘADNICE VB

BOD	Y [m]	X [m]	Z [m]
901	700580.576	1010599.256	-
902	700569.576	1010610.873	-
903	700559.293	1010623.129	-
101	700578.252	1010592.798	219.194
102	700575.469	1010595.514	210.700
103	700574.293	1010596.692	210.700
104	700587.507	1010604.013	210.700
105	700588.715	1010602.853	210.700
106	700591.549	1010600.194	218.875
201	700564.519	1010607.157	210.700
202	700563.744	1010608.557	210.700
203	700576.427	1010615.584	210.700
204	700577.203	1010614.185	210.700
301	700550.853	1010623.765	218.720
302	700553.257	1010620.699	210.700
303	700554.256	1010619.424	210.700
304	700567.127	1010626.555	210.700
305	700566.105	1010627.818	210.700
306	700563.699	1010630.881	218.380

LEGENDA



TRVALÝ ZÁBOR
DOČASNÝ ZÁBOR nad 1 rok
DOČASNÝ ZÁBOR do 1 roku
MOST LEŽÍ UVNITŘ TRVALÉHO I DOČASNÉHO ZÁBORU

POZNÁMKY:

- VYTYČOVACÍ ODCHYLKY: VIZ PŘÍLOHA E.4.5.1 - GVS - SEZNAM SOUŘADNIC
- NEDÍLNOU SOUČÁSTÍ VÝKRESU JSOU POZNÁMKY A SPECIFIKACE UVEDENÉ NA VÝKRESE POZNÁMEK A TECHNICKÝCH SPECIFIKACÍ

PODÉLNÝ ŘEZ PŘECHODOVOU DESKOU 1:50

VYKRESLENA PŘECHODOVÁ DESKA OPĚRY 01, PŘECHODOVÁ DESKA OPĚRY 03 ŘEŠENA ODBOBNĚ

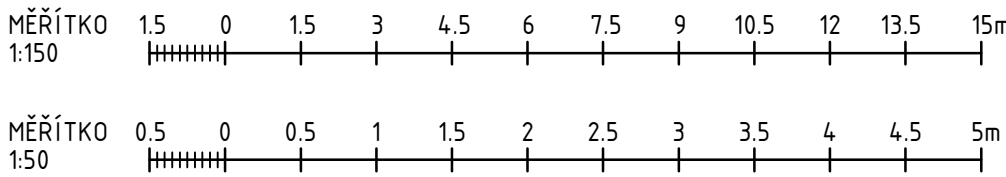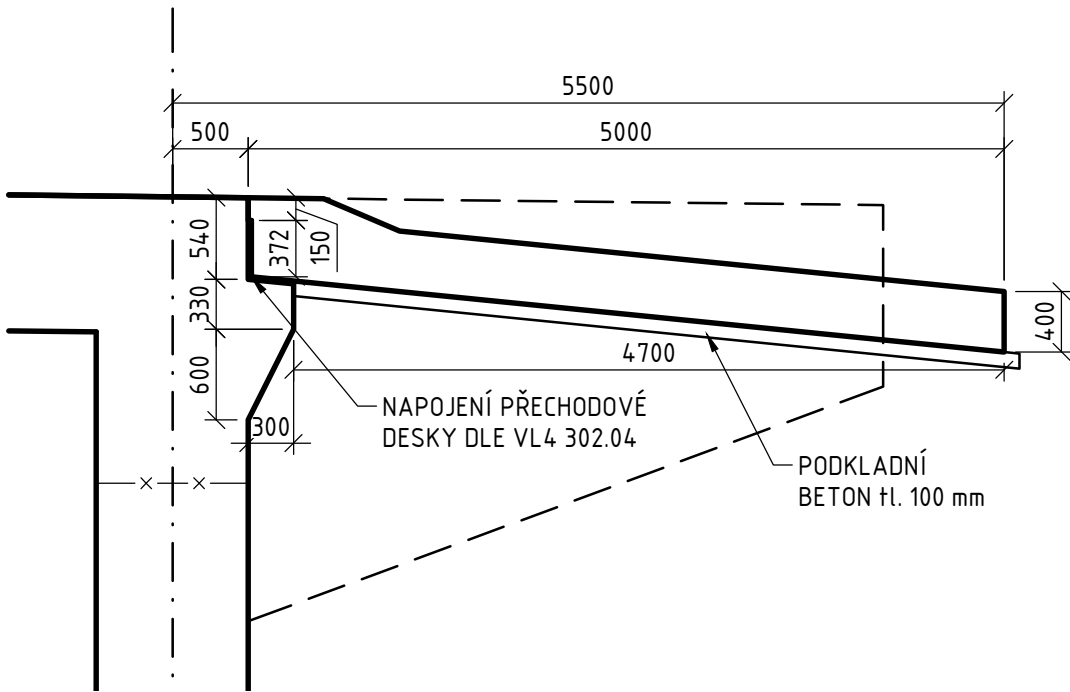

Souřadnicový systém: S-JTSK
Výškový systém: Bpv

SO 201 MOST NA I/16 PŘES MK A ZALUŽANSKOU VODOTEČ V KM 0,228

Objednatel:

Ředitelství silnic a dálnic
Čerčanská 2023/12, Krč, 140 00 Praha 4

Valbek, spol. s r.o.
Vaňurova 505/17
460 07 Liberec 3

Zhotovitel:
Valbek, spol. s r.o.
Vaňurova 505/17
460 07 Liberec 3

Vypracoval	M. KNESPOVÁ	Zak. číslo	21-L113-001
Zodp. projektant	ING. S. RUŽIČKA	Datum	02/2025
Tech. kontrola	ING. I. BELDA	Stupeň	PDPS
Akce	I/16 MLADÁ BOLESLAV - MARTINOVICE	Počet formátů	8x A4
		Měřítko	1:150, 50
		Č. přílohy	Paré

204