

PŮDORYS 1:150



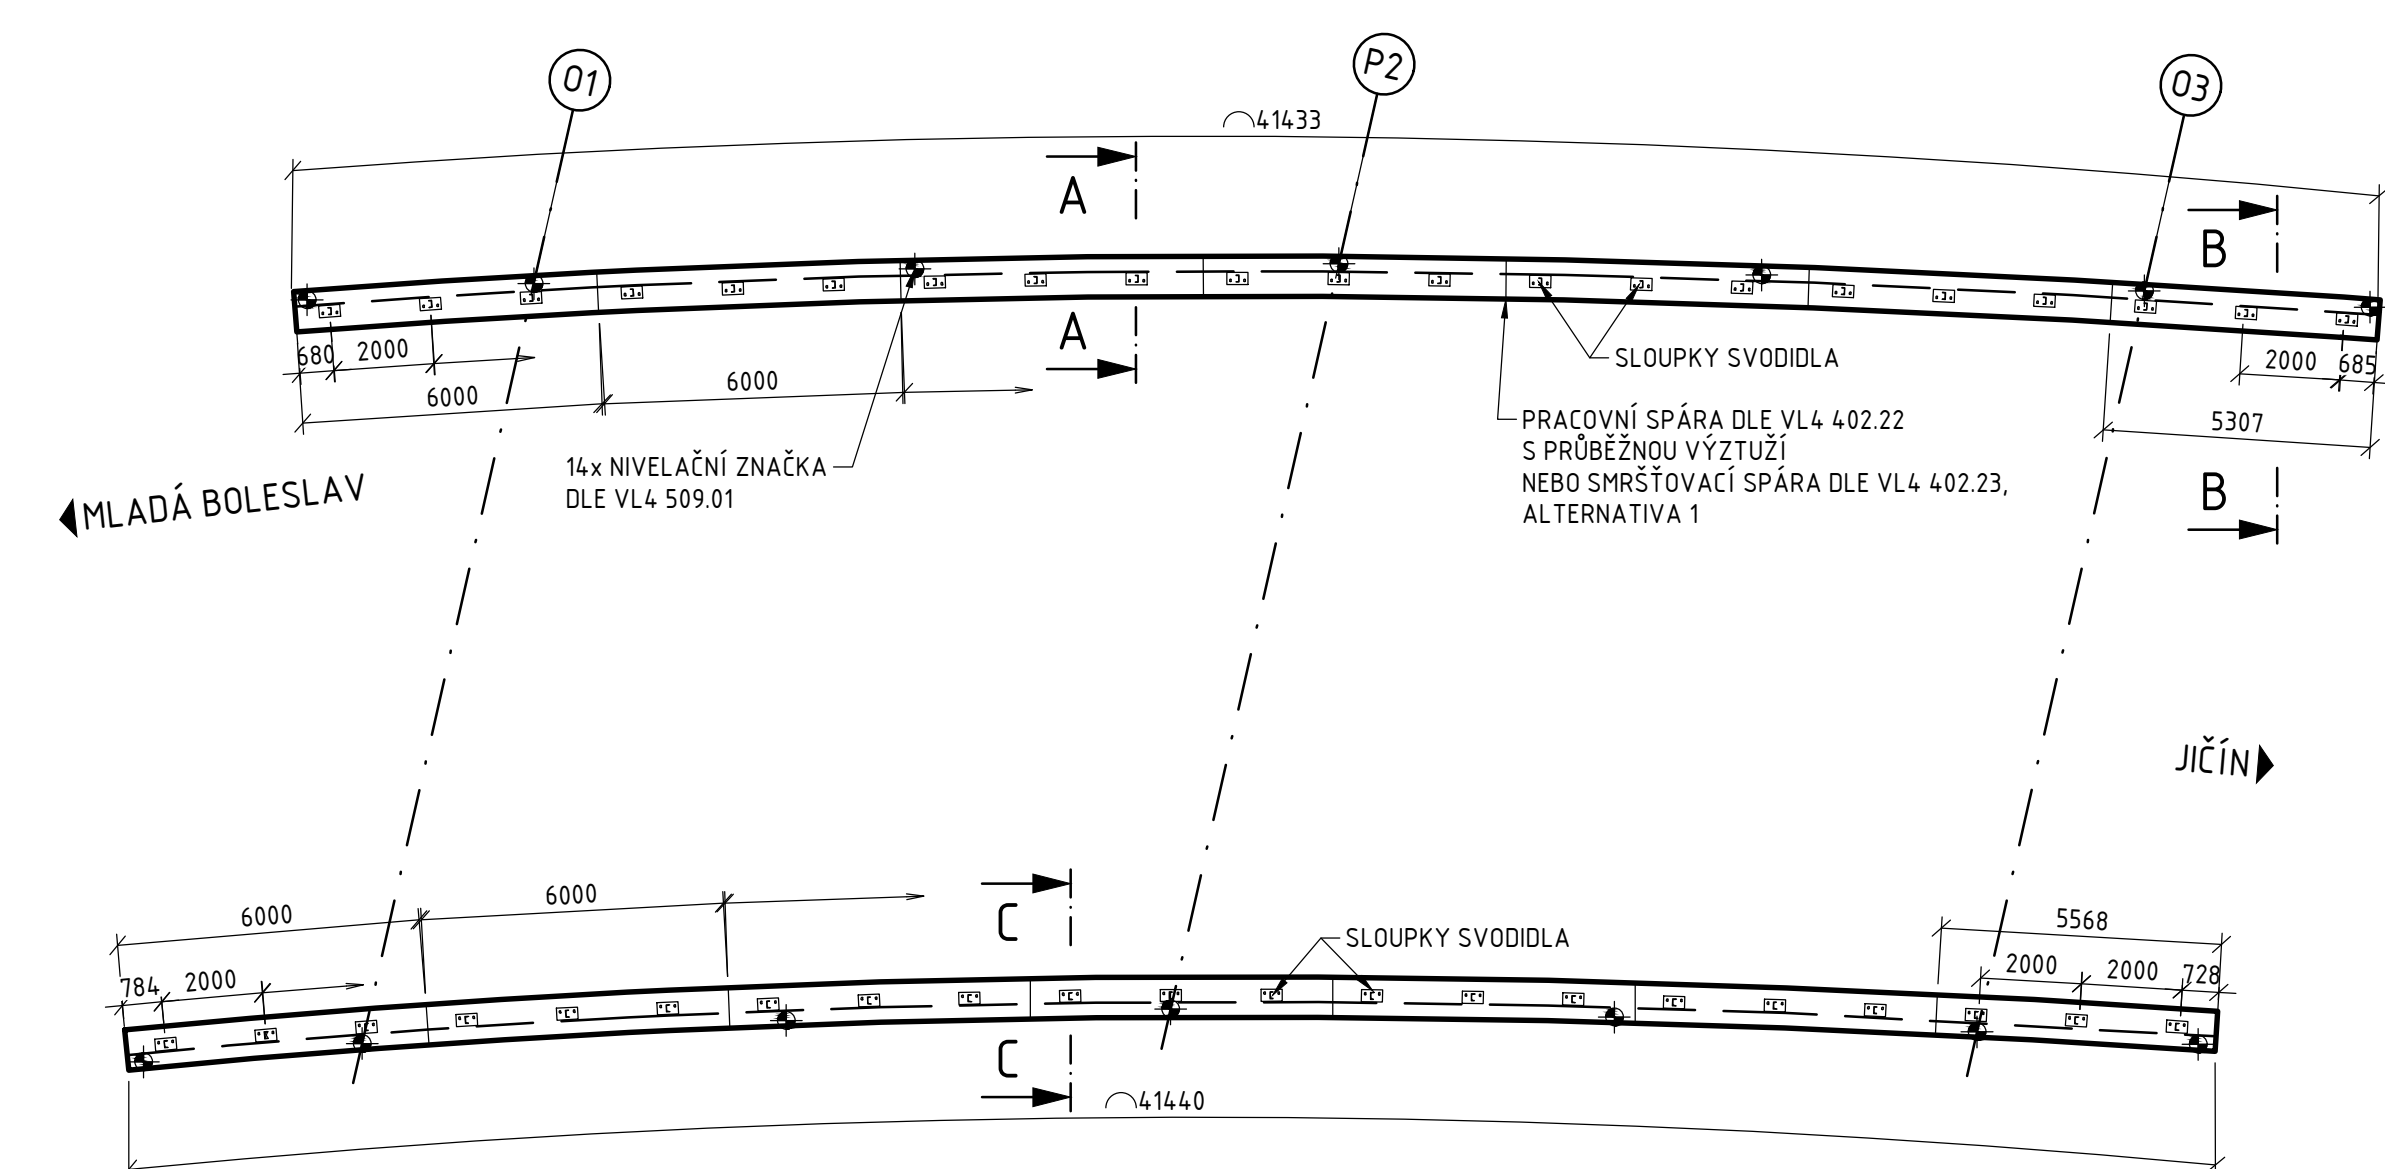


SCHÉMA ODVODNĚNÍ  
PODÉLNÝ ŘEZ 1:100

◀MLADÁ BOLESLAV

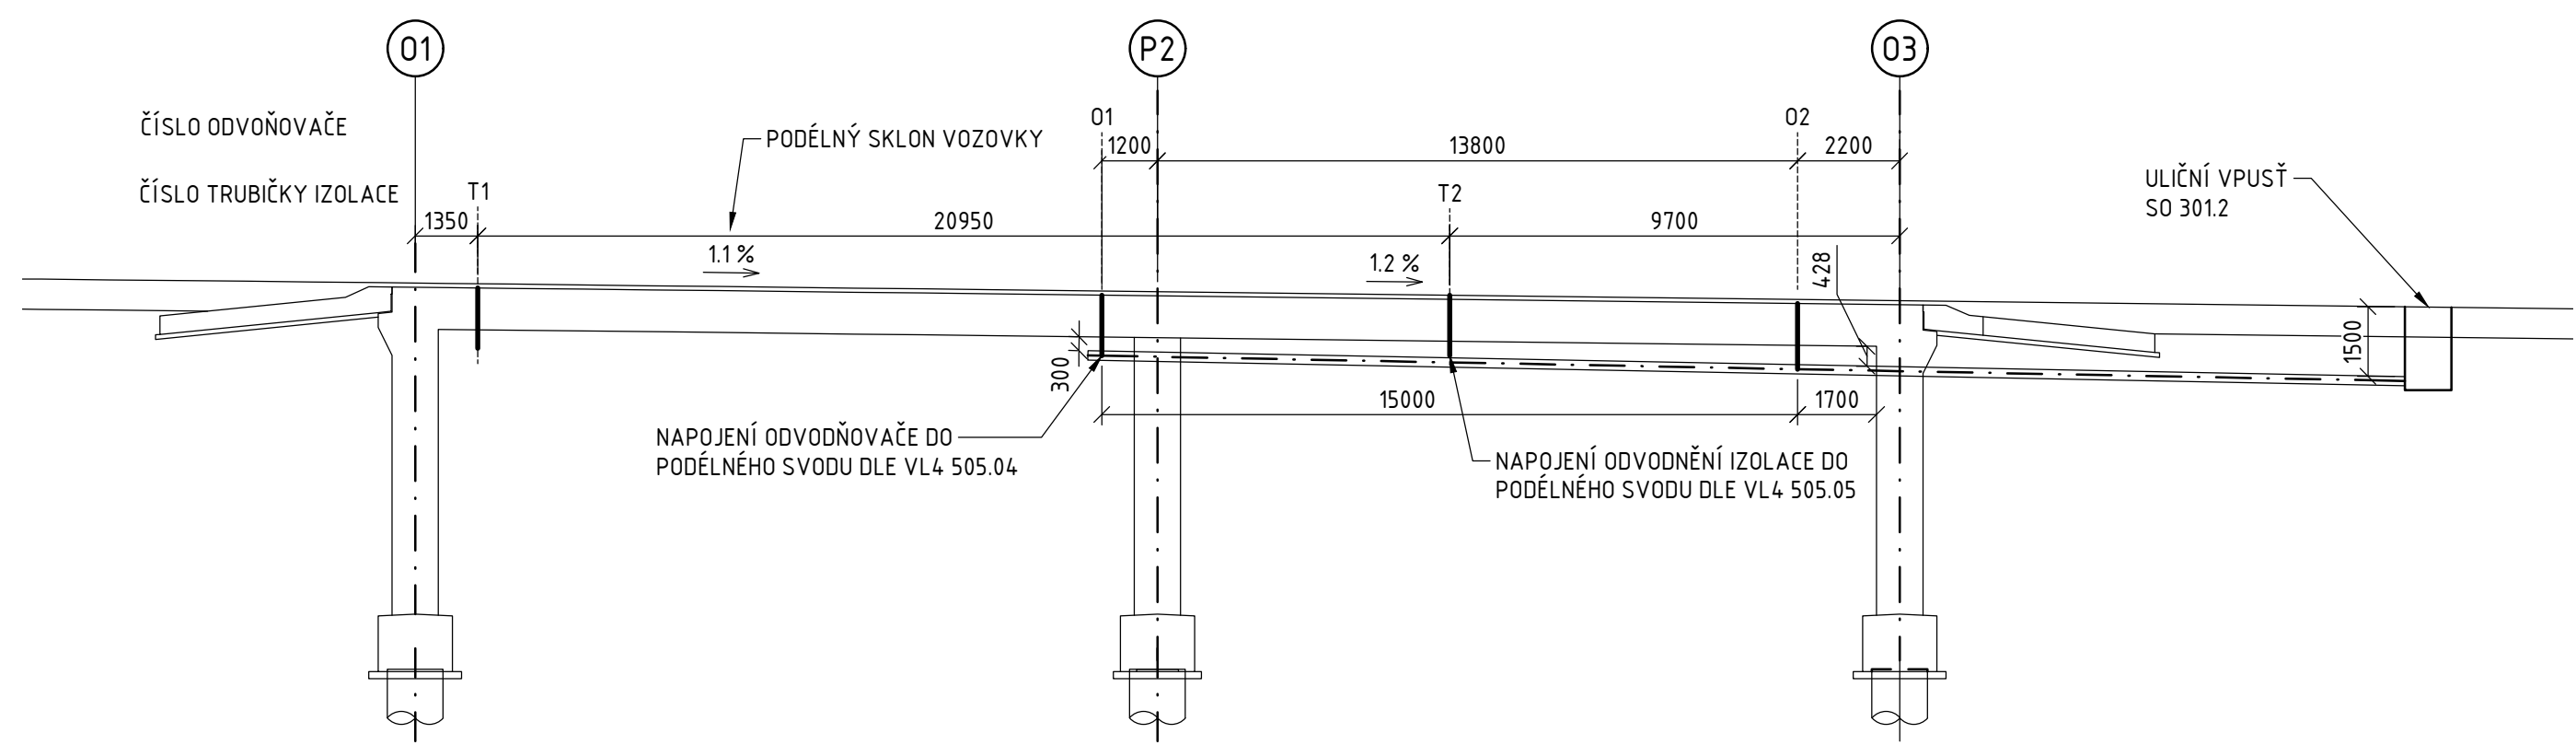


PŘÍČNÝ ŘEZ 1:50

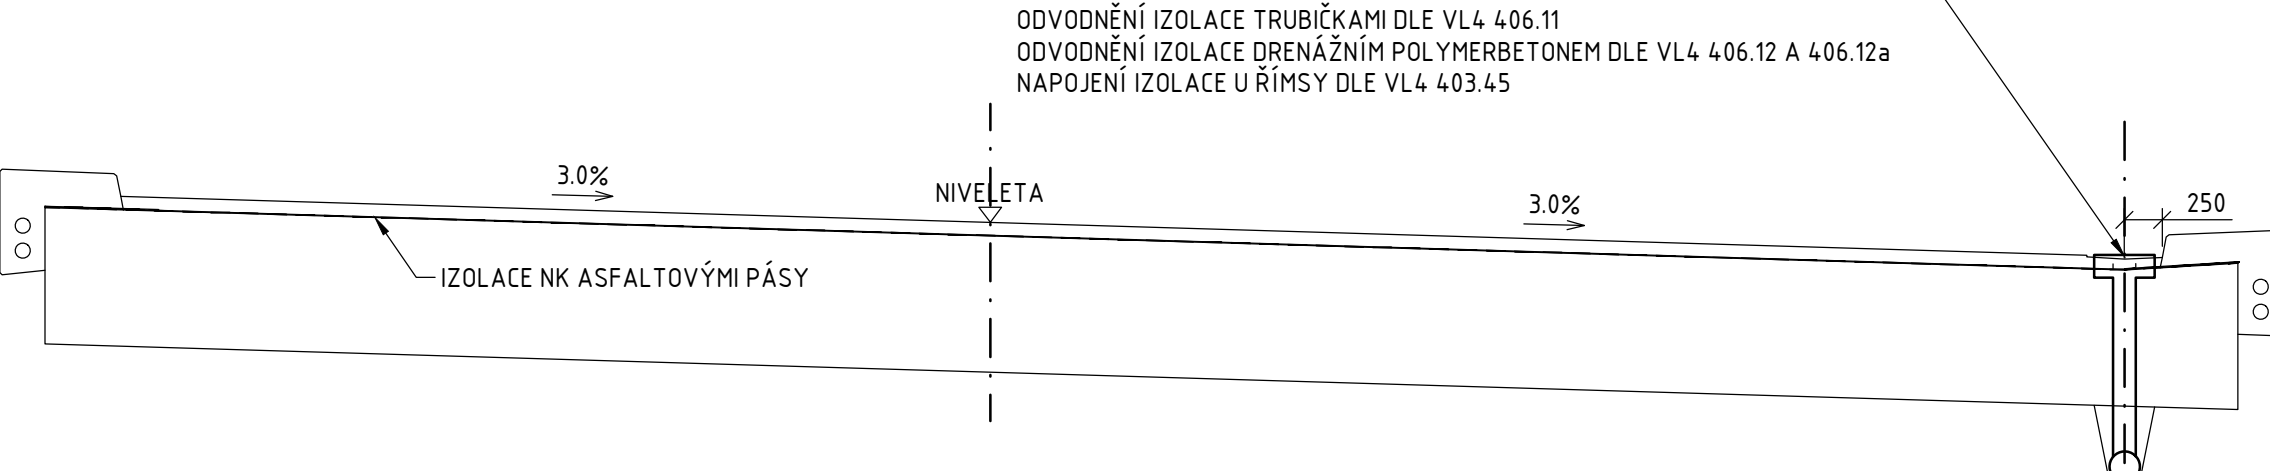


PŘÍČNÝ ŘEZ A-A 1:20

KRAJNÍ ŘÍMSA SE ZÁBRADELNÍM SVODIDLEM  
DLE VL4 101.05

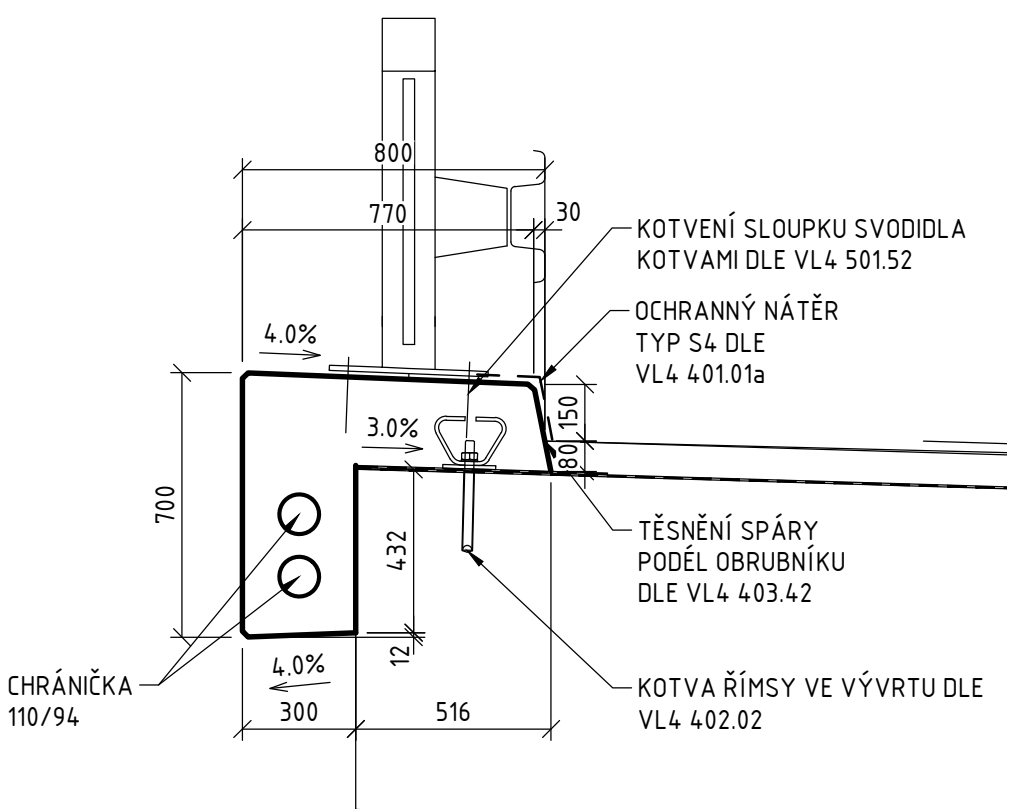


PŘÍČNÝ ŘEZ B-B 1:20

PLATÍ PRO VŠECHNA KŘÍDLA MOSTU

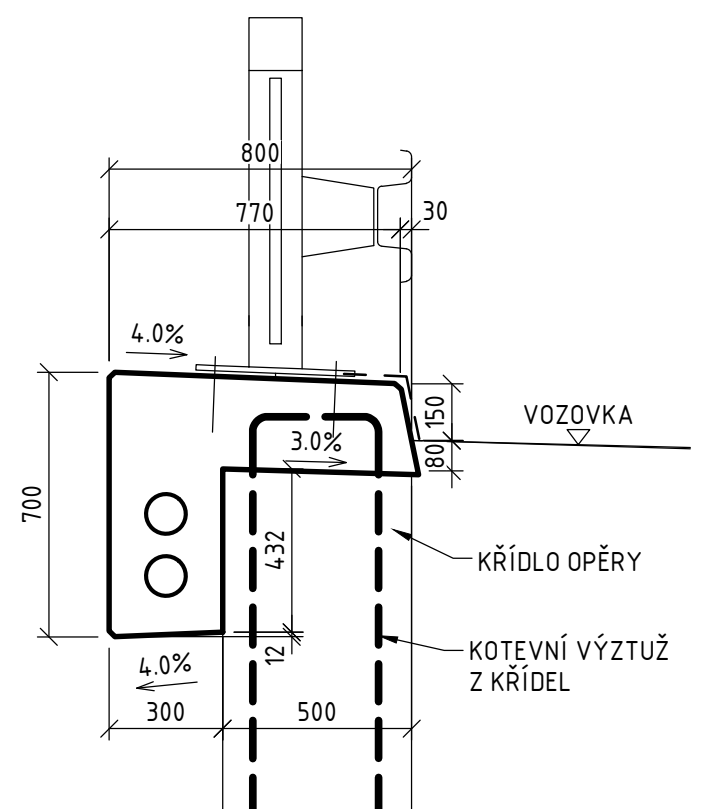

PŘÍČNÝ ŘEZ C-C 1:20

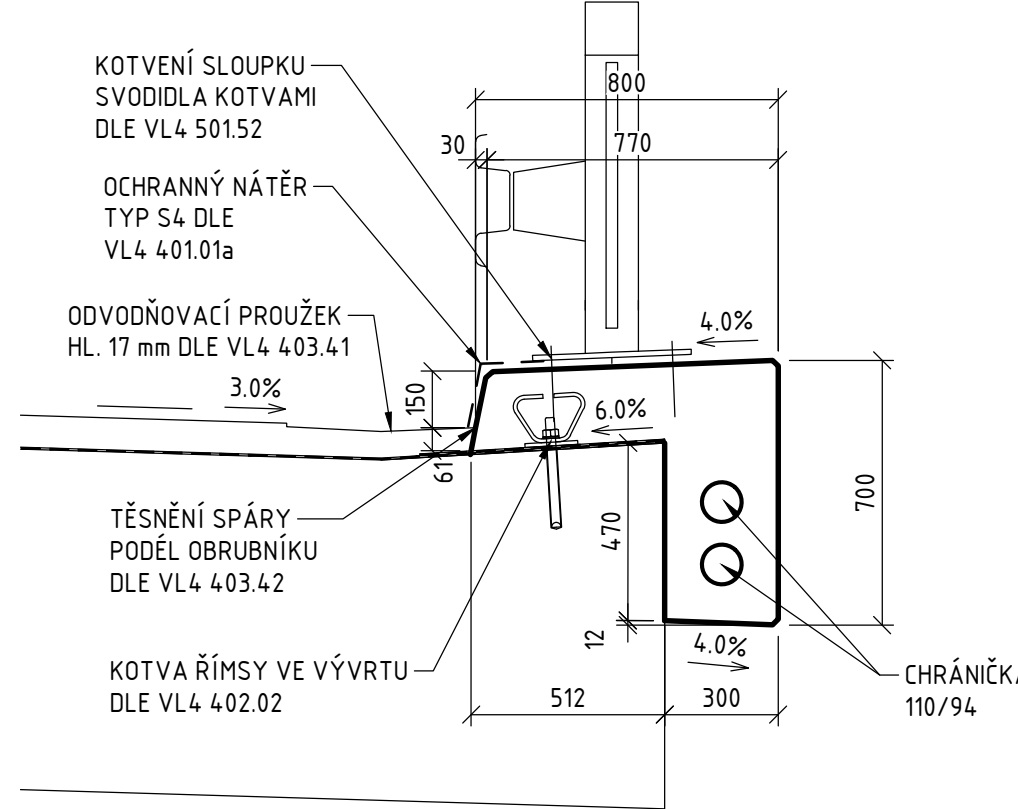


POZNÁMKY:

- NEDÍLNOU SOUČÁSTÍ VÝKRESU JSOU POZNÁMKY A SPECIFIKACE UVEDENÉ NA VÝKRESE POZNÁMEK A TECHNICKÝCH SPECIFIKACÍ



PŘECHODOVÉ OBLASTI, PODÉLNÝ ŘEZ 1:100

PŘECHODOVÉ OBLASTI S VLEČENOU PŘECHODOVOU DESKOU DLE VL4 201.07 A ČSN 73 624.4

◀MLADÁ BOLESLAV

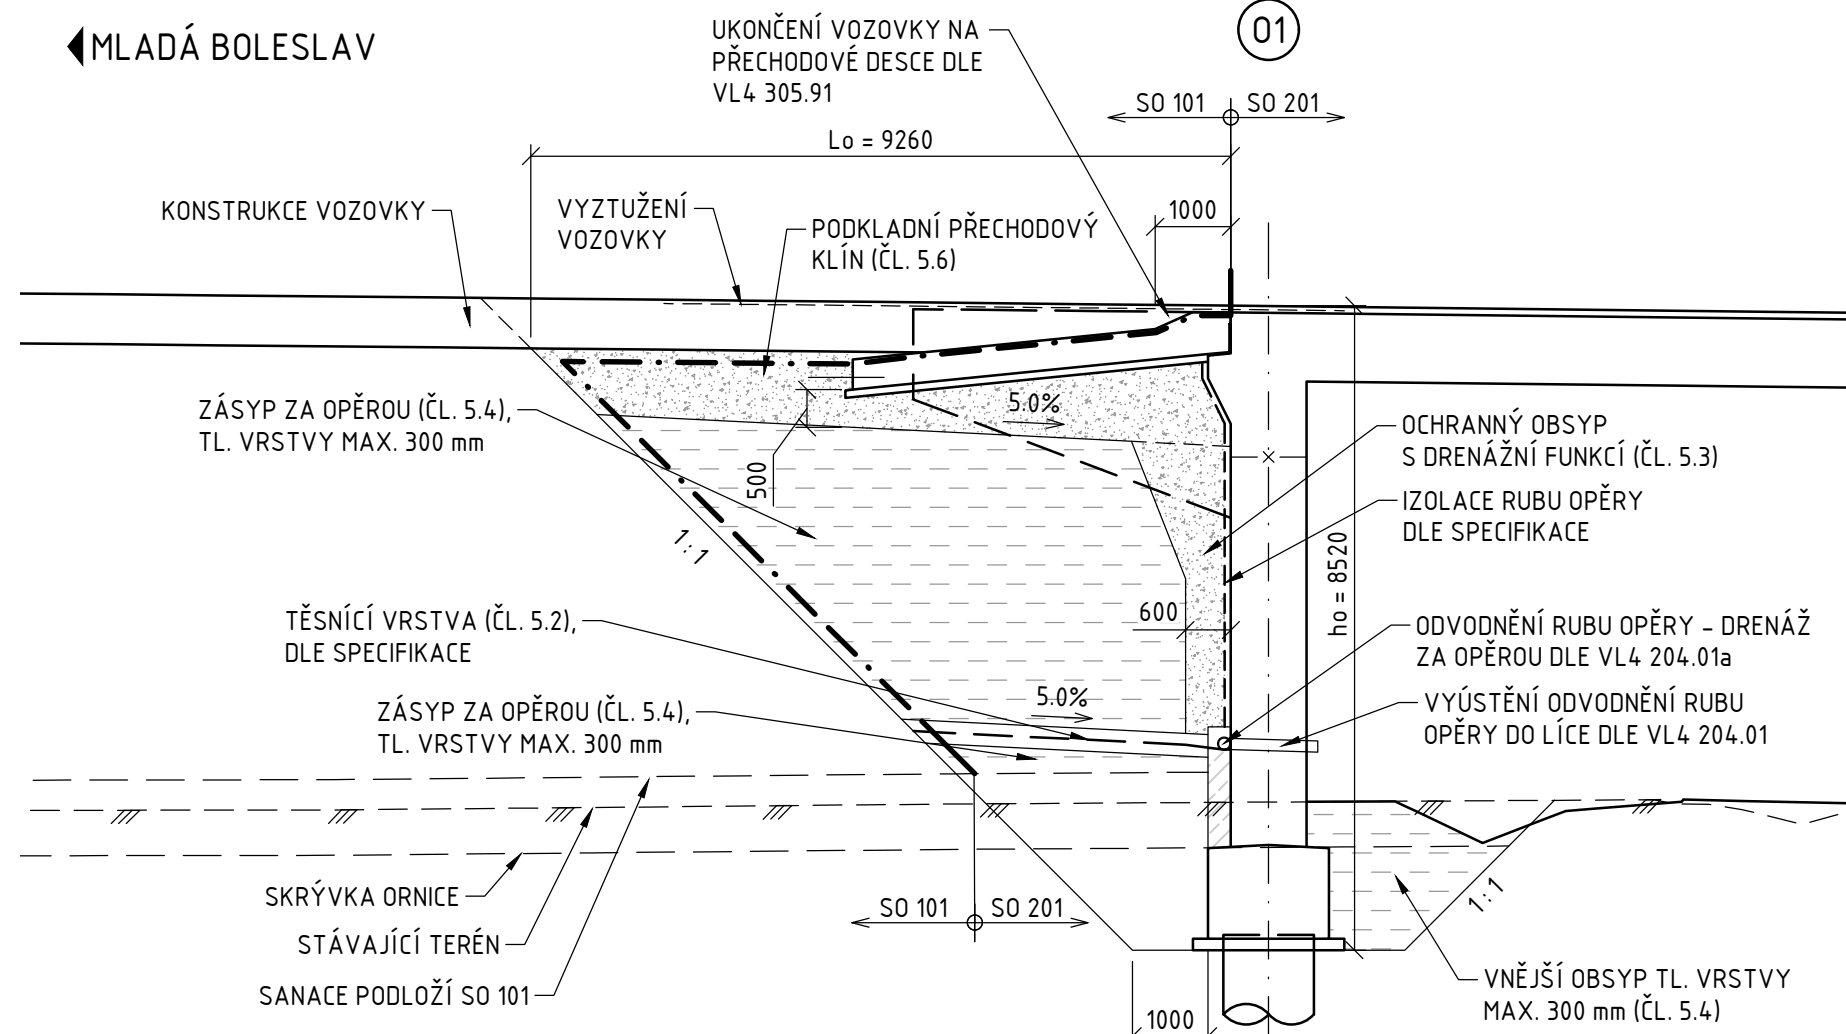

◀JIČÍN

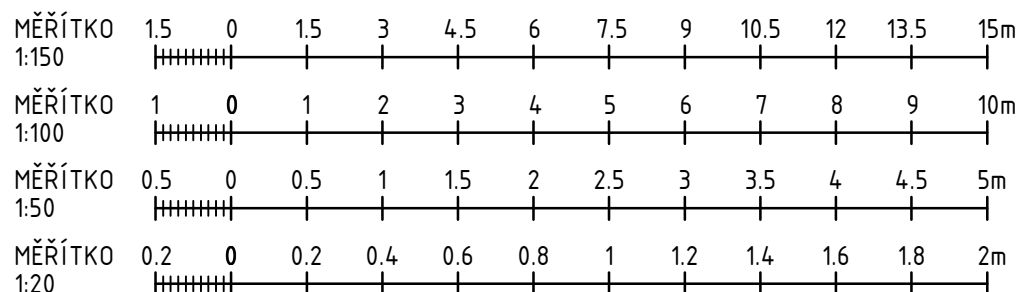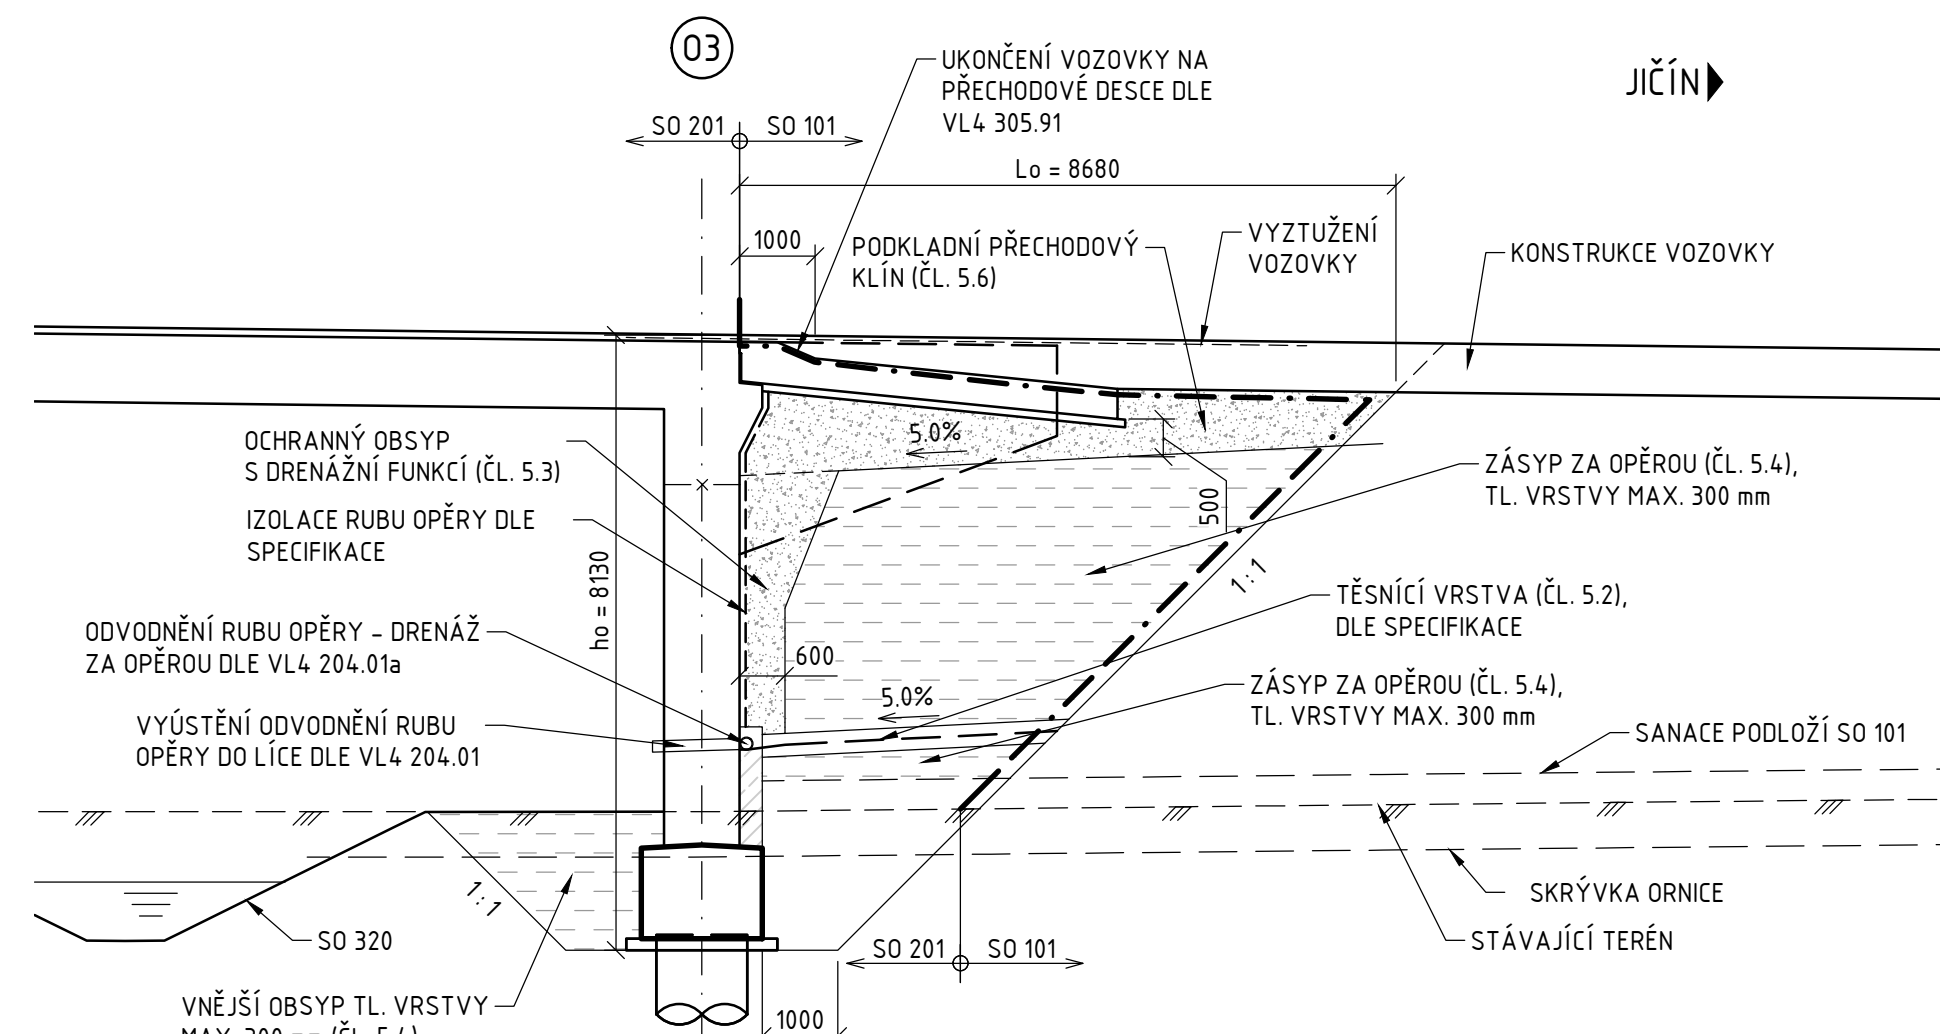

Souřadnicový systém: S-JTSK  
Výškový systém: Bpv

**SO 201** MOST NA I/16 PŘES MK A ZALUŽANSKOU VODOTEČ V KM 0,228

Objednatel: **Ředitelství silnic a dálnic**  
Čerčanská 2023/12, Krč, 140 00 Praha 4

**Valbek, spol. s r.o.**  
Vaňurova 505/17  
460 07 Liberec 3

|                                                                                       |                  |                                                   |                                                                                       |            |               |                    |
|---------------------------------------------------------------------------------------|------------------|---------------------------------------------------|---------------------------------------------------------------------------------------|------------|---------------|--------------------|
|  | Vypracoval       | M. KNESPLOVÁ                                      |  | Zak. číslo | 21-L113-001   |                    |
|                                                                                       | Zodp. projektant | ING. S. RŮŽIČKA                                   |  | Datum      | 02/2025       |                    |
|                                                                                       | Tech. kontrola   | ING. I. BELDA                                     |  | Stupeň     | PDPS          |                    |
|                                                                                       | Akce             | I/16 MLADÁ BOLESLAV - MARTINOVICE                 |                                                                                       |            | Počet formátů | 8x A4              |
| Zhotovitel:<br>Valbek, spol. s r.o.<br>Vaňurova 505/17<br>460 07 Liberec 3            | Příloha          | TVAR ŘÍMS, SCHÉMA ODVODNĚNÍ<br>PŘECHODOVÉ OBLASTI |                                                                                       |            | Měřítko       | 1:150, 100, 50, 20 |
|                                                                                       |                  |                                                   |                                                                                       |            | Č. přílohy    | Paré               |
|                                                                                       |                  |                                                   |                                                                                       |            | 205           |                    |

205