


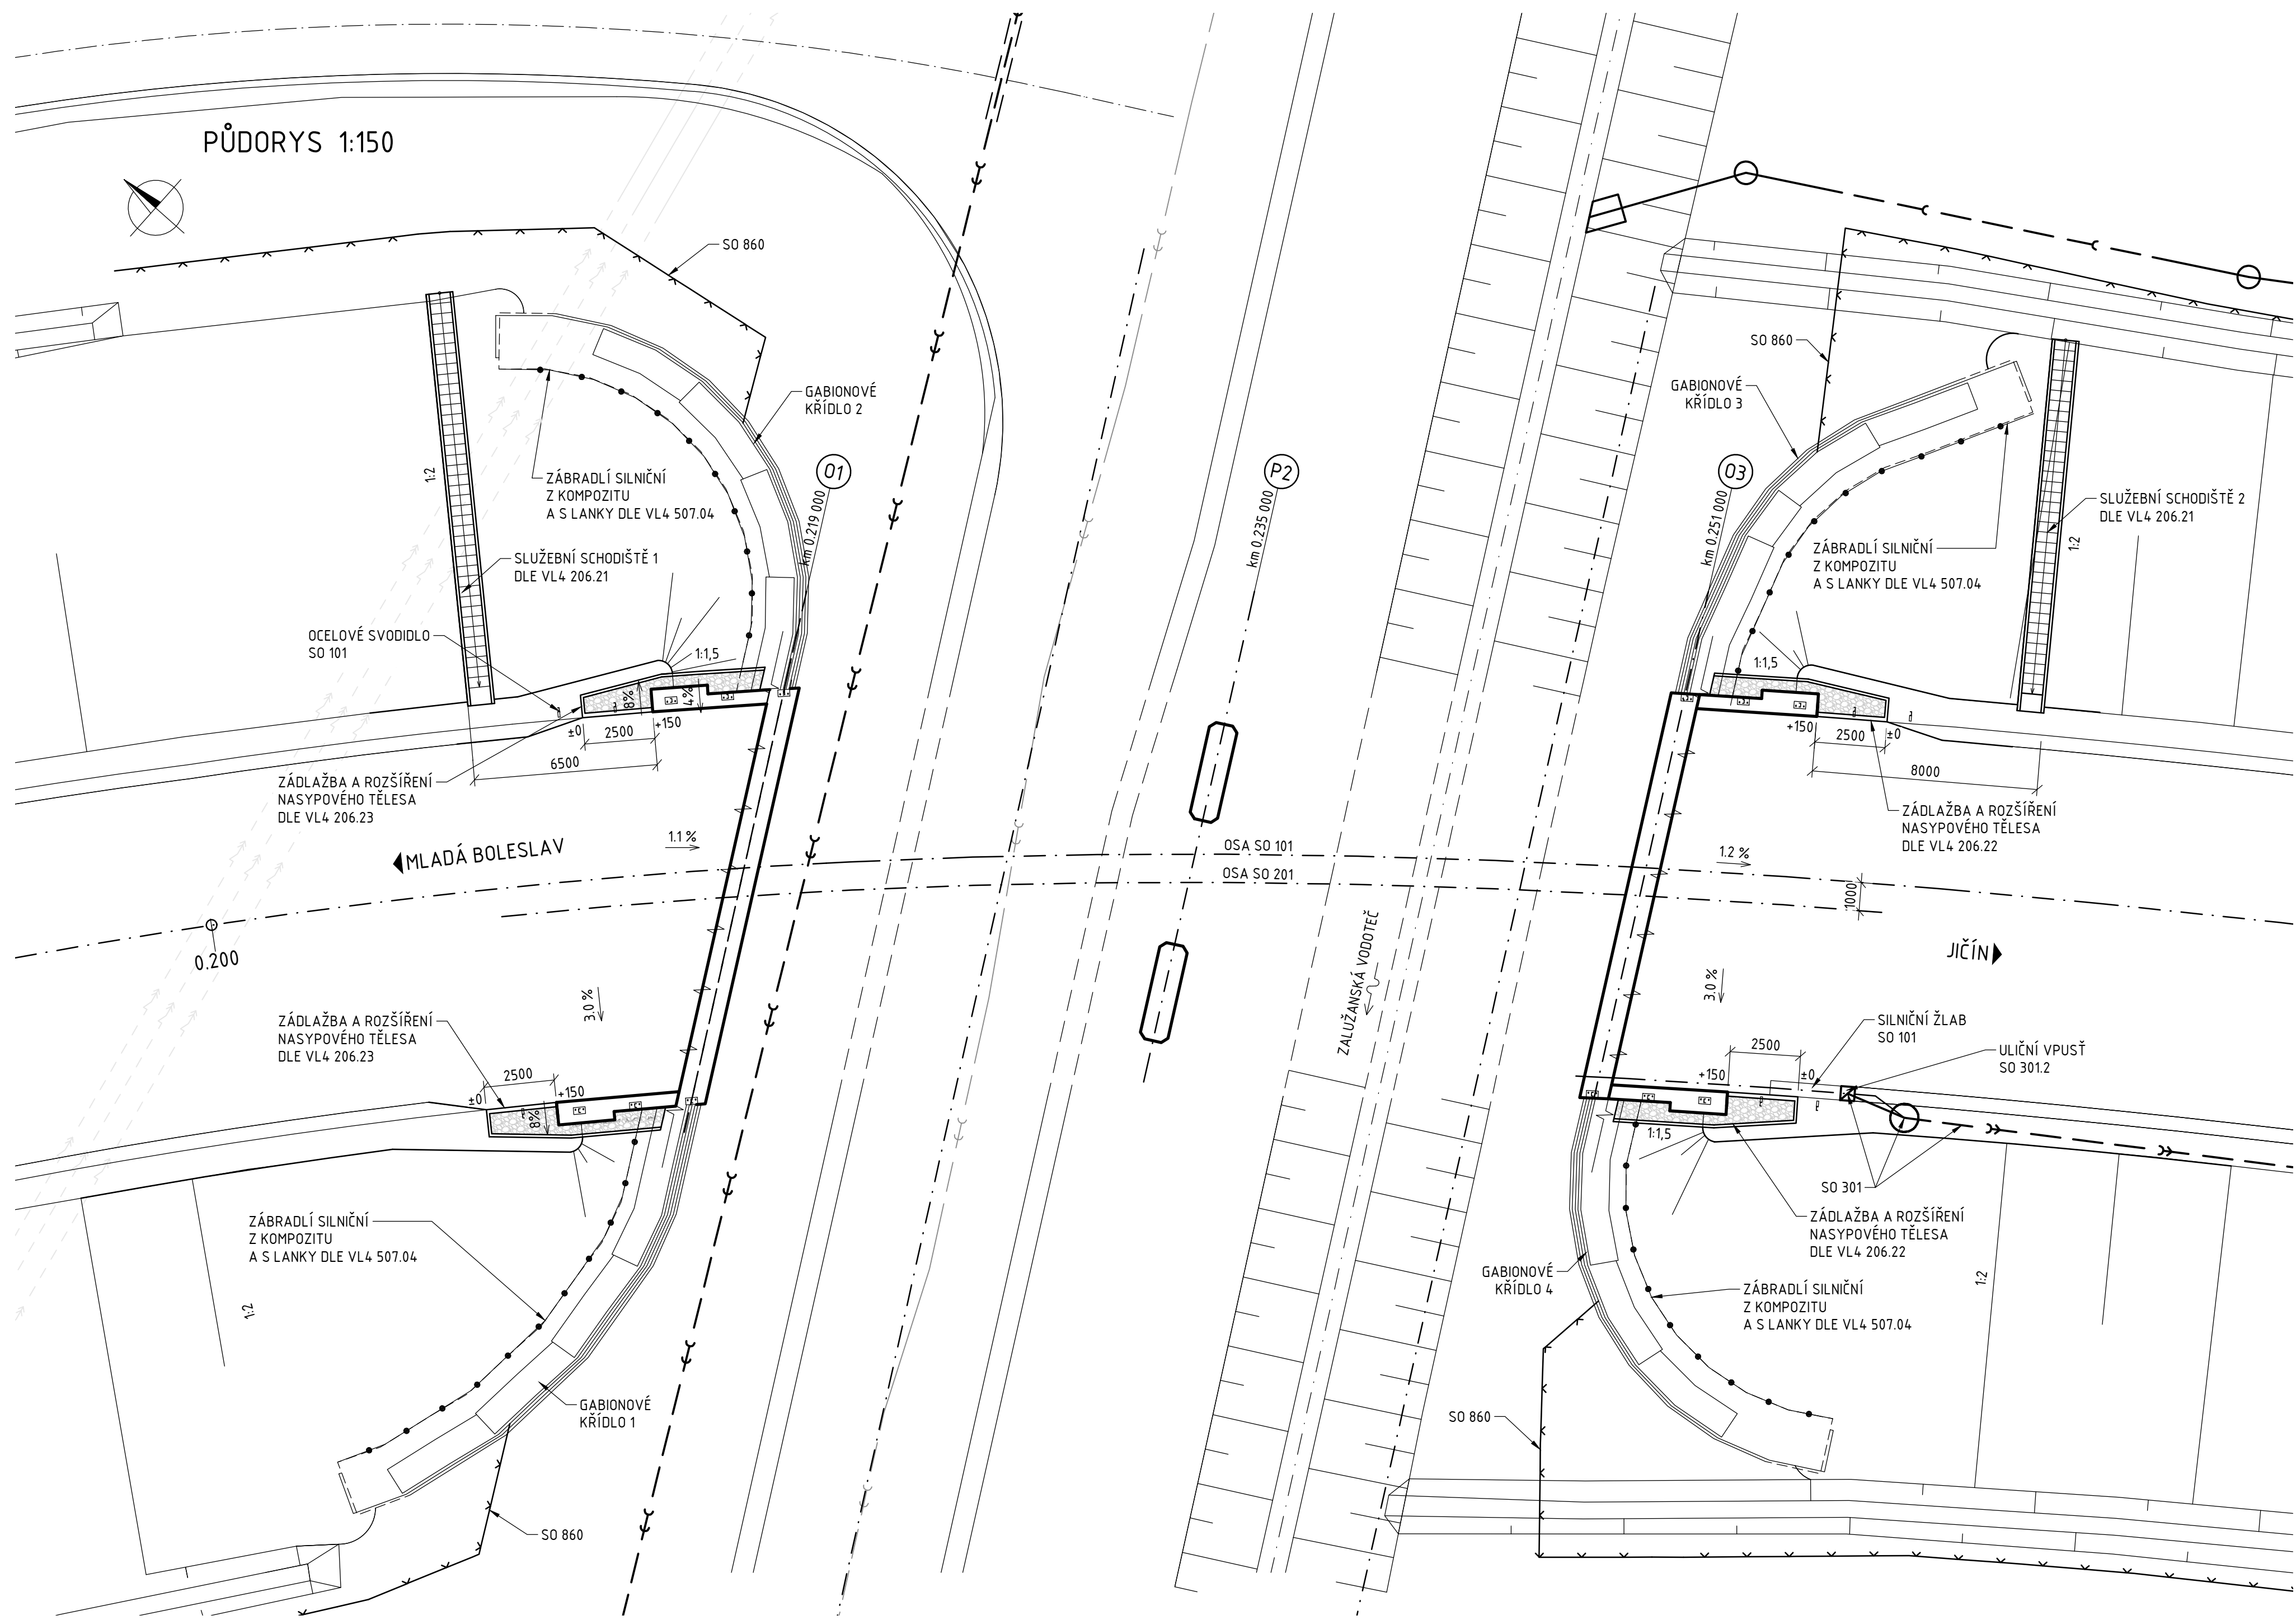

PŮDORYS 1:150

SLUŽEBNÍ SCHODIŠTĚ 1 1: 100

SLUŽEBNÍ SCHODIŠTĚ 2 1: 100

ŘEZ A-A 1:25

