




ROZVINUTÉ POHLEDY - OPĚRA 01 1:100

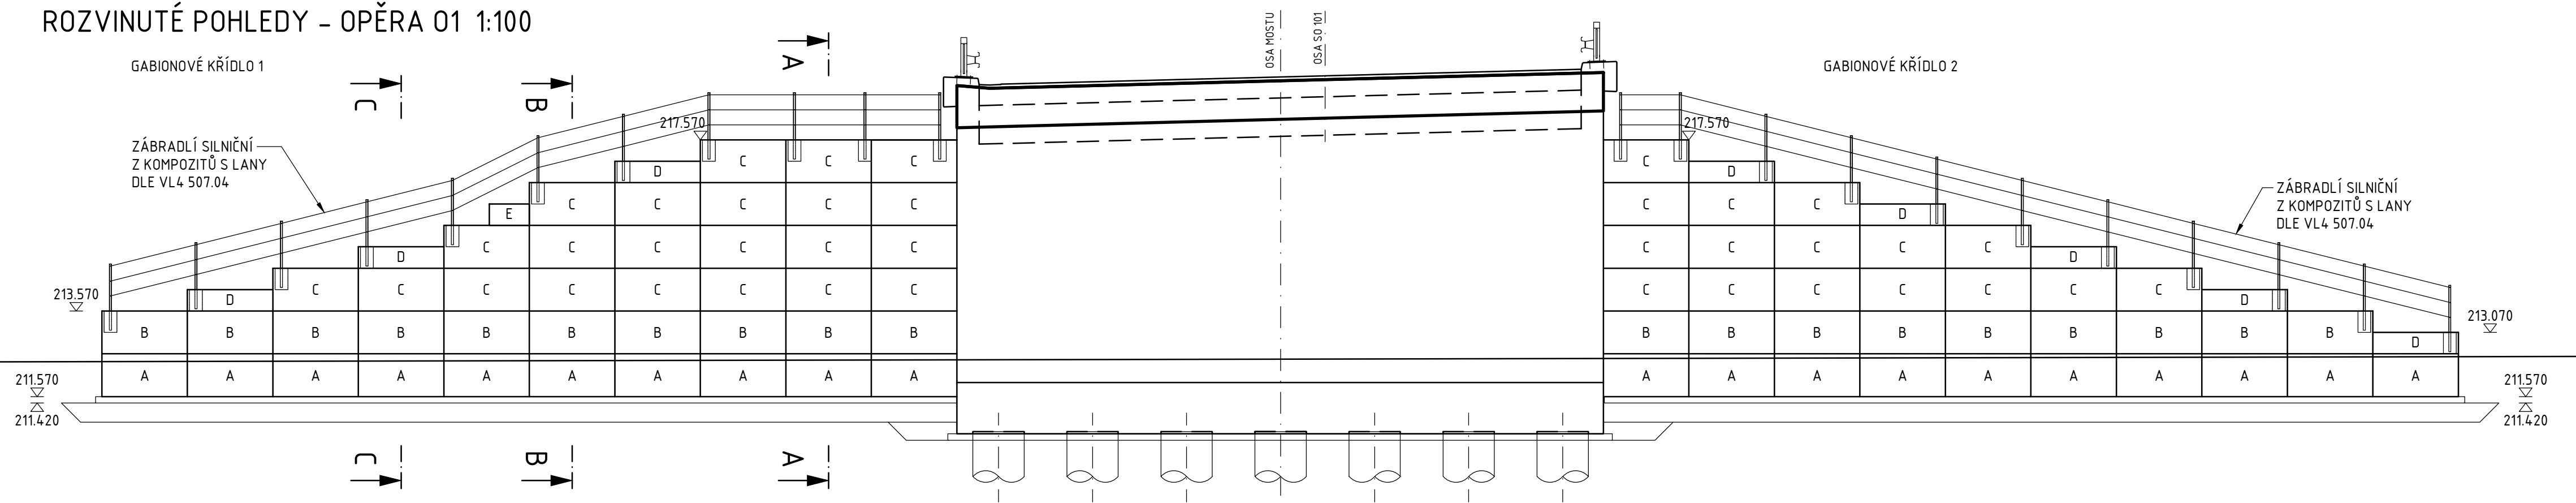


PŘÍČNÝ ŘEZ GABIONOVÝMI KŘÍDLY V LÍCI NK 1:100

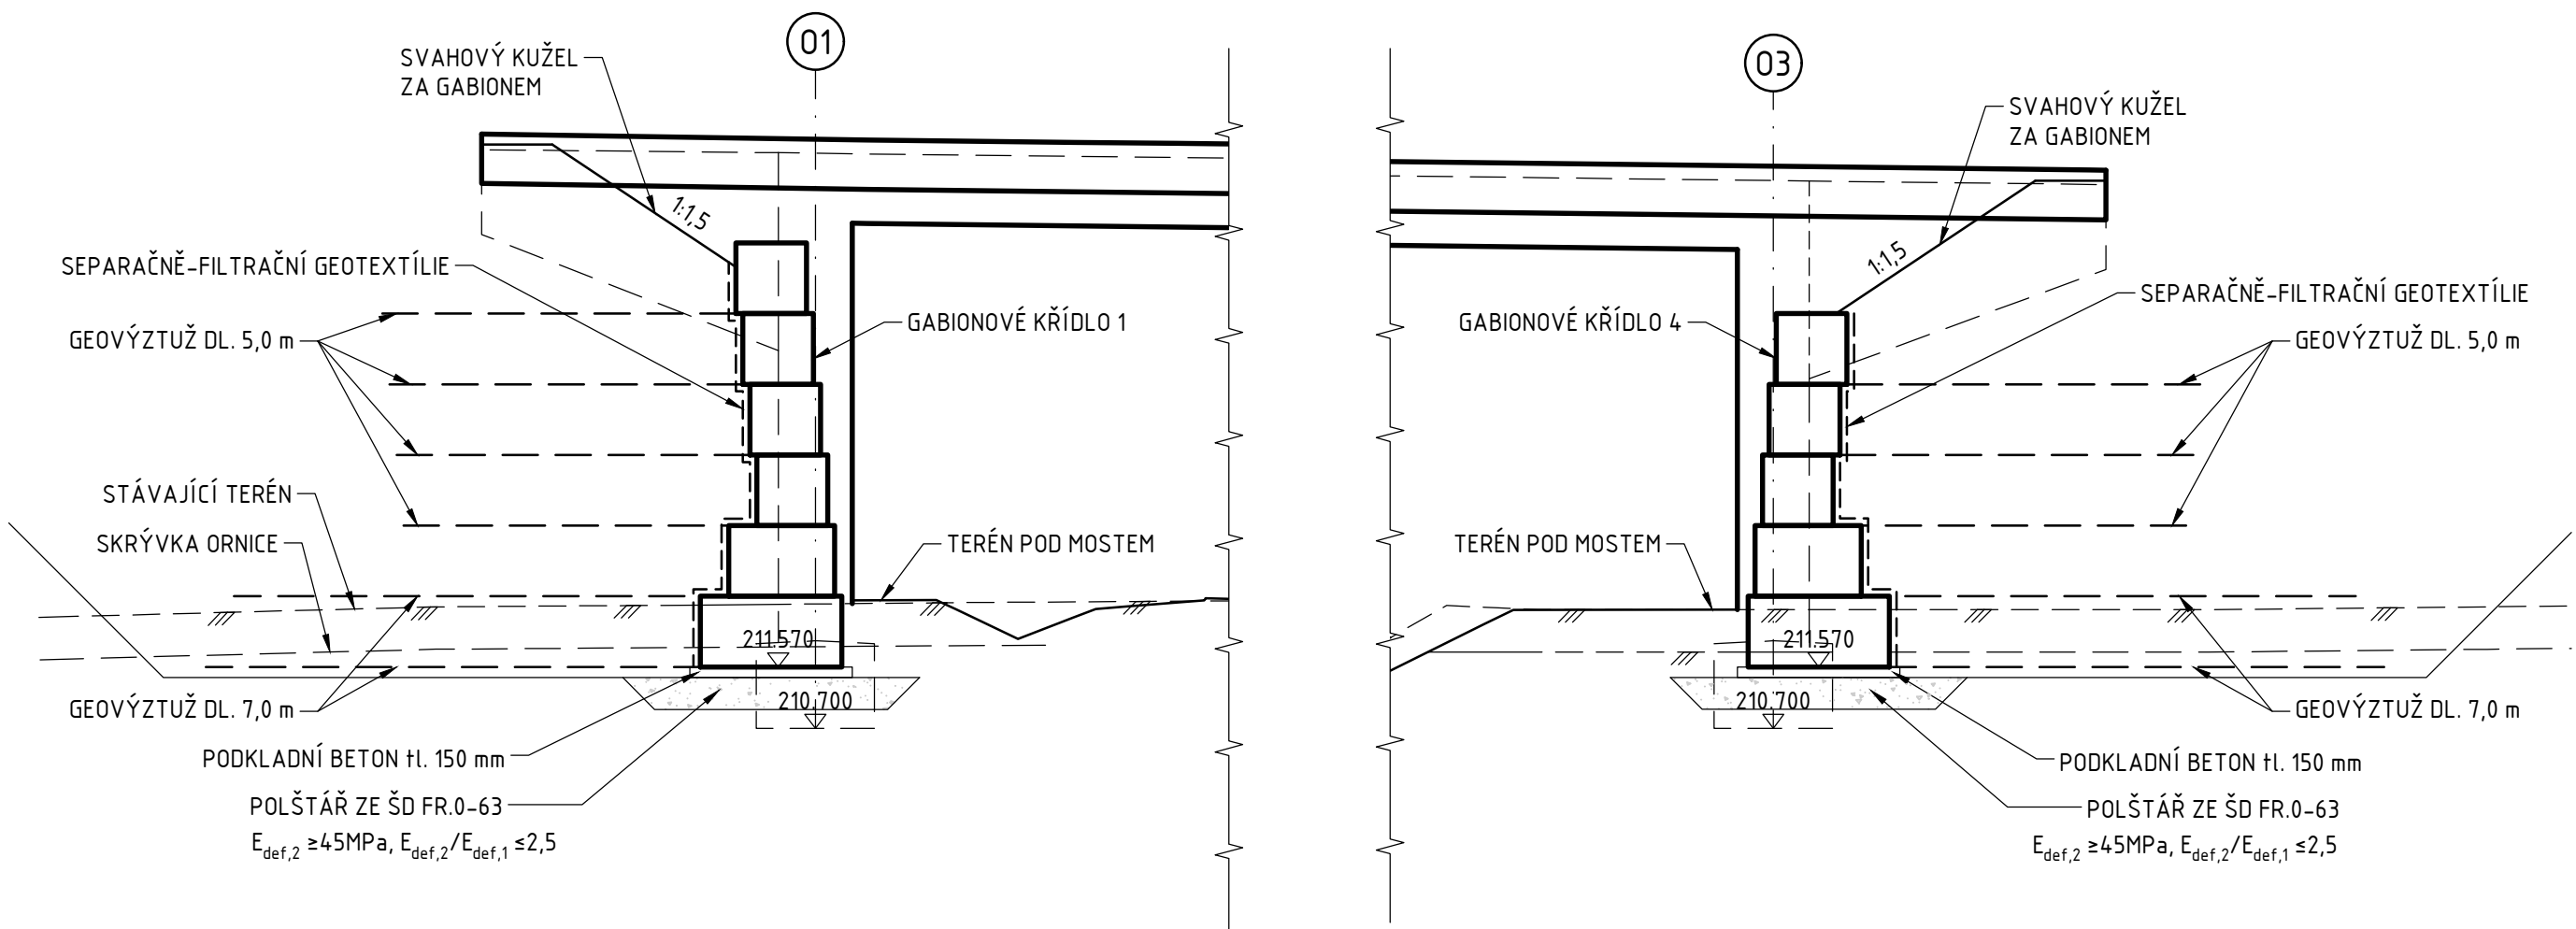


PŘÍČNÉ ŘEZY 1:100

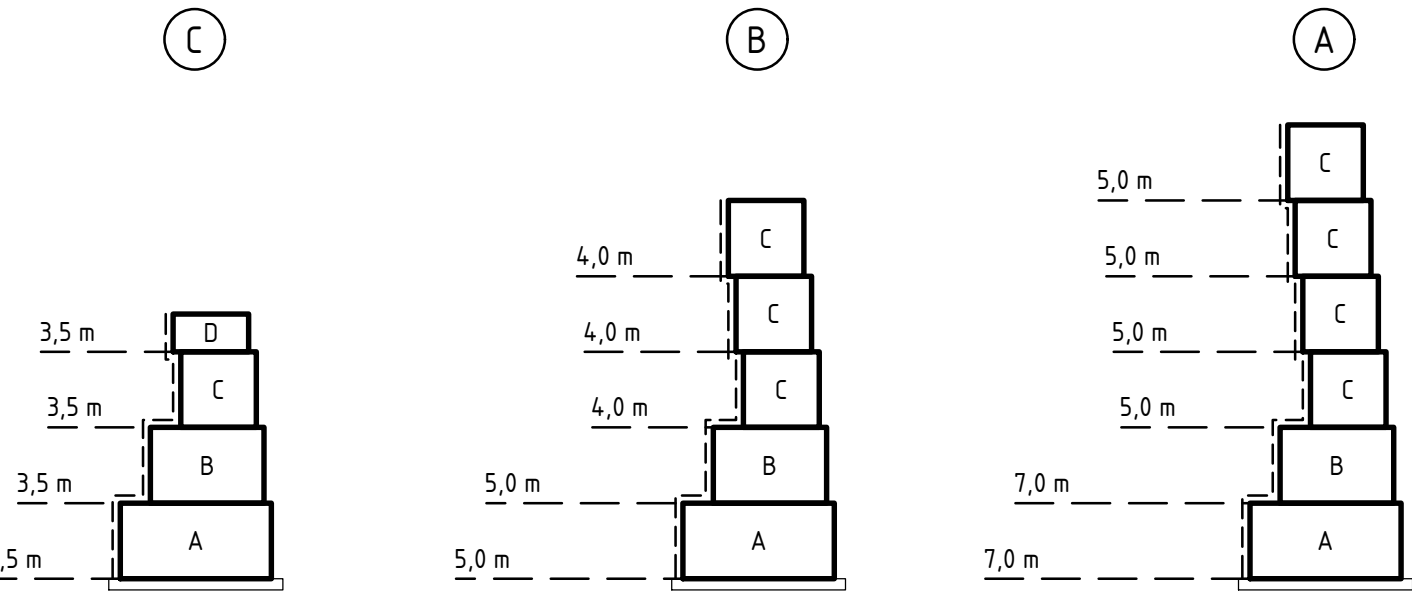



ROZVINUTÉ POHLEDY - OPĚRA 03 1:100

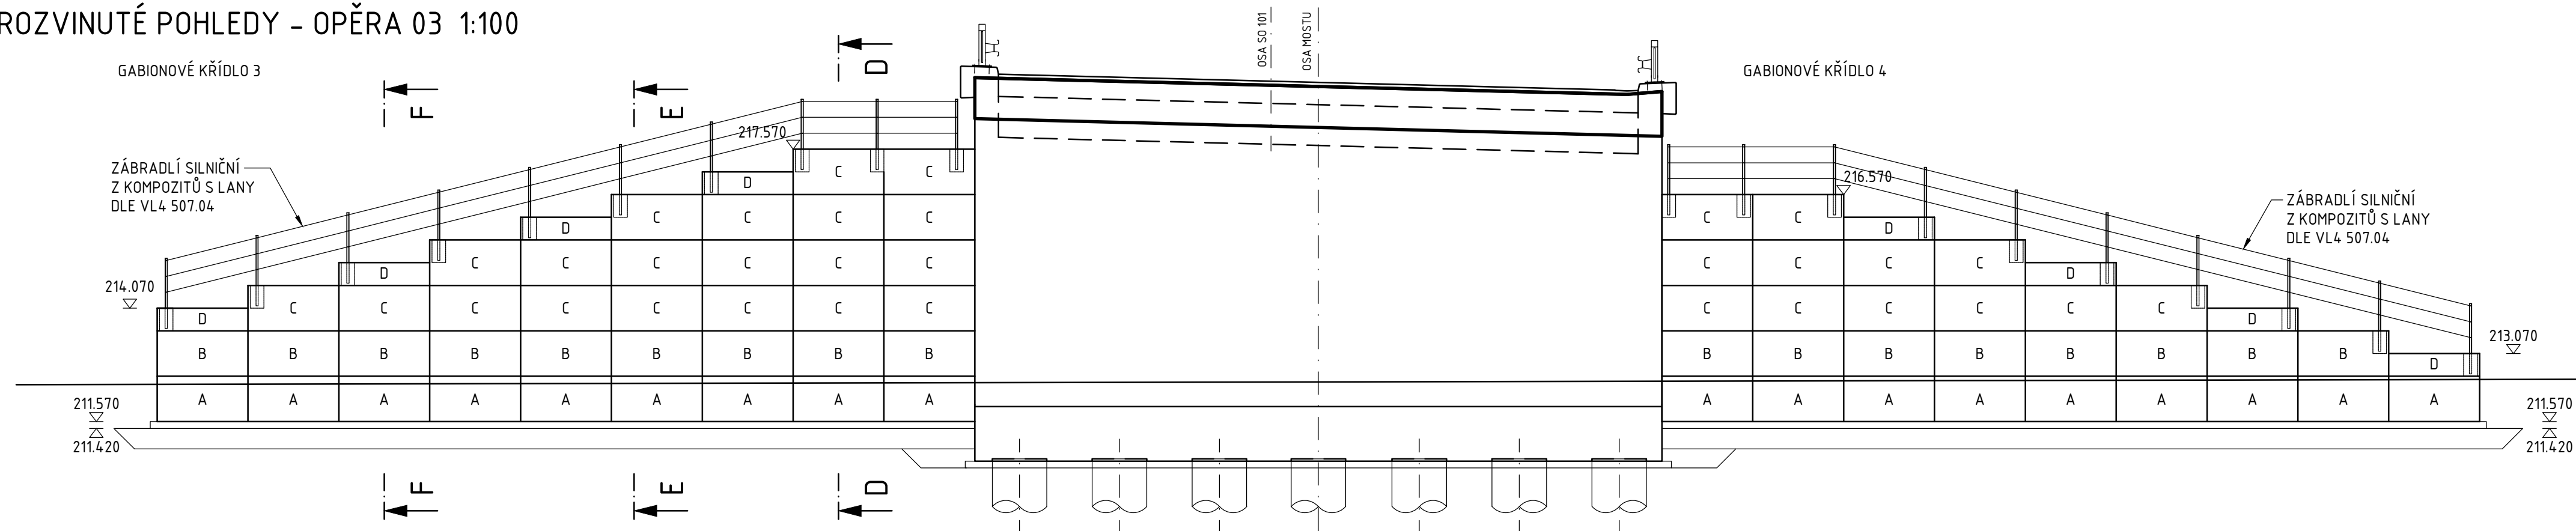

PŘÍČNÝ ŘEZ GABIONOVÝMI KŘÍDLY V LÍCI NK 1:100

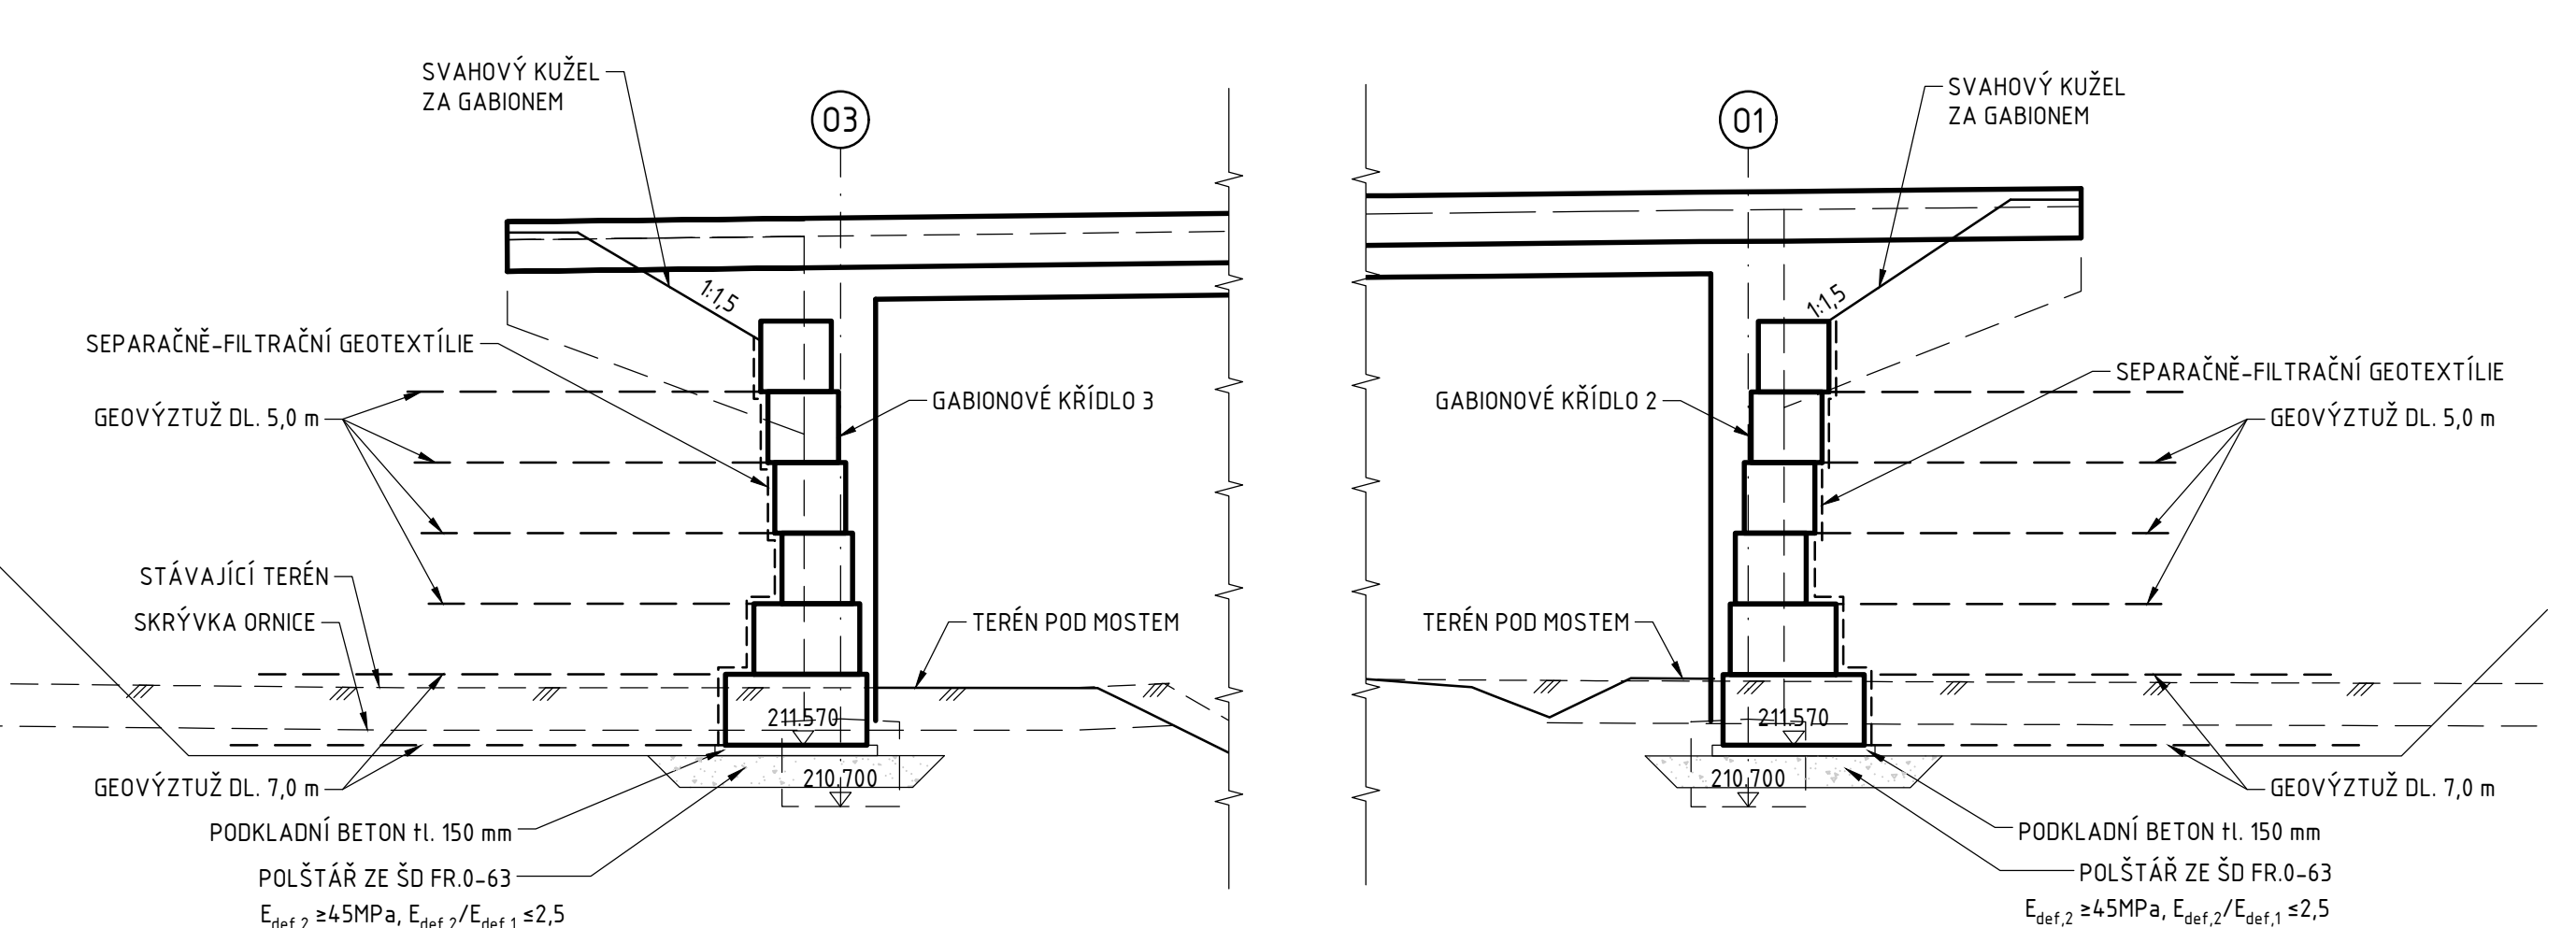

PŘÍČNÉ ŘEZY 1:100

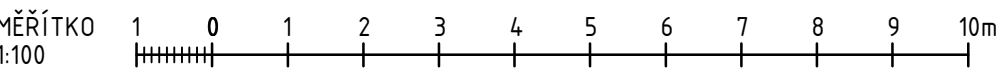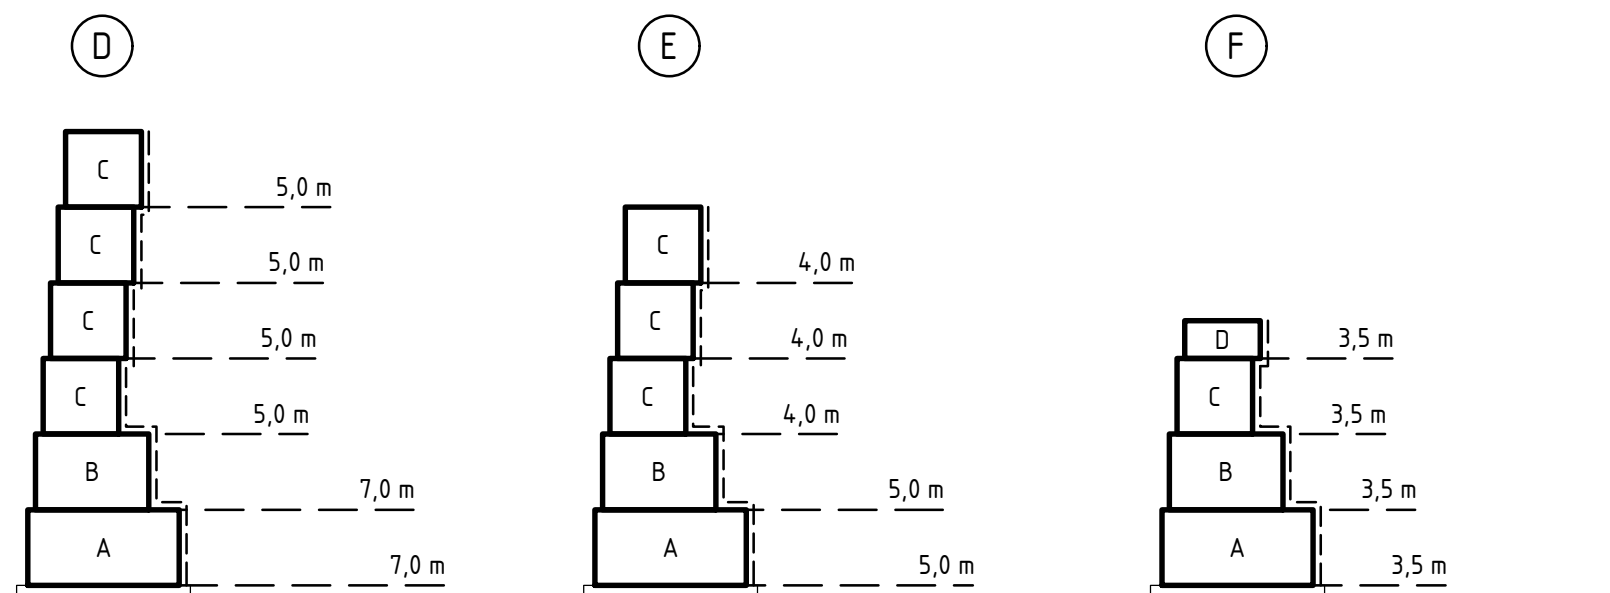

ROZMĚRY GABIONOVÝCH KOŠŮ:

- OZN. Š. DL. V.
A - 2000 x 2000 x 1000
B - 1500 x 2000 x 1000
C - 1000 x 2000 x 1000
D - 1000 x 2000 x 500
E - 1000 x 1000 x 500

POZNÁMKY:

- NEDÍLNOU SOUČÁSTÍ VÝKRESU JSOU POZNÁMKY A SPECIFIKACE UVEDENÉ NA VÝKRESE POZNÁMEK A TECHNICKÝCH SPECIFIKACÍ

Souřadnicový systém: S-JTSK
Výškový systém: Bpv

SO 201 MOST NA I/16 PŘES MK A ZALUŽANSKOU VODOTEČ V KM 0,228

Objednatel: Ředitelství silnic a dálnic
Ředitelství silnic a dálnic s. p.
Čerčanská 2023/12, Krč, 140 00 Praha 4

Valbek, spol. s r.o.
Vaňurova 505/17
460 07 Liberec 3

	Vypracoval	ING. S. RŮŽIČKA	Zak. číslo	21-L113-001
	Zodp. projektant	ING. S. RŮŽIČKA	Datum	02/2025
	Tech. kontrola	ING. I. BELDA	Stupeň	PDPS
	Akce	I/16 MLADÁ BOLESLAV - MARTINOVICE		
Zhotovitel: Valbek, spol. s r.o. Vaňurova 505/17 460 07 Liberec 3	Příloha	GABIONOVÁ KŘÍDLA	Počet formátů	8x A4
			Měřítko	1:100
			Č. přílohy	Paré
			207	