
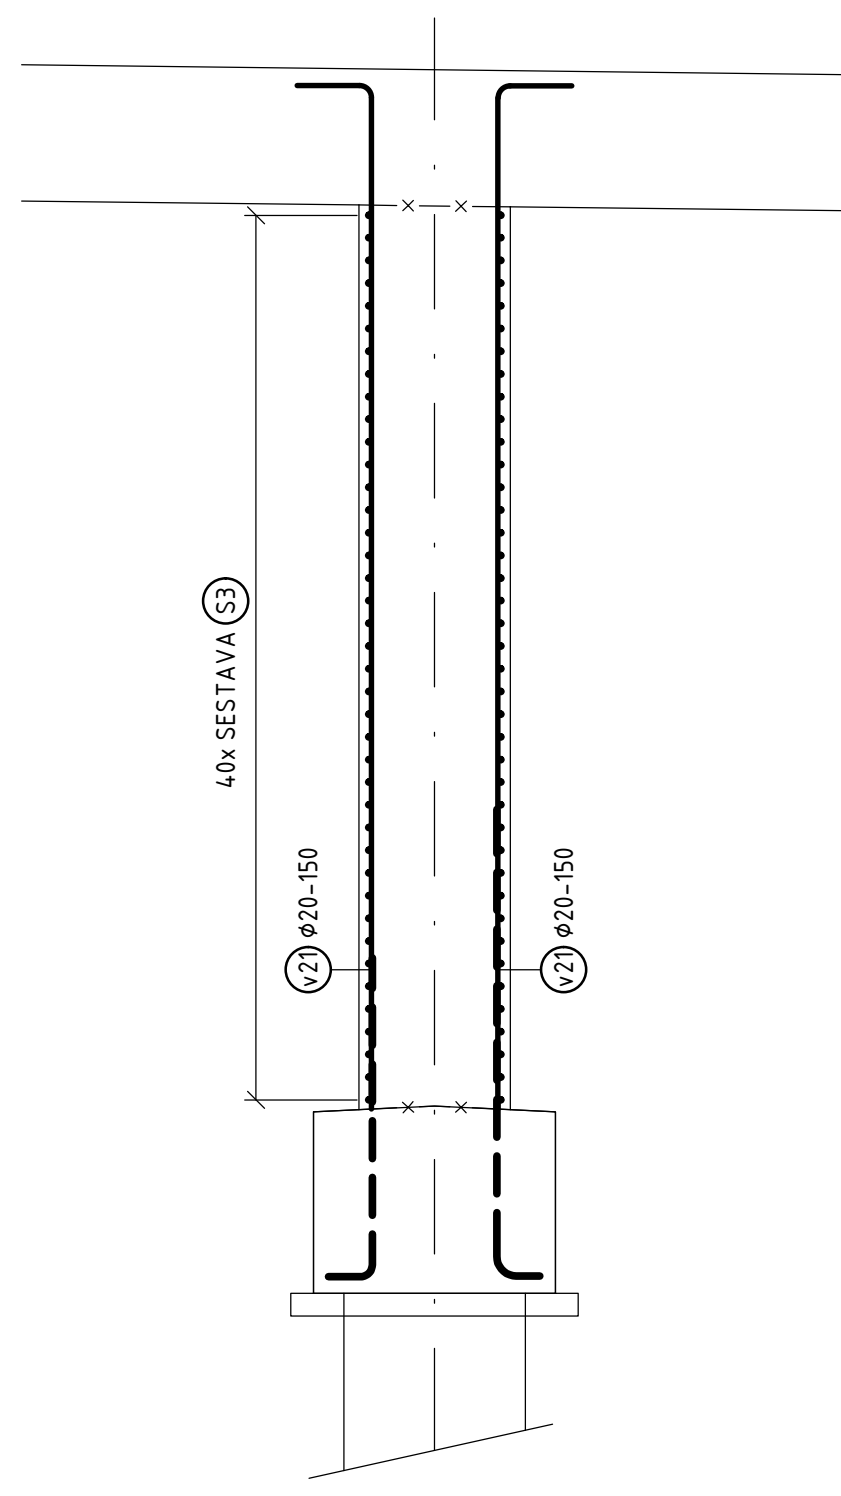
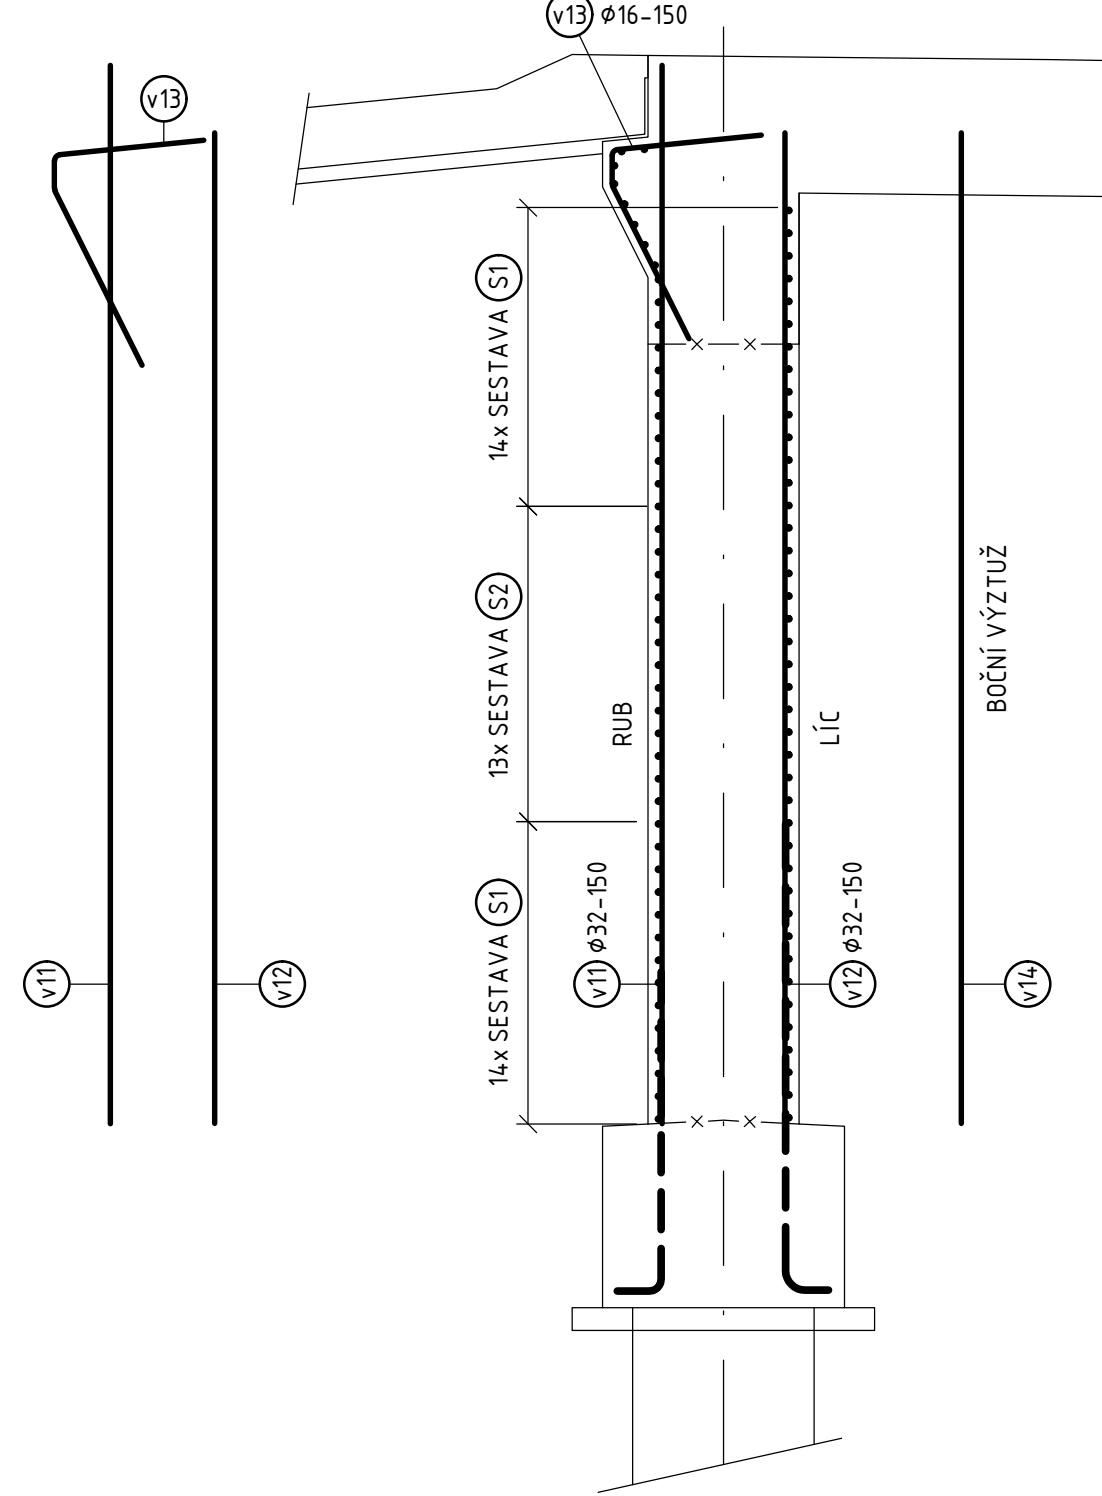


SCHÉMA VÝZTUŽE SPODNÍ STAVBY
PŘÍČNÝ ŘEZ 1:50


SCHÉMA VÝZTUŽE ZÁKLADŮ
PŘÍČNÝ ŘEZ 1:50

KRAJNÍ OPĚRA


PILÍŘ

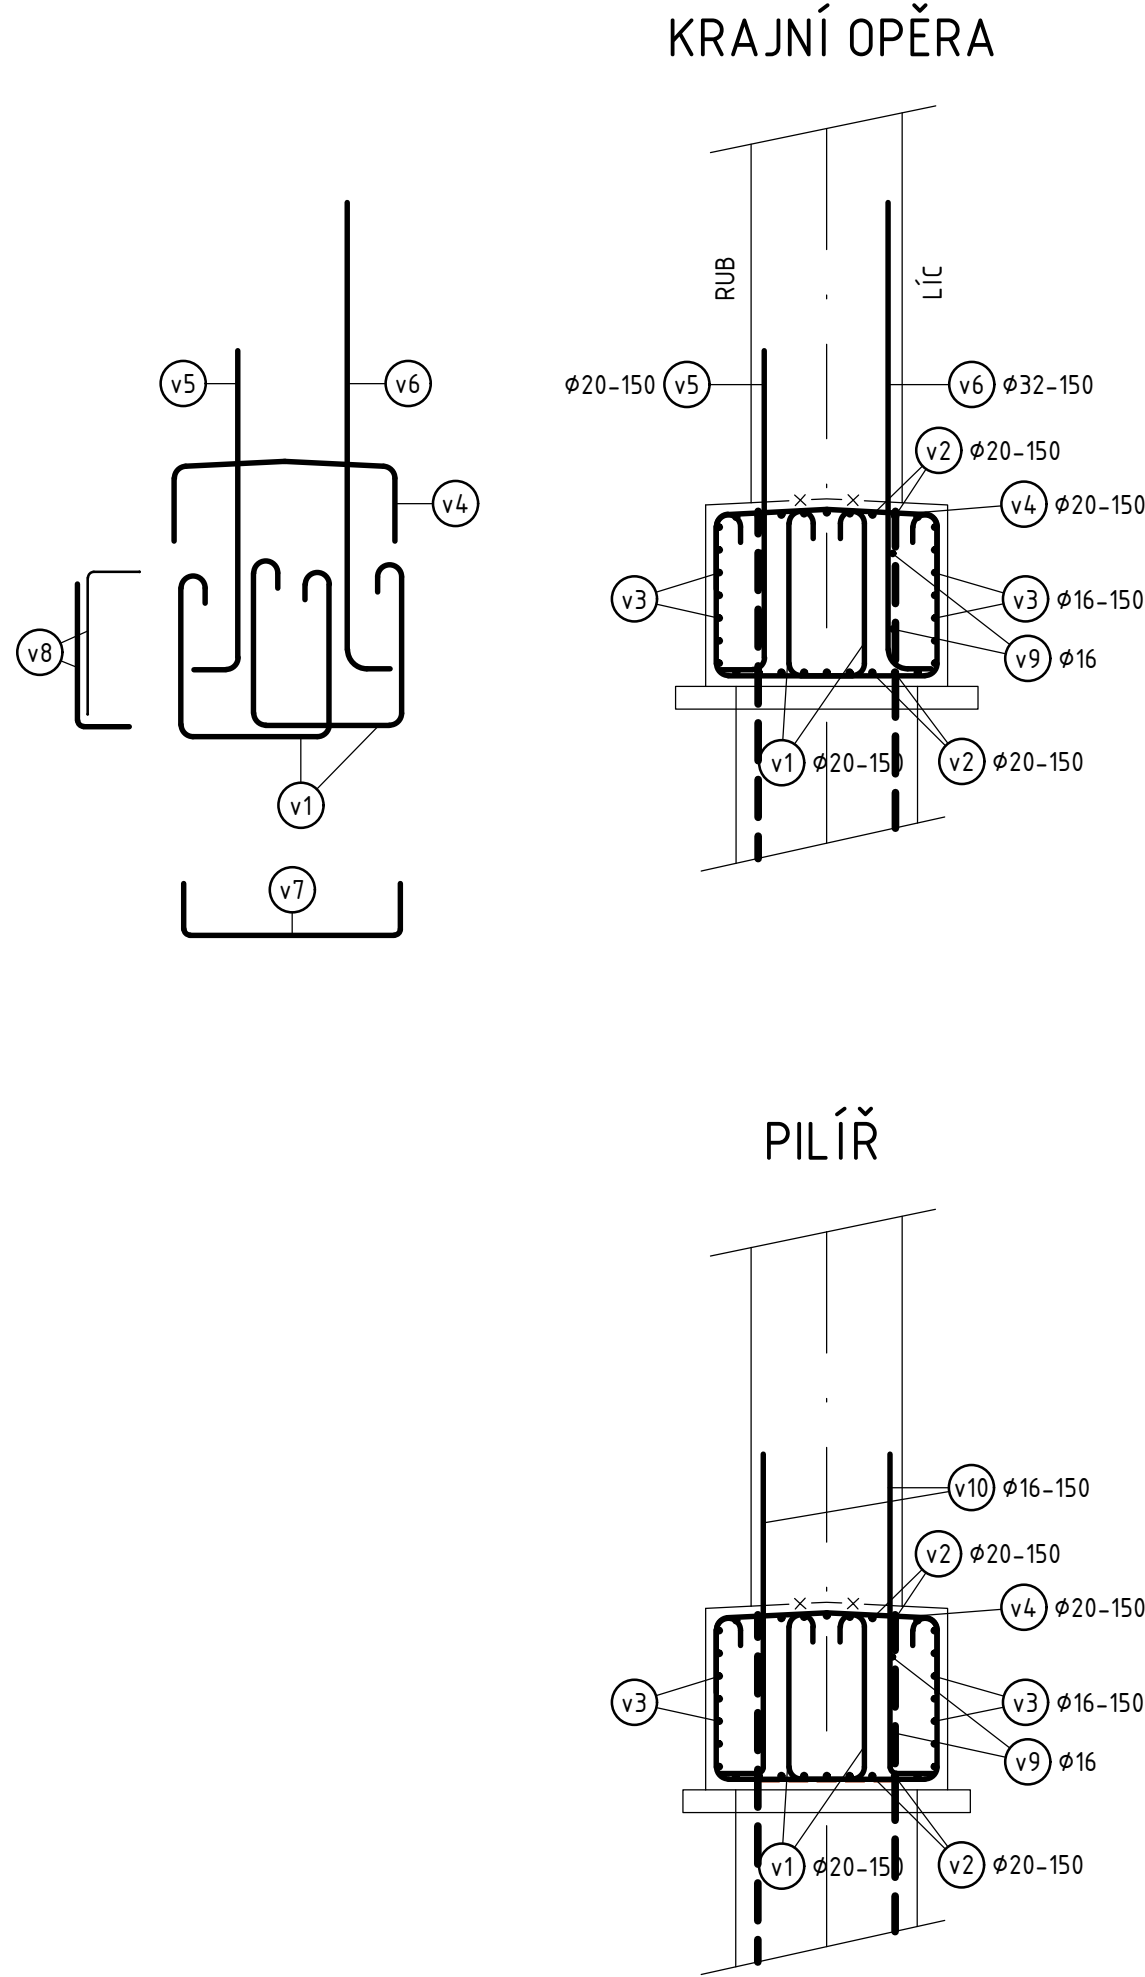

SESTAVA S1

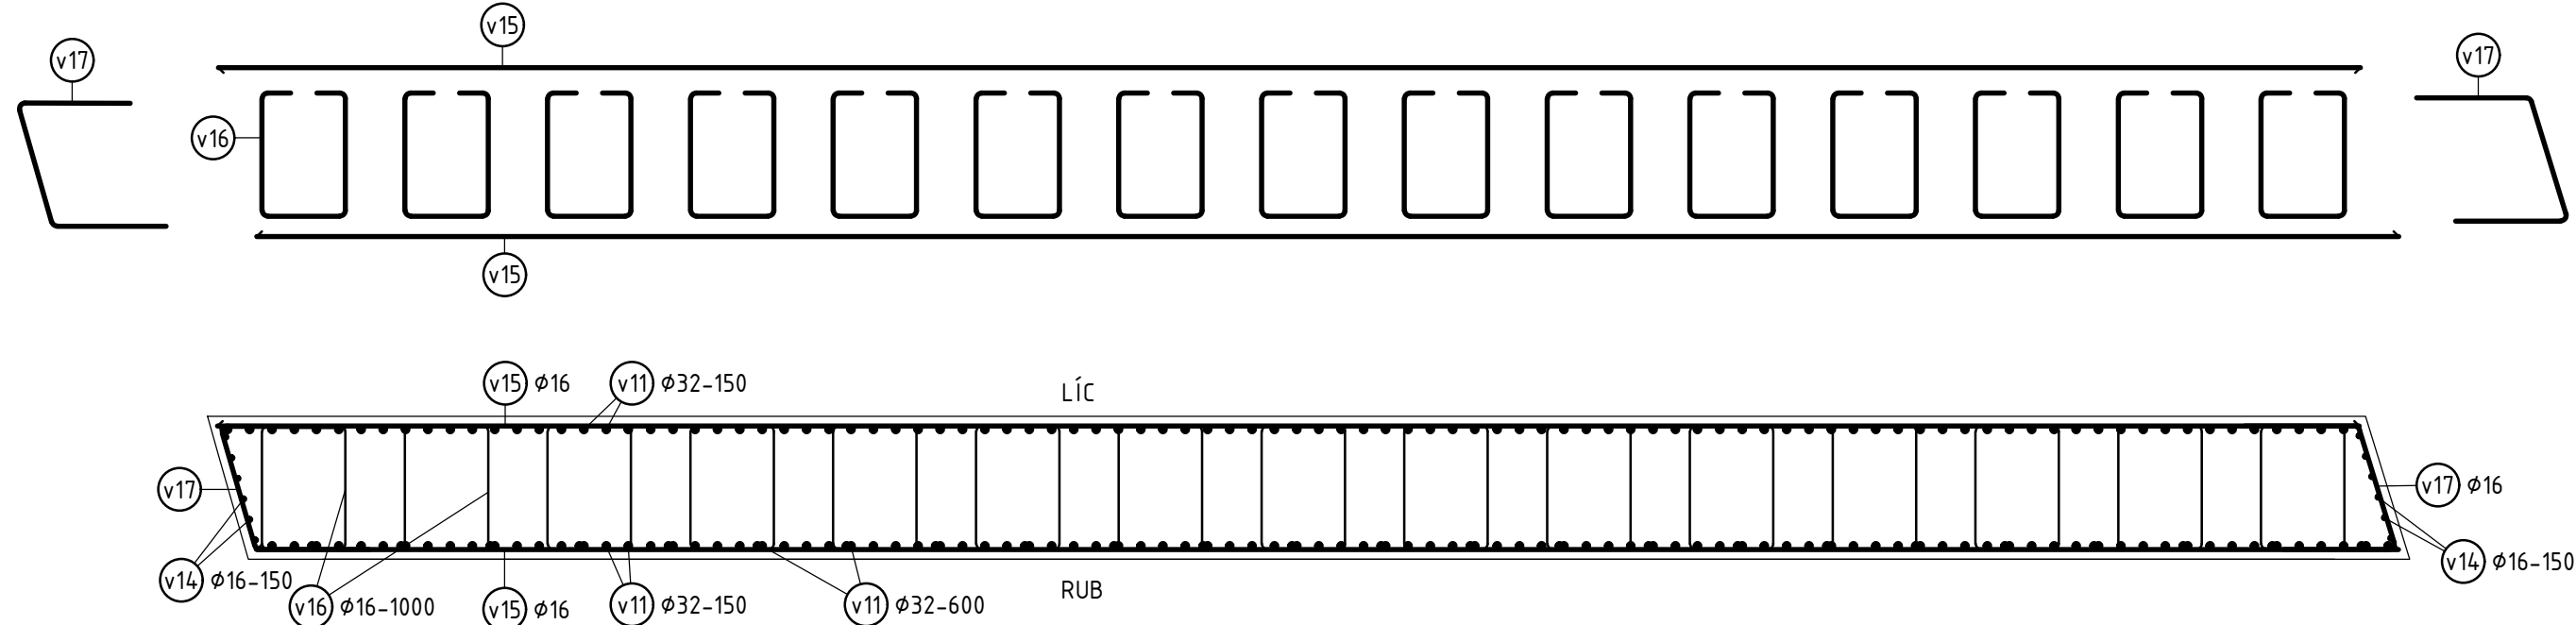


SESTAVA S2

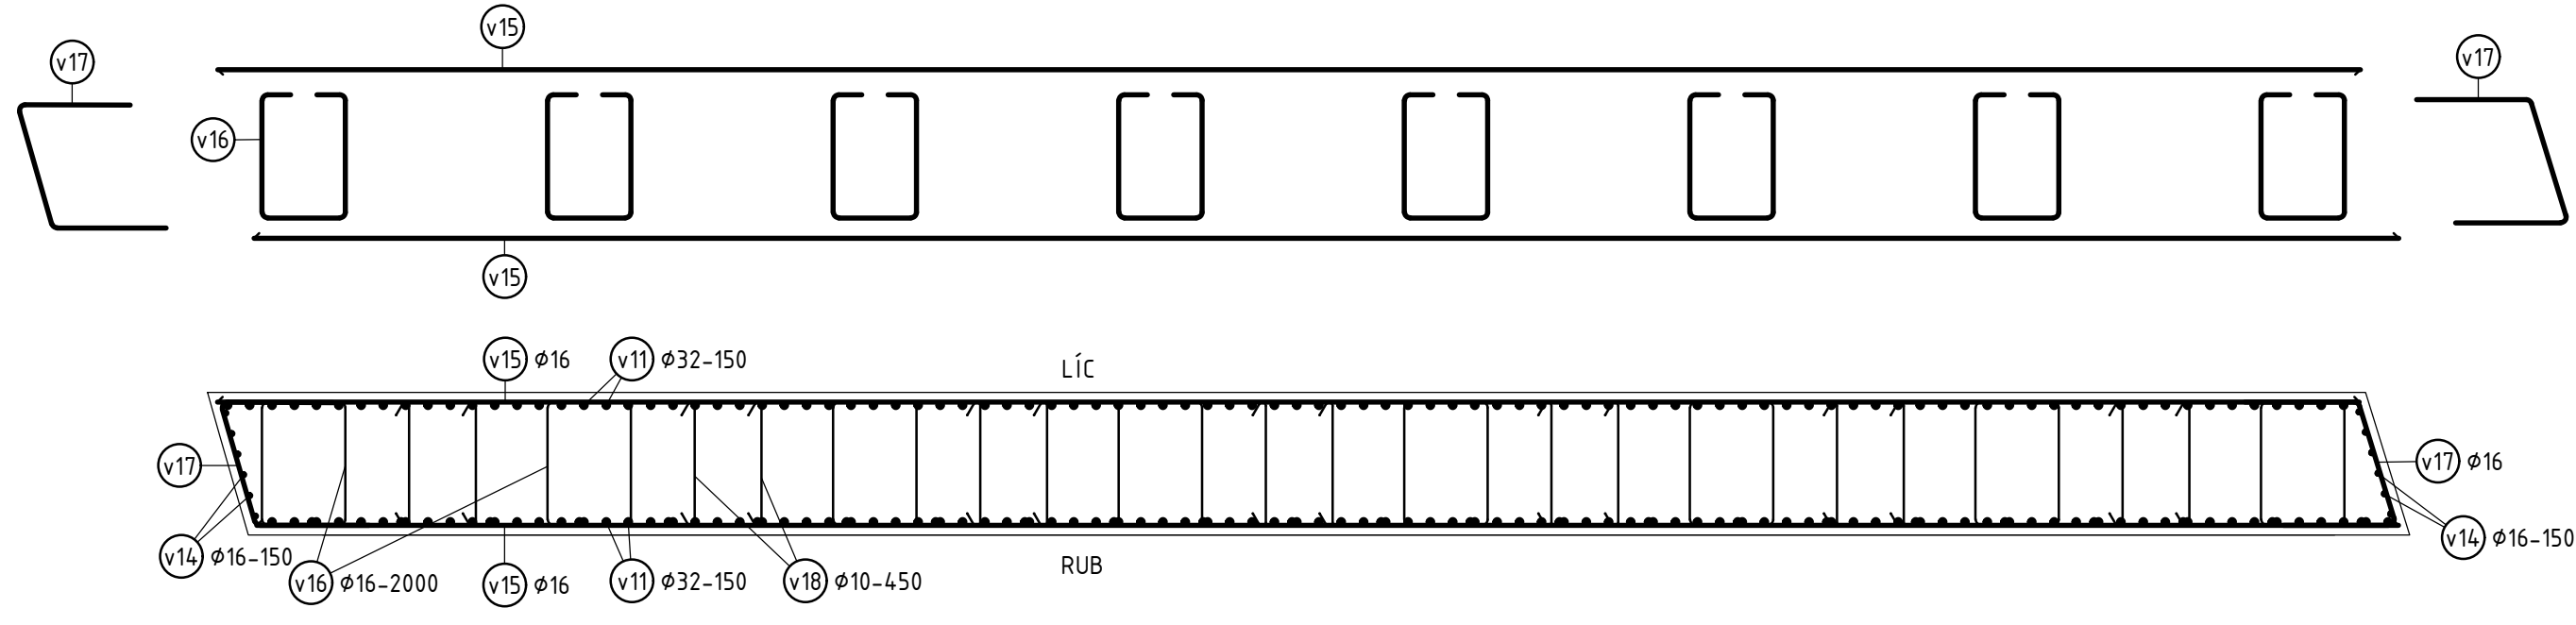


SESTAVA S3

PŮDORYS DŘÍKU PILÍŘE 1:35

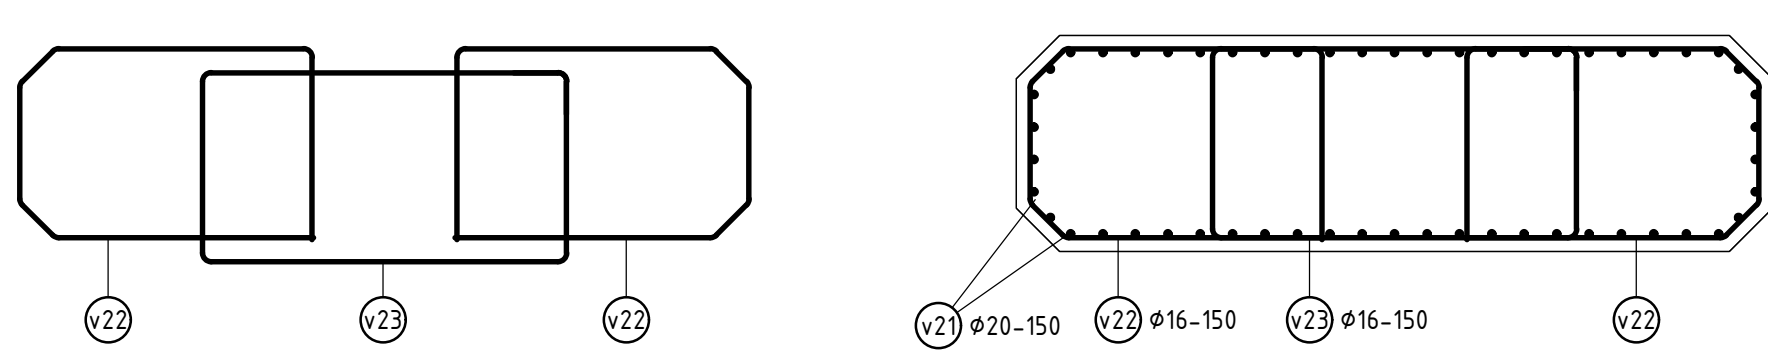

ODHAD MNOŽSTVÍ BETONÁŘSKÉ VÝZTUŽE SO 201	MNOŽSTVÍ VÝZTUŽE V %	MNOŽSTVÍ VÝZT.V KG/M3
VÝZTUŽ PILOT POD OPĚROU 1, D 1200MM	1.46%	114.6
VÝZTUŽ PILOT POD OPĚROU 3, D 1200MM	1.46%	114.6
VÝZTUŽ PILOT POD PILÍŘI, D 1200MM	0.48%	37.7
VÝZTUŽ ZÁKLADŮ OPĚRY 01	2.74%	215.3
VÝZTUŽ ZÁKLADŮ OPĚRY 03	2.74%	215.3
VÝZTUŽ ZÁKLADŮ PILÍŘŮ	1.92%	150.7
VÝZTUŽ PILÍŘŮ	1.27%	99.7
VÝZTUŽ DŘÍKU A KŘÍDEL OPĚRY 01	2.10%	162.0
VÝZTUŽ DŘÍKU A KŘÍDEL OPĚRY 03	2.10%	162.0
VÝZTUŽ NOSNÉ KONSTRUKCE	1.56%	122.5
VÝZTUŽ ŘÍMS	1.64%	128.7
VÝZTUŽ PŘECHODOVÝCH DESEK	1.87%	146.4

ŘEZ KŘÍDLEM 1:50

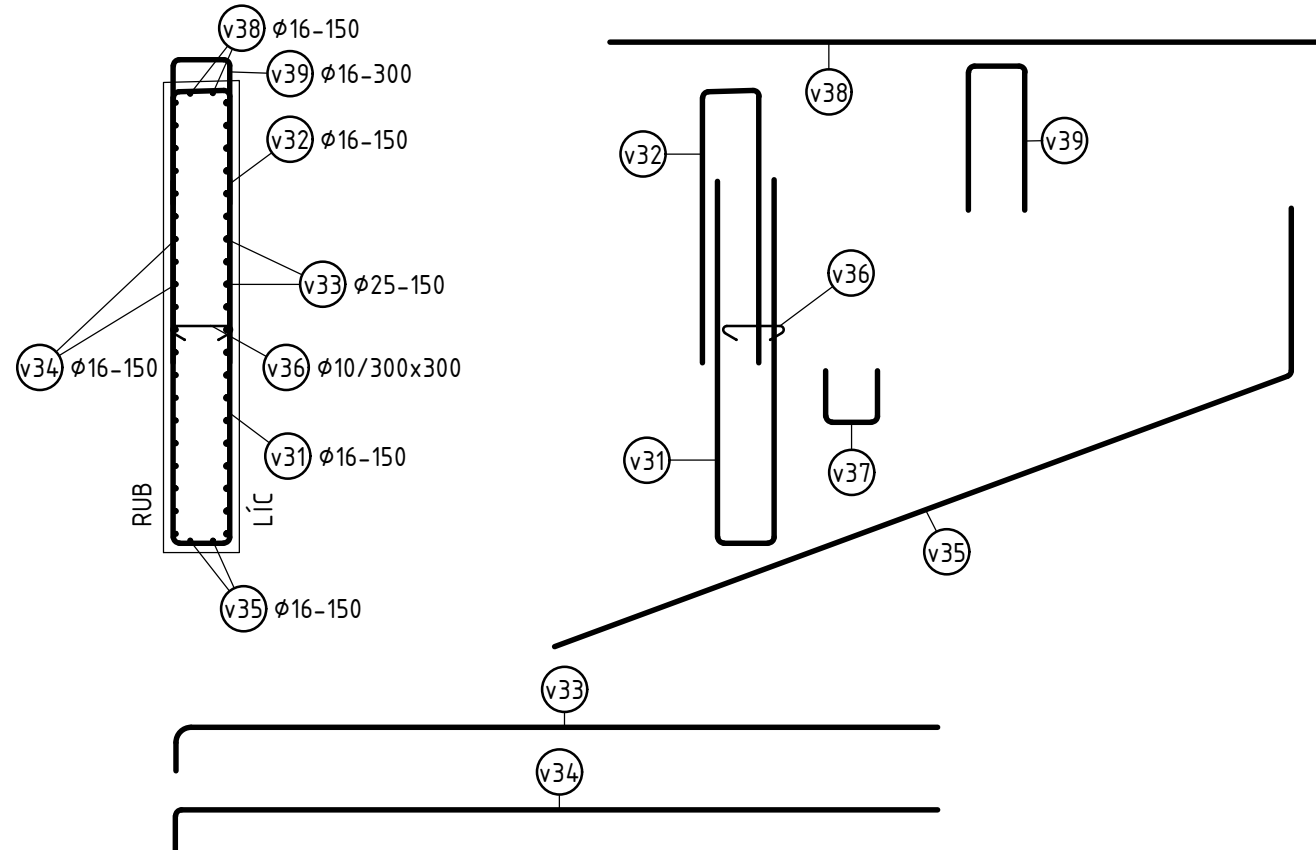

Souřadnicový systém: S-JTSK
Výškový systém: Bpv

SO 201 MOST NA I/16 PŘES MK A ZALUŽANSKOU VODOTEČ V KM 0,228

Objednatel:
ŘEDITELSTVÍ SILNIC A DÁLNIC
Ředitelství silnic a dálnic s. p.
Čerčanská 2023/12, Krč, 140 00 Praha 4

Valbek, spol. s r.o.
Vaňurova 505/17
460 07 Liberec 3

	Vypracoval	M. KNESPLOVÁ	Zak. číslo	21-L113-001	
	Zodp. projektant	ING. S. RŮŽIČKA	Datum	02/2025	
	Tech. kontrola	ING. I. BELDA	Stupeň	PDPS	
	Akce	I/16 MLADÁ BOLESLAV - MARTINOVICE		Počet formátů	8x A4
				Měřítko	-
Zhotovitel:	Příloha	SCHÉMATICKÉ VÝKRESY VÝZTUŽE 1(2)		301	
Valbek, spol. s r.o. Vaňurova 505/17 460 07 Liberec 3			C. přílohy		