

SCHÉMA VÝZTUŽE NOSNÉ KONSTRUKCE
PODÉLNÝ ŘEZ 1:50



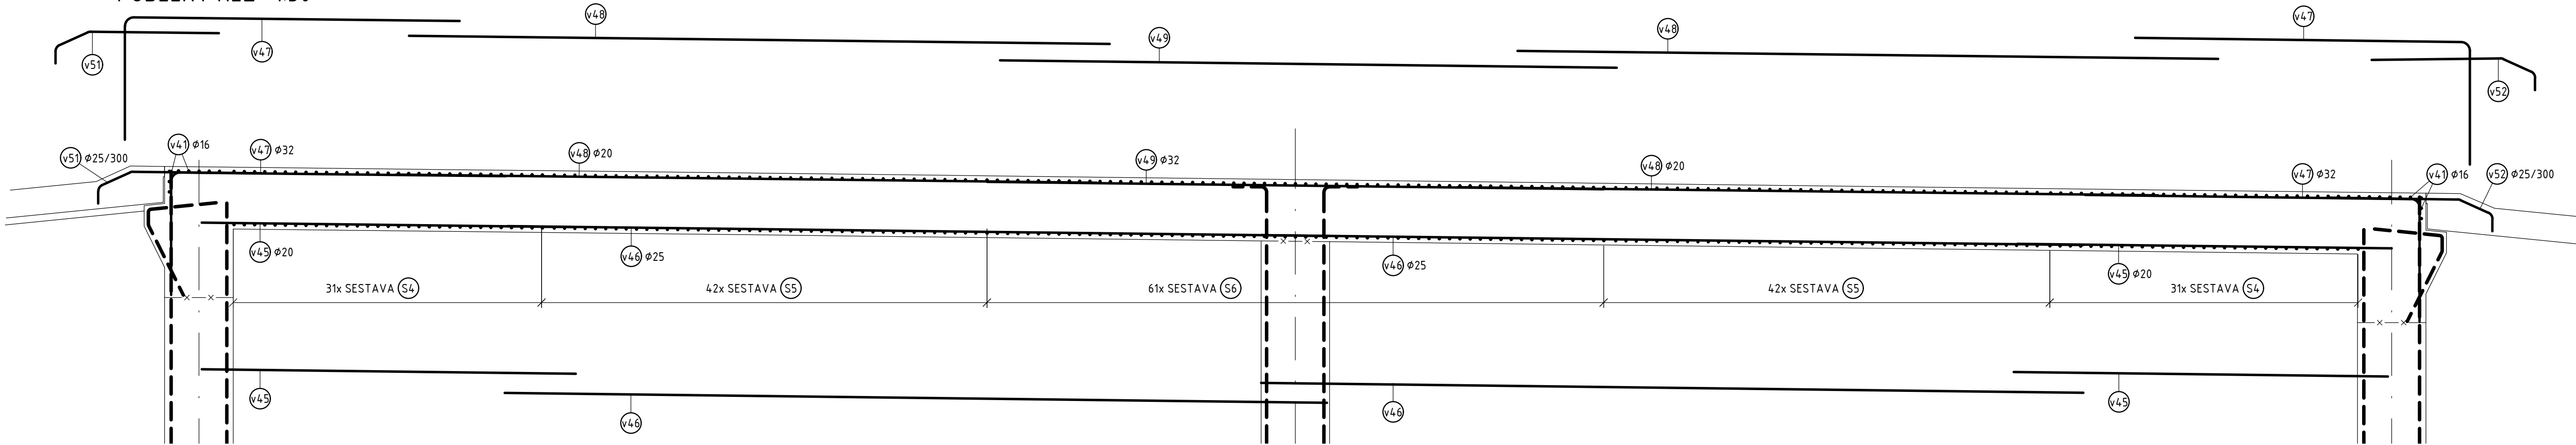



SCHÉMA VÝZTUŽE NOSNÉ KONSTRUKCE
PŘÍČNÝ ŘEZ NAD OPĚROU 1:50

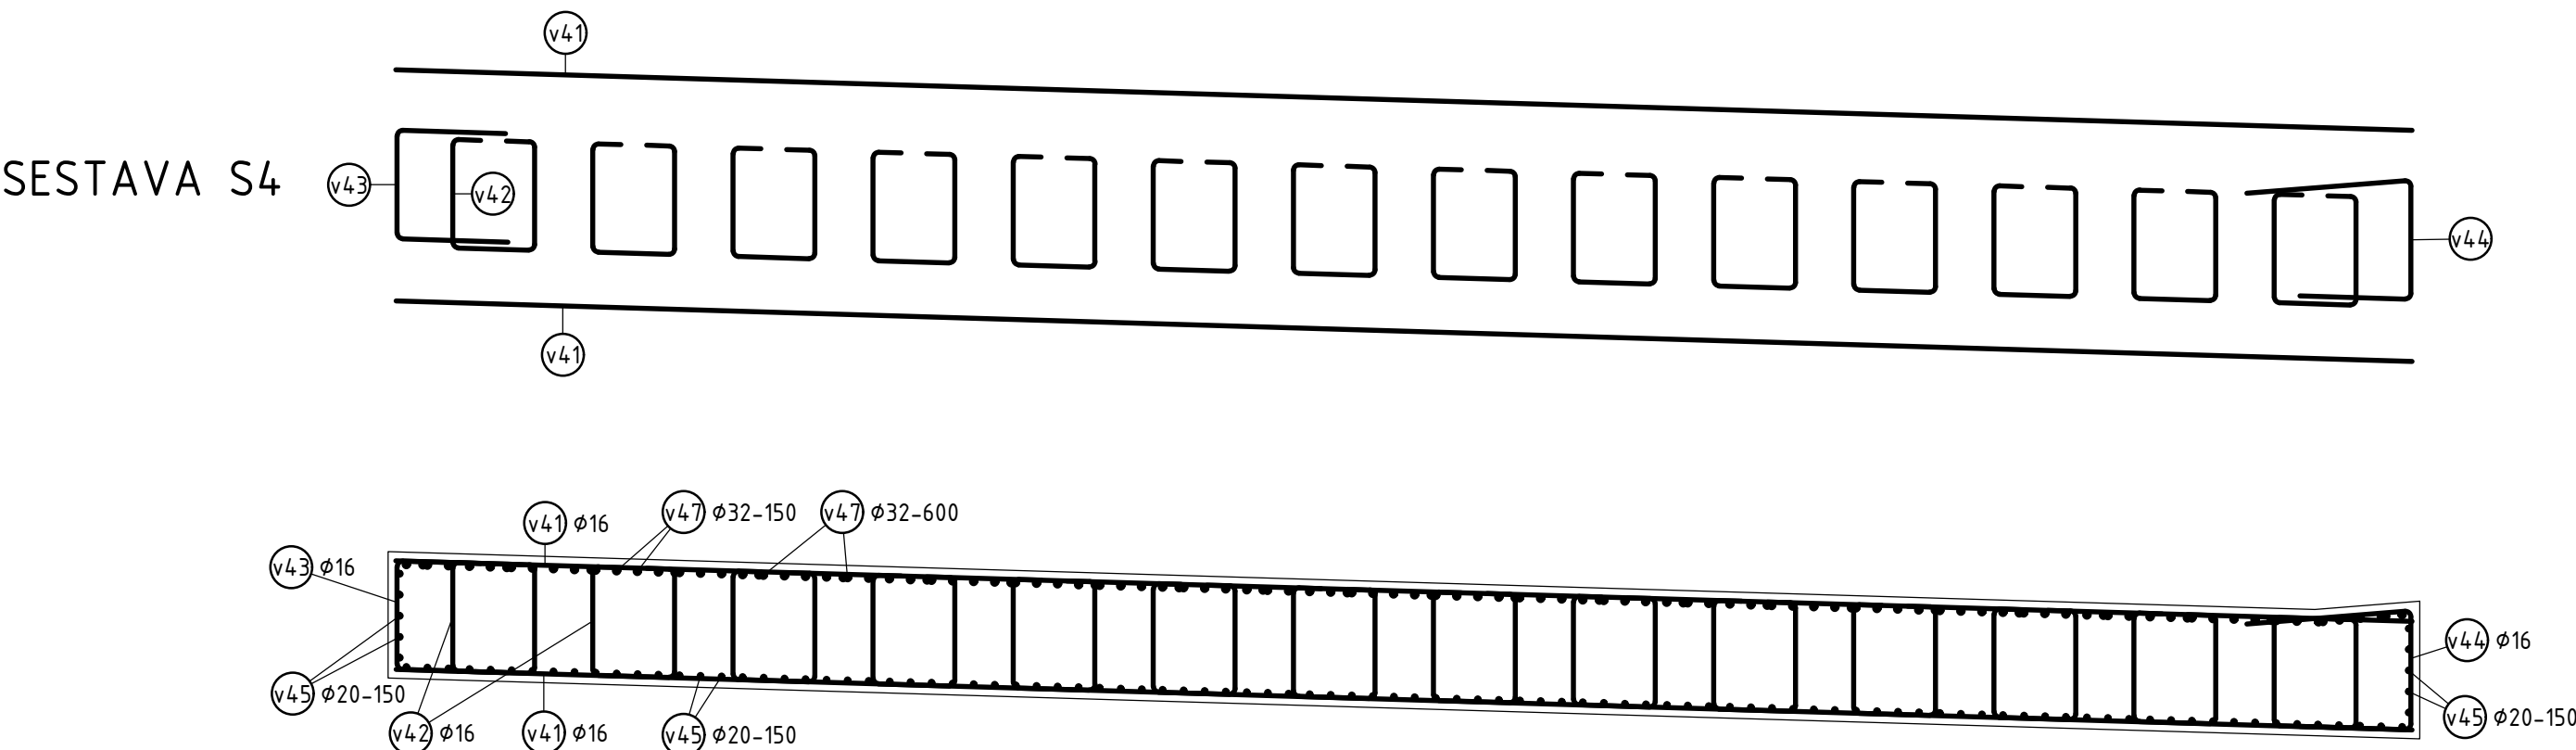

PŘÍČNÝ ŘEZ V POLI 1:50

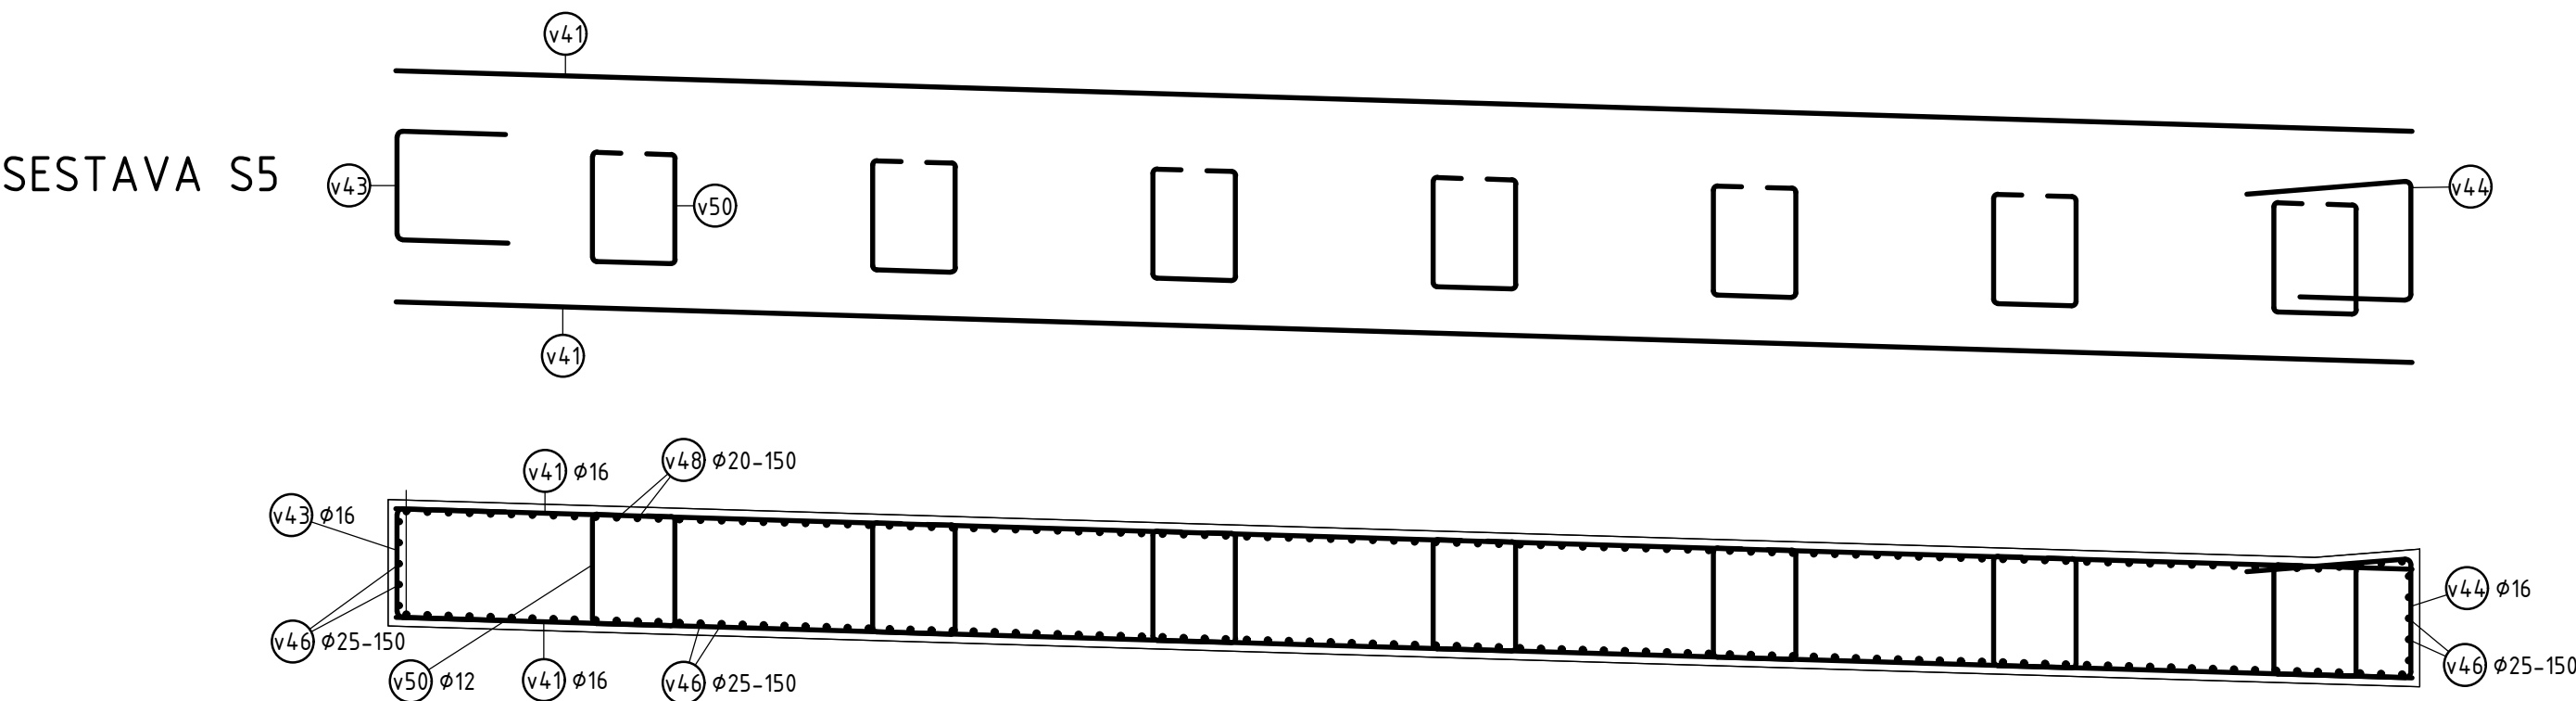

PŘÍČNÝ ŘEZ NAD PODPOROU 1:50

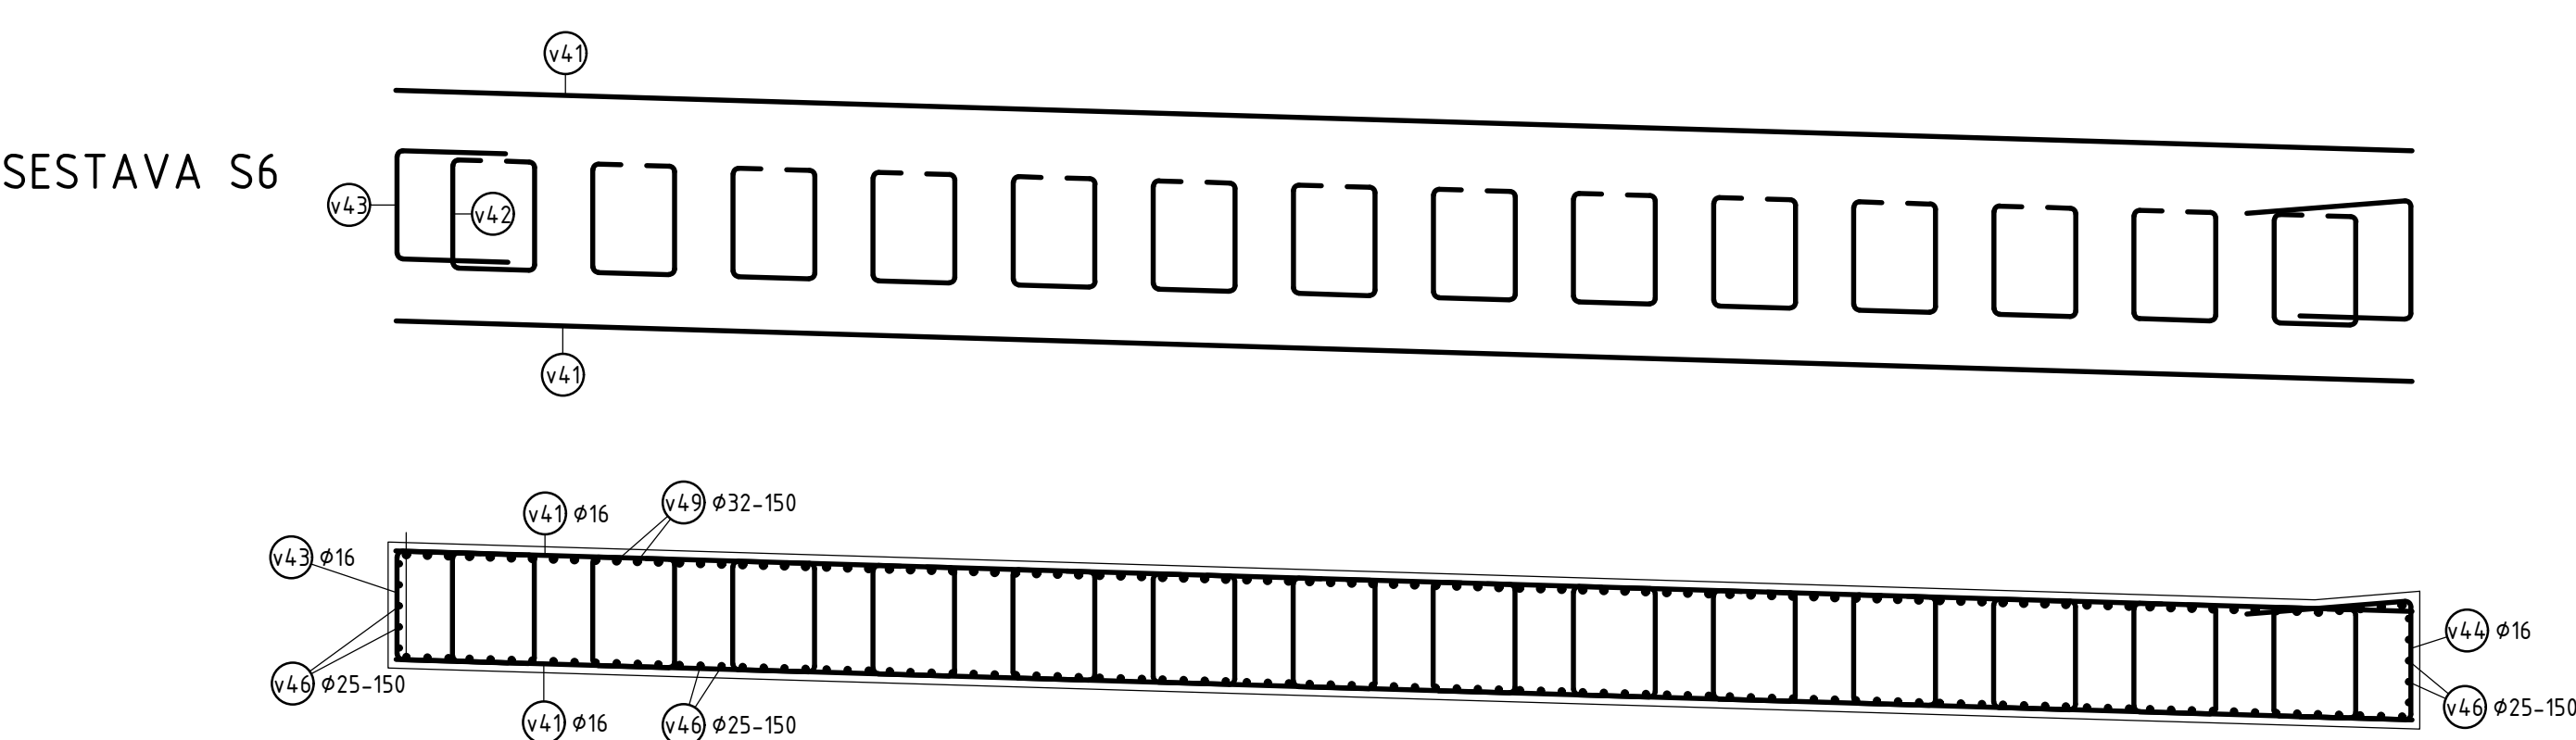

Souřadnicový systém: S-JTSK
Výškový systém: Bpv

SO 201

MOST NA I/16 PŘES MK A ZALUŽANSKOU VODOTEČ V KM 0,228

Objednatel:



ŘEDITELSTVÍ
SILNIC
A DÁLNIC

Ředitelství silnic a dálnic s. p.
Čerčanská 2023/12, Krč, 140 00 Praha 4



Valbek

Valbek, spol. s r.o.

Vaňurova 505/17
460 07 Liberec 3



Valbek

Vypracoval

M. KNĚSPLOVÁ

Zodp. projektant

ING. S. RUŽIČKA

Tech. kontrola

ING. I. BELDÁ

Akce

I/16 MLADÁ BOLESLAV - MARTINOVICE

Zhotovitel:

Valbek, spol. s r.o.
Vaňurova 505/17
460 07 Liberec 3

Zak. číslo

21-LI13-001

Datum

02/2025

Stupeň

PDPS

Počet formátů

8x A4

Měřítka

-

Č. přílohy

Paré

302

SCHÉMATICKÉ VÝKRESY VÝZTUŽE 2(2)