


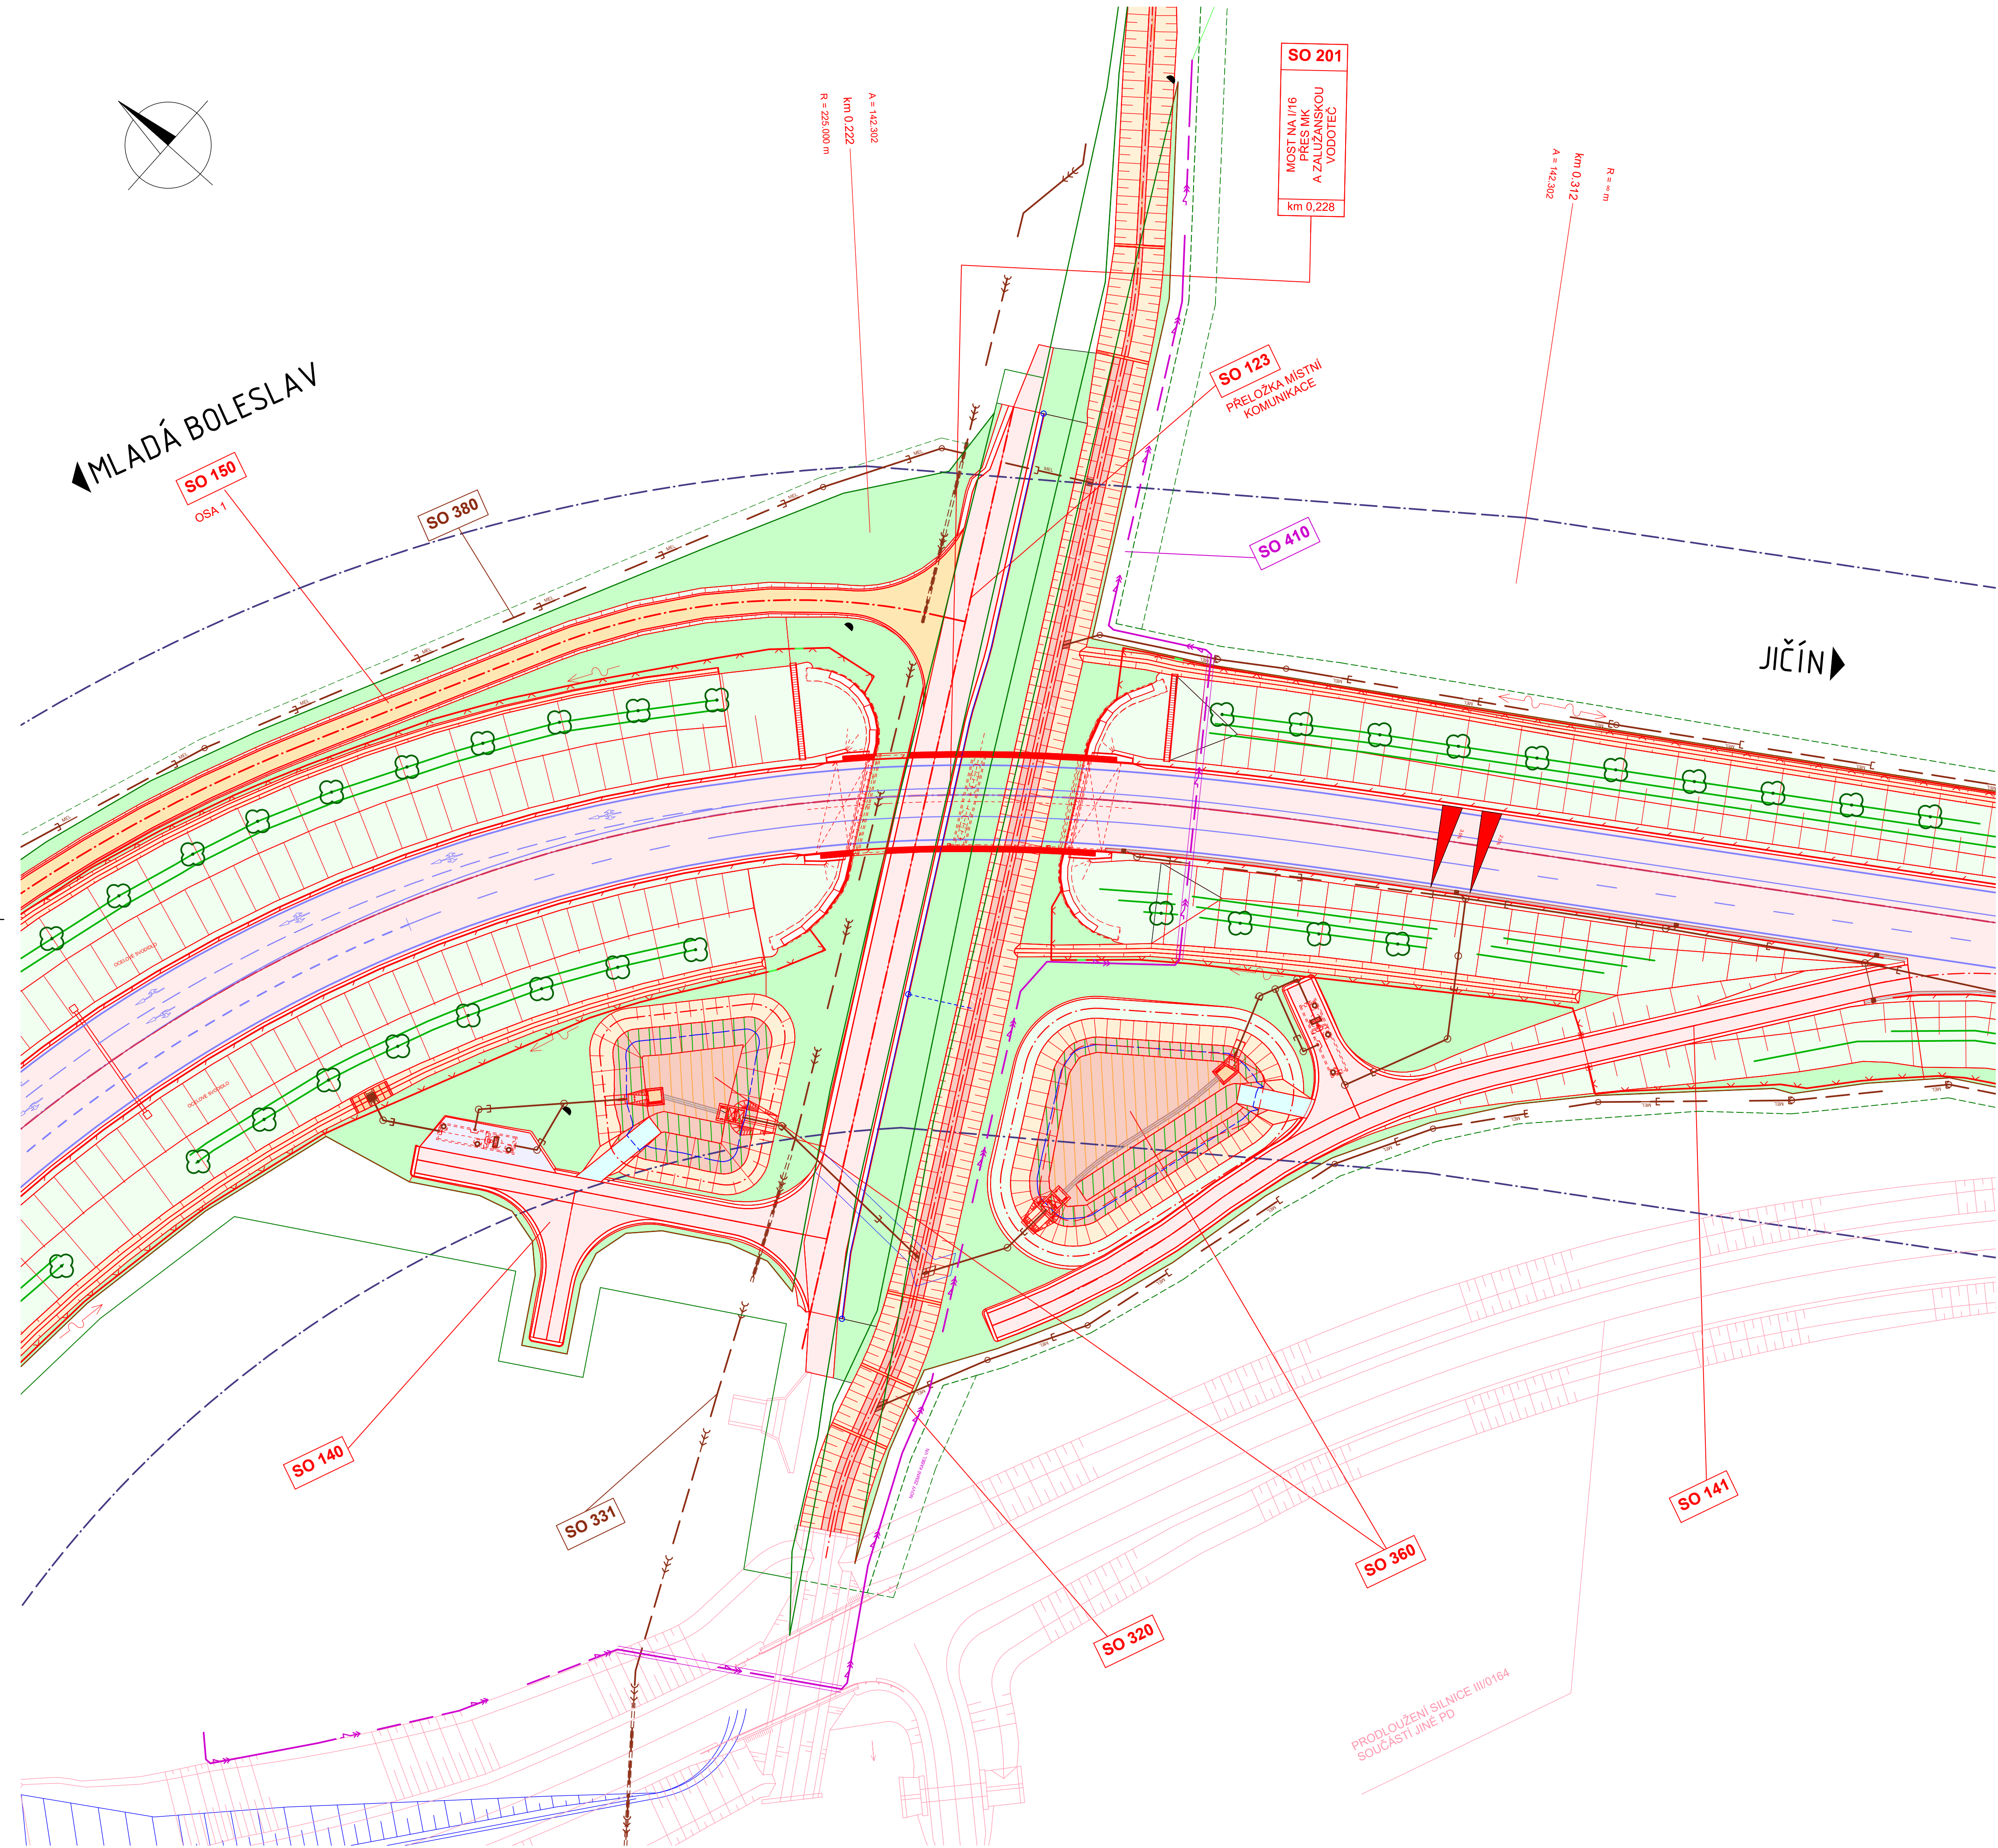

Souřadnicový systém: S-JTSK
Výškový systém: Bpv

SO 201 MOST NA I/16 PŘES MK A ZALUŽANSKOU VODOTEČ V KM 0,228

Objednatel:



Ředitelství silnic a dálnic s. p.
Čerčanská 2023/12, Krč, 140 00 Praha 4



Valbek, spol. s r.o.
Vaňurova 505/17
460 07 Liberec 3



Vypracoval	ING. S. RŮŽIČKA	<i>Ing. S. Růžička</i>	Zak. číslo	21-L113-001
Zodp. projektant	ING. S. RŮŽIČKA	<i>Ing. S. Růžička</i>	Datum	02/2025
Tech. kontrola	ING. I. BELDA	<i>Ing. I. Belda</i>	Stupeň	PDPS
Akce	I/16 MLADÁ BOLESLAV - MARTINOVICE		Počet formátů	8x A4
			Měřítko	1:500
			Č. přílohy	Paré
Zhotovitel:	Příloha		401	
Valbek, spol. s r.o. Vaňurova 505/17 460 07 Liberec 3	PŘEHLEDNÁ SITUACE			