



PŮDORYS 1:150

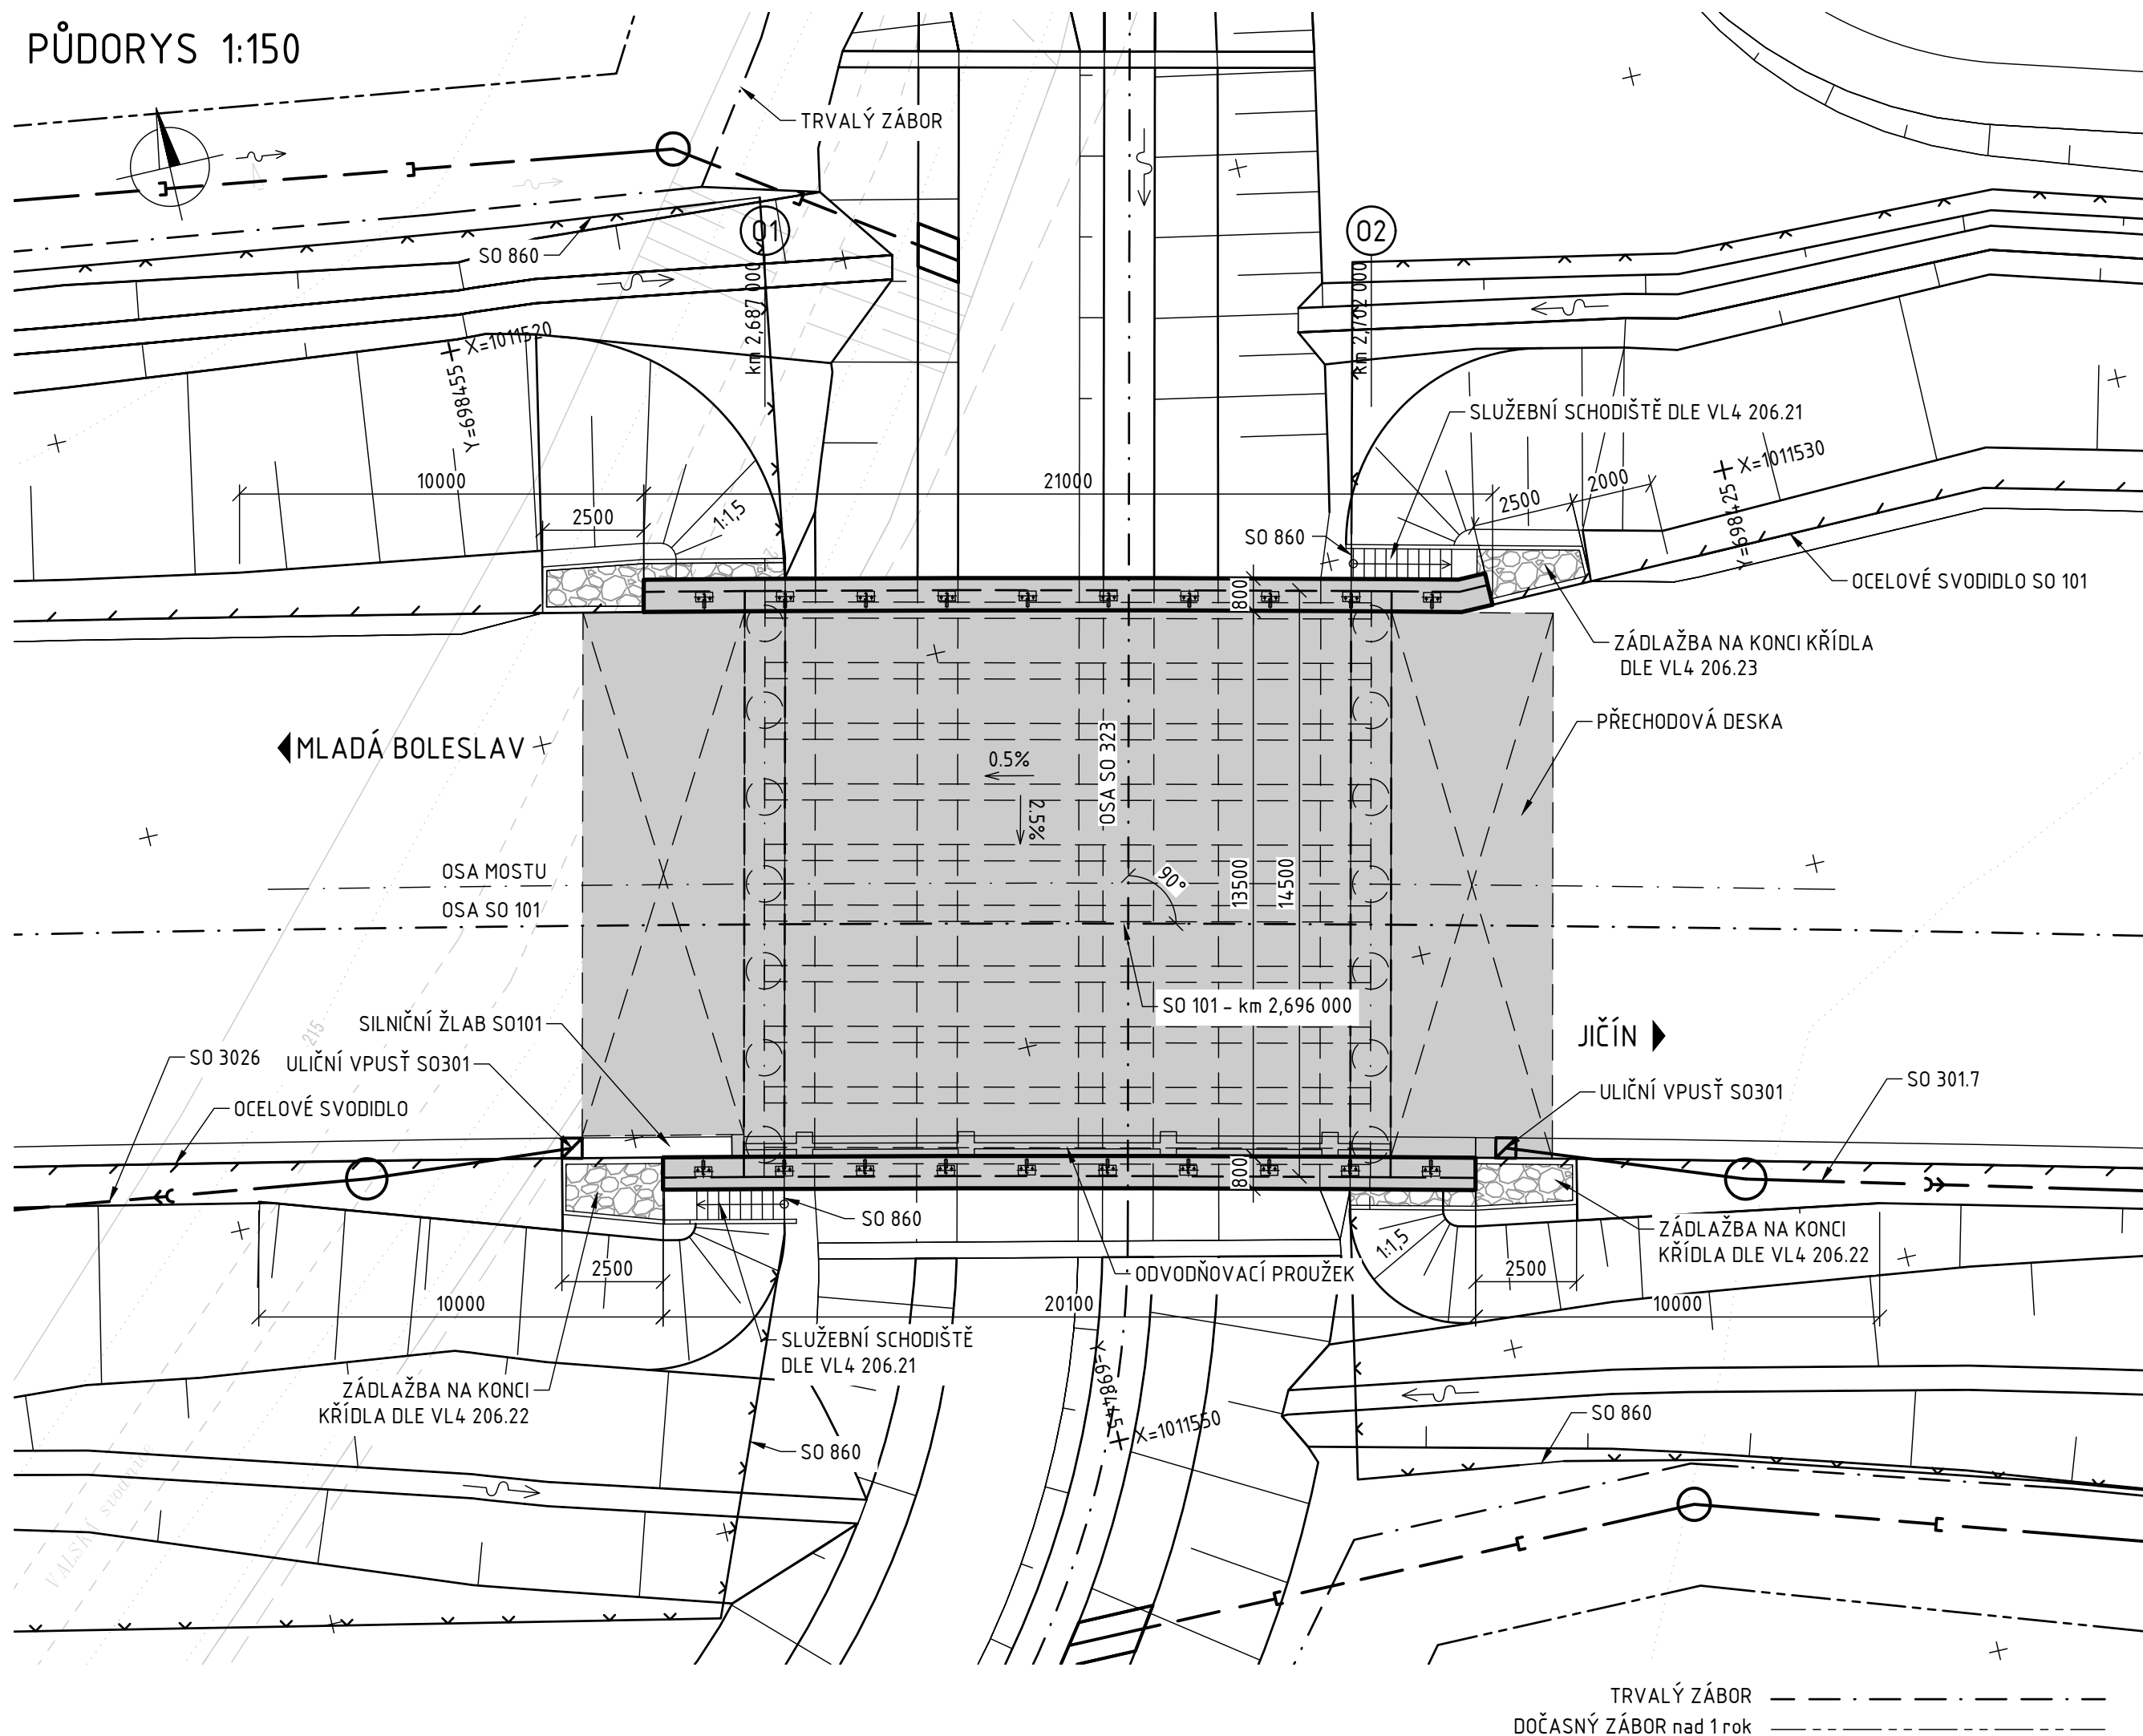


PODÉLNÝ ŘEZ 1:150

OSOU SO 101

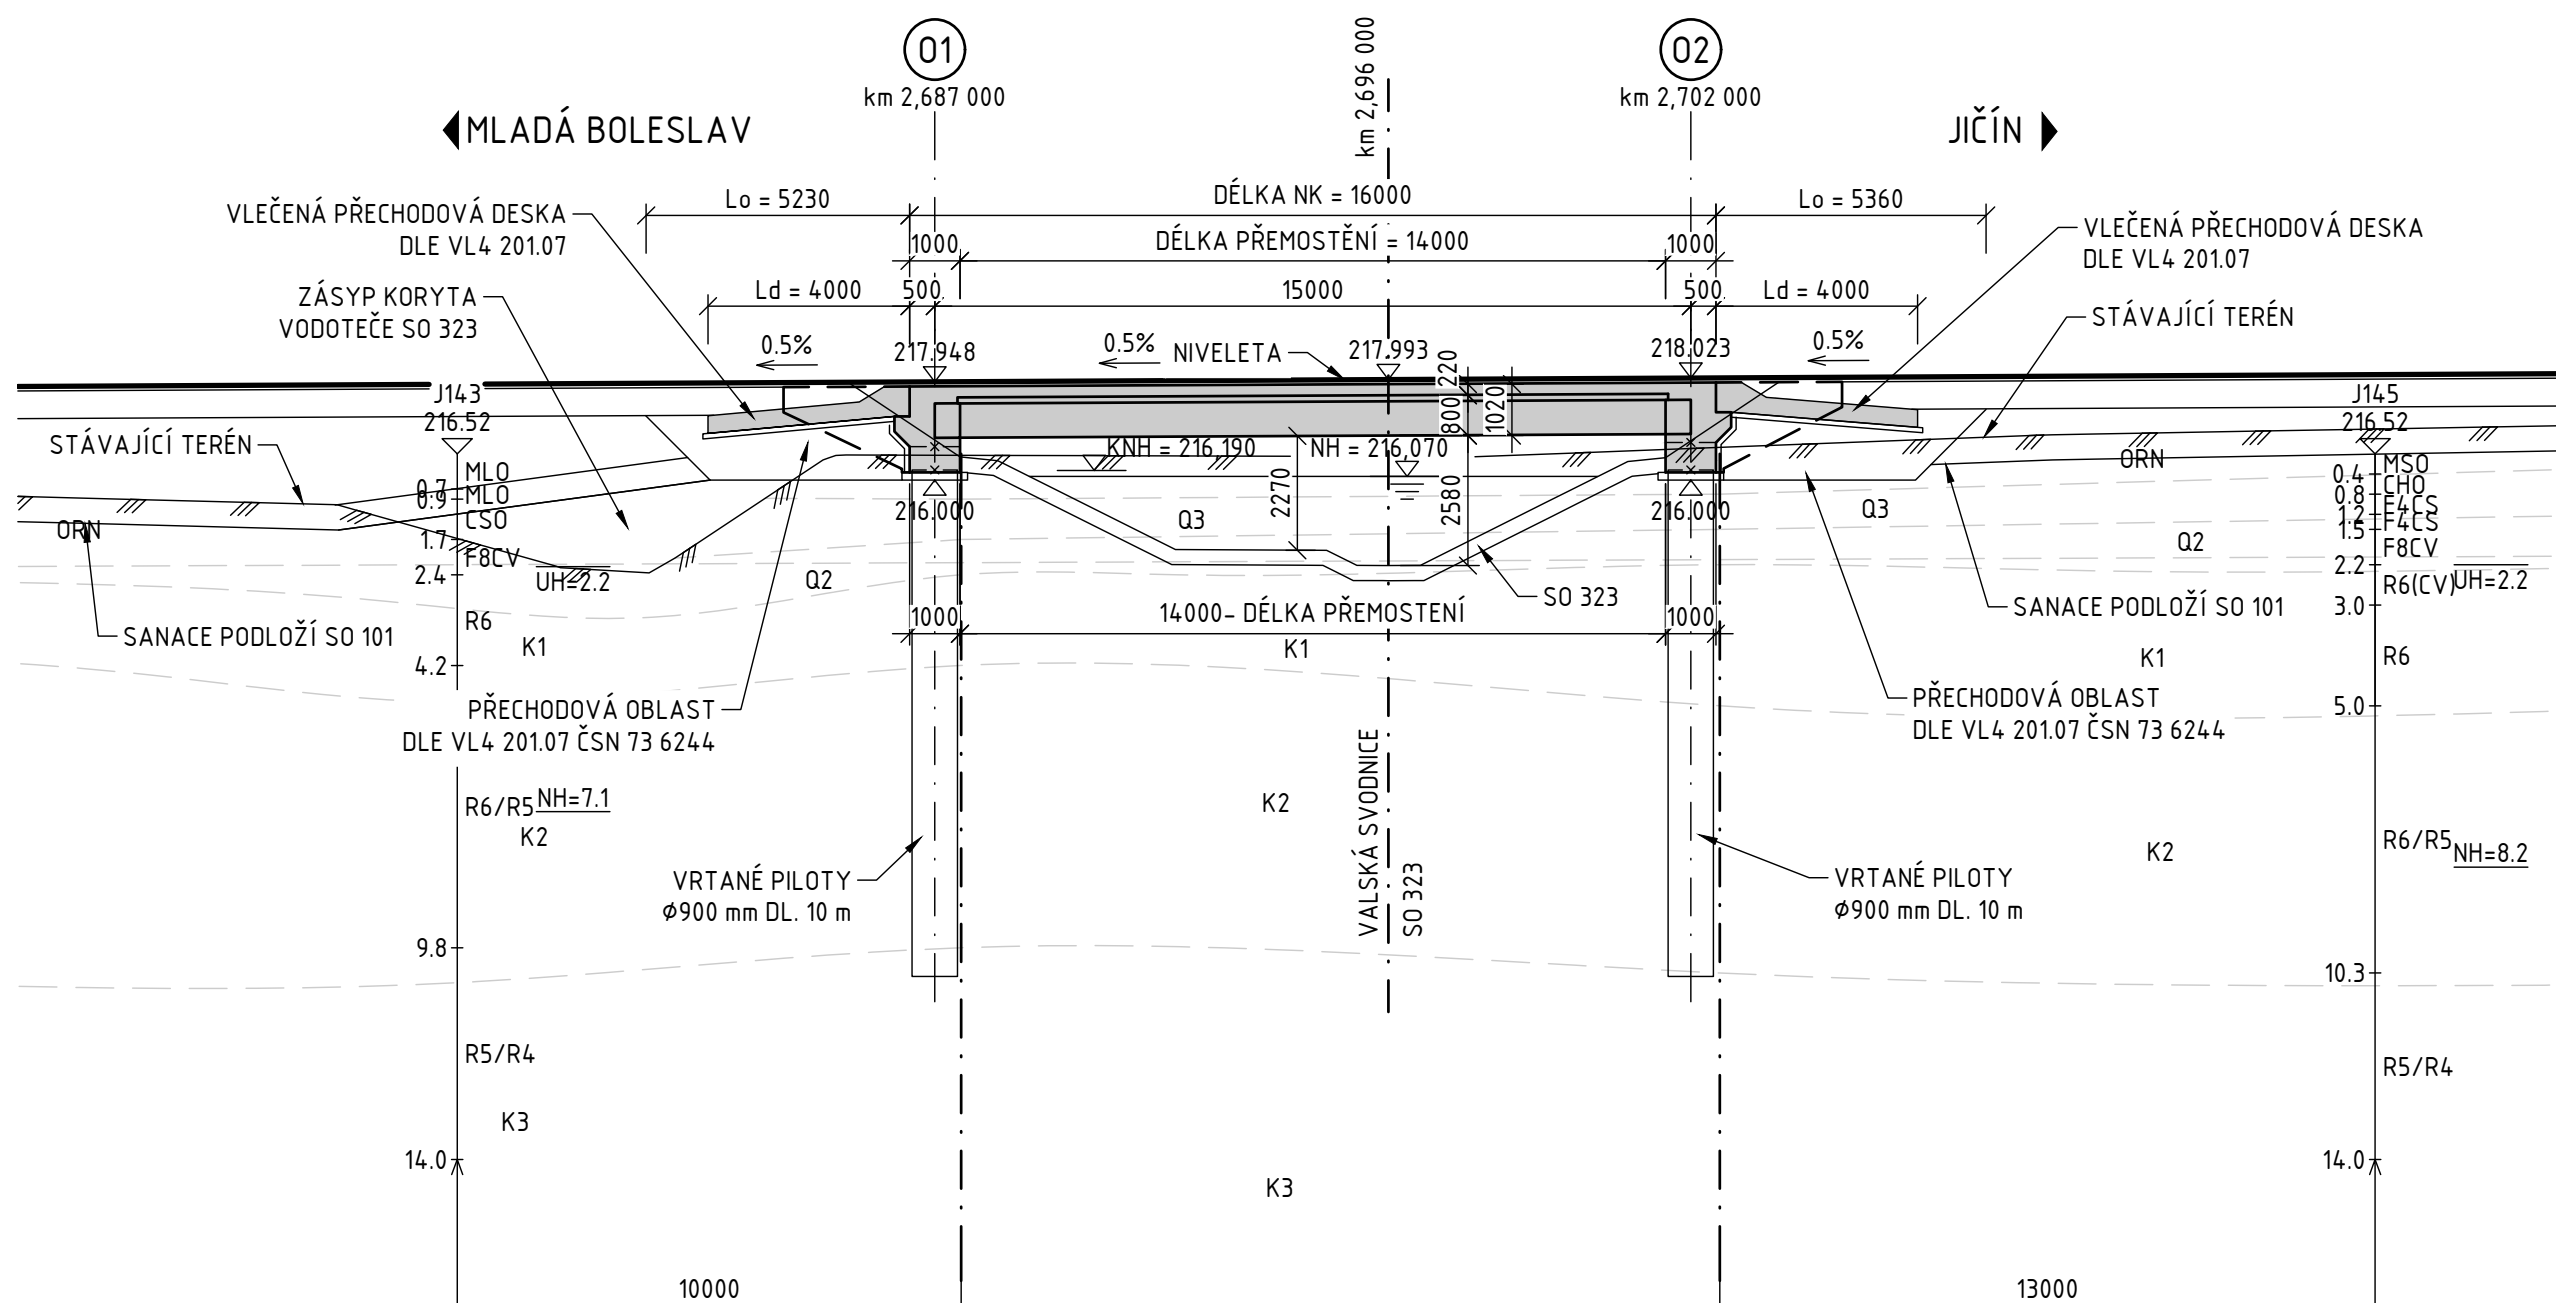


VZOROVÝ PŘÍČNÝ ŘEZ 1:75

-V POLI

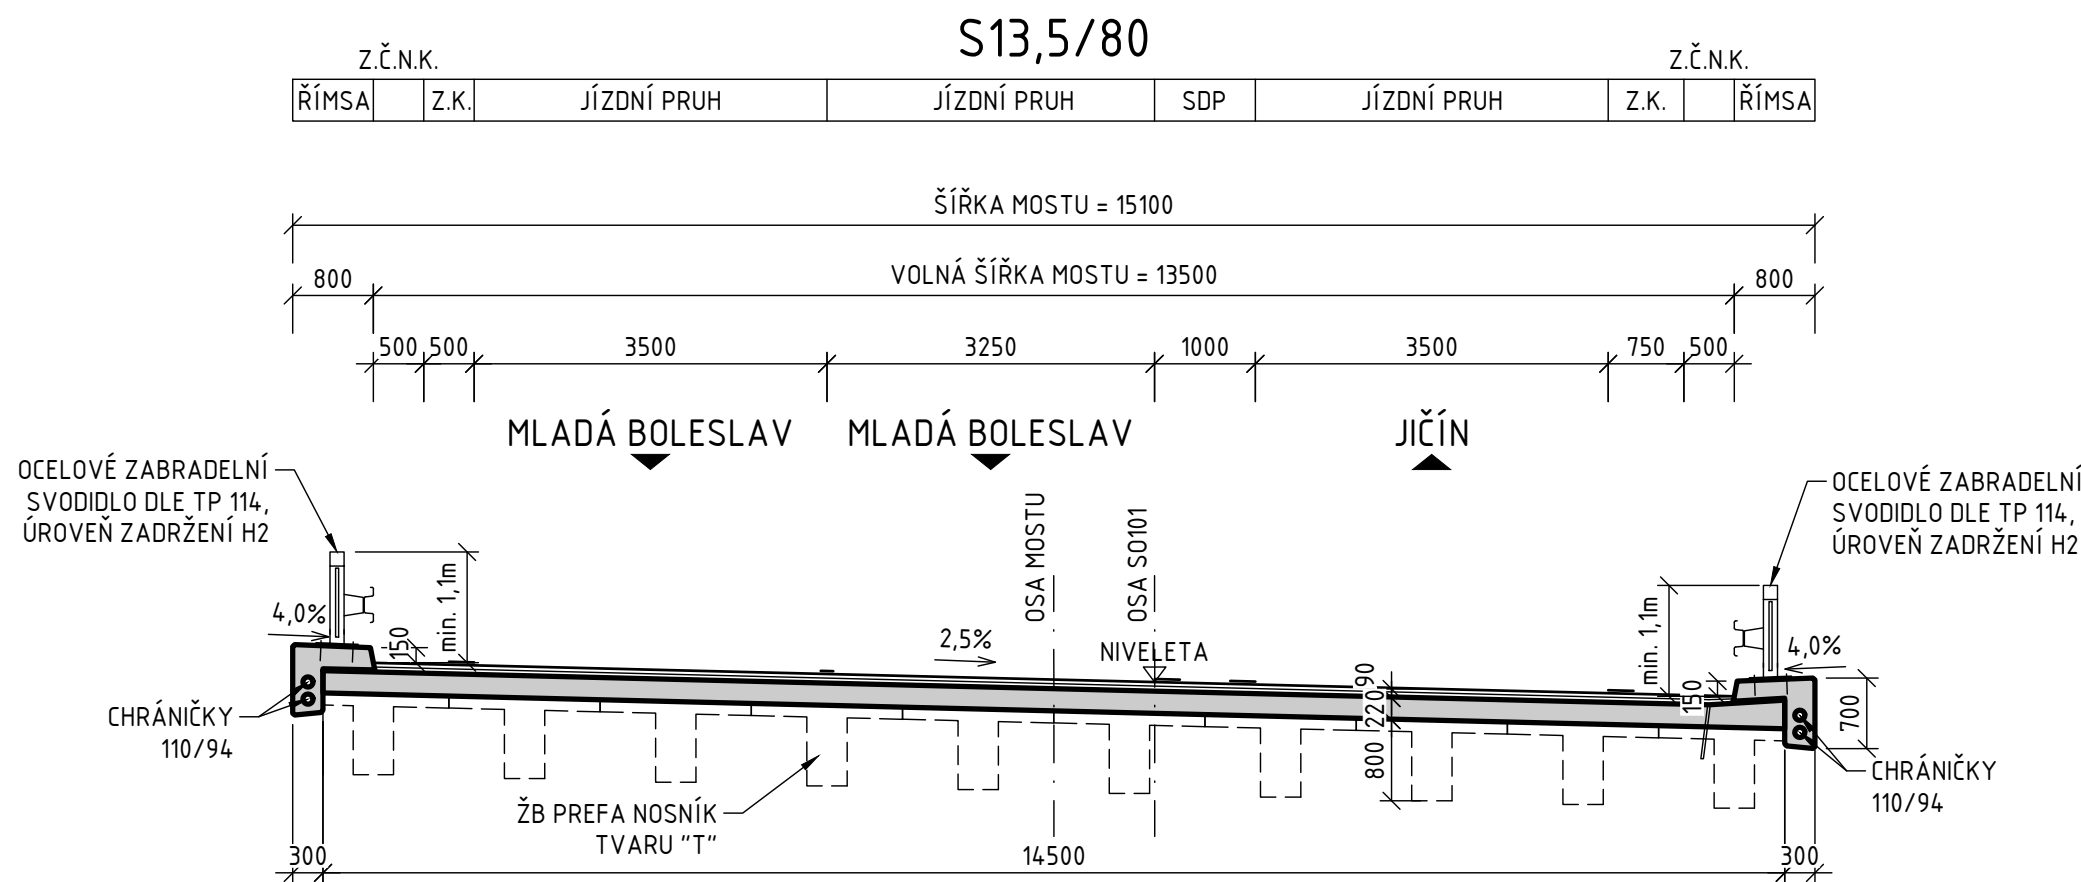

VÝŠKOVÉ VEDENÍ SO 101

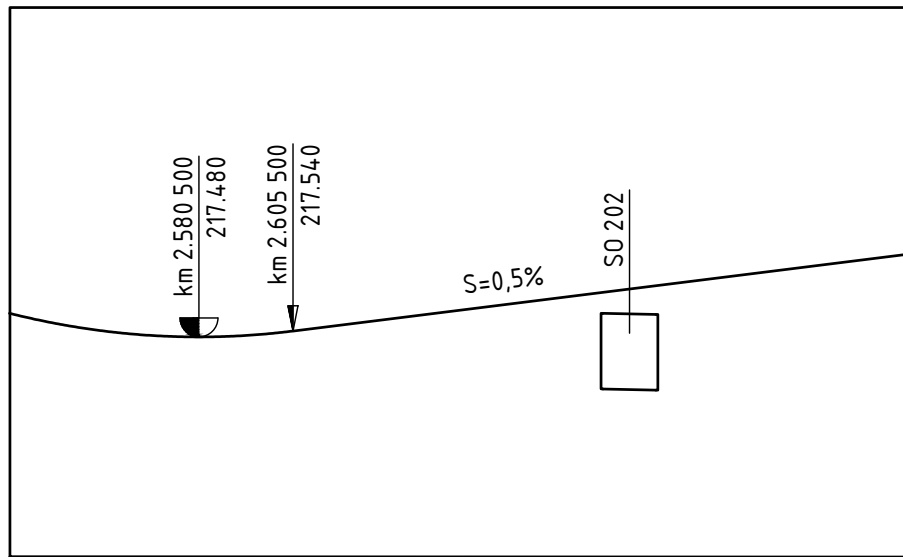

SMĚROVÉ VEDENÍ SO 101

STANIČNÍ	X	Y	PARAMETR
km 2.637 88	698 498.761	1 011 525.684	R = 1200 m
km 2.979 39	698 176.153	1 011 634.168	

POZNÁMKY:

- NEJEDNOU SOUČÁSTI VÝKRESU JSOU POZNÁMKY A SPECIFIKACE UVEDENÉ NA VÝKRESE POZNÁMEK A TECHNICKÝCH SPECIFIKACÍ

SOUVISEJÍCÍ OBJEKTY:

- SO 020 PŘÍPRAVA ÚZEMÍ
- SO 101 SILNICE I/16 MLADÁ BOLESLAV - MARTINOVICE
- SO 122 PŘELOŽKA SILNICE III/27612 V KM 6,080
- SO 144 PŘÍJEZD K DUN V KM 2,600
- SO 145 PŘÍJEZD K DUN V KM 2,760
- SO 190 DOPRAVNÍ ZNAČENÍ
- SO 301.x ODVODNĚNÍ I/16
- SO 343 PŘELOŽKA VODOVODU PVC 160 V KM 6,091
- SO 323 ÚPRAVA VALSKÉ SVODNICE
- SO 461 PŘELOŽKA VEDENÍ SEK CETIN KM 6,070-6,087
- SO 801 VEGETAČNÍ ÚPRAVY
- SO 810 KÁČENÍ ZELENĚ
- SO 830 REKULTIVACE PLOCH DOČASNÉHO ZÁBORU
- SO 860 OPLOČENÍ

MĚŘÍTKO 0.75 0 0.75 1.5 2.25 3 3.75 4.5 5.25 6 6.75 7.5m
1: 75

MĚŘÍTKO 1.5 0 1.5 3 4.5 6 7.5 9 10.5 12 13.5 15m
1: 150

Souřadnicový systém: S-JTSK
Výškový systém: Bpv

SO 202 MOST NA I/16 PŘES VALSKOU SVODNICI V KM 2,695

Objednatel:



Ředitelství silnic a dálnic s. p.
Čerčanská 2023/12, Krč, 140 00 Praha 4



Valbek, spol. s r.o.
Vaňurova 505/17
460 07 Liberec 3



Vypracoval	ING. O. BAKHMET	Zak. číslo	21-L113-001
Zodp. projektant	ING. O. BAKHMET	Datum	02/2025
Tech. kontrola	ING. I. BELDA	Stupeň	PDPS
Akce	I/16 MLADÁ BOLESLAV - MARTINOVICE	Počet formátů	8x A4
		Měřítko	1:150,75
Zhotovitel:	Příloha	Č. přílohy	Paré

Valbek, spol. s r.o.
Vaňurova 505/17
460 07 Liberec 3

**PŮDORYS, PODÉLNÝ ŘEZ,
VZOROVÝ PŘÍČNÝ ŘEZ**

102