



PŮDORYS 1:100

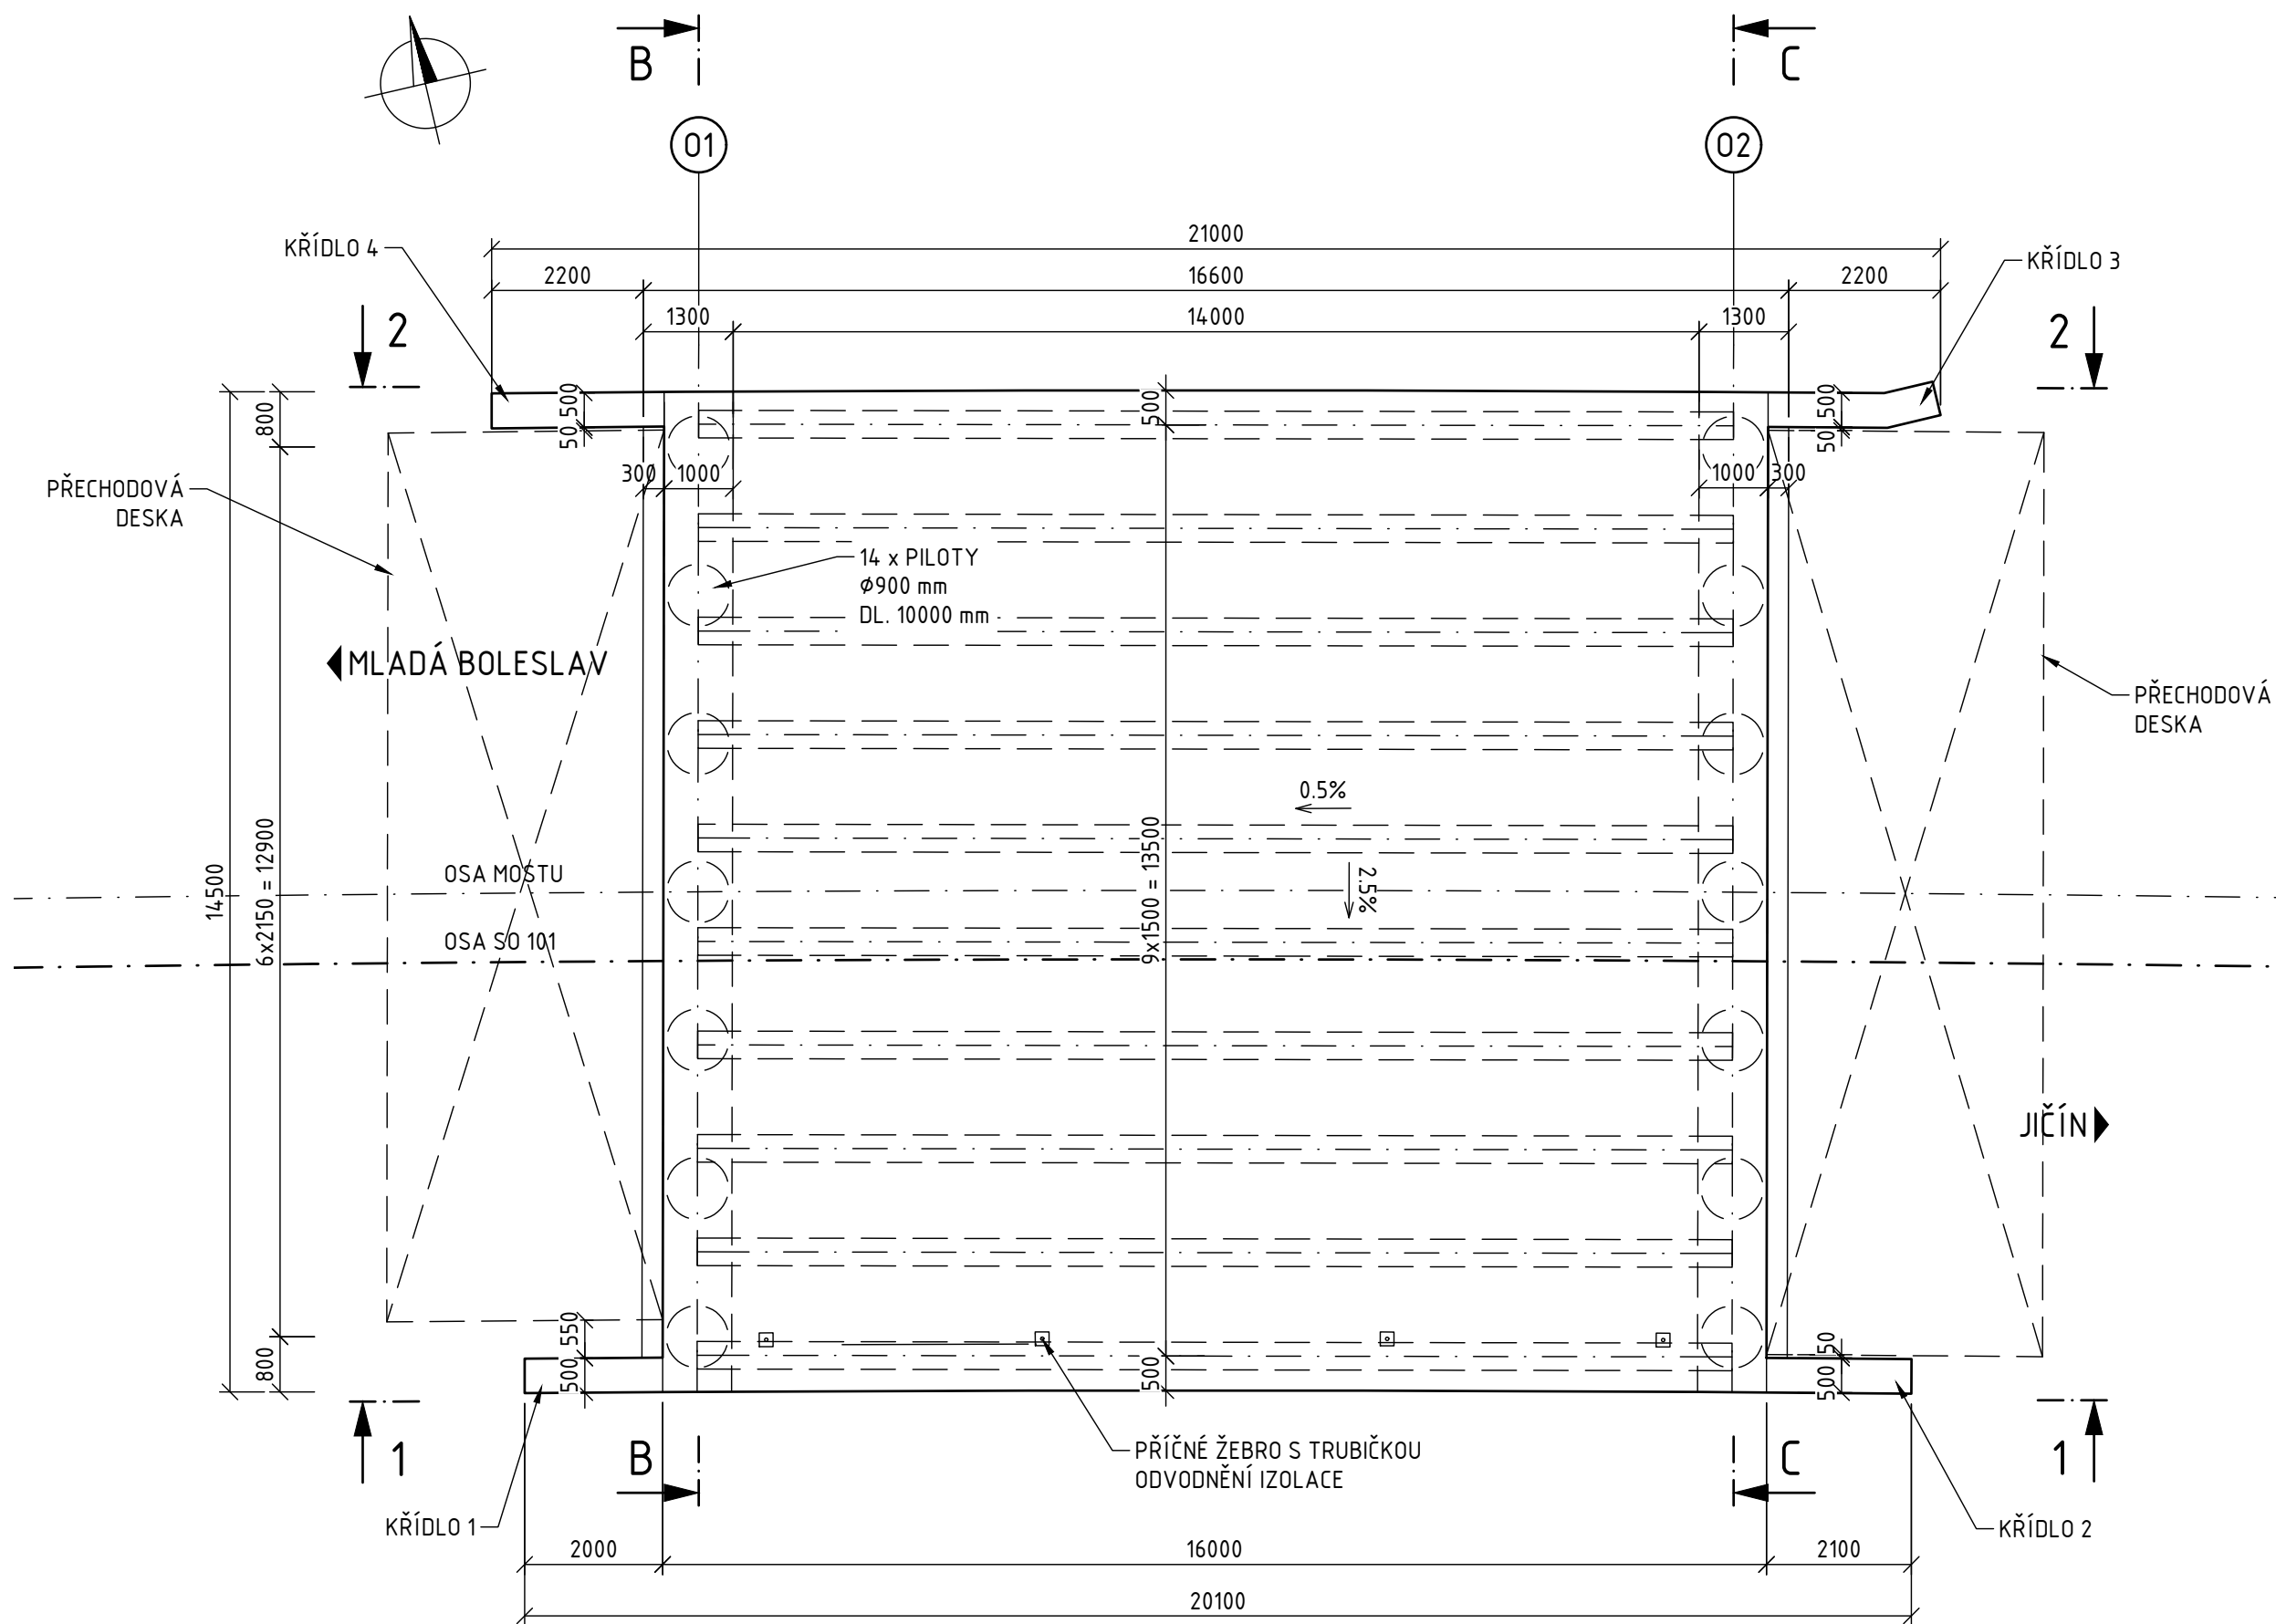


VZOROVÝ PŘÍČNÝ ŘEZ 1:50

-V POLI

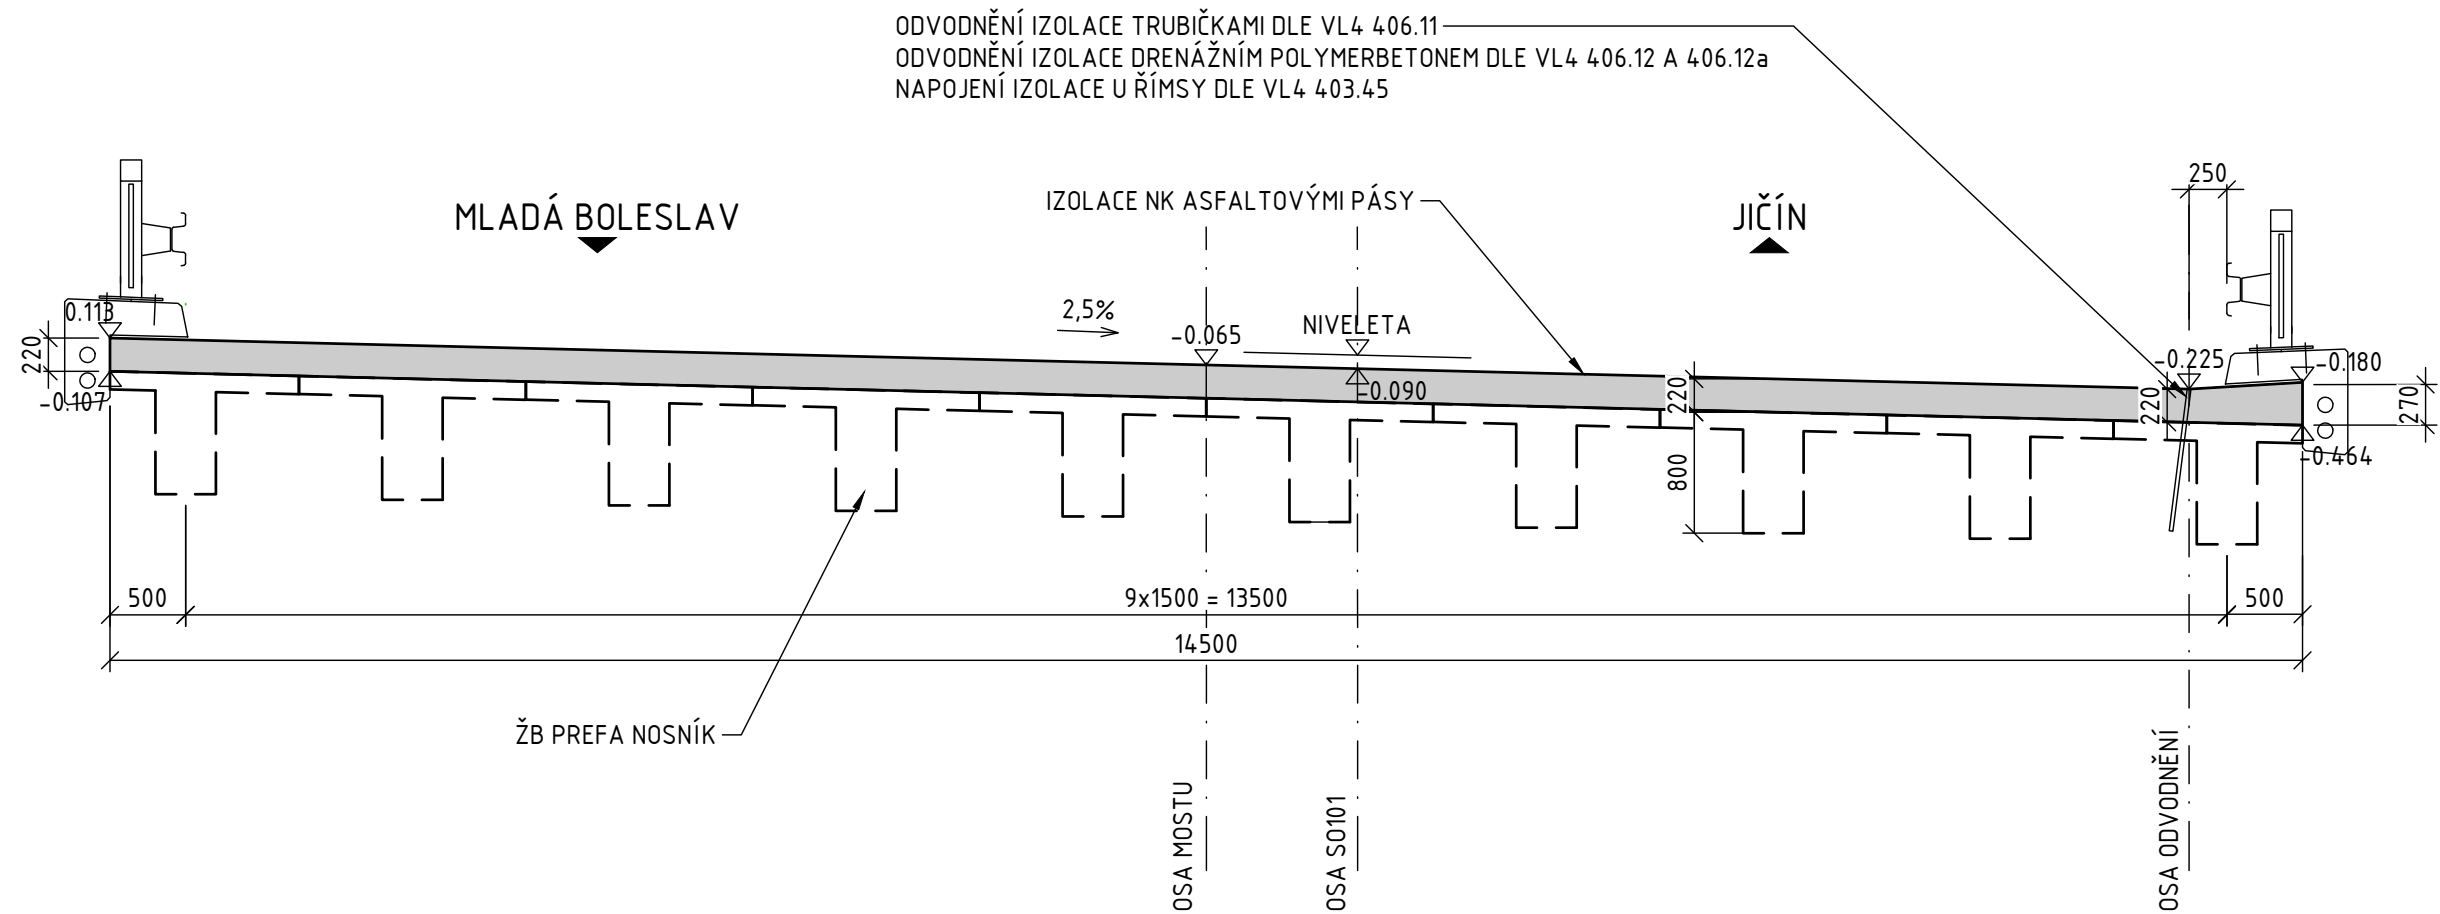

PODÉLNÝ ŘEZ PŘECHODOVOU DESKOU 1:50

VYKRESLENA PŘECHODOVÁ DESKA OPĚRY 02, PŘECHODOVÁ DESKA OPĚRY 01 ŘEŠENA OBOOBNĚ



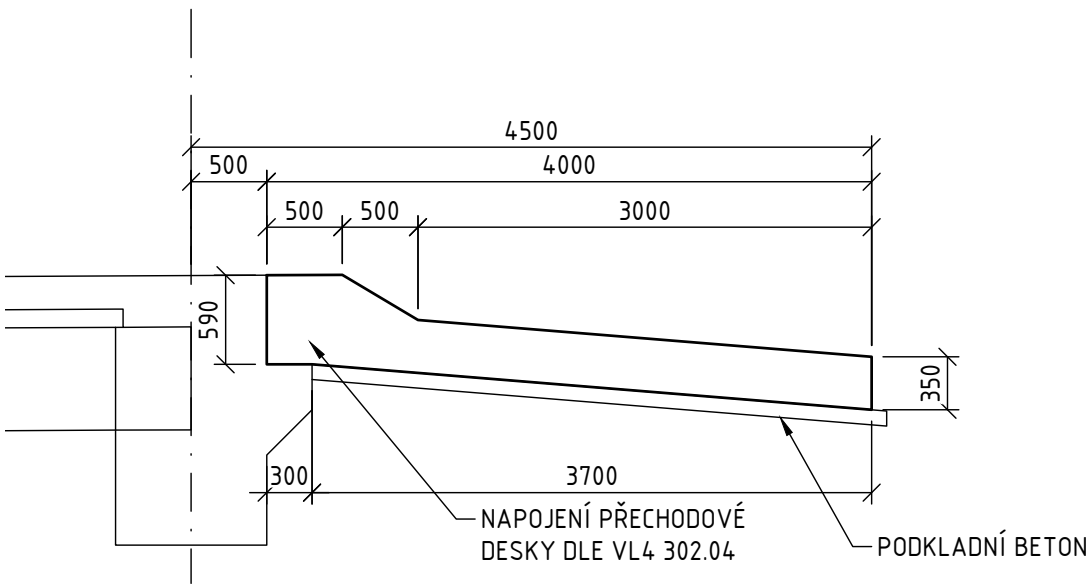


POZNÁMKY:

- NEDÍLNOU SOUČÁSTÍ VÝKRESU JSOU POZNÁMKY A SPECIFIKACE UVEDENÉ NA VÝKRESE
POZNÁMEK A TECHNICKÝCH SPECIFIKACÍ

PODÉLNÝ ŘEZ 1:100

OSOU SO 101

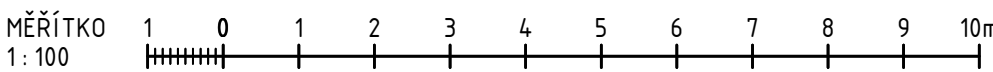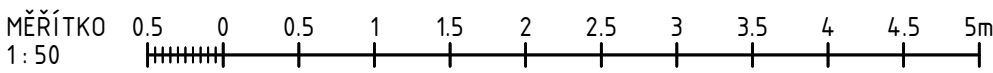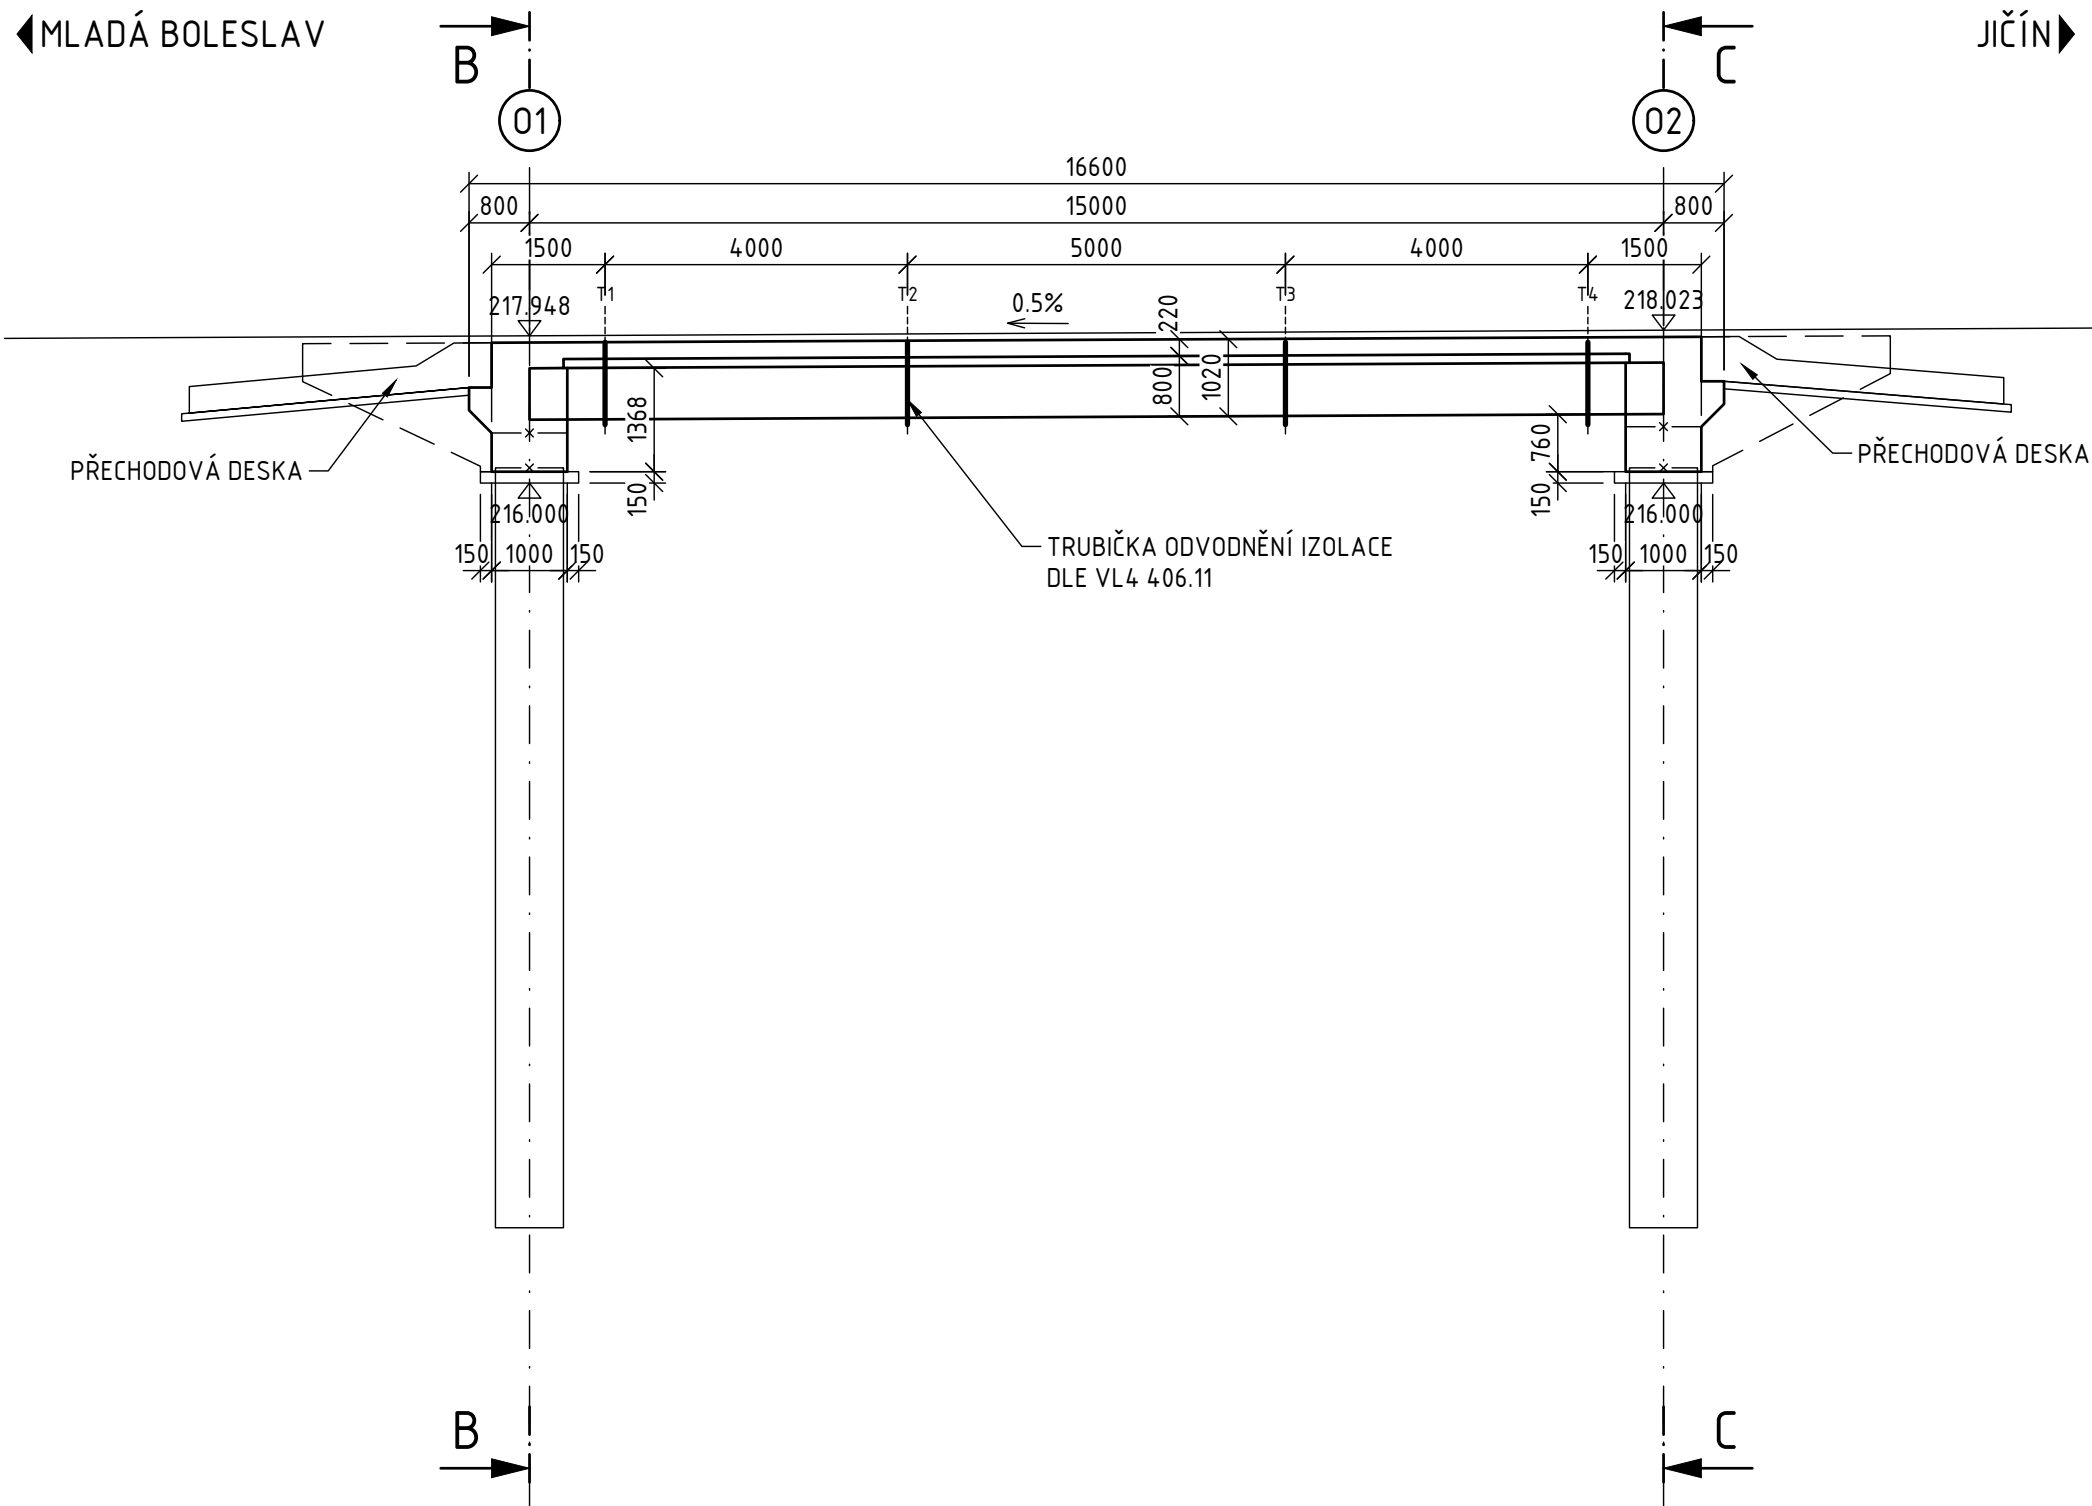

Souřadnicový systém: S-JTSK
Výškový systém: Bpv

SO 202 MOST NA I/16 PŘES VALSKOU SVODNICI V KM 2,695

Objednatel:



Ředitelství silnic a dálnic s. p.
Čerčanská 2023/12, Krč, 140 00 Praha 4



Valbek, spol. s r.o.
Vaňurova 505/17
460 07 Liberec 3



Vypracoval	A. MICHALIKOVÁ	Zak. číslo	21-L113-001	
Zodp. projektant	ING. O. BAKHMET	Datum	02/2025	
Tech. kontrola	ING. I. BELDA	Stupeň	PDPS	
Akce	I/16 MLADÁ BOLESLAV - MARTINOVICE		Počet formátů	8x A4
			Měřítko	1:100,50
			Č. přílohy	Paré
Příloha			201	
TVAR NOSNÉ KONSTRUKCE 1(2), SCHÉMA ODVODNĚNÍ				