


SCHÉMA VYTYČENÍ  
PŮDORYS 1:100

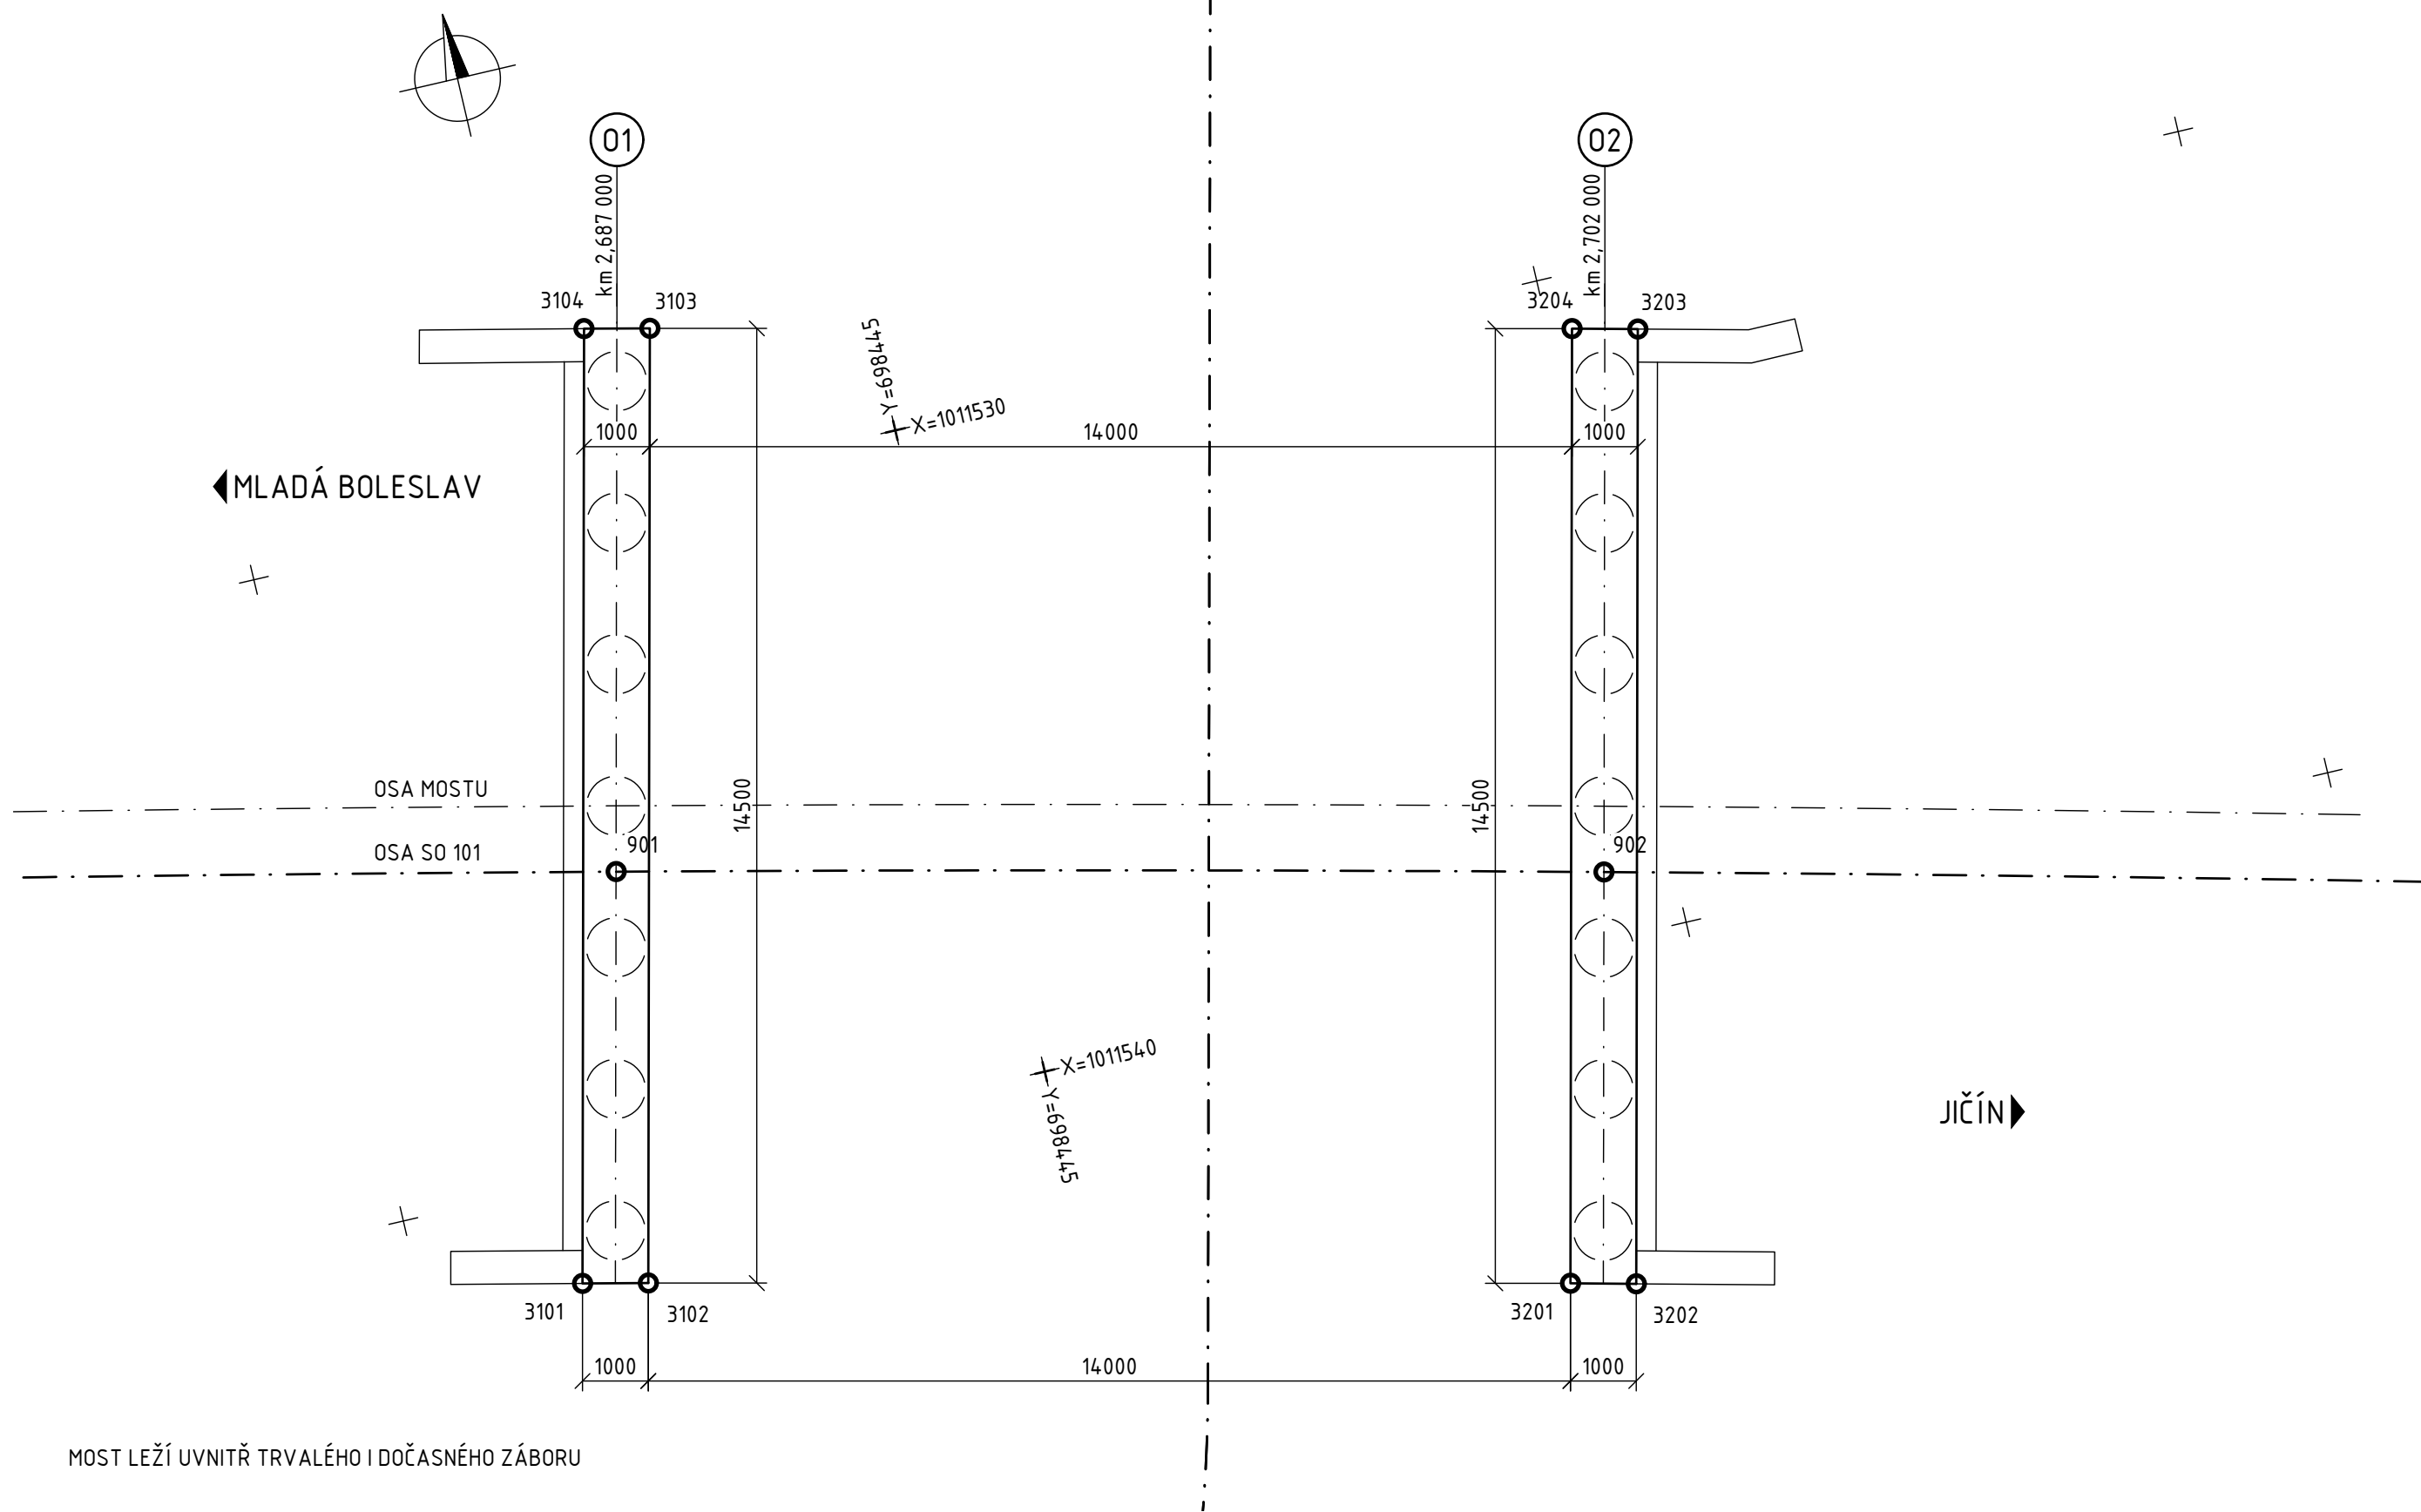

MOST LEŽÍ UVNITŘ TRVALÉHO I DOČASNÉHO ZÁBORU

PODÉLNÝ ŘEZ 1:50



| KLÍČ ZNAČENÍ VYTYČOVANÝCH BODŮ |   |    |                                           |
|--------------------------------|---|----|-------------------------------------------|
| X                              | Y | ZZ | ÚPLNÉ ČÍSLO VYTYČOVANÉHO BODU             |
| X                              |   |    | ČÍSLO ČINNOSTI, 9 - OSY, 3 - SPOD. STAVBA |
|                                | Y |    | ČÍSLO PODPĚRY, 1 - OPĚRA 1, 2 - OPĚRA 2   |
|                                |   | ZZ | POŘADOVÉ ČÍSLO BODU                       |

OSA

| č.bodu | Y [m]       | X [m]         |
|--------|-------------|---------------|
| 901    | 698 450.650 | 1 011 535.565 |
| 902    | 698 436.043 | 1 011 538.974 |

OPĚRA 1

| č.bodu | Y [m]       | X [m]         | Z [m.n.m.] |
|--------|-------------|---------------|------------|
| 3101   | 698 452.566 | 1 011 541.541 | 216.150    |
| 3102   | 698 451.590 | 1 011 541.760 | 216.150    |
| 3103   | 698 448.278 | 1 011 527.645 | 216.150    |
| 3104   | 698 449.253 | 1 011 527.423 | 216.150    |

OPĚRA 2

| č.bodu | Y [m]       | X [m]         | Z [m.n.m.] |
|--------|-------------|---------------|------------|
| 3201   | 698 437.957 | 1 011 544.943 | 216.150    |
| 3202   | 698 436.985 | 1 011 545.178 | 216.150    |
| 3203   | 698 433.672 | 1 011 531.061 | 216.150    |
| 3204   | 698 434.644 | 1 011 530.826 | 216.150    |

POZNÁMKY:

- VYTYČOVACÍ ODCHYLKY: VIZ PŘÍLOHA E.4.5.1 - GVS - SEZNAM SOUŘADNIC
- NEDÍLNOU SOUČÁSTÍ VÝKRESU JSOU POZNÁMKY A SPECIFIKACE UVEDENÉ NA VÝKRESE POZNÁMEK A TECHNICKÝCH SPECIFIKACÍ

Souřadnicový systém: S-JTSK  
Výškový systém: Bpv

**SO 202** MOST NA I/16 PŘES VALSKOU SVODNICI V KM 2,695

Objednatel:



**Ředitelství silnic a dálnic s. p.**  
Čerčanská 2023/12, Krč, 140 00 Praha 4



**Valbek, spol. s r.o.**  
Vaňurova 505/17  
460 07 Liberec 3



|                  |                                   |            |               |          |
|------------------|-----------------------------------|------------|---------------|----------|
| Vypracoval       | A. MICHALÍKOVÁ                    | Zak. číslo | 21-L113-001   |          |
| Zodp. projektant | ING. O. BAKHMET                   | Datum      | 02/2025       |          |
| Tech. kontrola   | ING. I. BELDA                     | Stupeň     | PDPS          |          |
| Akce             | I/16 MLADÁ BOLESLAV - MARTINOVICE |            | Počet formátů | 8x A4    |
|                  |                                   |            | Měřítko       | 1:100,50 |
|                  |                                   |            | Č. přílohy    | Paré     |
| Příloha          |                                   |            | 203           |          |
| SCHÉMA VYTYČENÍ  |                                   |            |               |          |

