

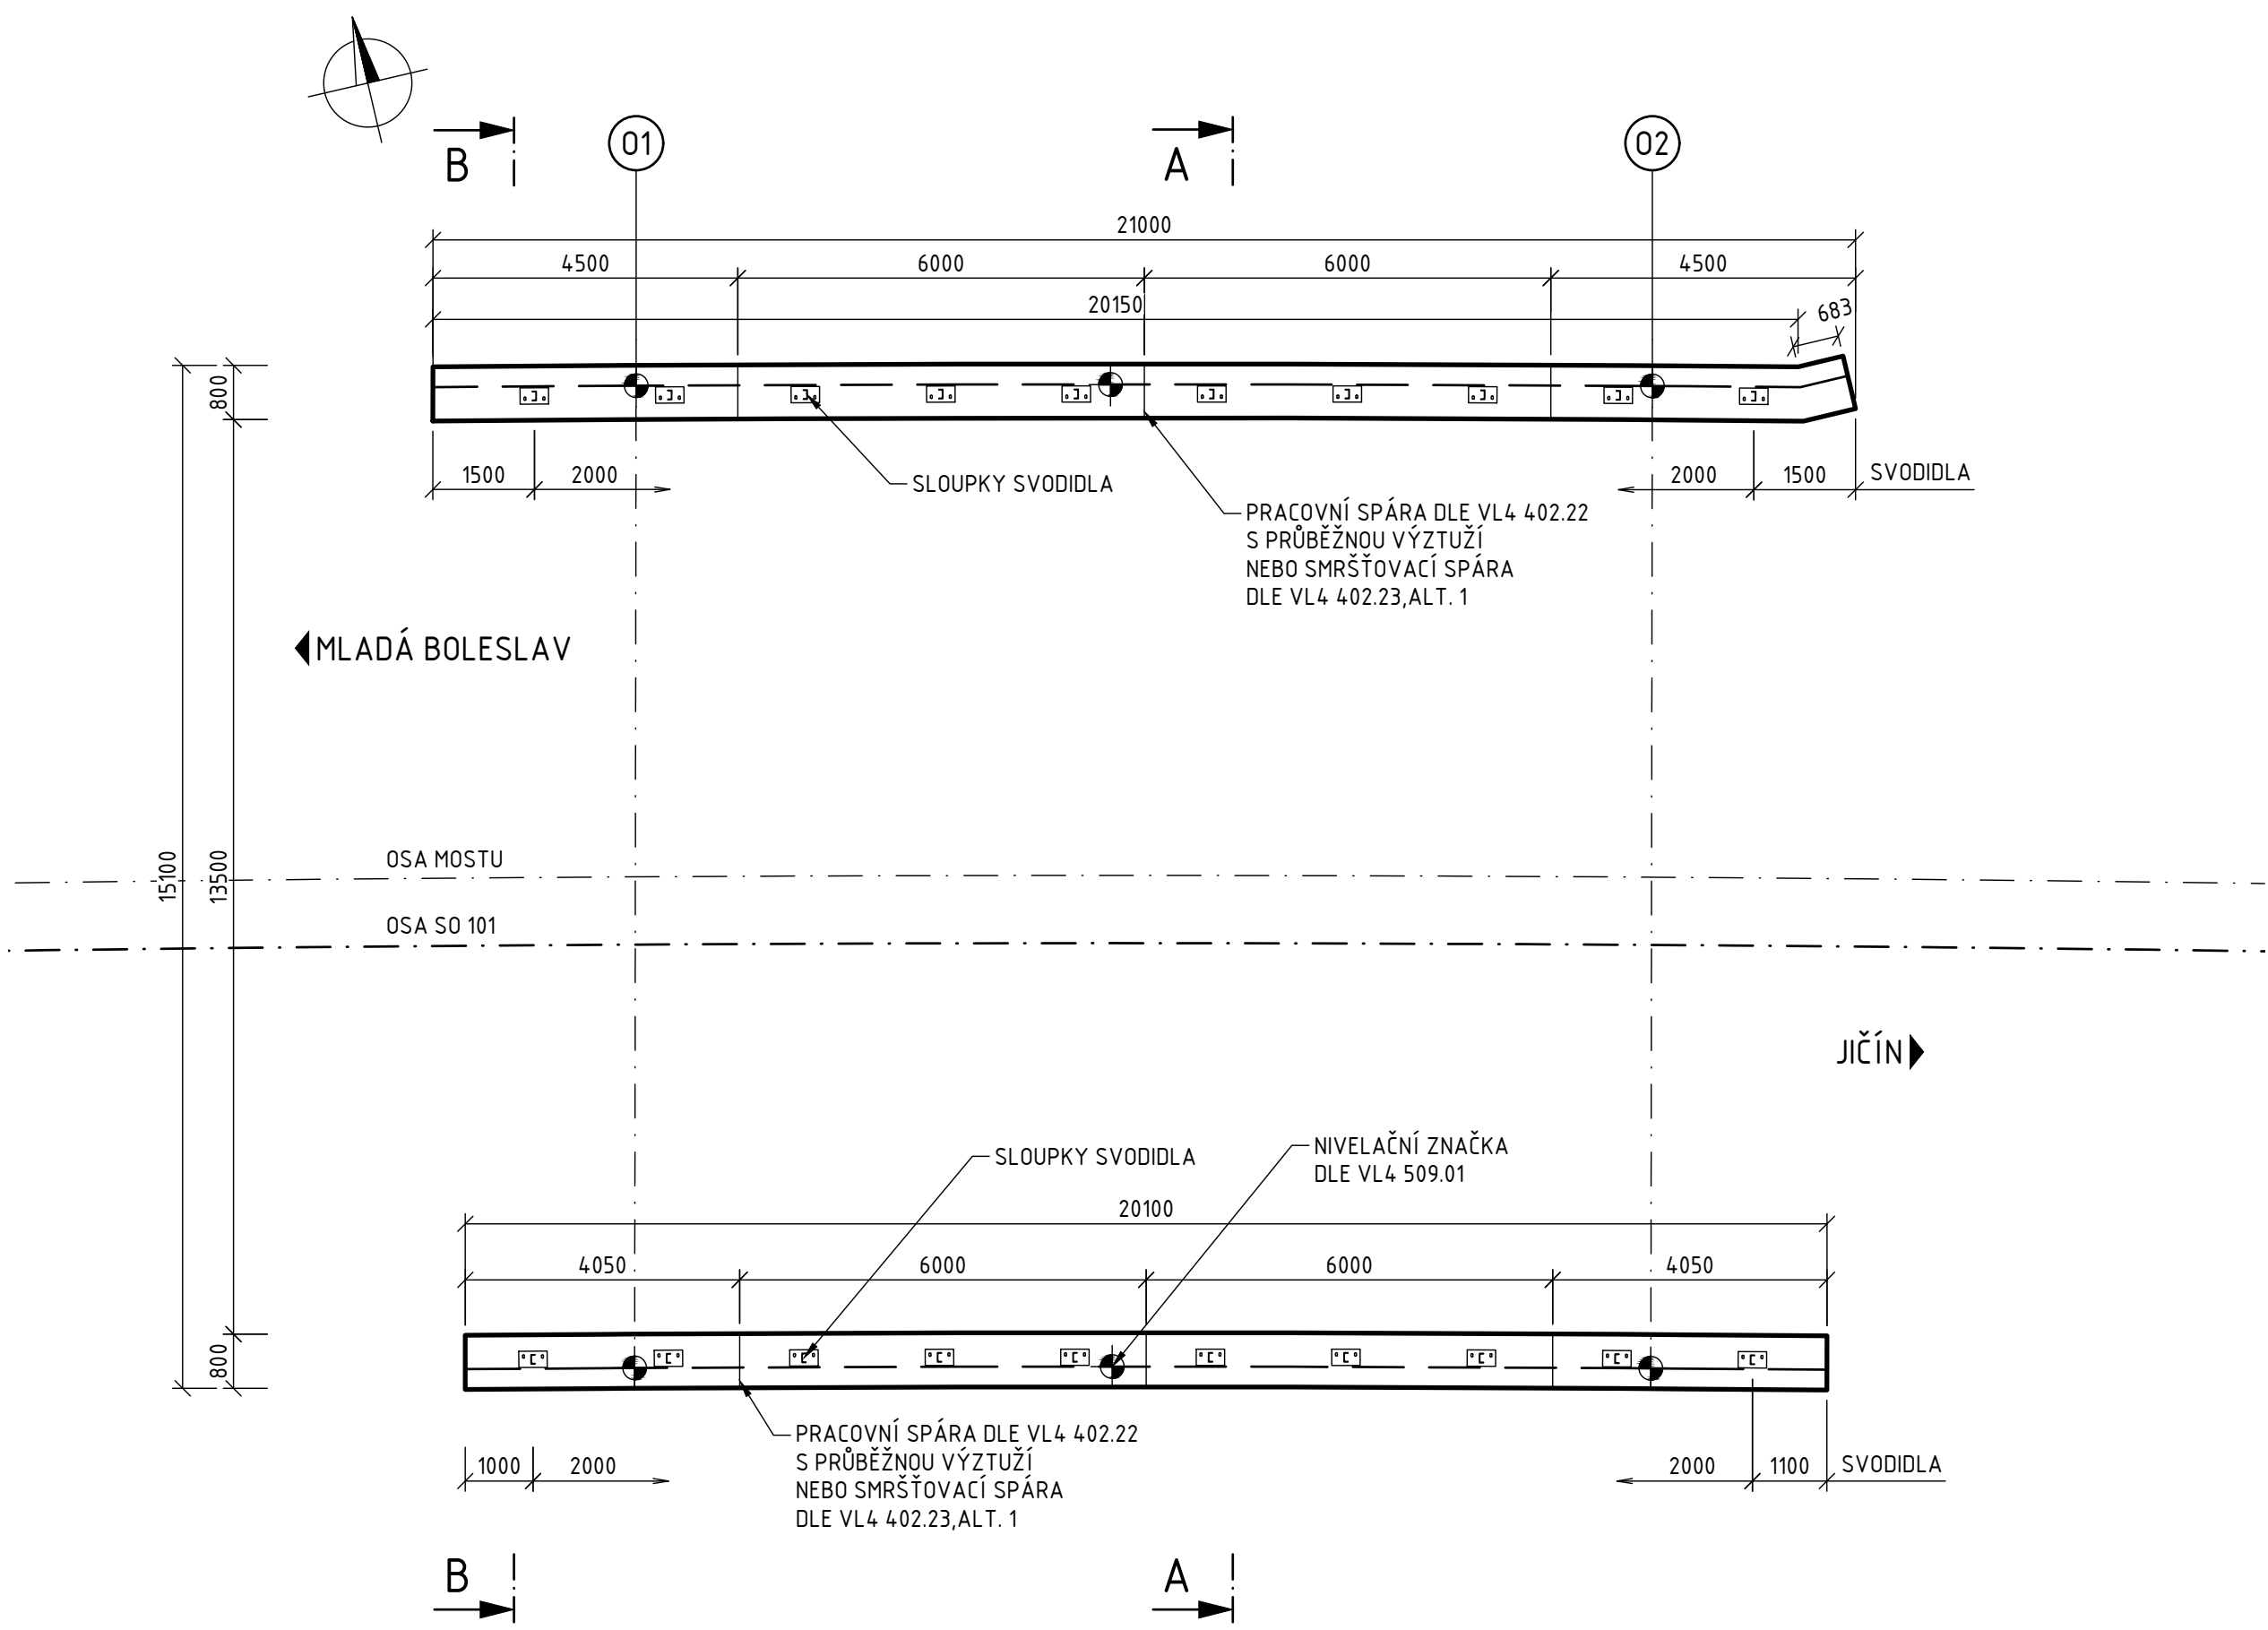



PŮDORYS 1:100

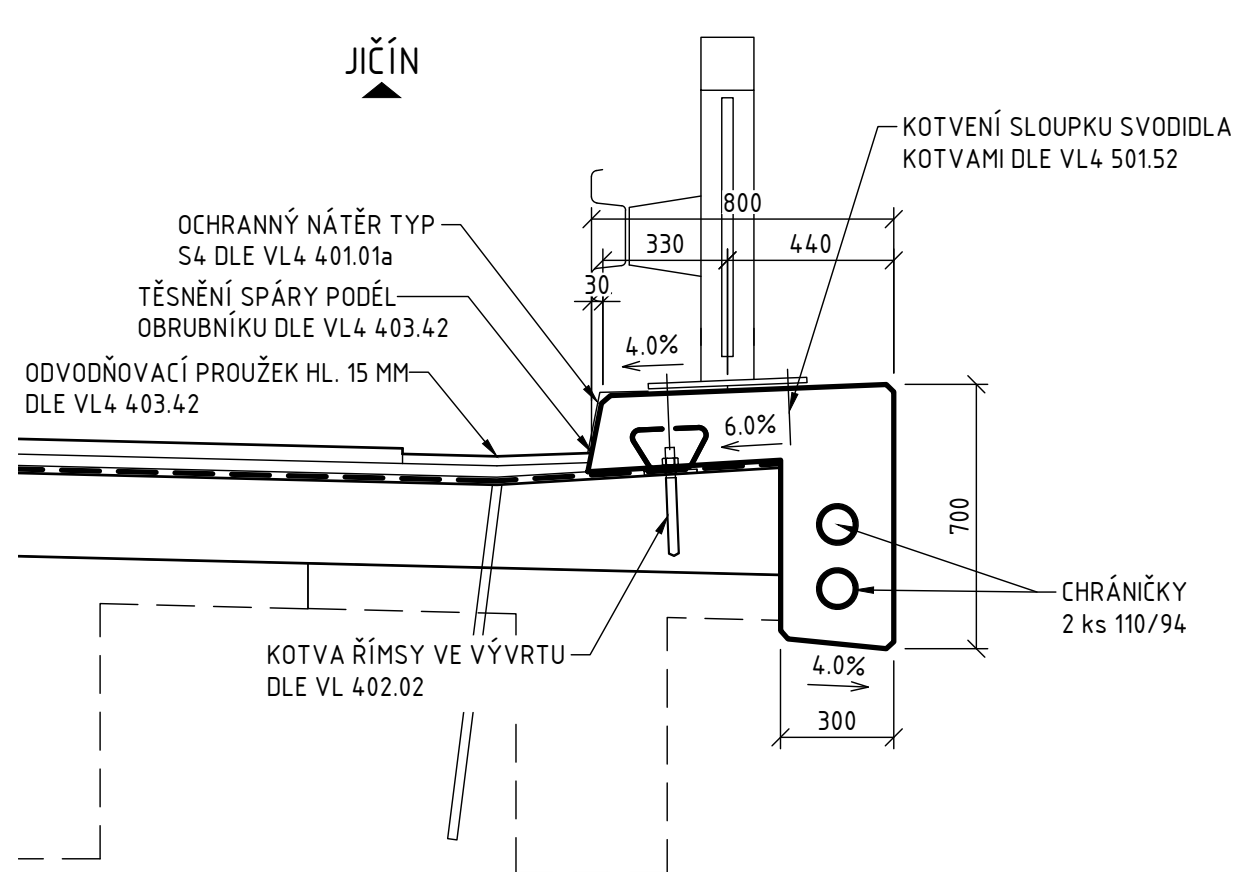

ŘEZ A-A 1:20

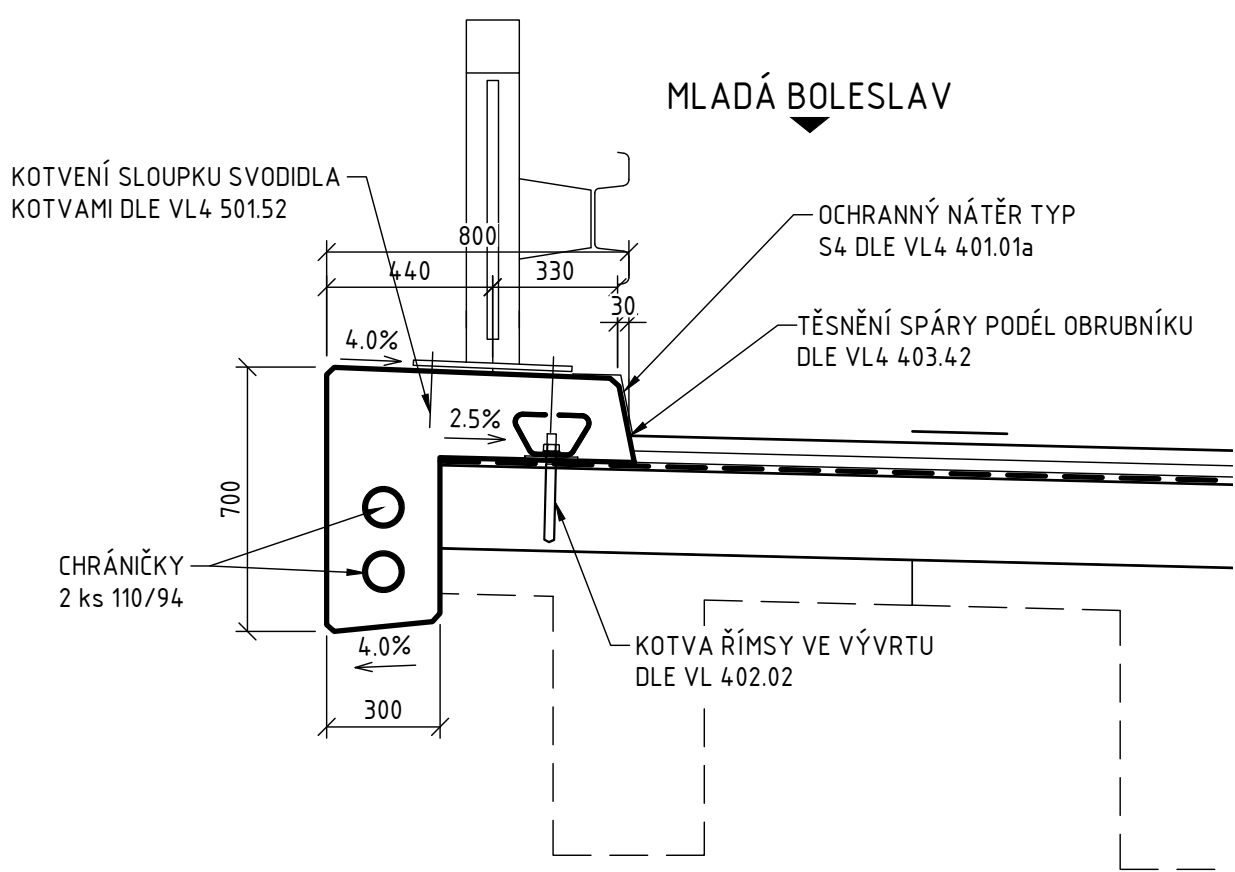

ŘEZ B-B 1:20



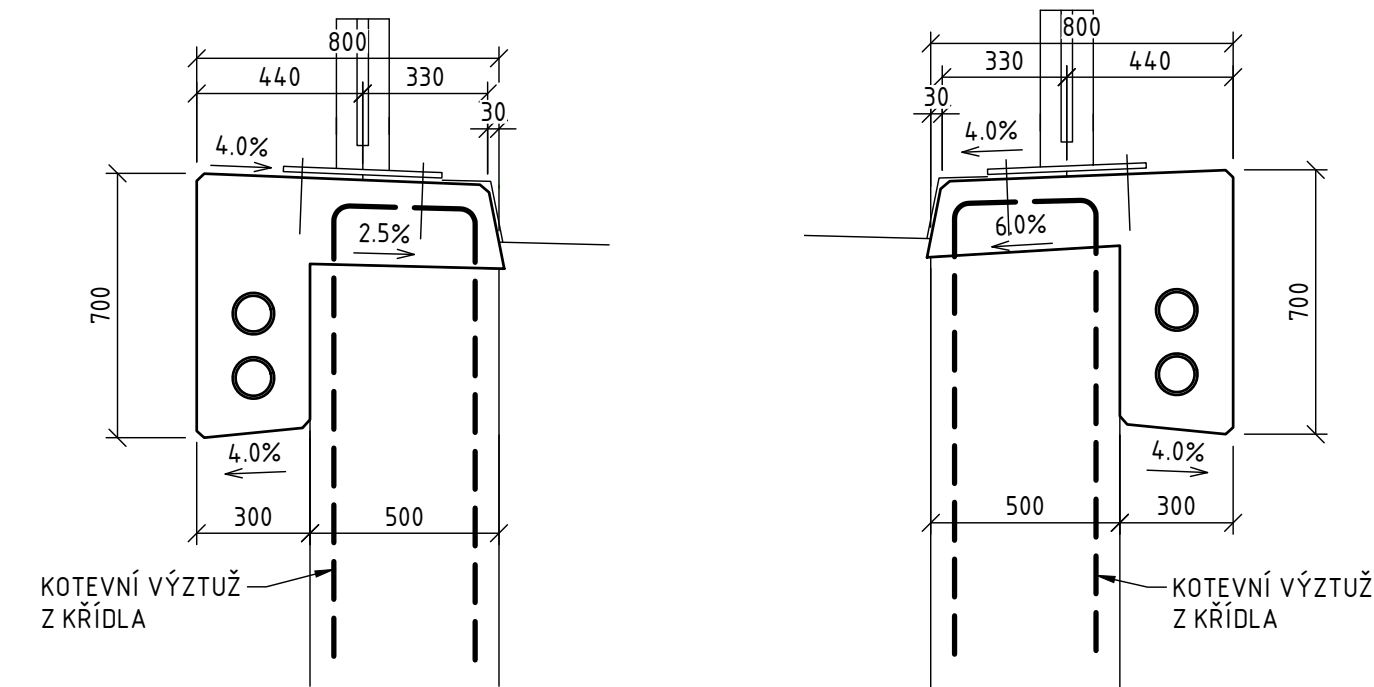


POZNÁMKY:

- NEDILNOU SOUČÁSTÍ VÝKRESU JSOU POZNÁMKY A SPECIFIKACE UVEDENÉ NA VÝKRESE POZNÁMEK A TECHNICKÝCH SPECIFIKACÍ

PŘECHODOVÉ OBLASTI
1:50

PODÉLNÝ ŘEZ OSOU SO 101

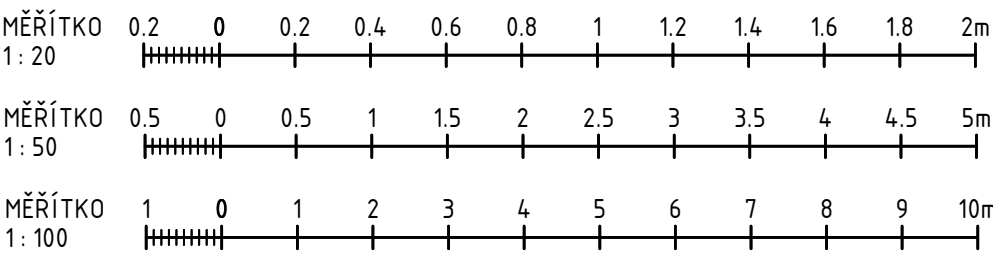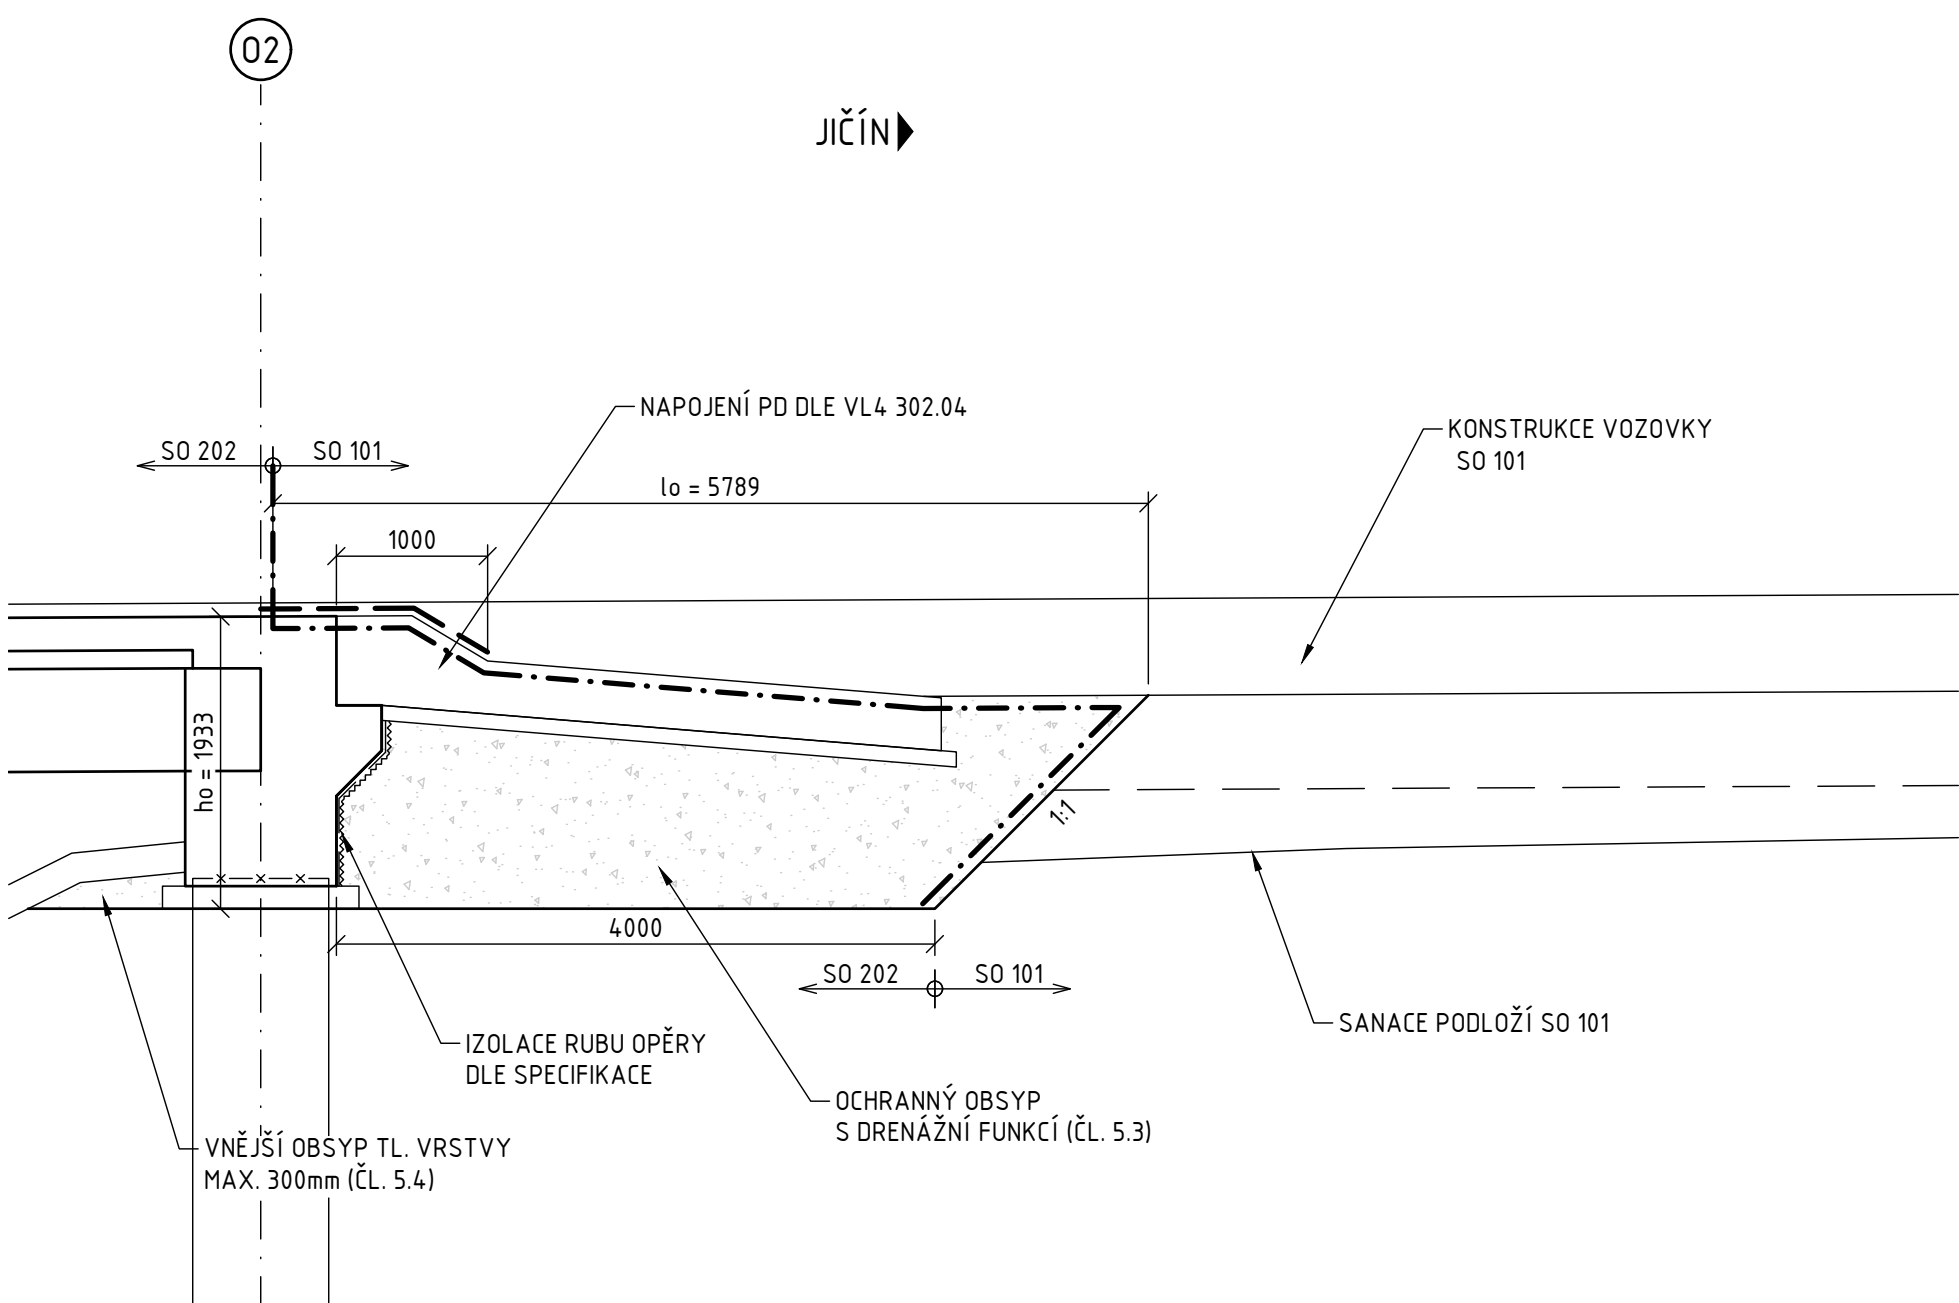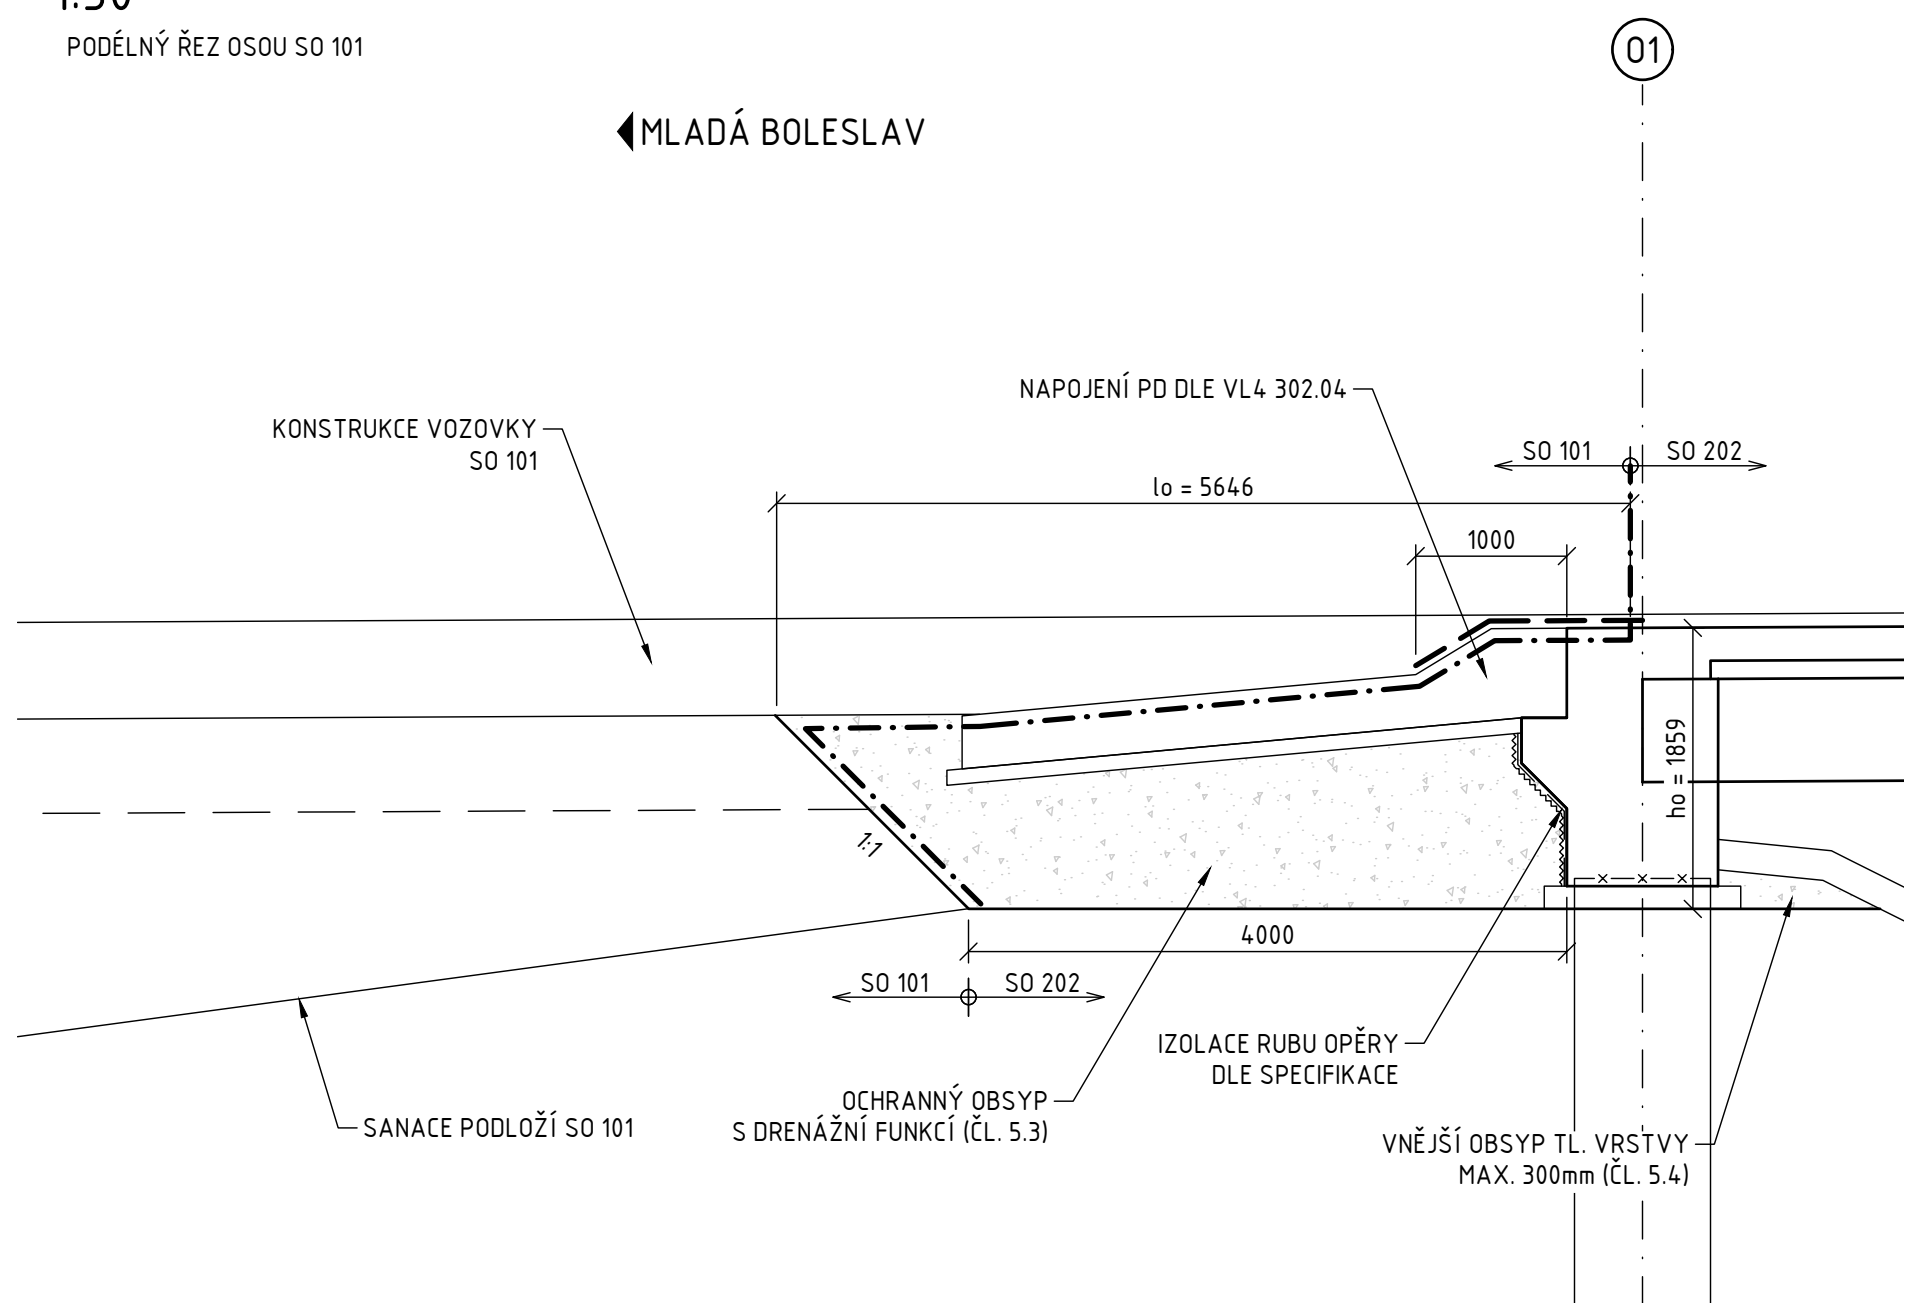

Souřadnicový systém: S-JTSK
Výškový systém: Bpv

SO 202 MOST NA I/16 PŘES VALSKOU SVODNICI V KM 2,695

Objednatel:



Ředitelství silnic a dálnic s. p.
Čerčanská 2023/12, Krč, 140 00 Praha 4



Valbek, spol. s r.o.
Vaňurova 505/17
460 07 Liberec 3



	Vypracoval	A. MICHALIKOVÁ		Zak. číslo	21-L113-001	
	Zodp. projektant	ING. O. BAKHMET		Datum	02/2025	
	Tech. kontrola	ING. I. BELDA		Stupeň	PDPS	
	Akce	I/16 MLADÁ BOLESLAV - MARTINOVICE			Počet formátů	8x A4
Zhotovitel: Valbek, spol. s r.o. Vaňurova 505/17 460 07 Liberec 3	Příloha	PŘECHODOVÉ OBLASTI, TVAR ŘÍMS			Měřítko	1:100, 50, 20
					Č. přílohy	Paré
					204	