



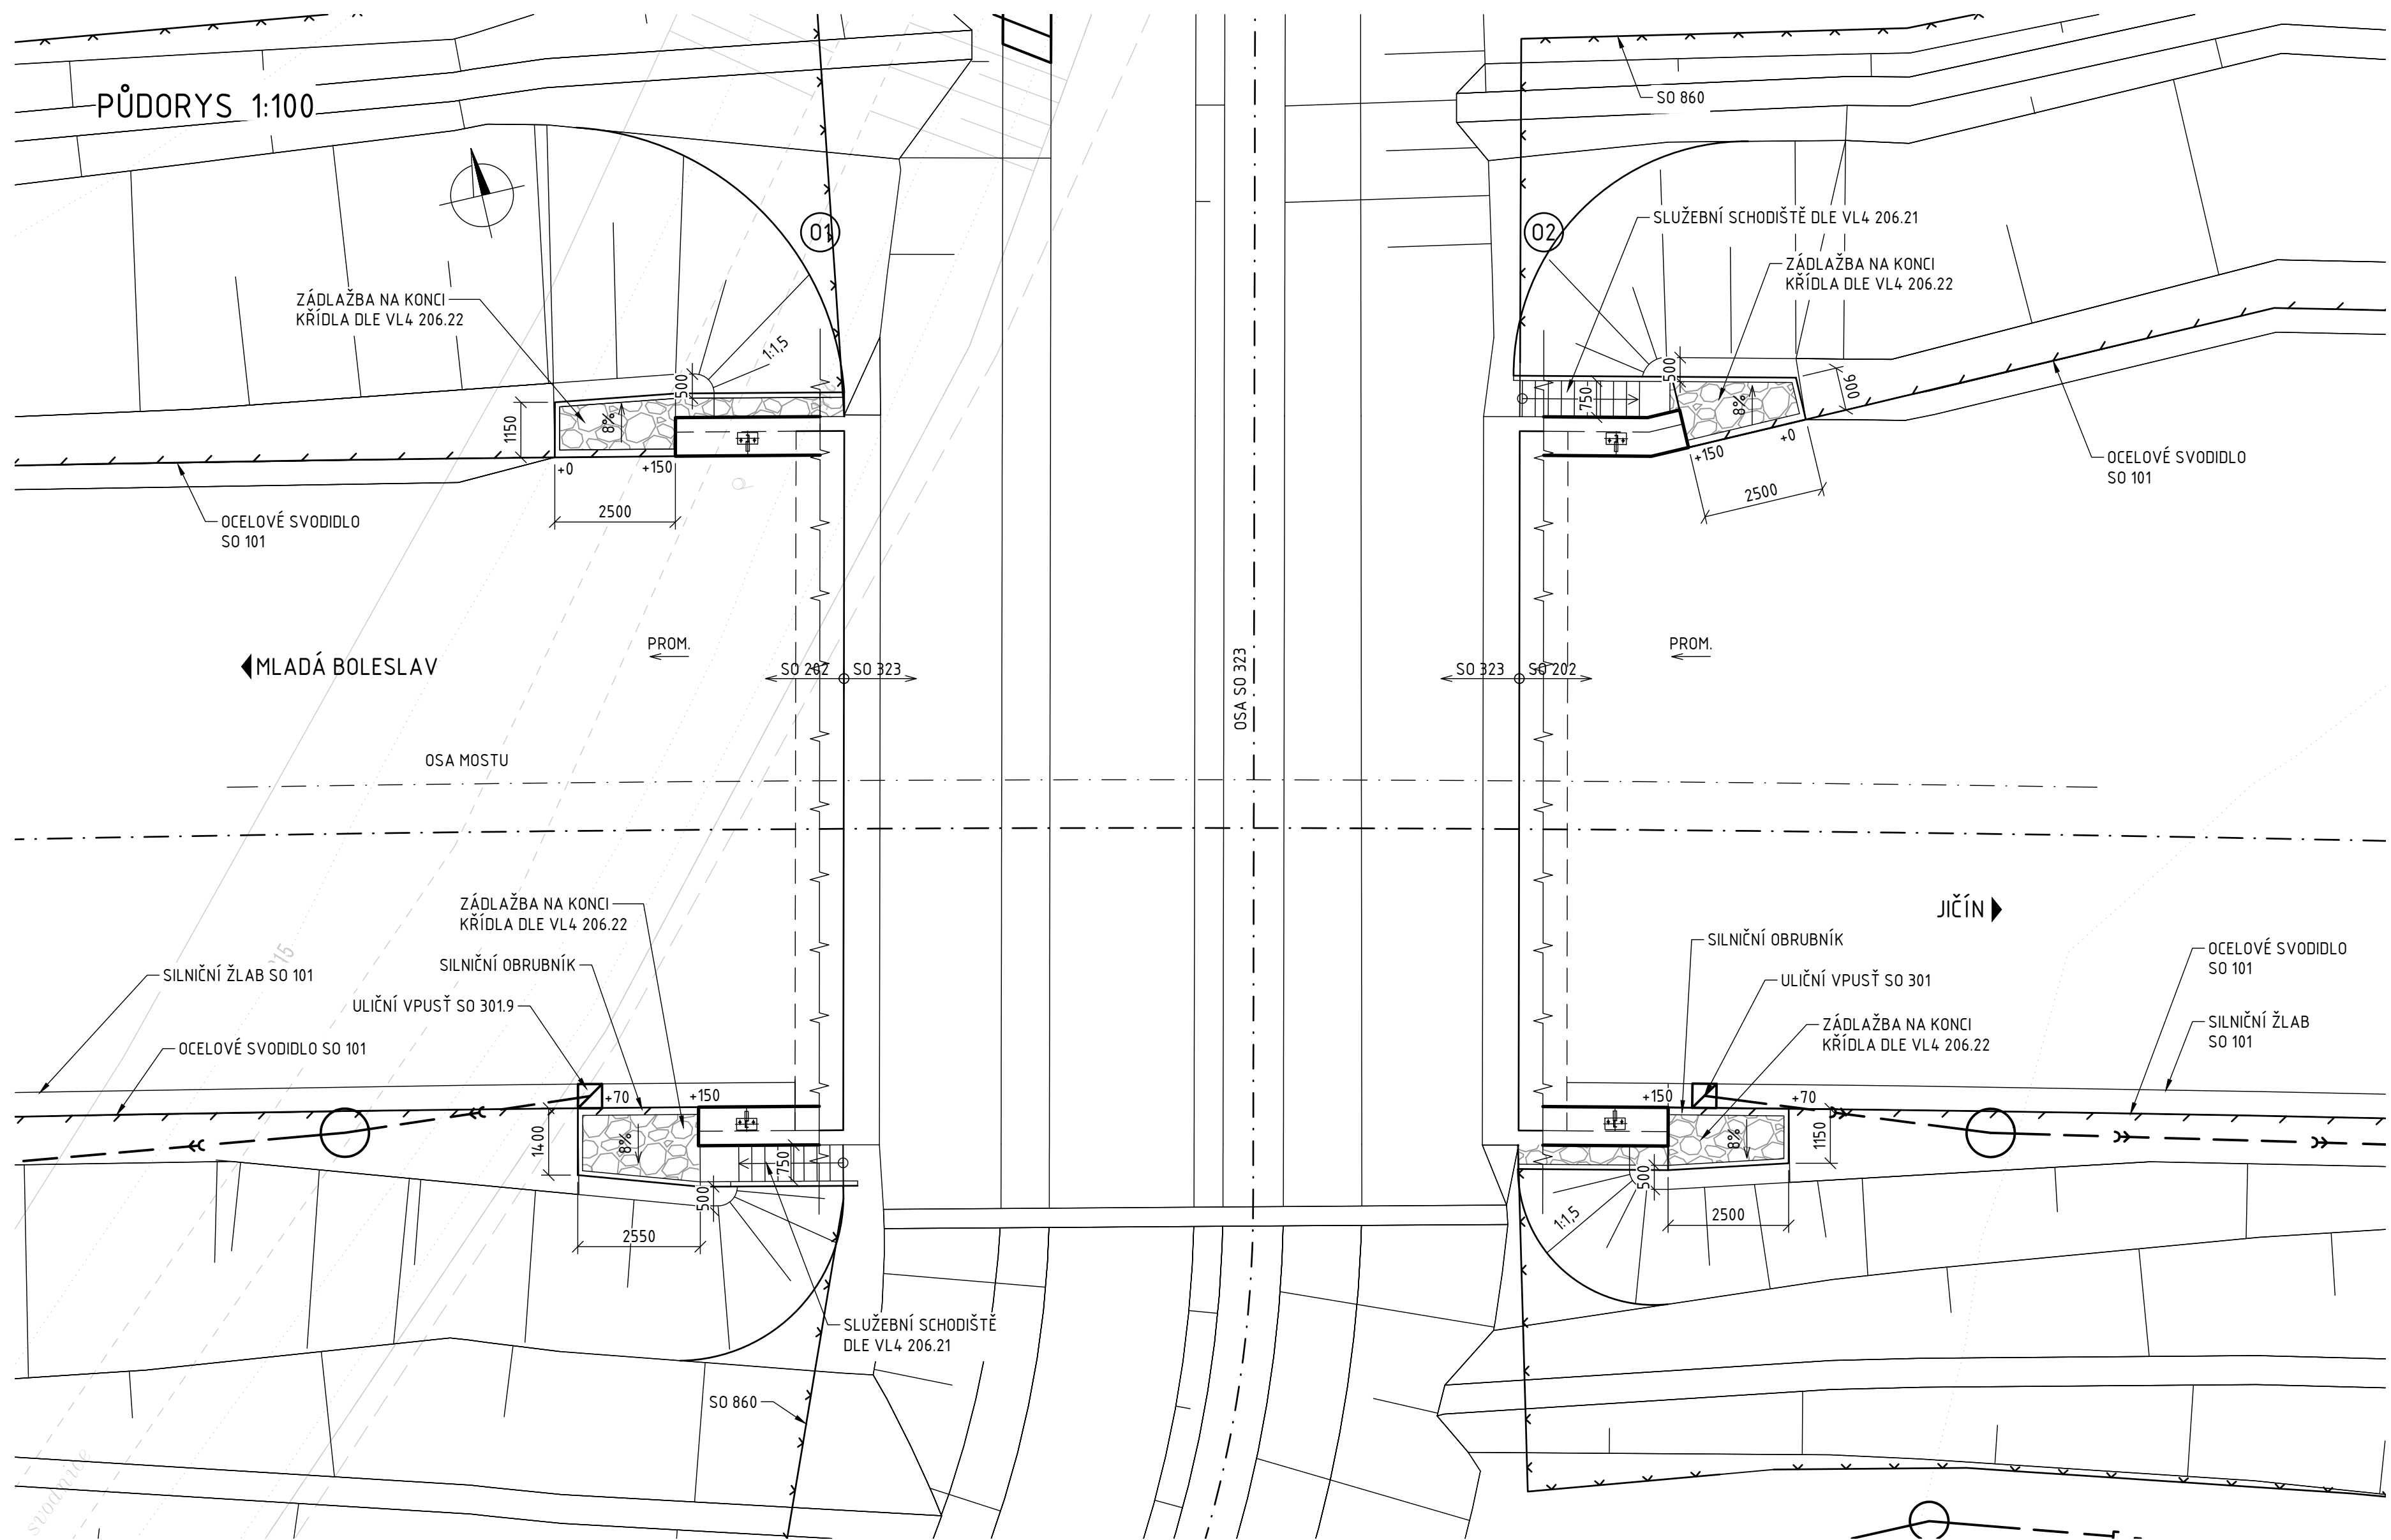


POZNÁMKY:
- NEDÍLNOU SOUČÁSTÍ VÝKRESU JSOU POZNÁMKY A SPECIFIKACE UVEDENÉ NA VÝKRESE
POZNÁMEK A TECHNICKÝCH SPECIFIKACÍ

SLUŽEBNÍ SCHODIŠTĚ

SCHODIŠTĚ 1 - PODÉLNÝ ŘEZ 1:75

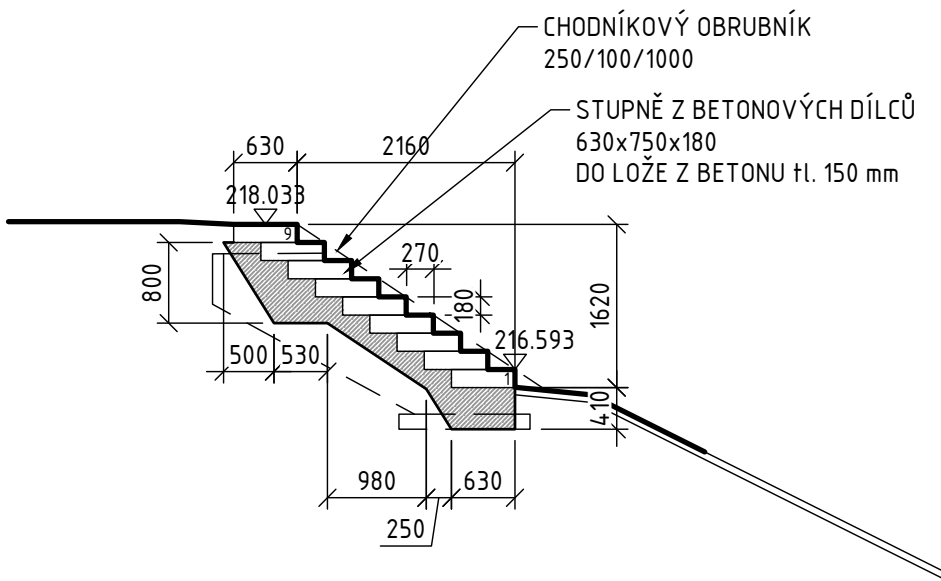

SCHODIŠTĚ 2 - PODÉLNÝ ŘEZ 1:75

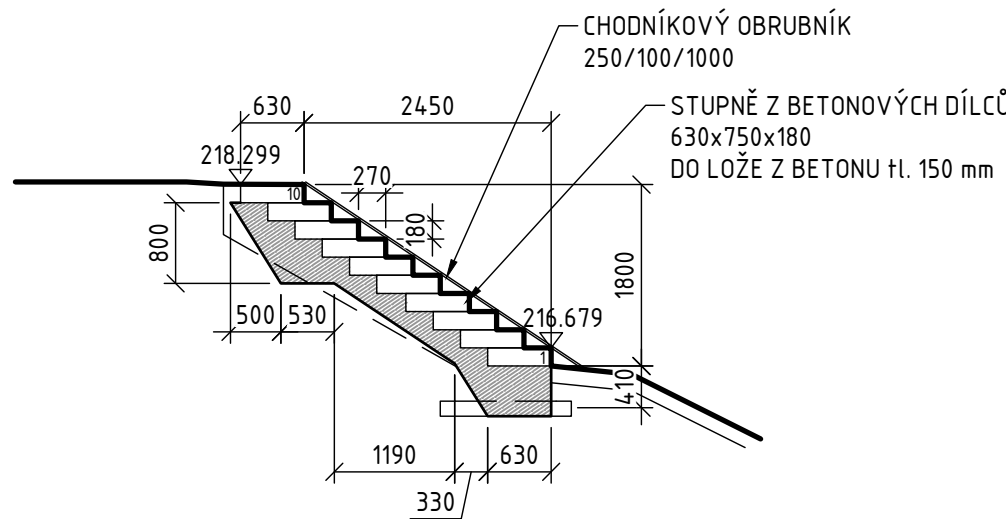

Souřadnicový systém: S-JTSK
Výškový systém: Bpv

SO 202 MOST NA I/16 PŘES VALSKOU SVODNICI V KM 2,695

Objednatel:



Ředitelství silnic a dálnic s. p.
Čerčanská 2023/12, Krč, 140 00 Praha 4



Valbek, spol. s r.o.
Vaňurova 505/17
460 07 Liberec 3



Vypracoval	A. MICHALIKOVÁ		Zak. číslo	21-L113-001	
Zodp. projektant	ING. O. BAKHMET	<i>OB</i>	Datum	02/2025	
Tech. kontrola	ING. I. BELDA	<i>IB</i>	Stupeň	PDPS	
Akce	I/16 MLADÁ BOLESLAV - MARTINOVICE			Počet formátů	8x A4
				Měřítko	1:100,75
				Č. přílohy	Paré
Příloha				205	
ÚPRAVY POD MOSTEM, SLUŽEBNÍ SCHODIŠTĚ					

