



SCHÉMA VÝZTUŽE NK 1:50
PODÉLNÝ ŘEZ

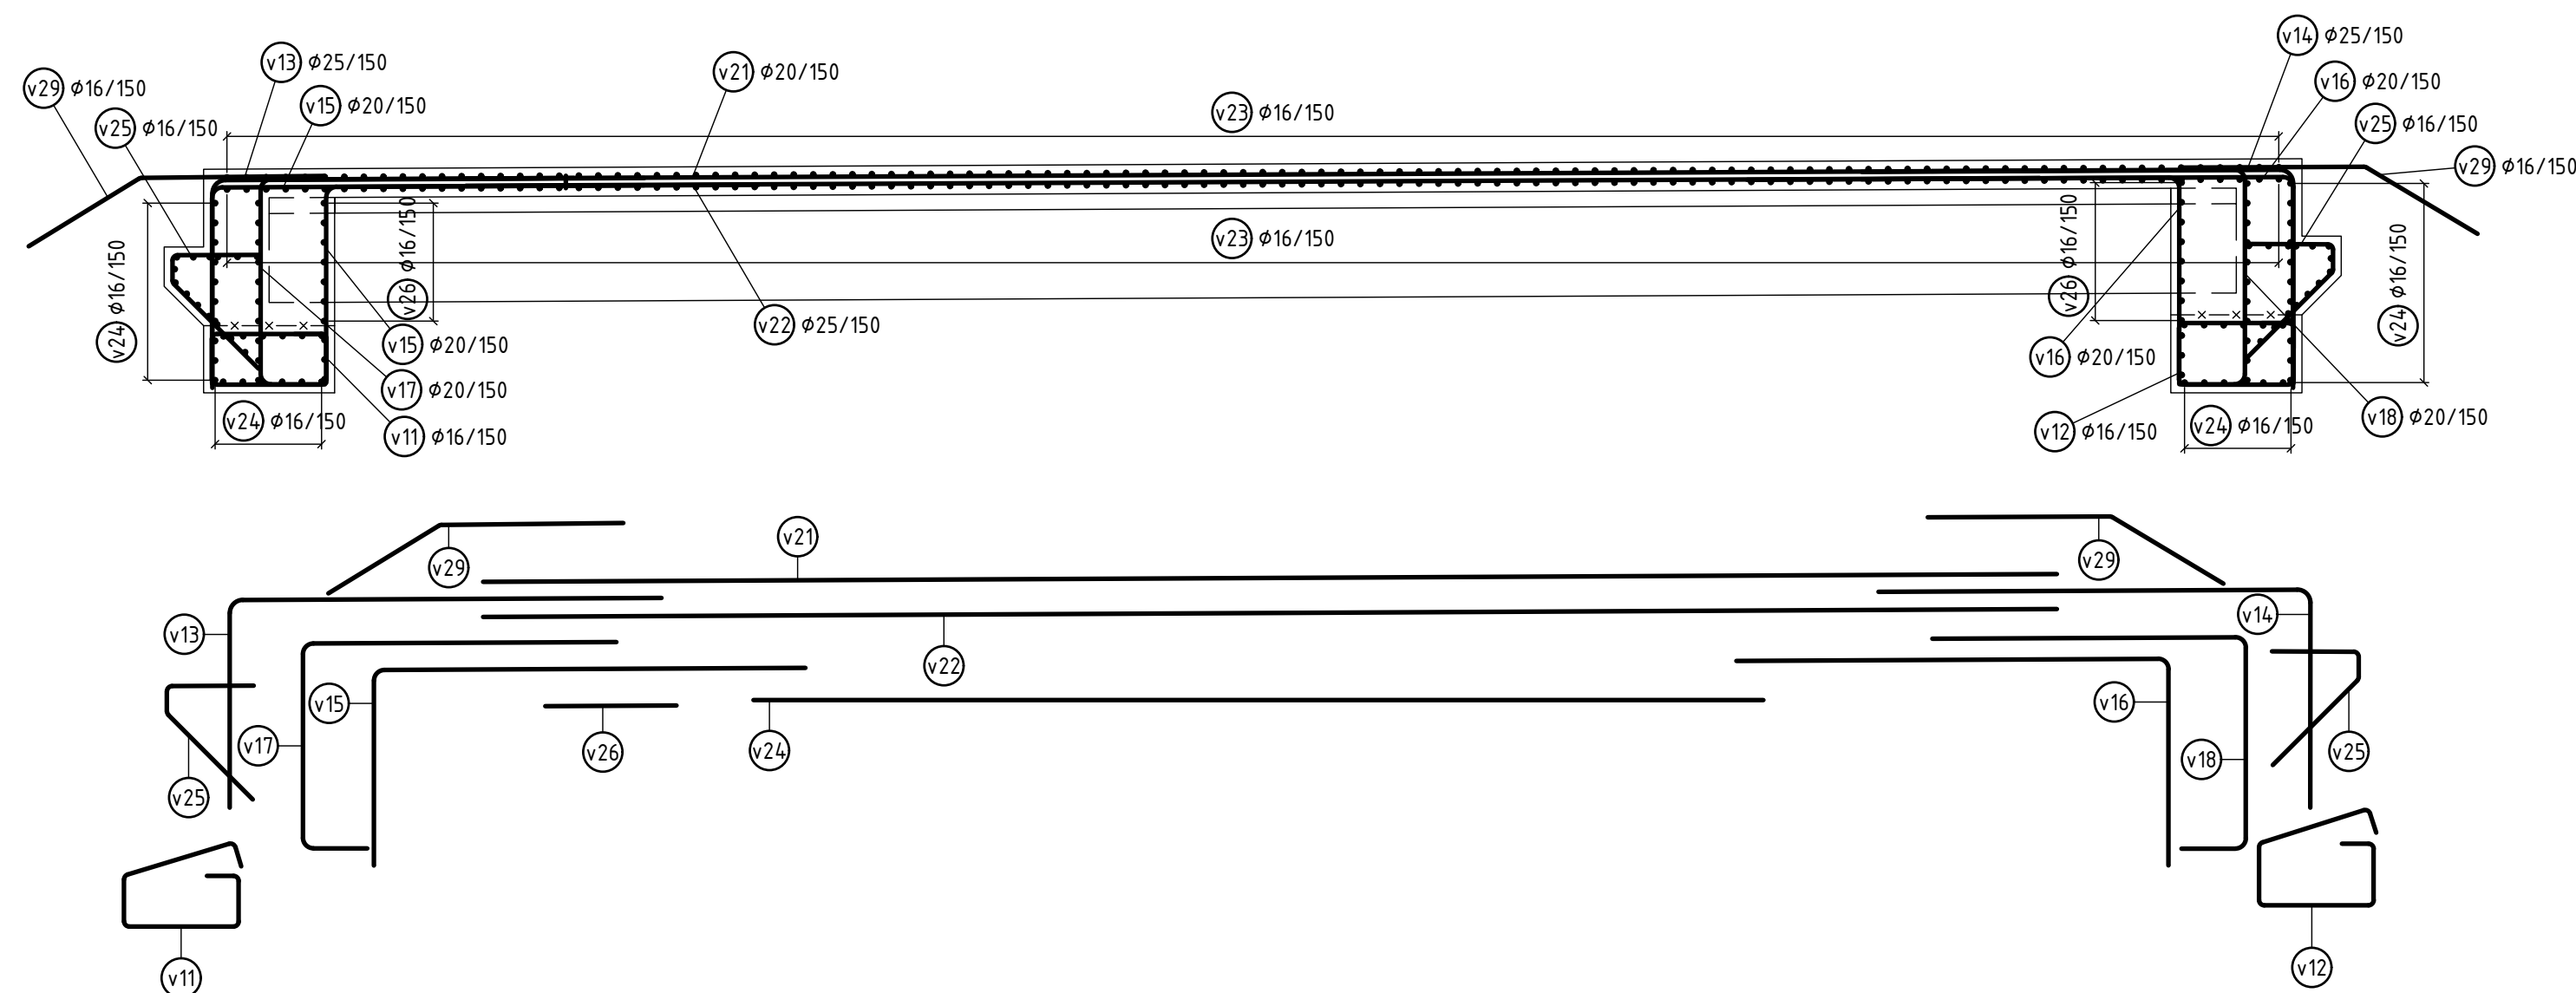


ODHAD MNOŽSTVÍ BETONÁŘSKÉ VÝTUŽE SO 202	MNOŽSTVÍ VÝTUŽE V %	MNOŽSTVÍ VÝT. V KG/M3
VÝTUŽ PILOT POD OPĚROU 1, D 900MM	1.02%	80
VÝTUŽ PILOT POD OPĚROU 2, D 900MM	1.02%	80
VÝTUŽ PRO DŘÍK OPĚRY, KŘÍDLA	2.93%	230
VÝTUŽ ŘÍMS	1.72%	135
VÝTUŽ PŘECHODOVÝ DESEK	2.04%	160

PŘÍČNÝ ŘEZ 1:50

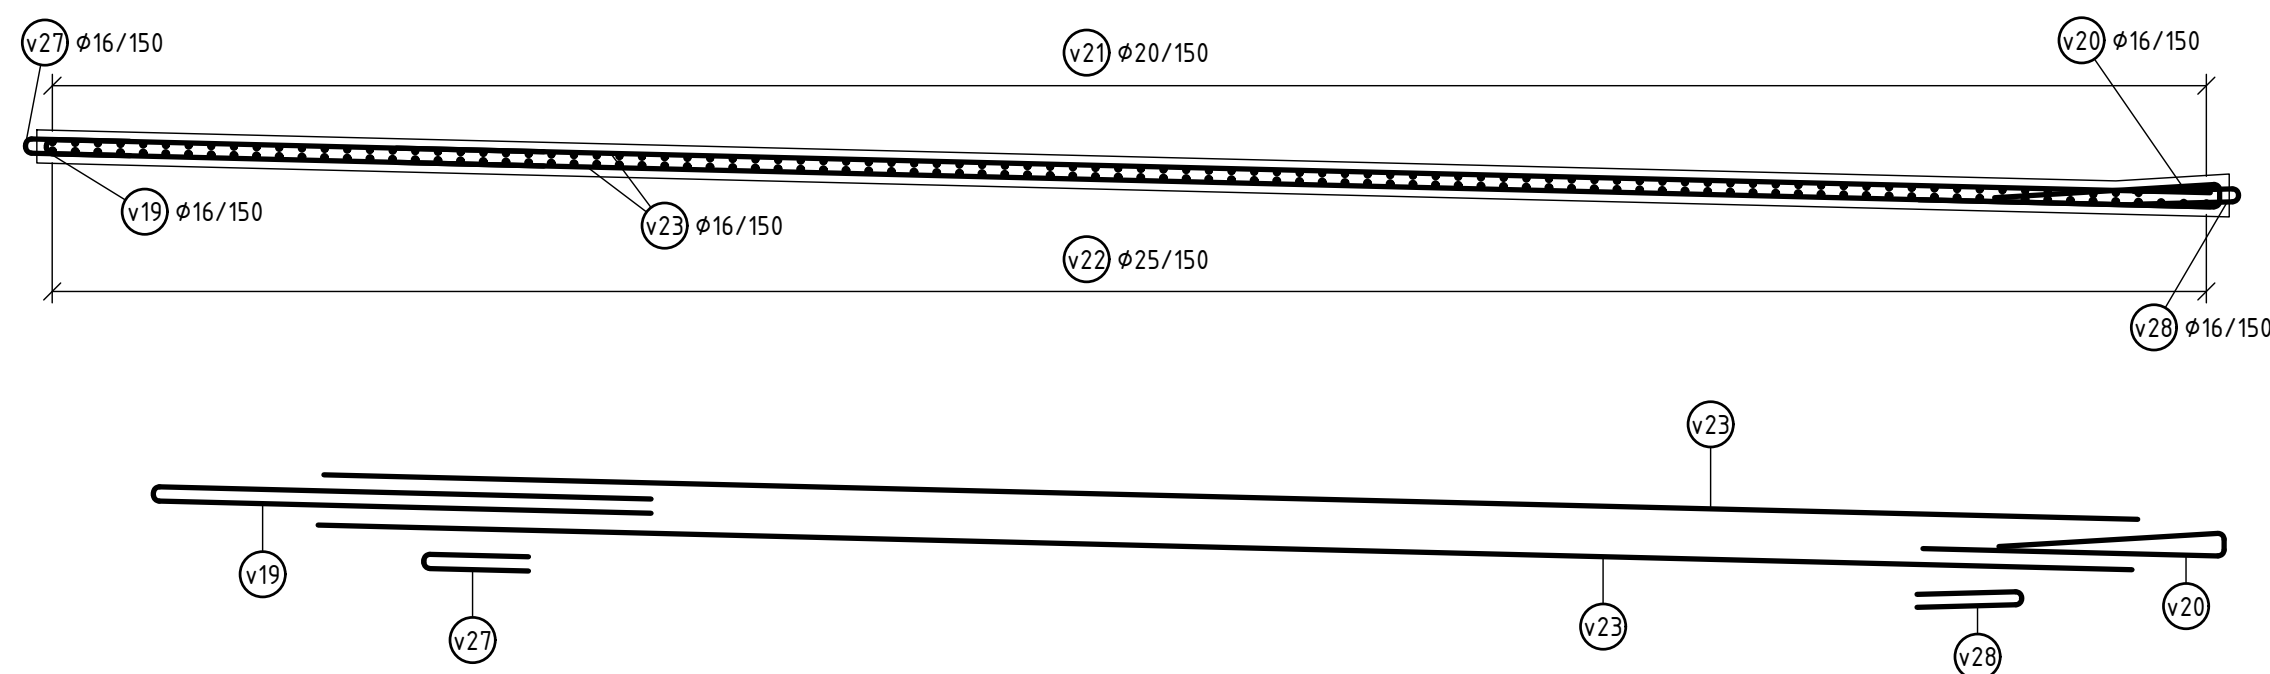

ŘEZ KŘÍDLEM 1, 2, 3, 4
1:50

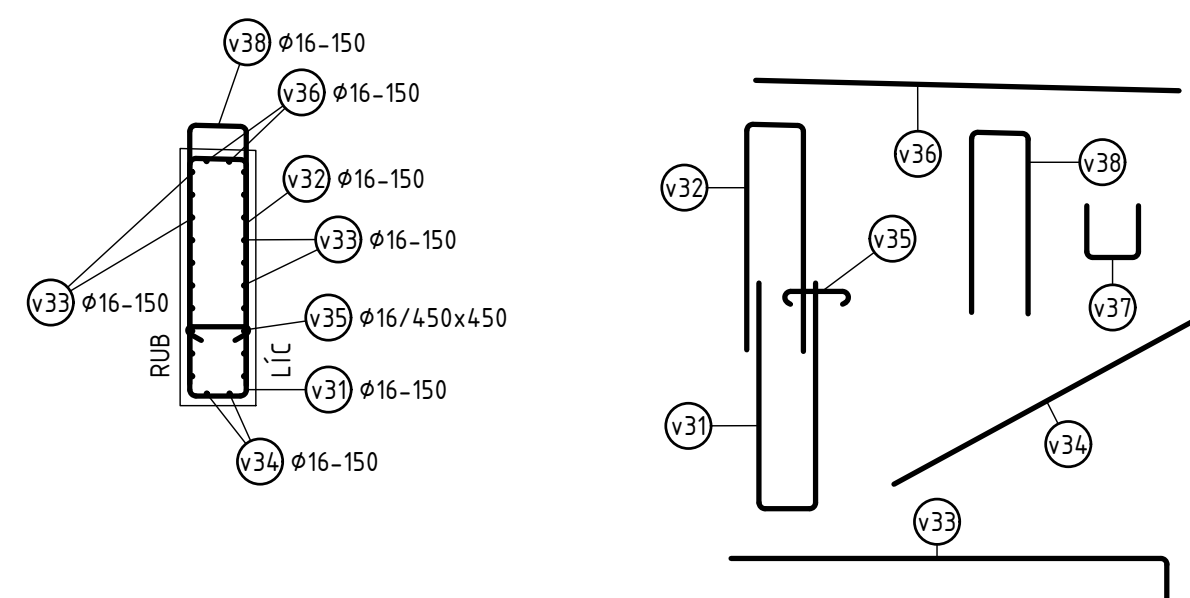

POZNÁMKY:

- NEDÍLNOU SOUČÁSTÍ VÝKRESU JSOU POZNÁMKY A SPECIFIKACE UVEDENÉ NA VÝKRESE
POZNÁMEK A TECHNICKÝCH SPECIFIKACÍ

Souřadnicový systém: S-JTSK
Výškový systém: Bpv

SO 202 MOST NA I/16 PŘES VALSKOU SVODNICI V KM 2,695



Ředitelství silnic a dálnic s. p.
Čerčanská 2023/12, Krč, 140 00 Praha 4



Valbek, spol. s r.o.
Vaňurova 505/17
460 07 Liberec 3



Vypracoval	A. MICHALIKOVÁ	<i>M. Michalíková</i>	Zak. číslo	21-L113-001
Zodp. projektant	ING. O. BAKHMET		Datum	02/2025
Tech. kontrola	ING. I. BELDA	<i>I. Belda</i>	Stupeň	PPDS
Akce	I/16 MLADÁ BOLESLAV - MARTINOVICE		Počet formátů	8x A4
			Měřítko	1:50
			Č. přílohy	Paré
Příloha	SCHÉMATICKÉ VÝKRESY VÝZTUŽE		301	

