
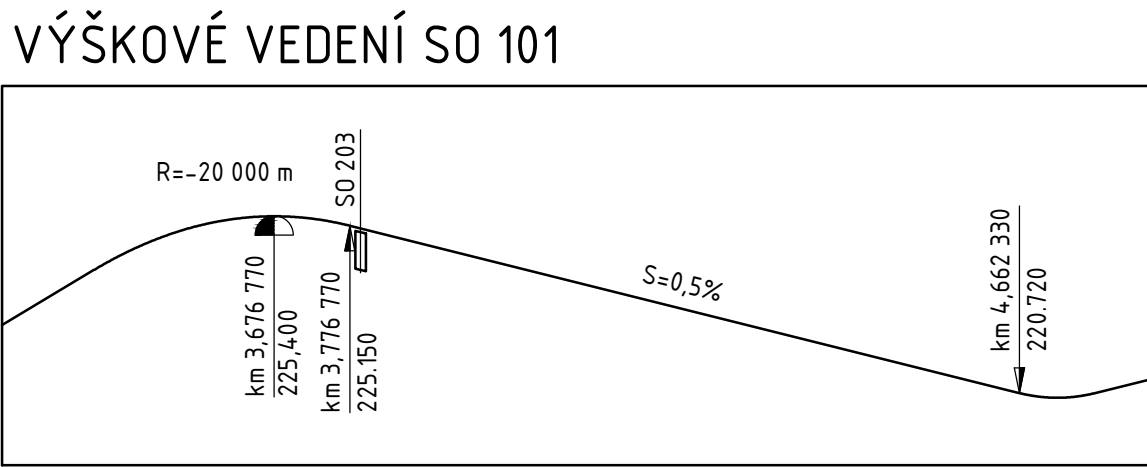
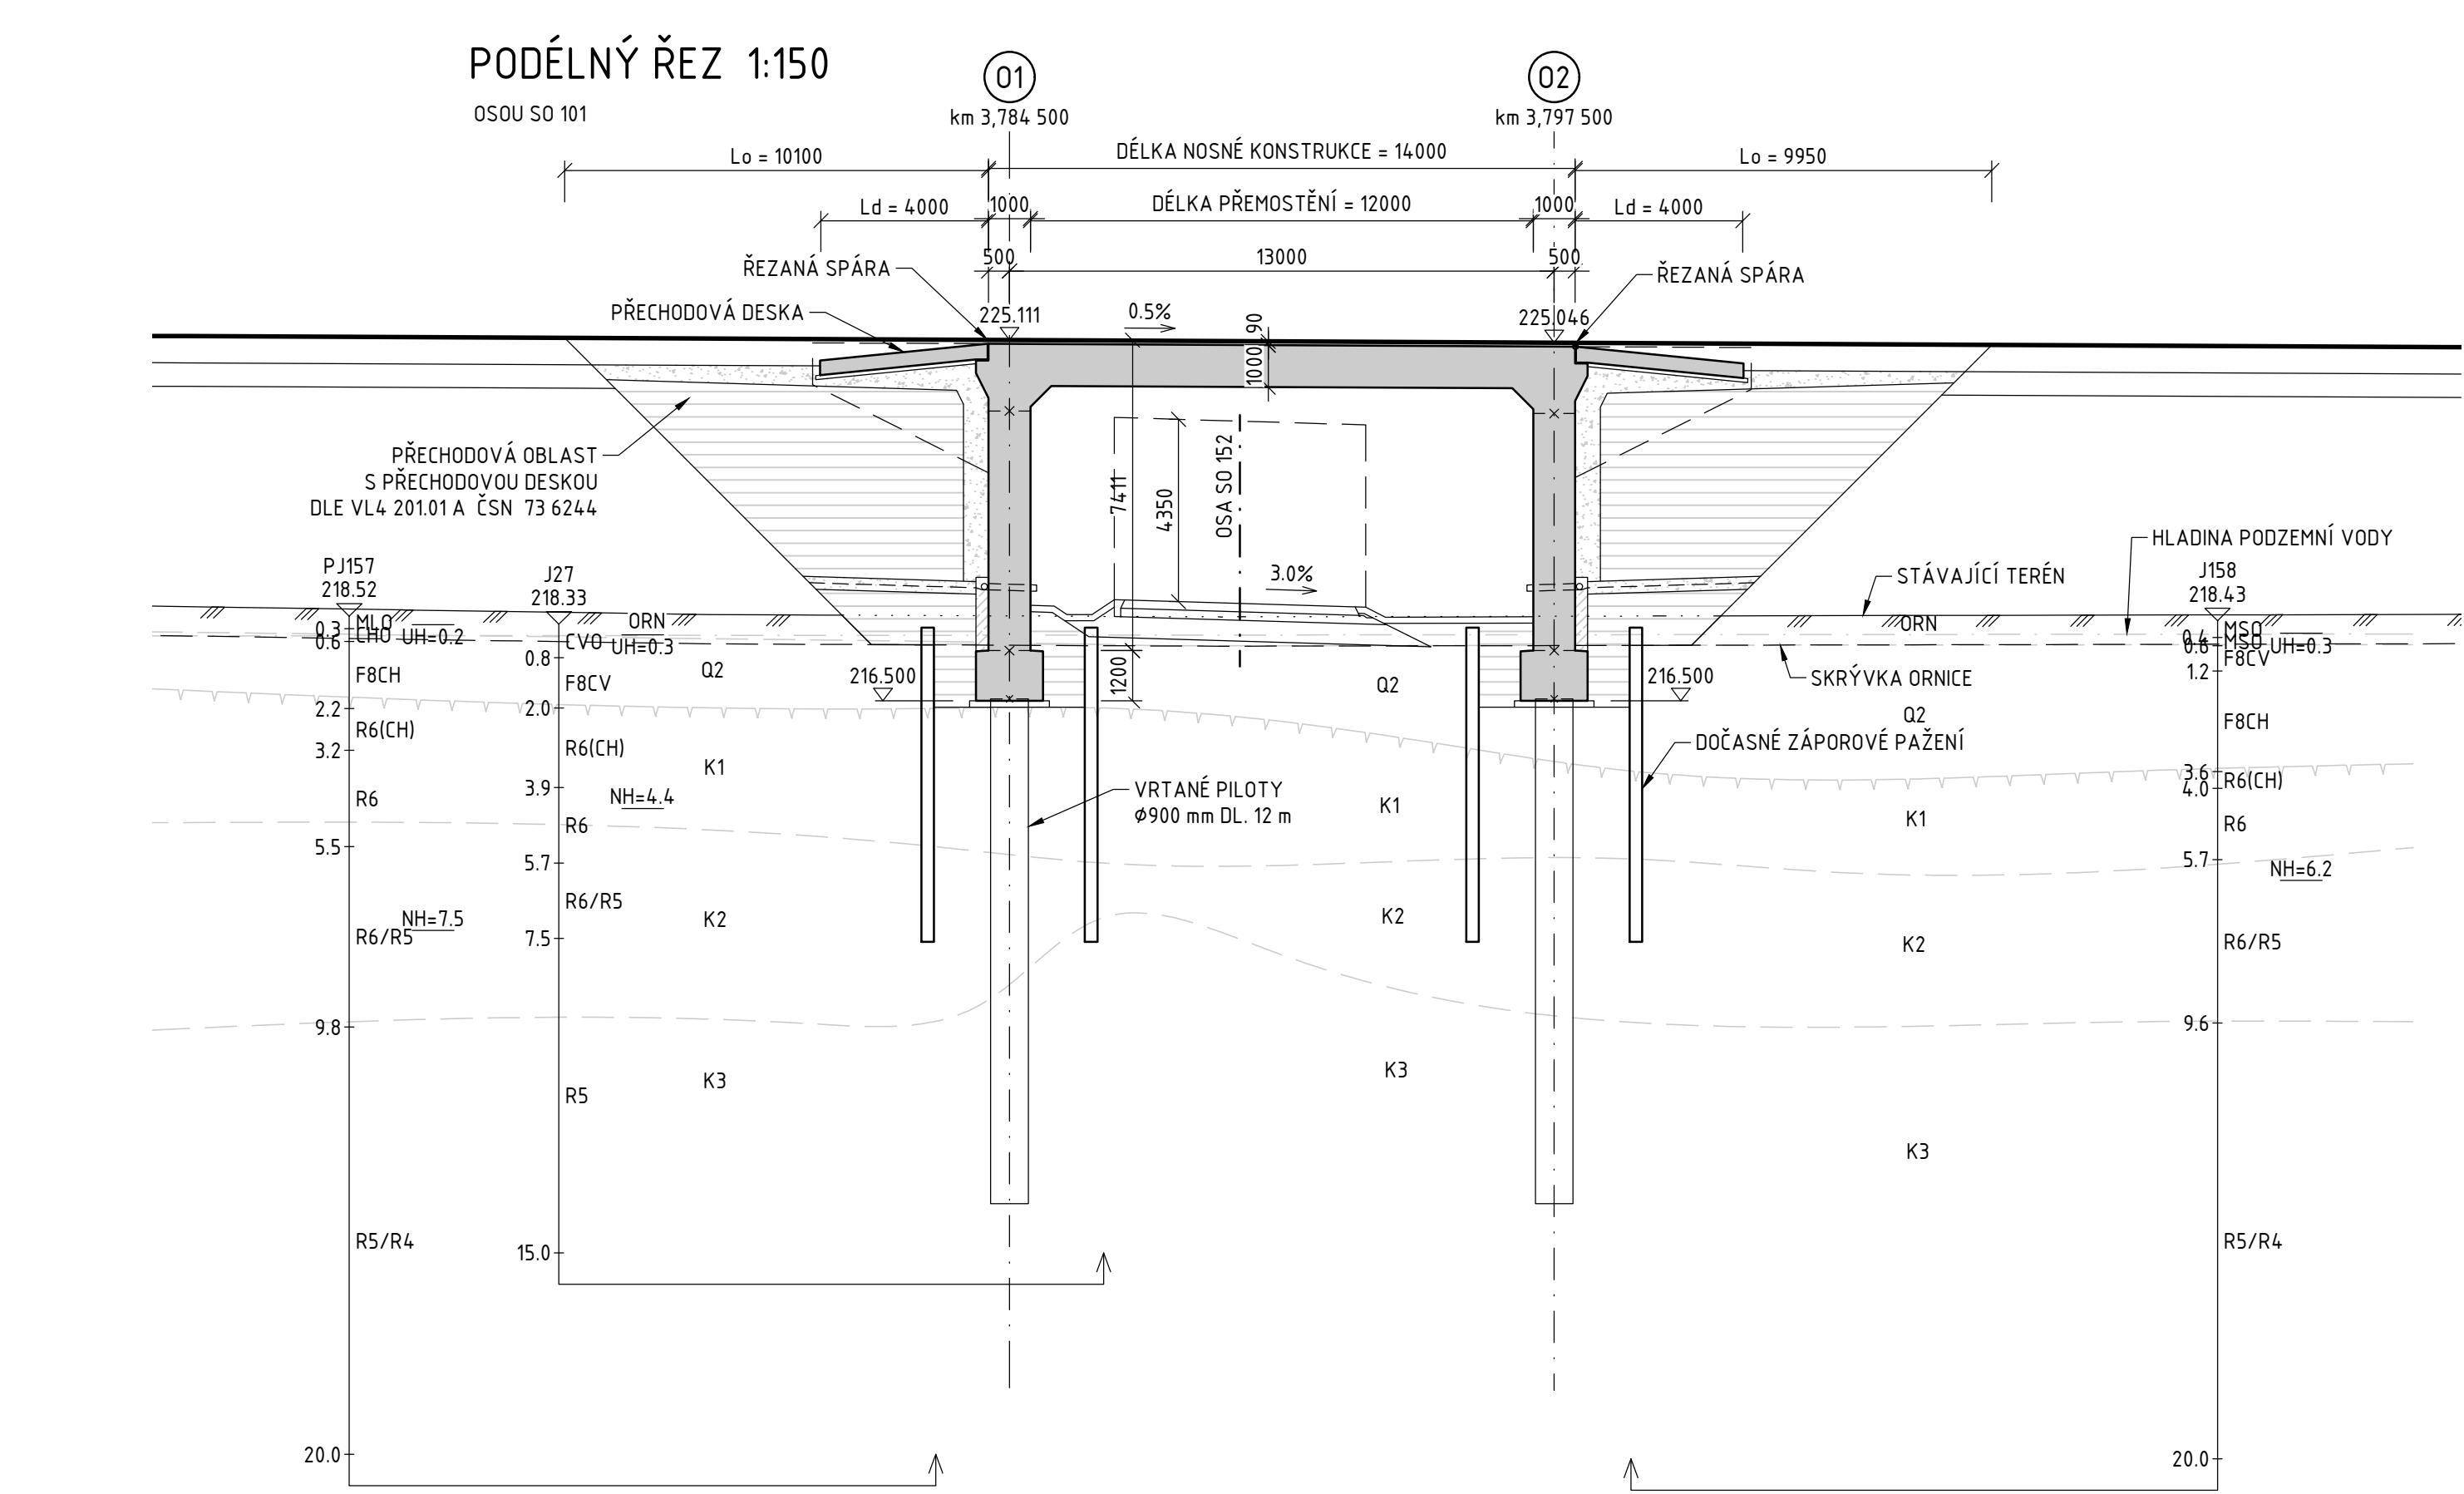


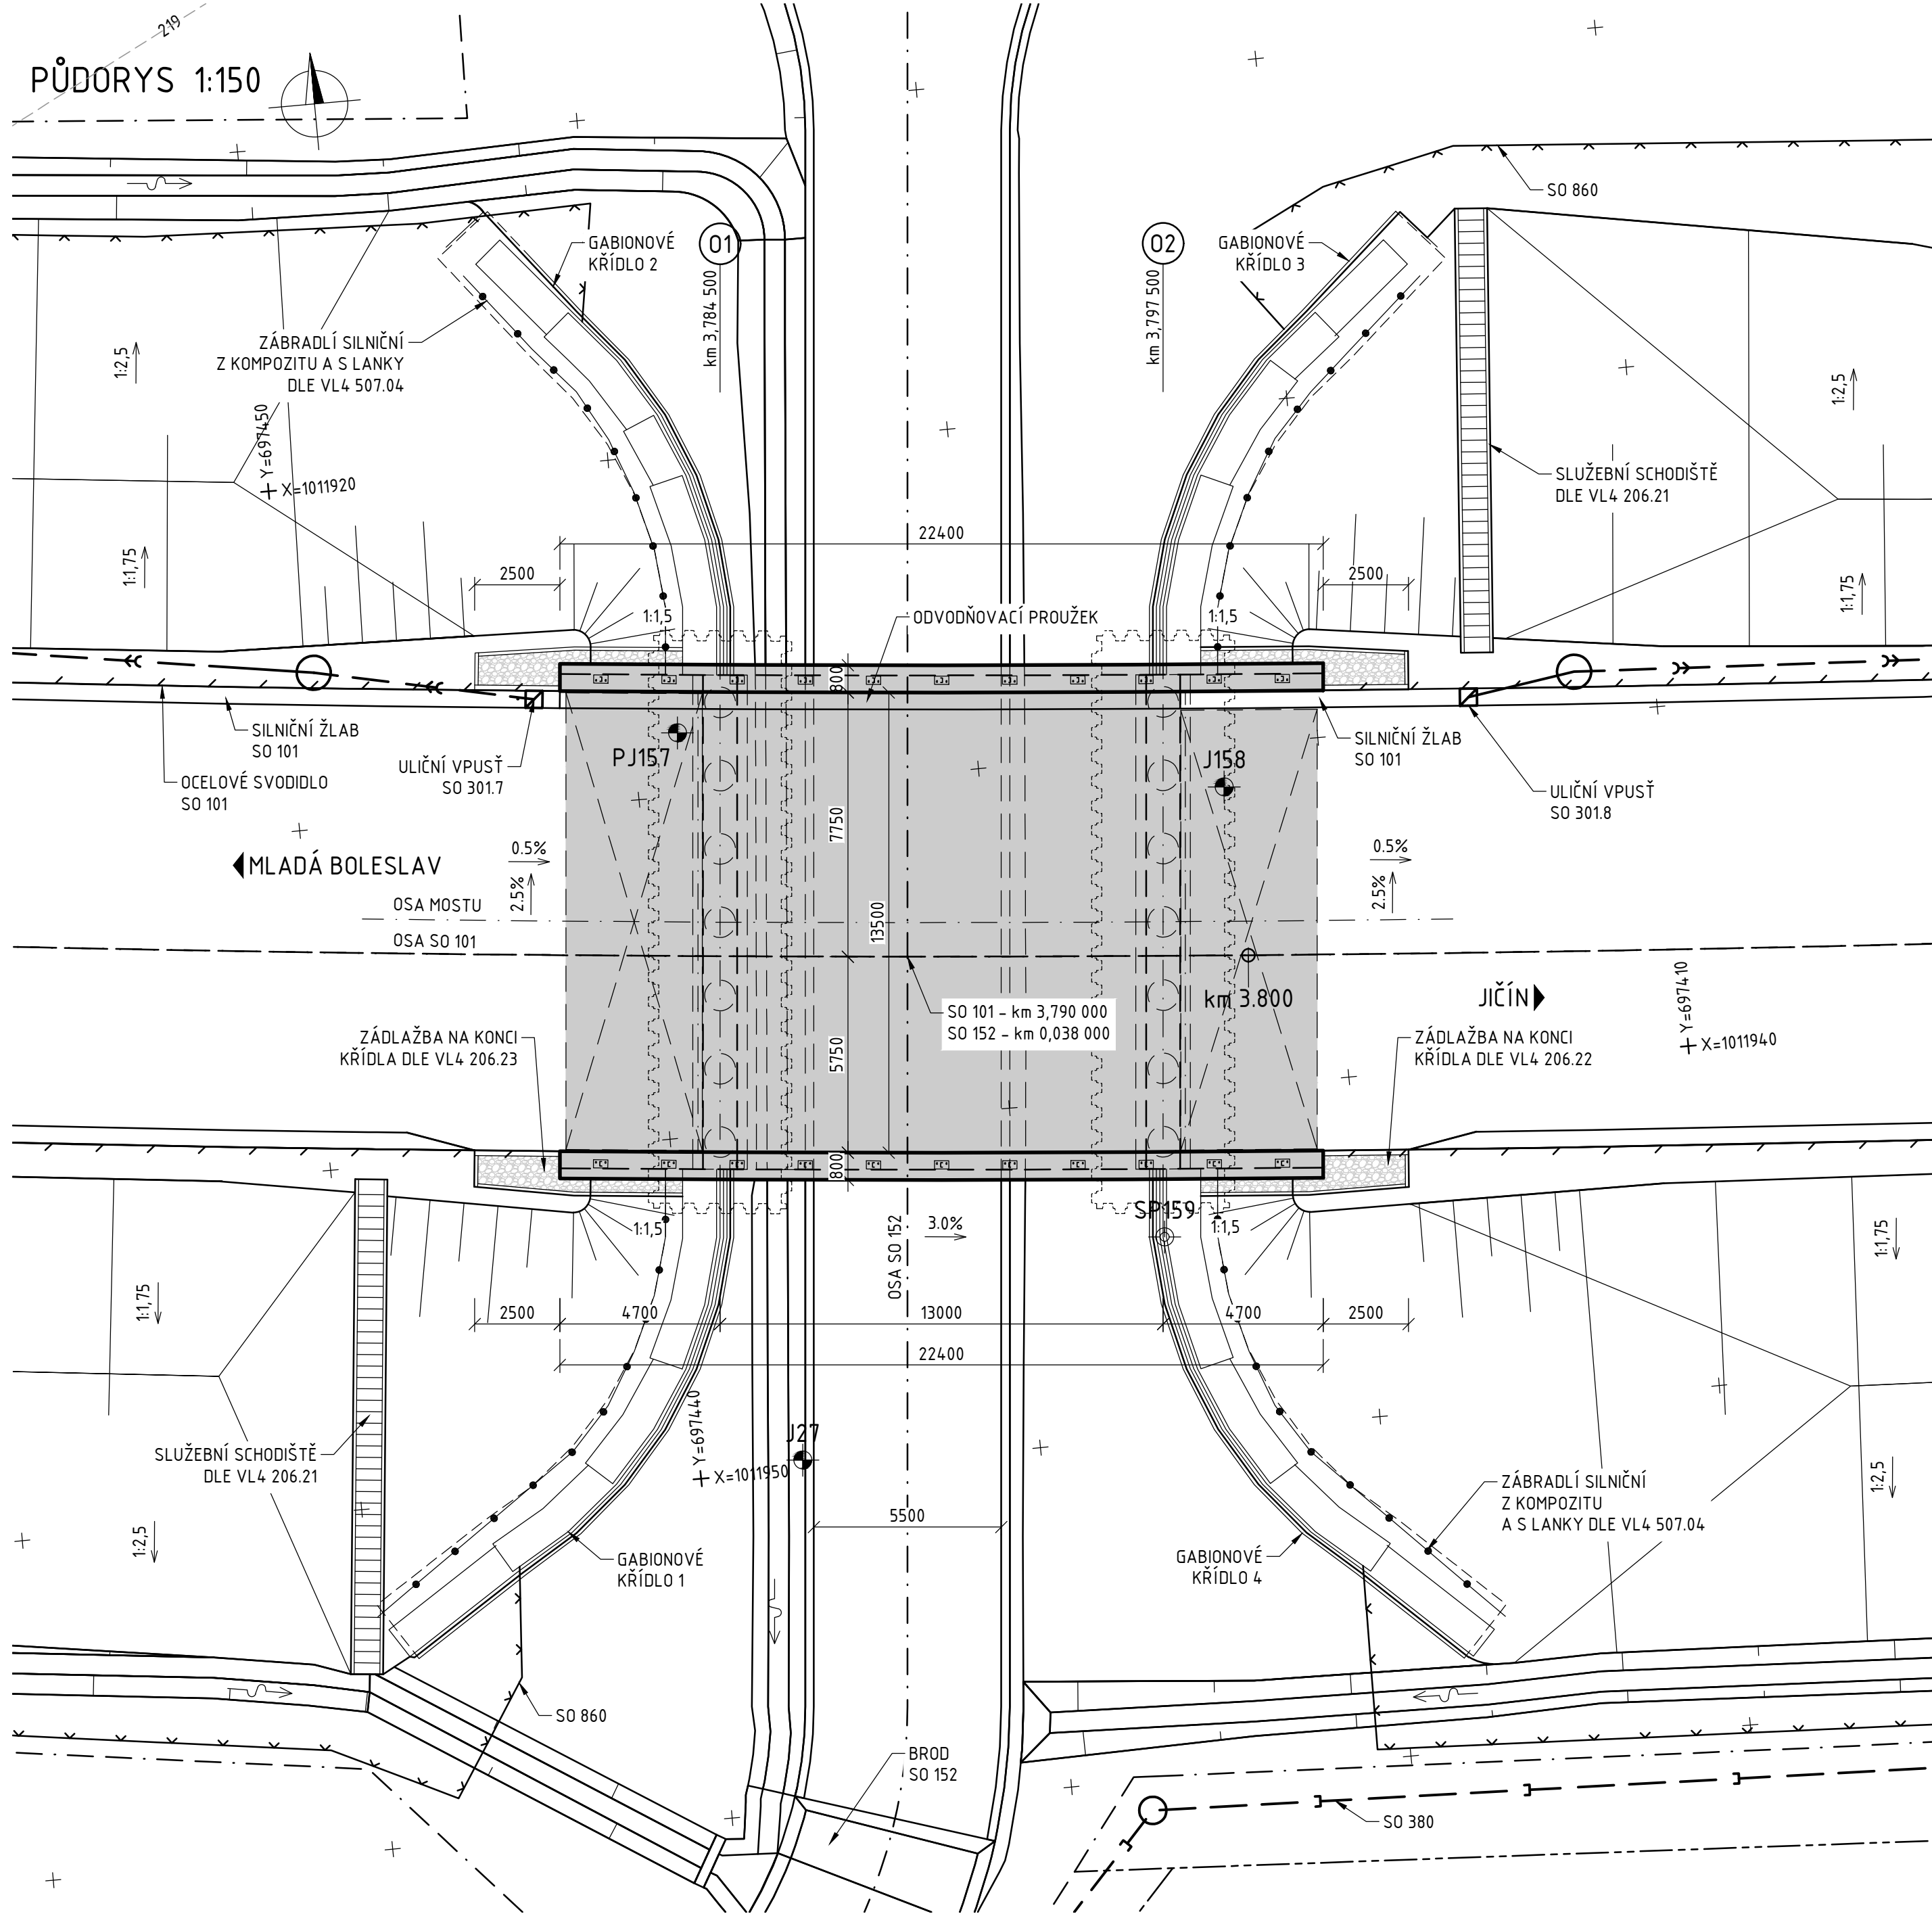



SMĚROVÉ VEDENÍ SO 101

STANIČENÍ	X	Y	PARAMETR
km 3.339 39	697 863.226	1 011 811.964	R = -1200 m
km 3.889 79	697 332.935	1 011 940.249	

SOUVISEJÍCÍ OBJEKTY:

- SO 020 PŘÍPRAVA ÚZEMÍ
- SO 101 SILNICE I/16 MLADÁ BOLESLAV - MARTINOVICE
- SO 152 PŘÍSTUPY NA POZEMKY V K.Ú. ŽIDNĚVES
- SO 190 DOPRAVNÍ ZNAČENÍ
- SO 301.x ODVODNĚNÍ I/16
- SO 380 ÚPRAVY MELIORACÍ ŽÚ - KÚ
- SO 801 VEGETAČNÍ ÚPRAVY
- SO 810 KÁČENÍ ZELENĚ
- SO 830 REKULTIVACE PLOCH DOČASNÉHO ZÁBORU
- SO 860 OPLOČENÍ

LEGENDA

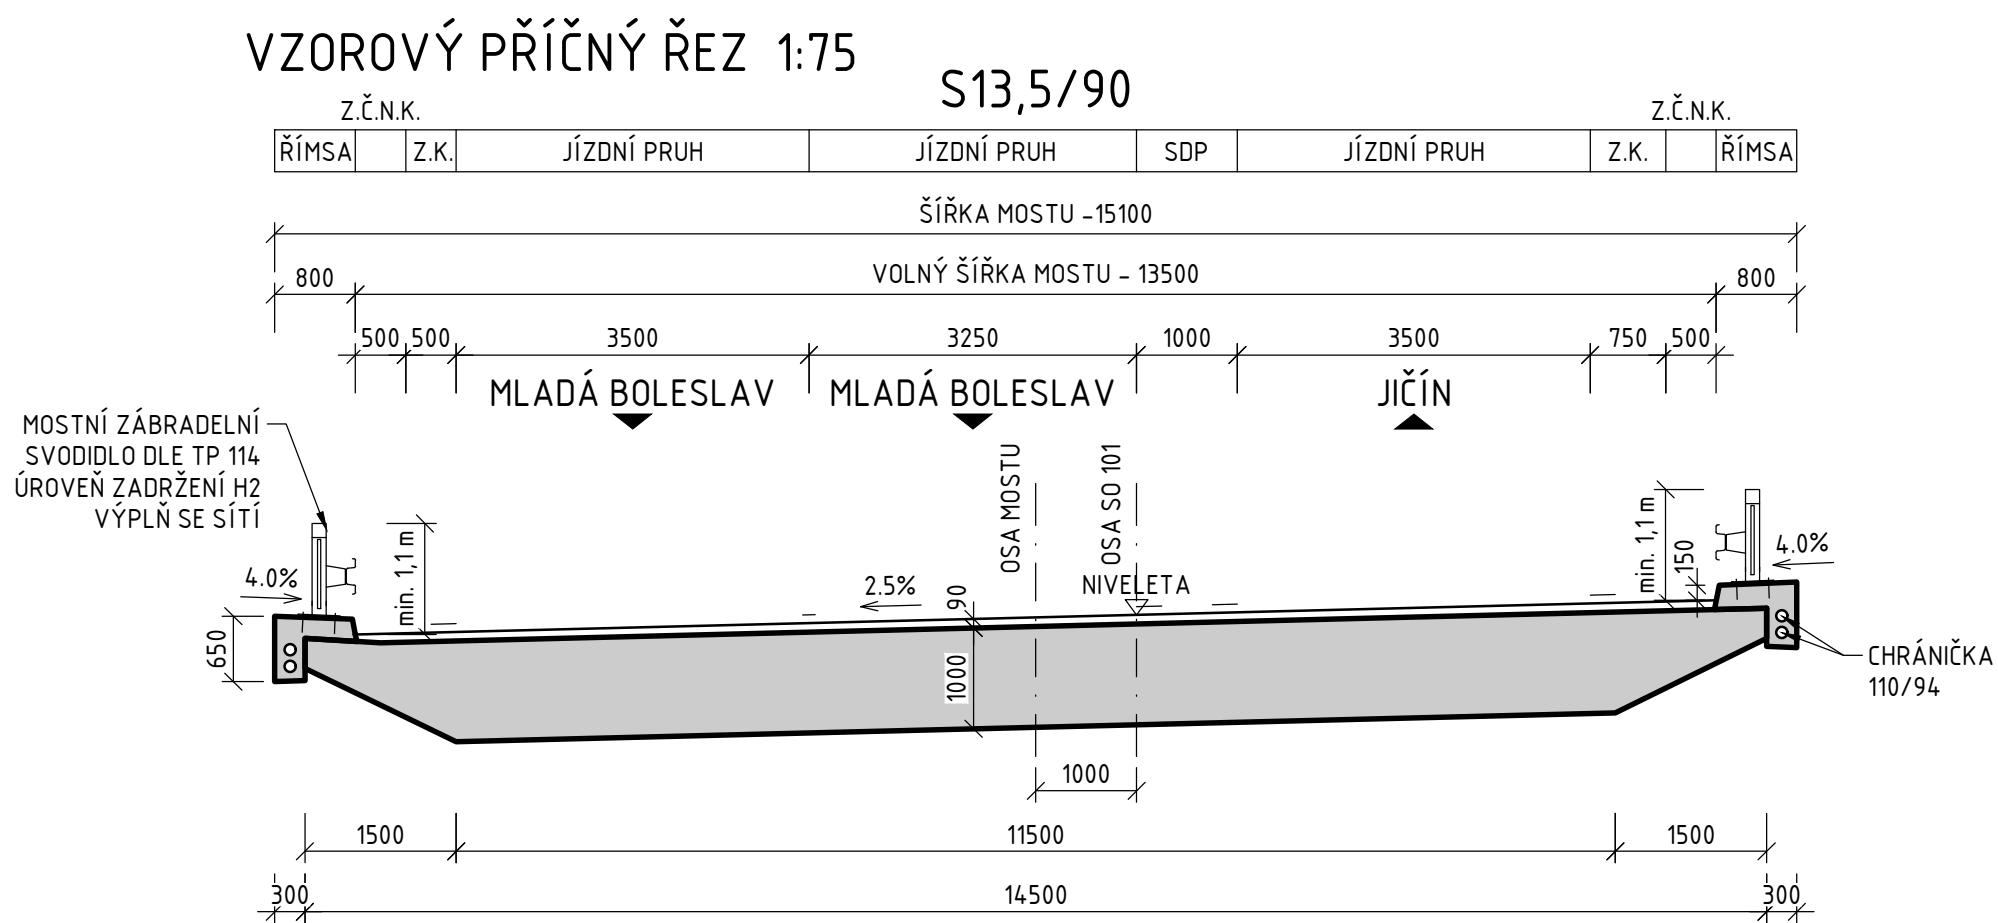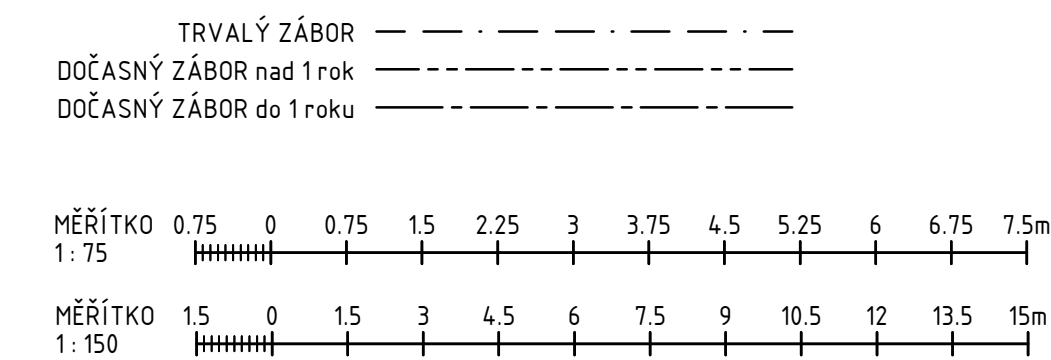

Souřadnicový systém: S-JTSK
Výškový systém: Bpv

SO 203 MOST NA I/16 PŘES PŘELOŽKU POLNÍ CESTY V KM 3,790

Objednatel:
ŘEDITELSTVÍ SILNIC A DÁLNIC
Ředitelství silnic a dálnic s. p.
Čerčanská 2023/12, Krč, 140 00 Praha 4

Valbek, spol. s r.o.
Vaňurova 505/17
460 07 Liberec 3

	Vypracoval	L. MARTÍNEK		Zak. číslo	21-L113-001	
	Zodp. projektant	ING. I. BELDA		Datum	02/2025	
	Tech. kontrola	ING. I. BELDA		Stupeň	PDPS	
	Akce	I/16 MLADÁ BOLESLAV - MARTINOVICE			Počet formátů	8x A4
Zhotovitel: Valbek, spol. s r.o. Vaňurova 505/17 460 07 Liberec 3	Příloha	PŮDORYS, PODÉLNÝ ŘEZ, VZOROVÝ PŘÍČNÝ ŘEZ			Měřítko	1:150,75
					Č. přílohy	Paré
					102	