




PŮDORYS 1:100

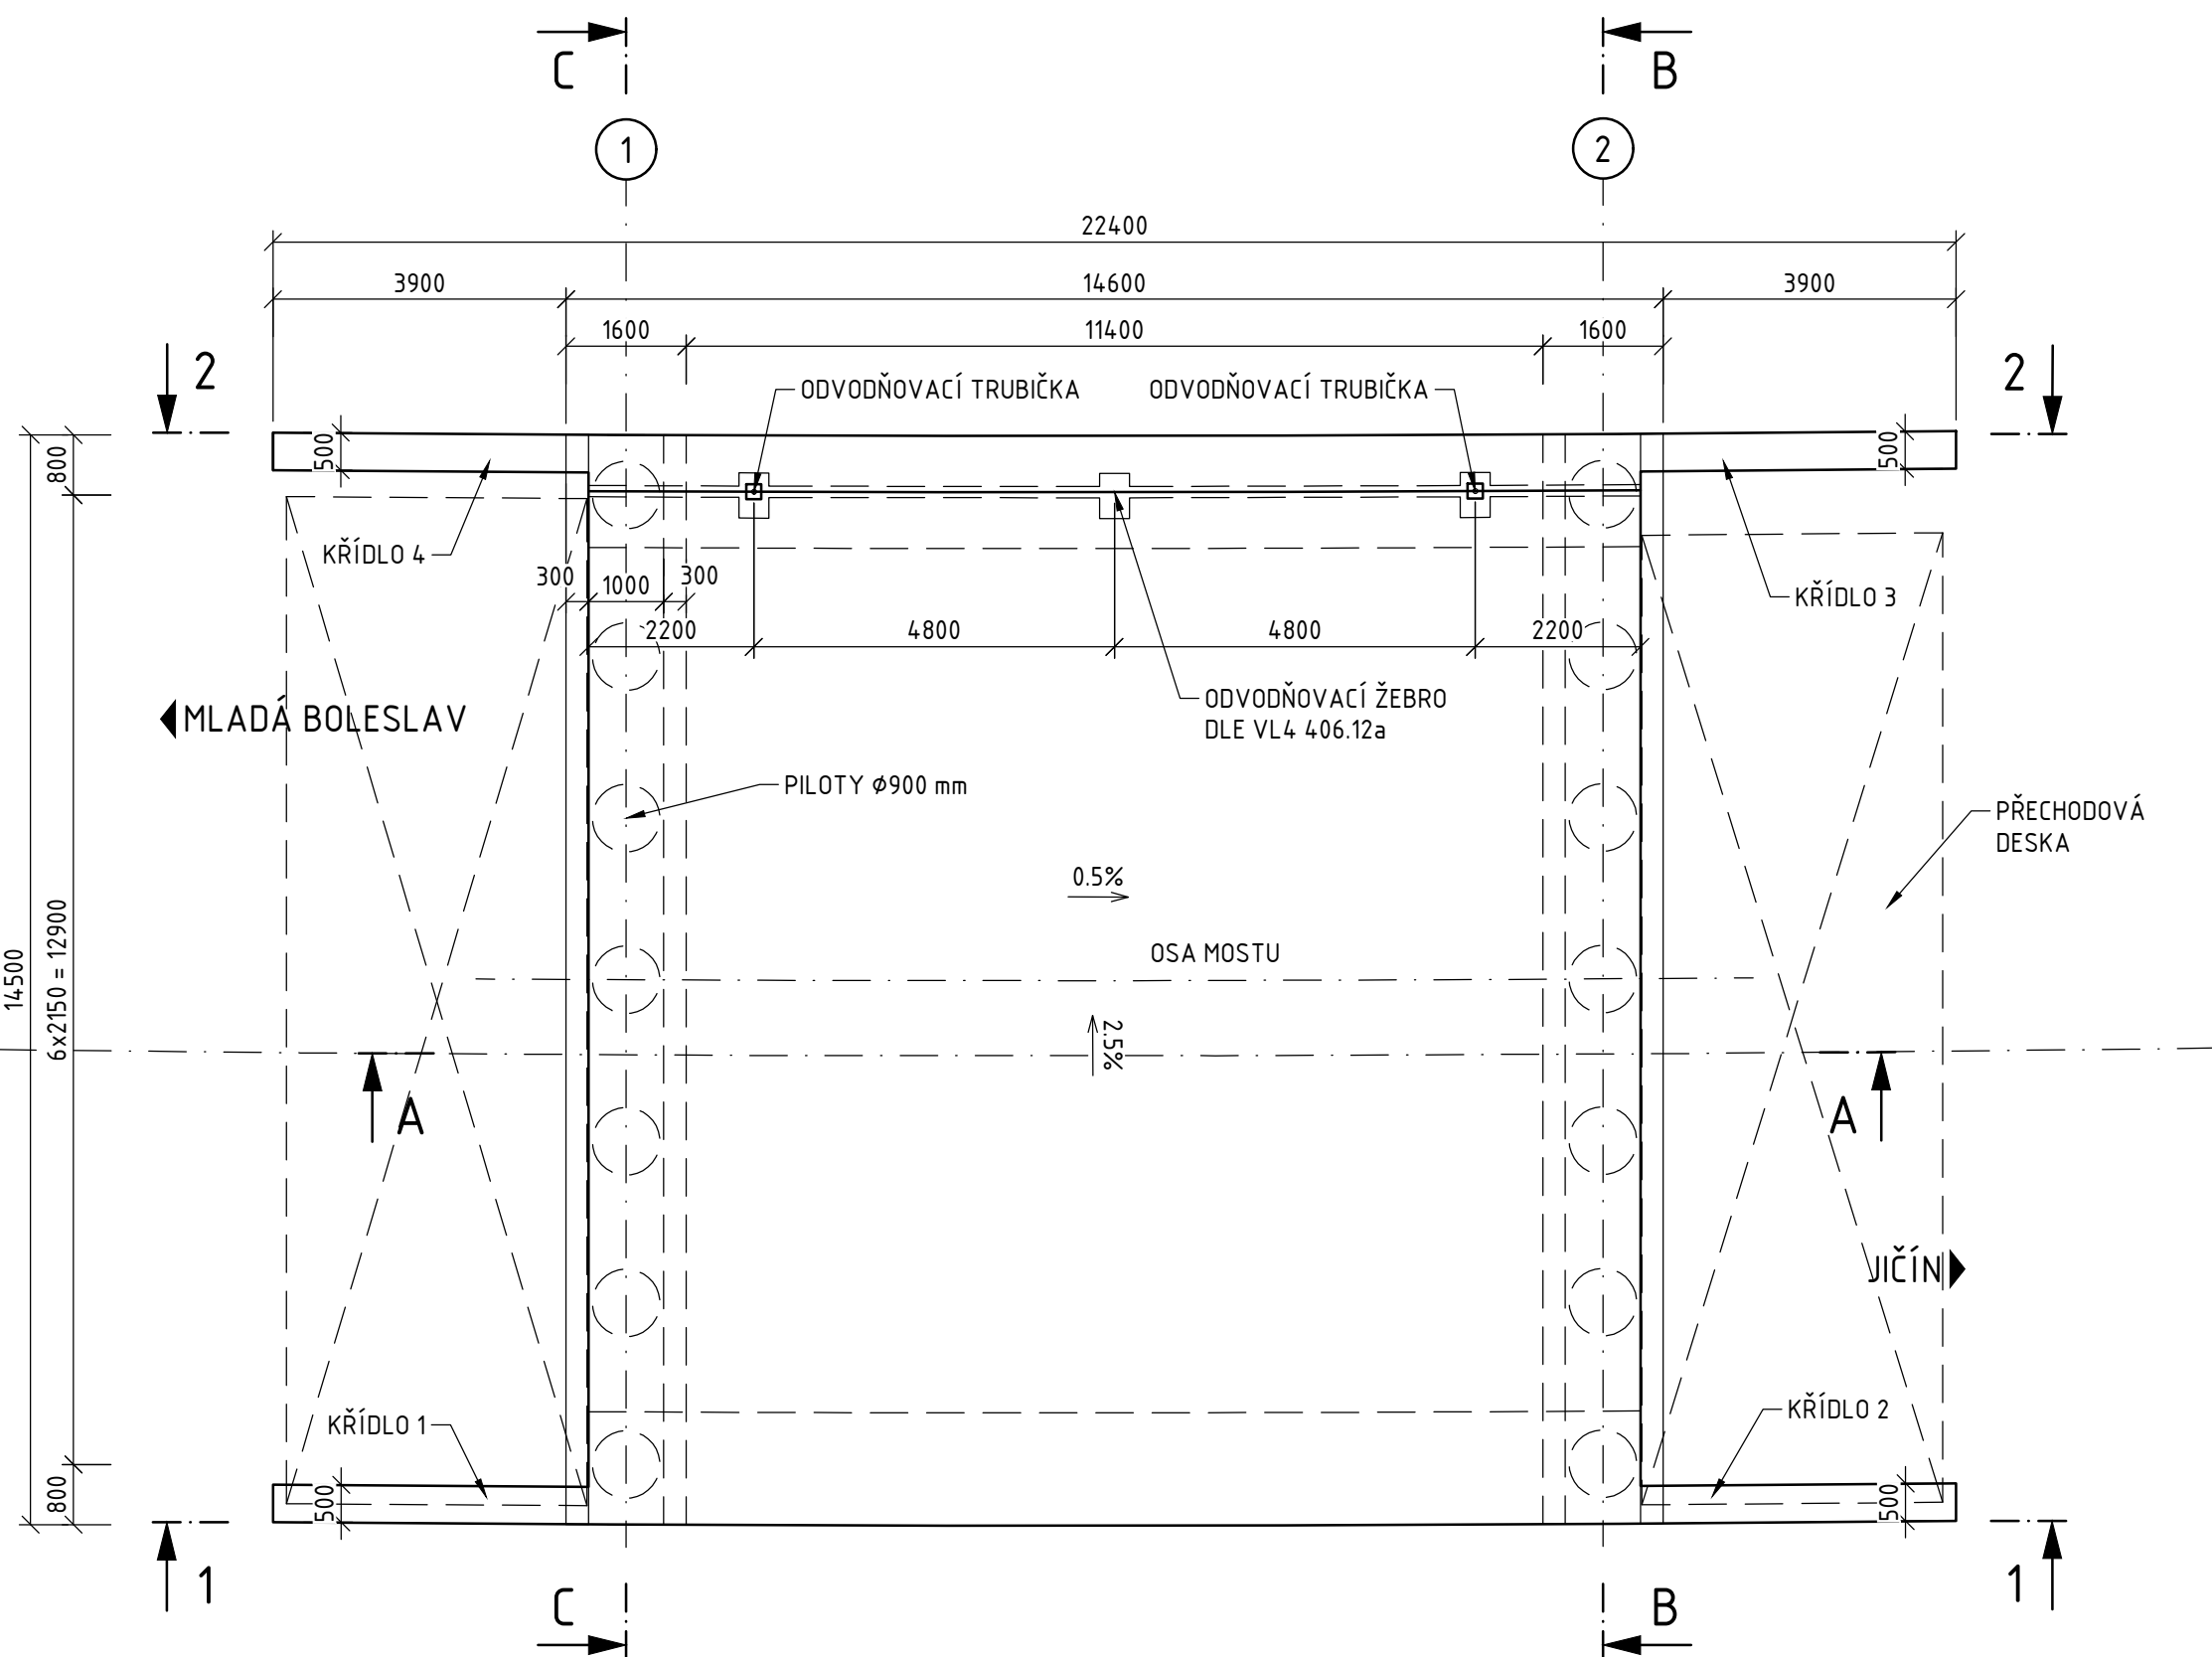



POHLED 1-1 1:100

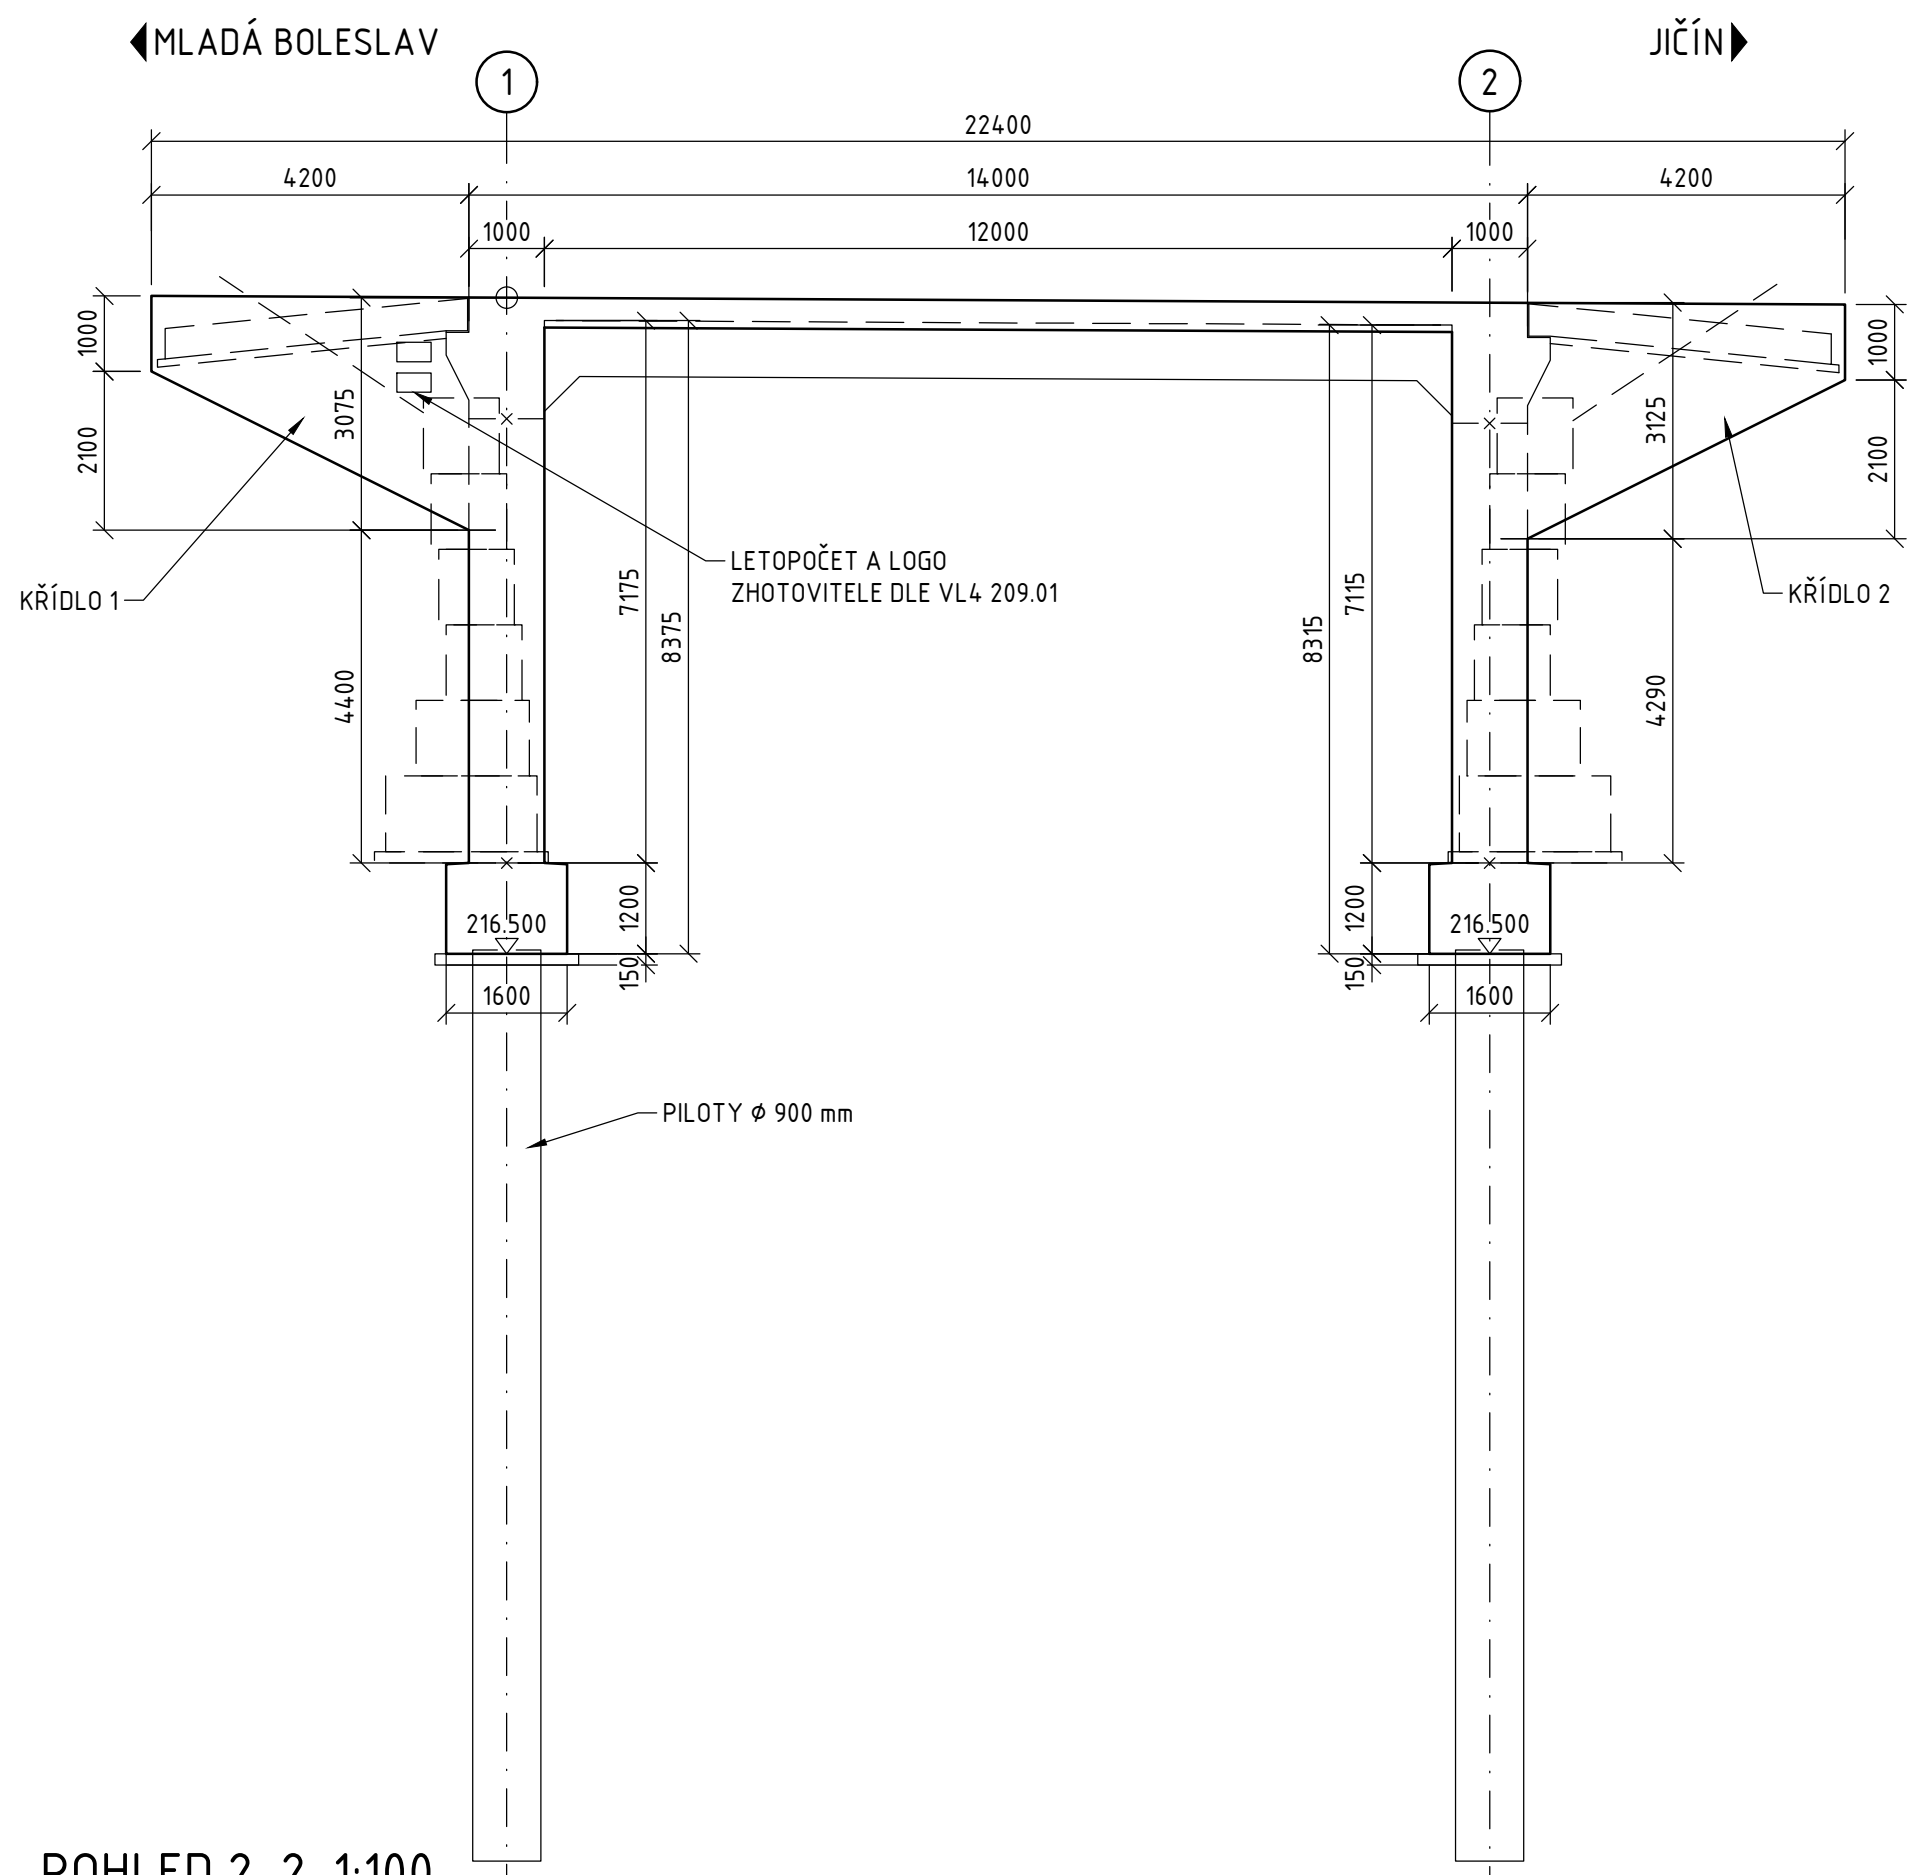

ŘEZ A-A 1:100

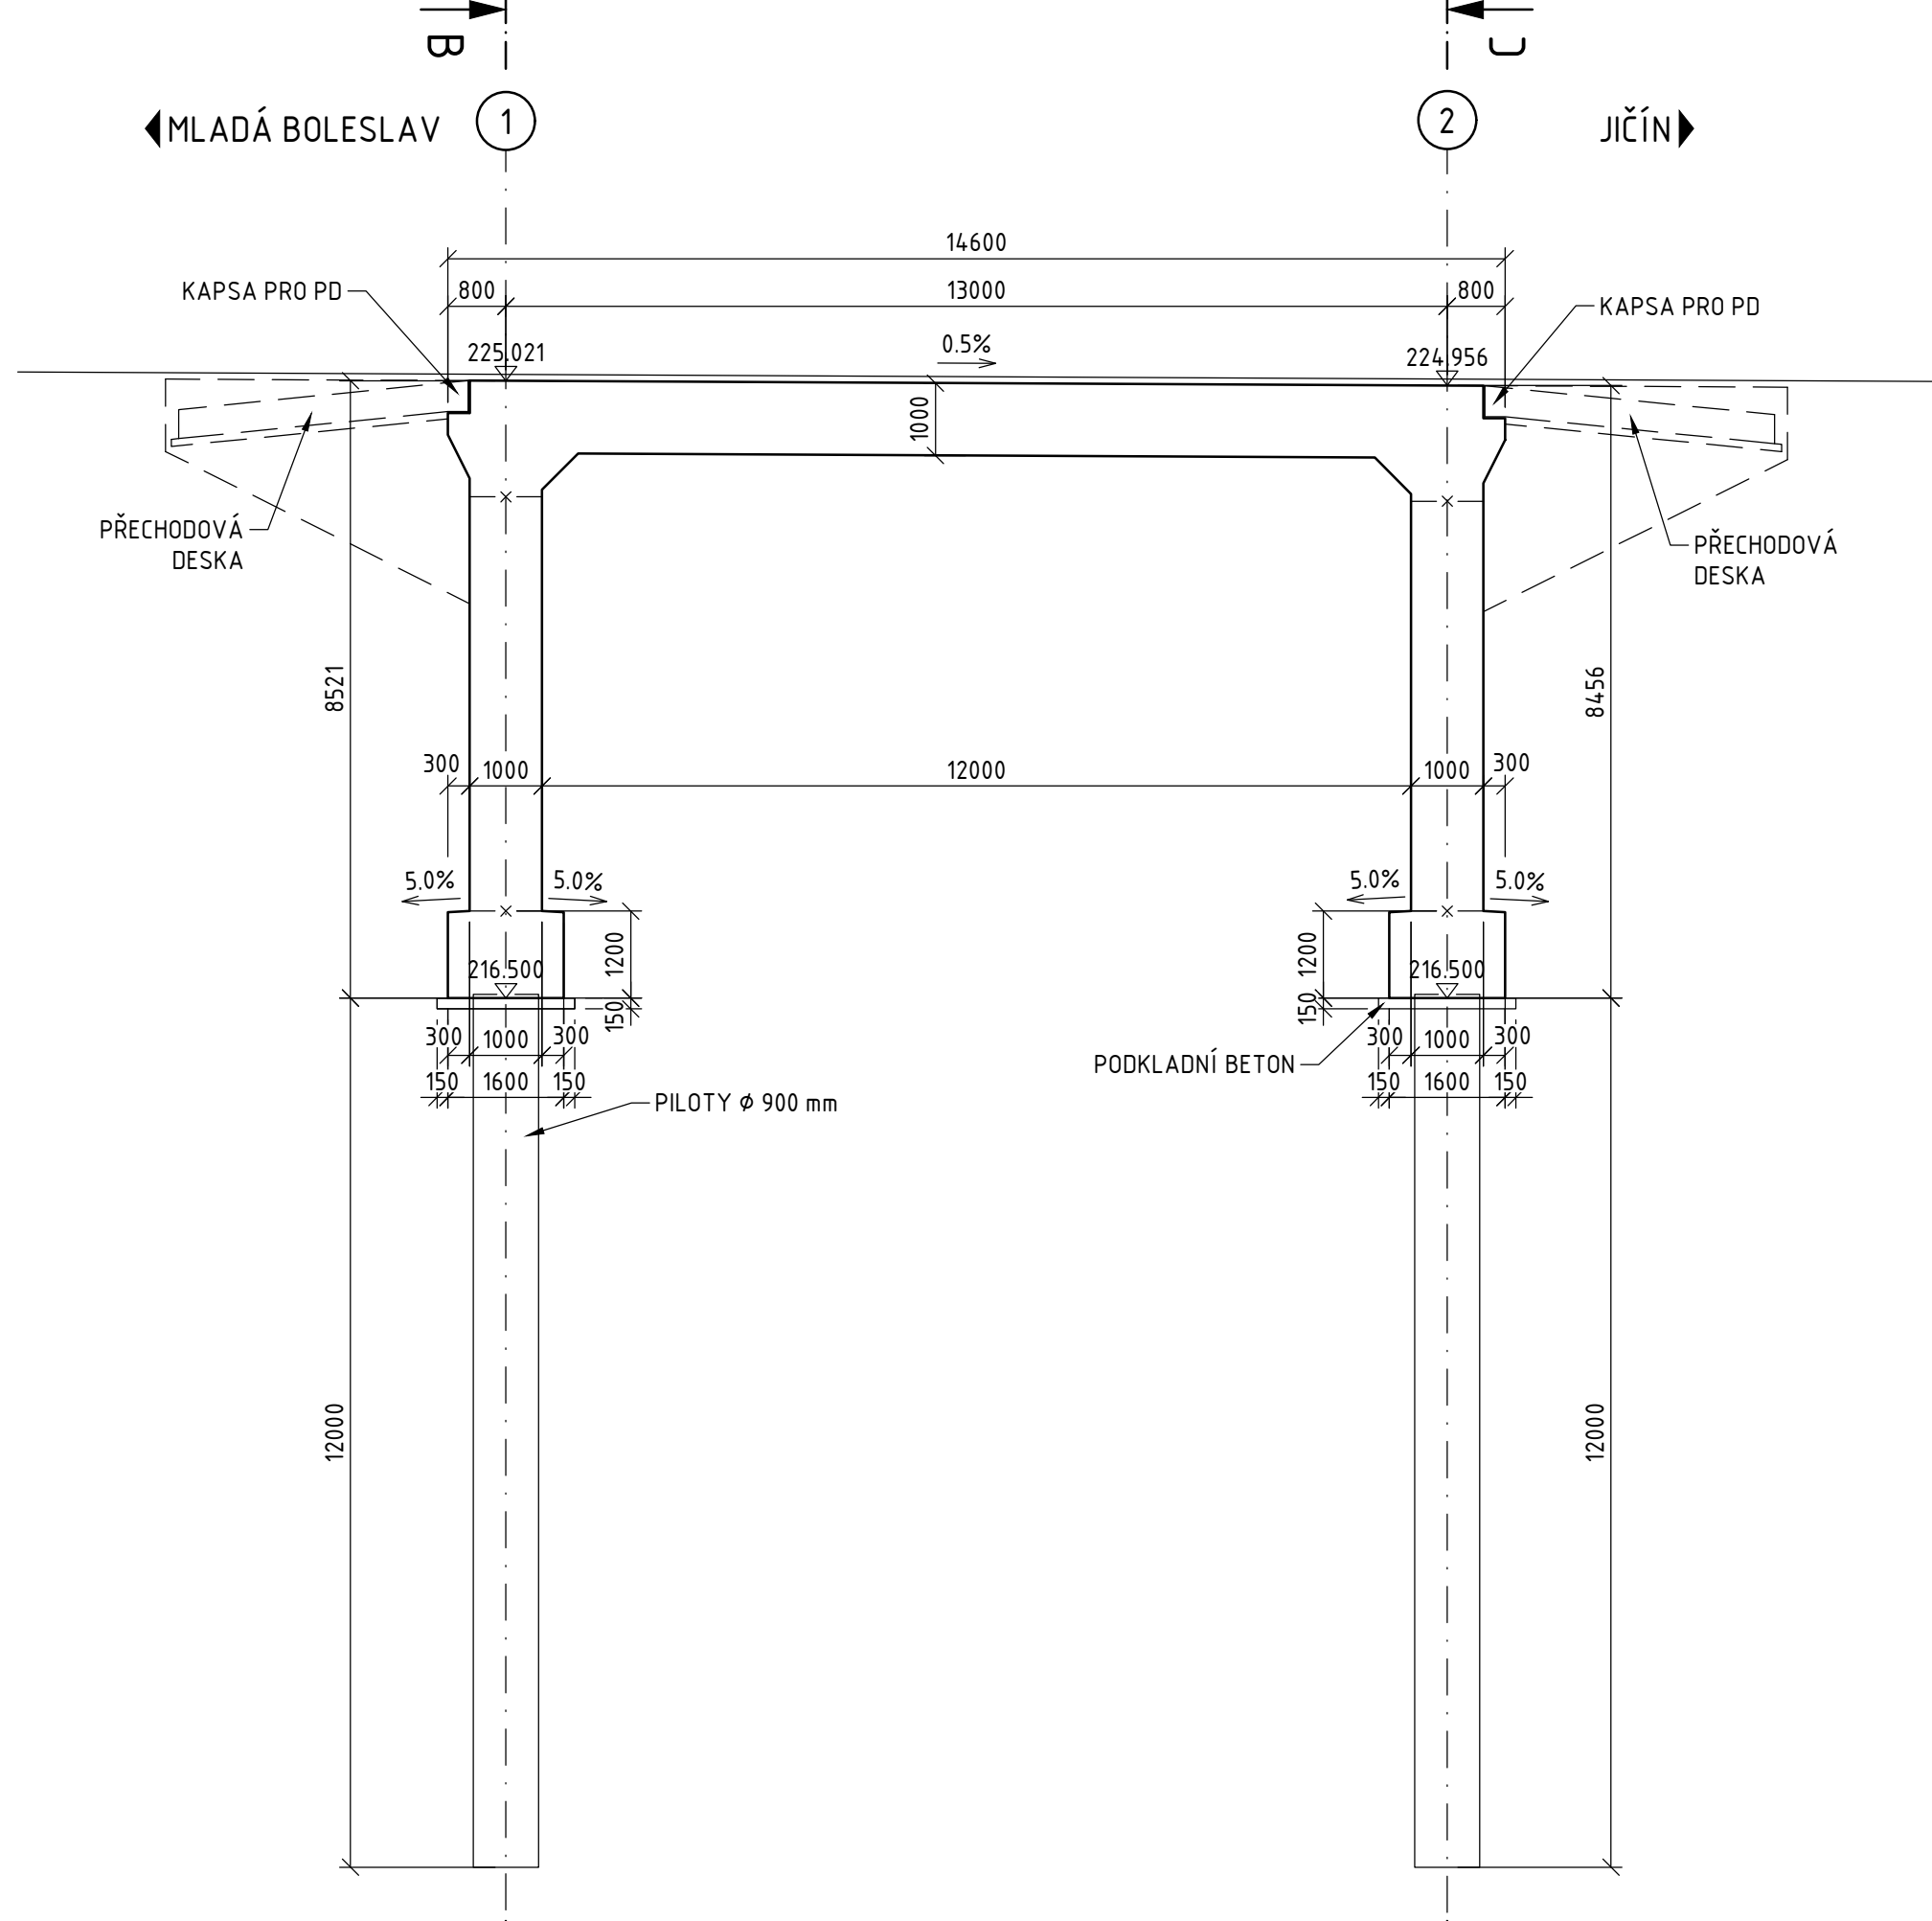

POHLED 2-2 1:100

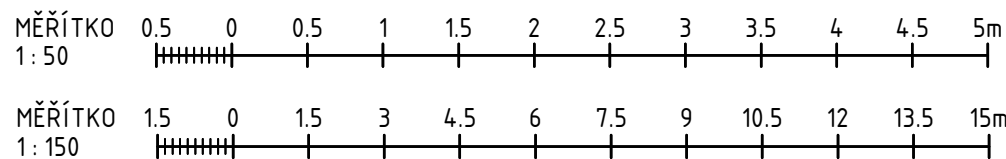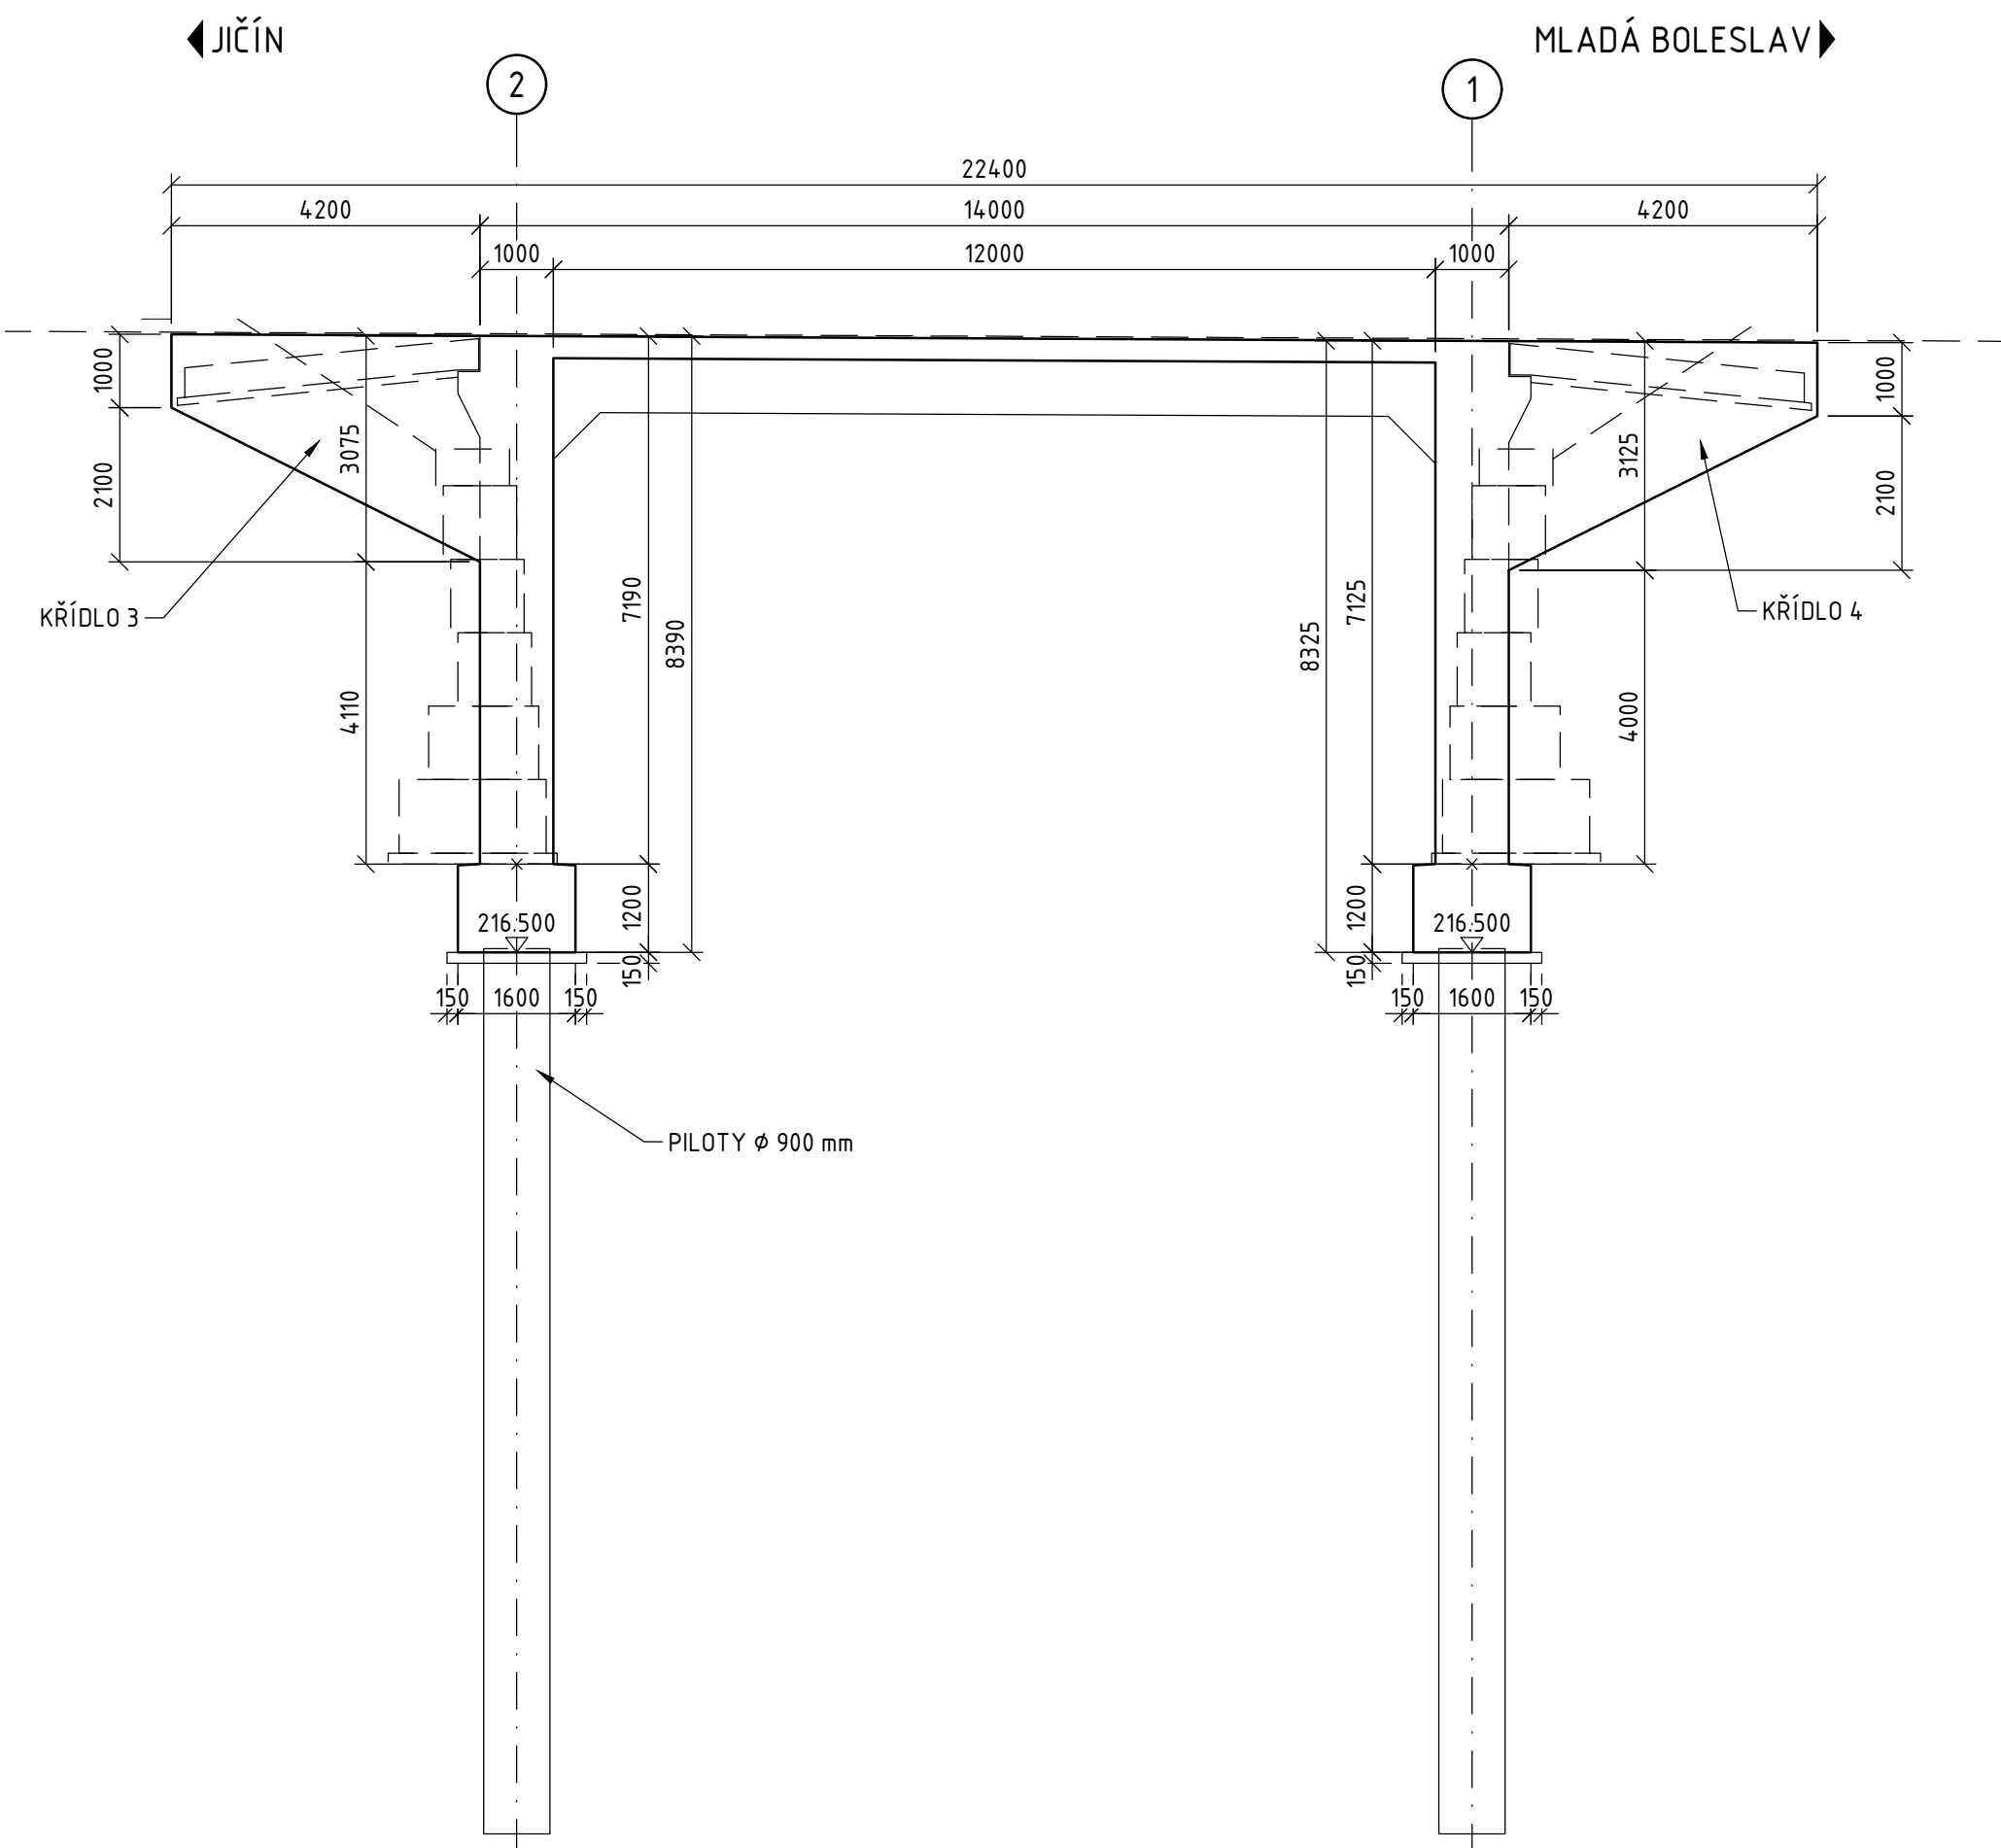

LEGENDA:

— x — PRACOVNÍ SPÁRA

POZNÁMKY:

- NEDÍLNOU SOUČÁSTÍ VÝKRESU JSOU POZNÁMKY A SPECIFIKACE UVEDENÉ NA VÝKRESE POZNÁMEK A TECHNICKÝCH SPECIFIKACÍ

Souřadnicový systém: S-JTSK
Výškový systém: BpV

SO 203 MOST NA I/16 PŘES PŘELOŽKU POLNÍ CESTY V KM 3,790

Objednatel:



Ředitelství silnic a dálnic s. p.
Čerčanská 2023/12, Krč, 140 00 Praha 4



Valbek, spol. s r.o.
Vaňurova 505/17
460 07 Liberec 3



Vypracoval	L. MARTÍNEK	Zak. číslo	21-L113-001
Zodp. projektant	ING. I. BELDA	Datum	02/2025
Tech. kontrola	ING. I. BELDA	Stupeň	PDPS
Akce	I/16 MLADÁ BOESLAV - MARTINOVICE		
Zhotovitel:	Příloha	Počet formátů	8x A4
Valbek, spol. s r.o. Vaňurova 505/17 460 07 Liberec 3	TVAR NOSNÉ KONSTRUKCE ČÁST 1	Měřítko	1:100,50
		Č. přílohy	Paré
			201