



ŘEZ B-B 1:100

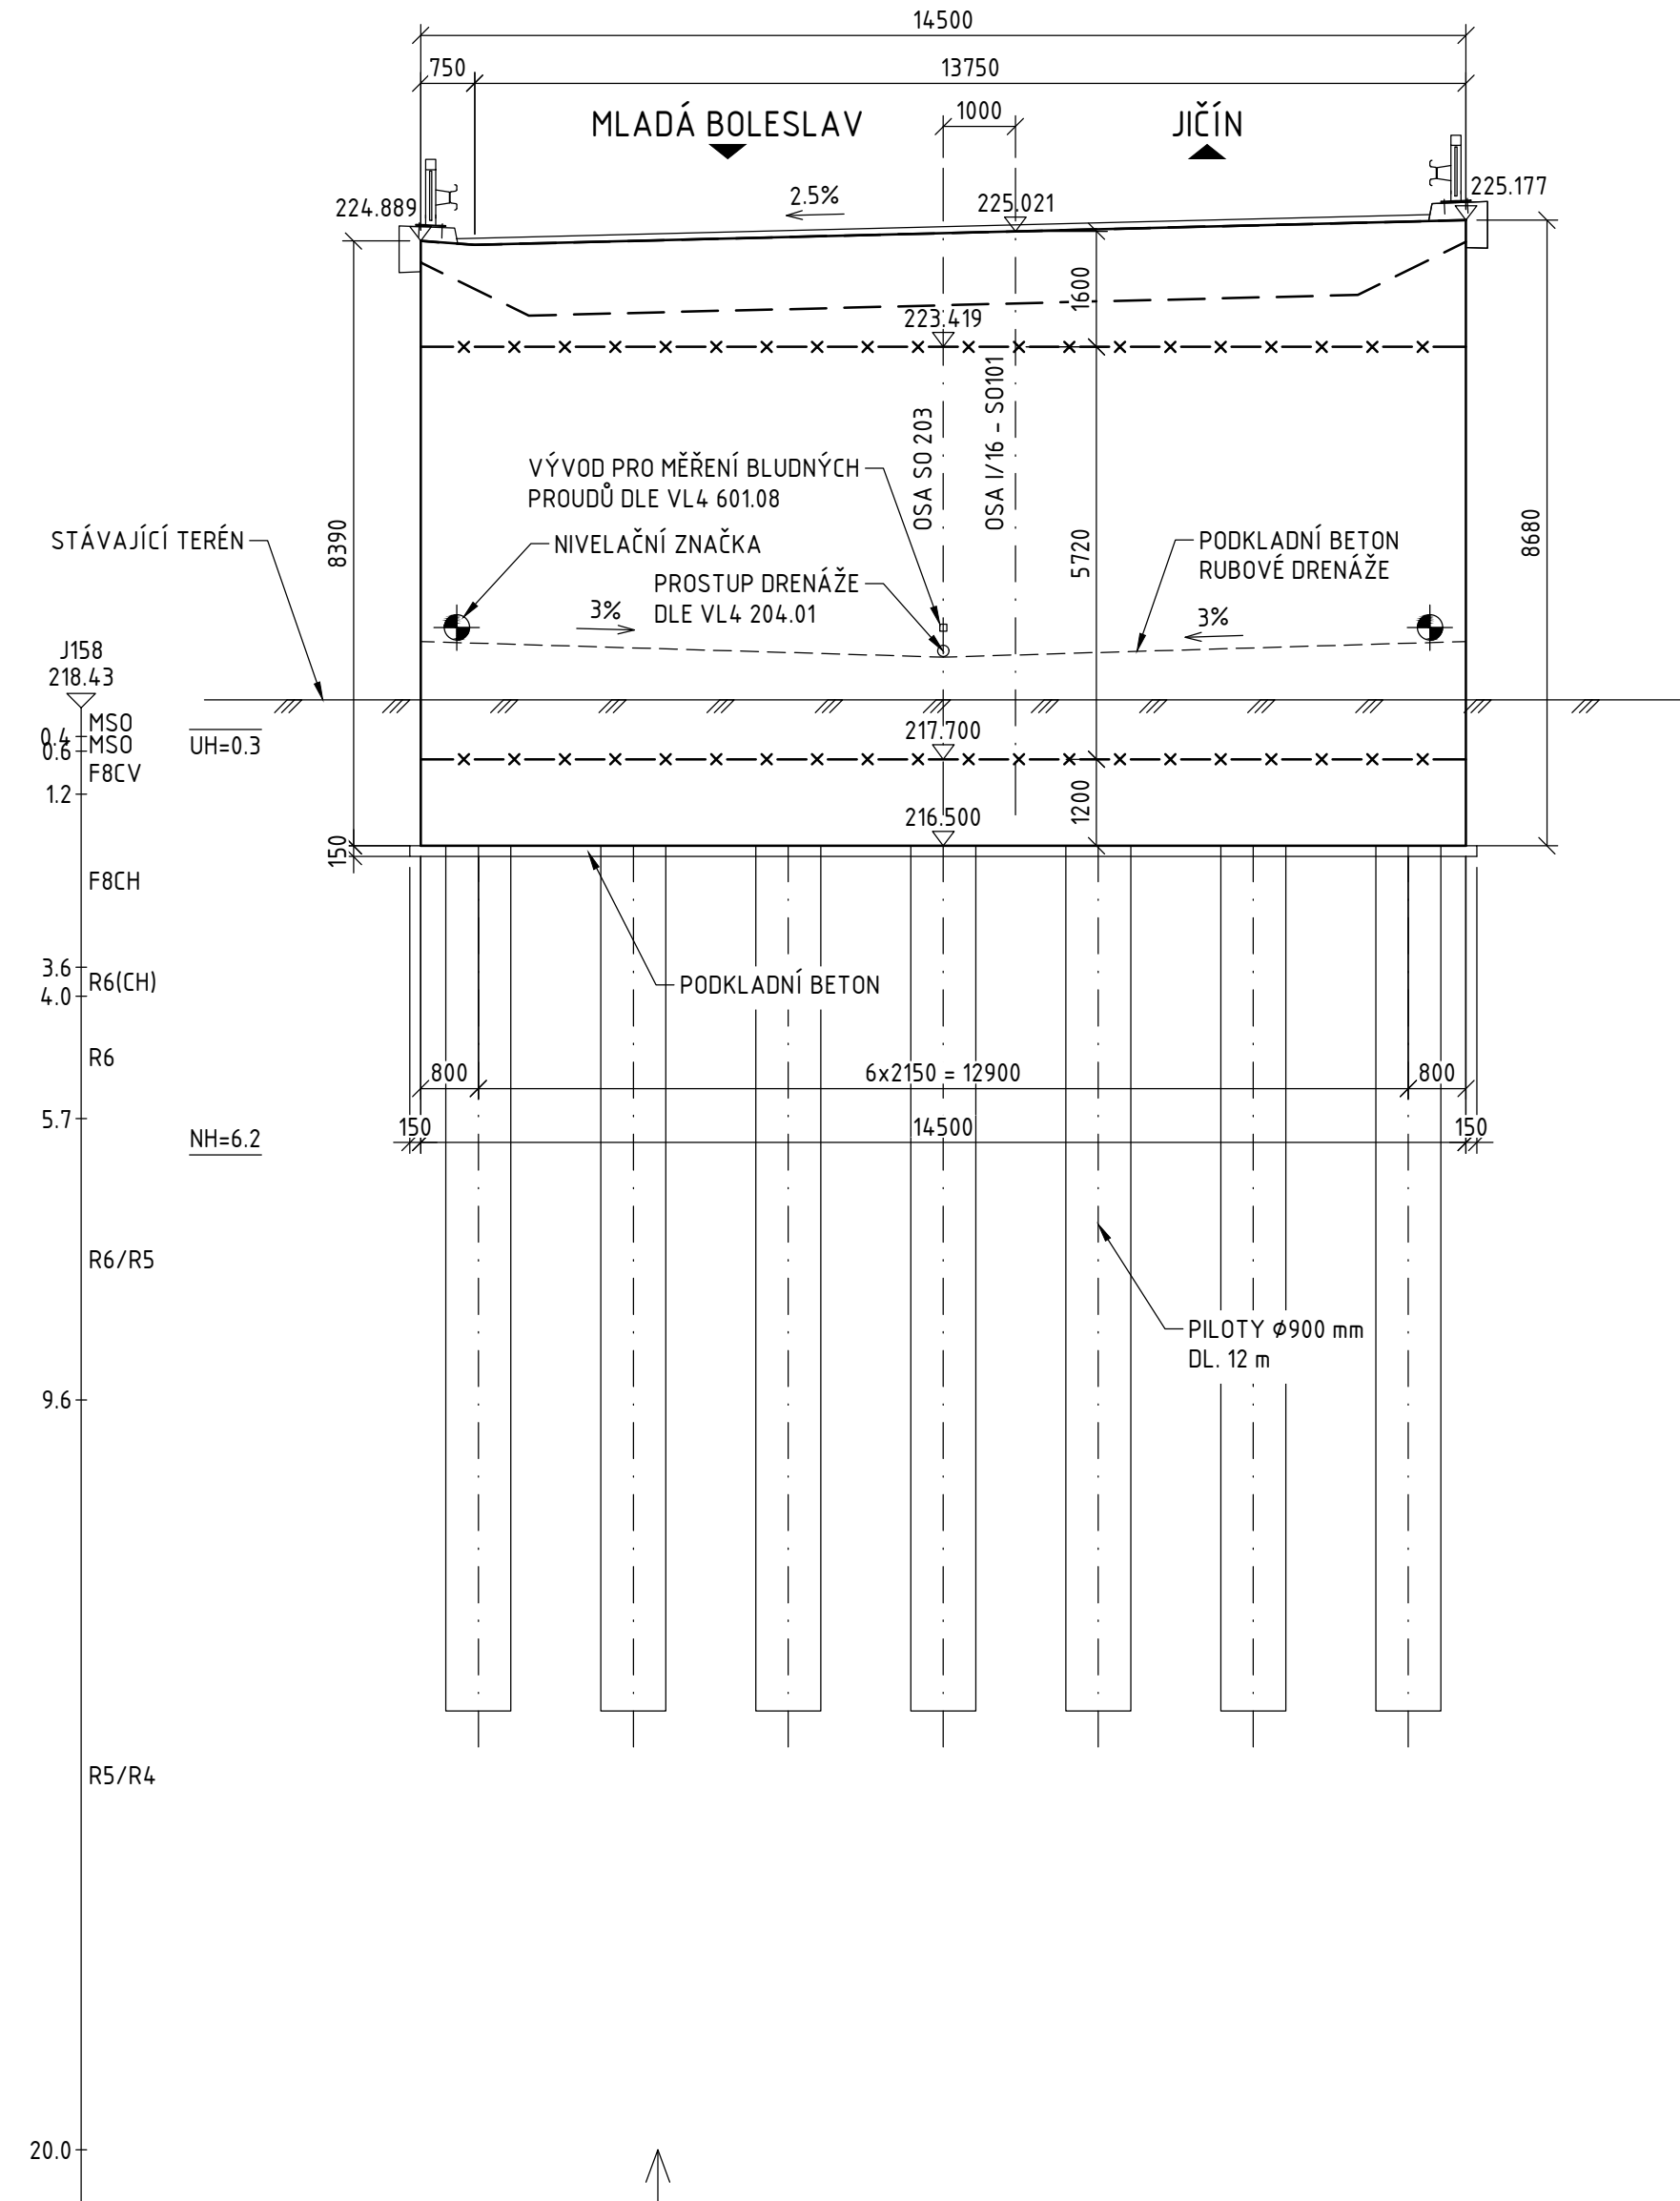

ŘEZ C-C 1:100

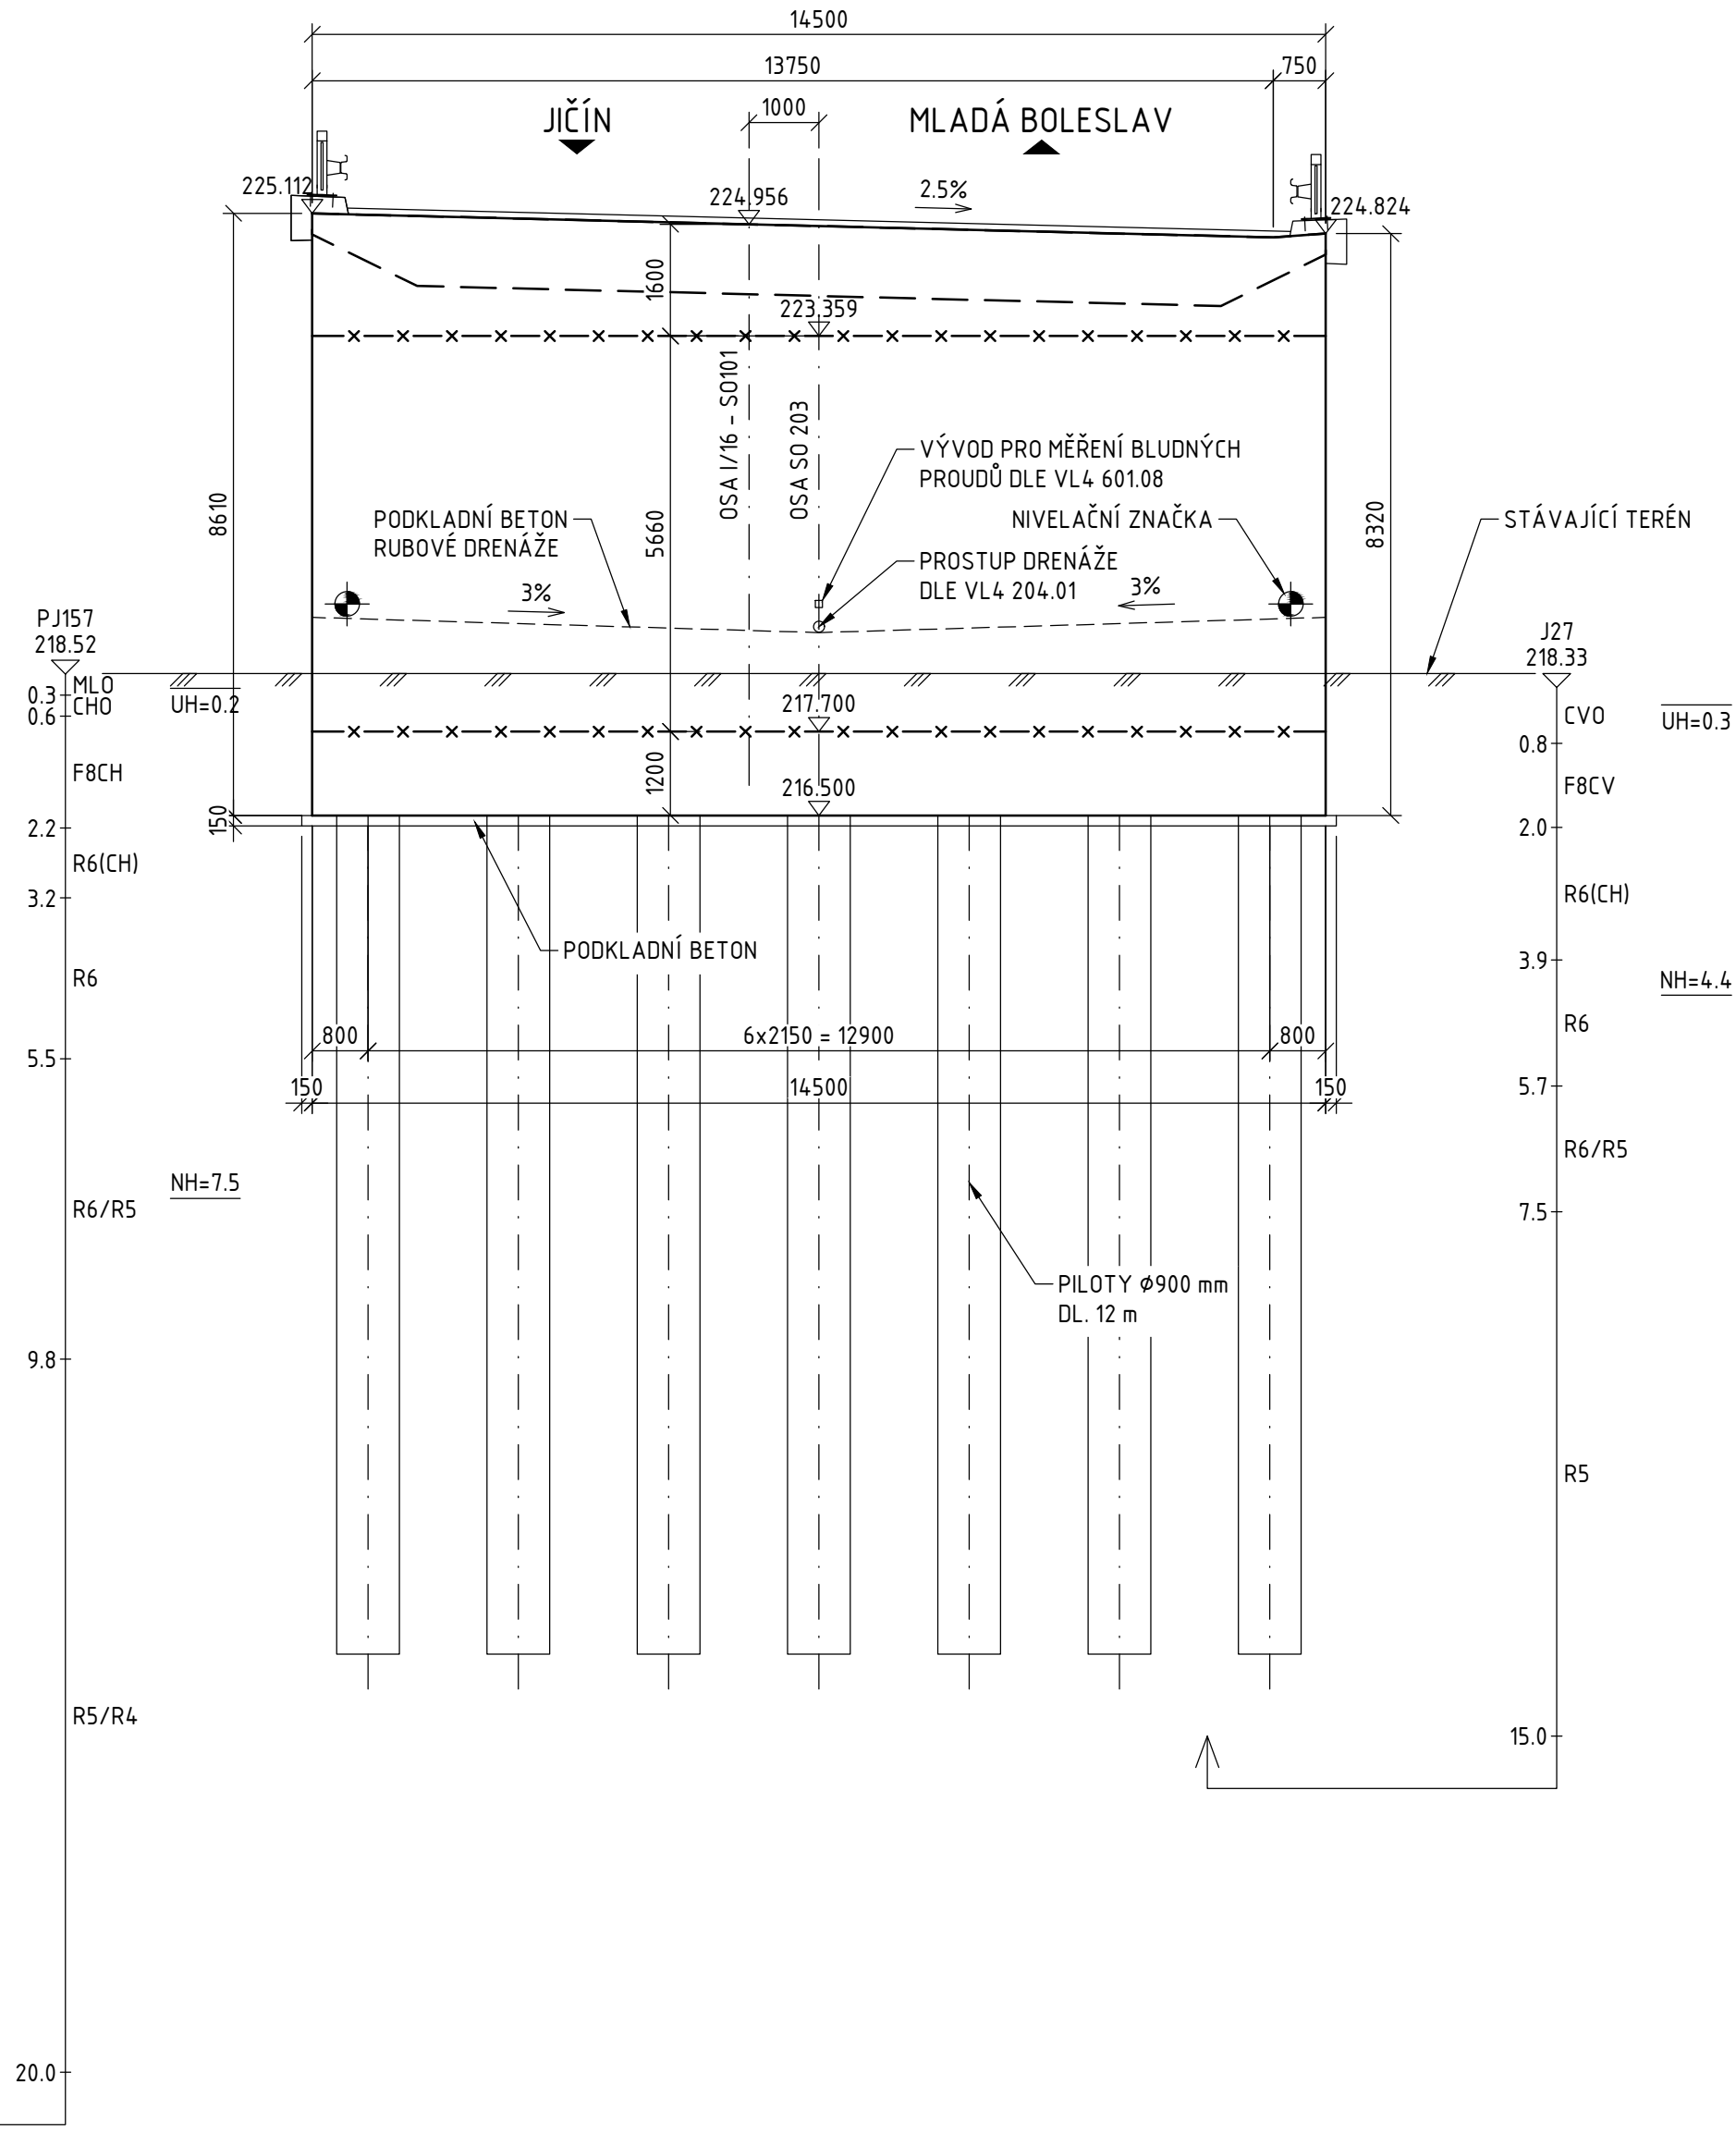


LEGENDA:

—x— PRACOVNÍ SPÁRA


POZNÁMKY:

- NEDÍLNOU SOUČÁSTÍ VÝKRESU JSOU POZNÁMKY A SPECIFIKACE UVEDENÉ NA VÝKRESE POZNÁMEK A TECHNICKÝCH SPECIFIKACÍ

VZOROVÝ PŘÍČNÝ ŘEZ 1:50

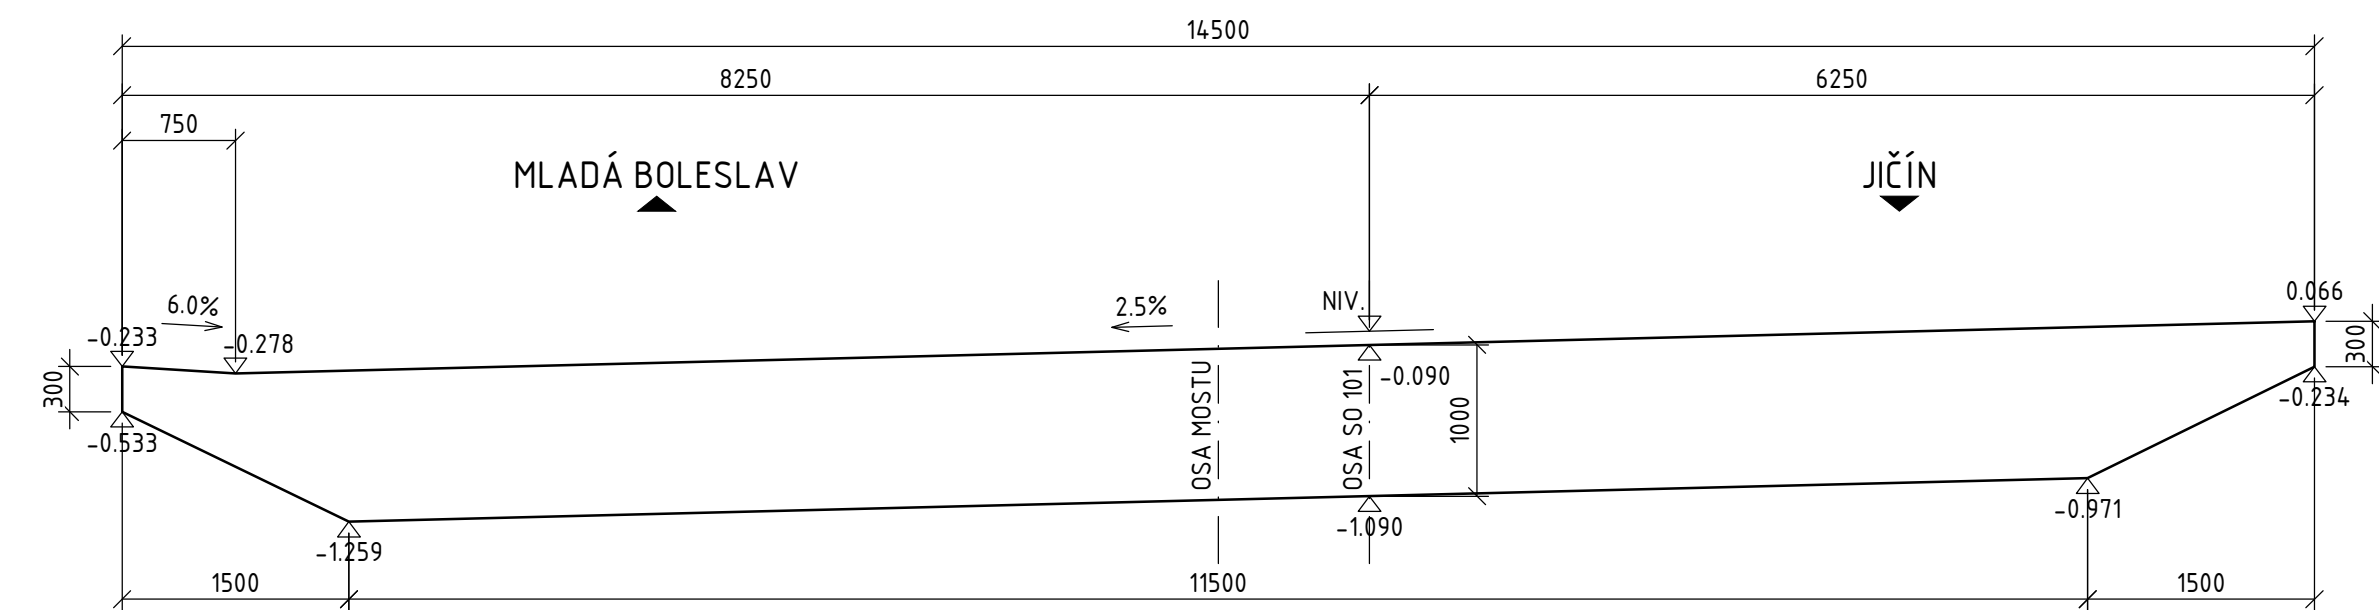


PŘÍČNÝ ŘEZ 1:50

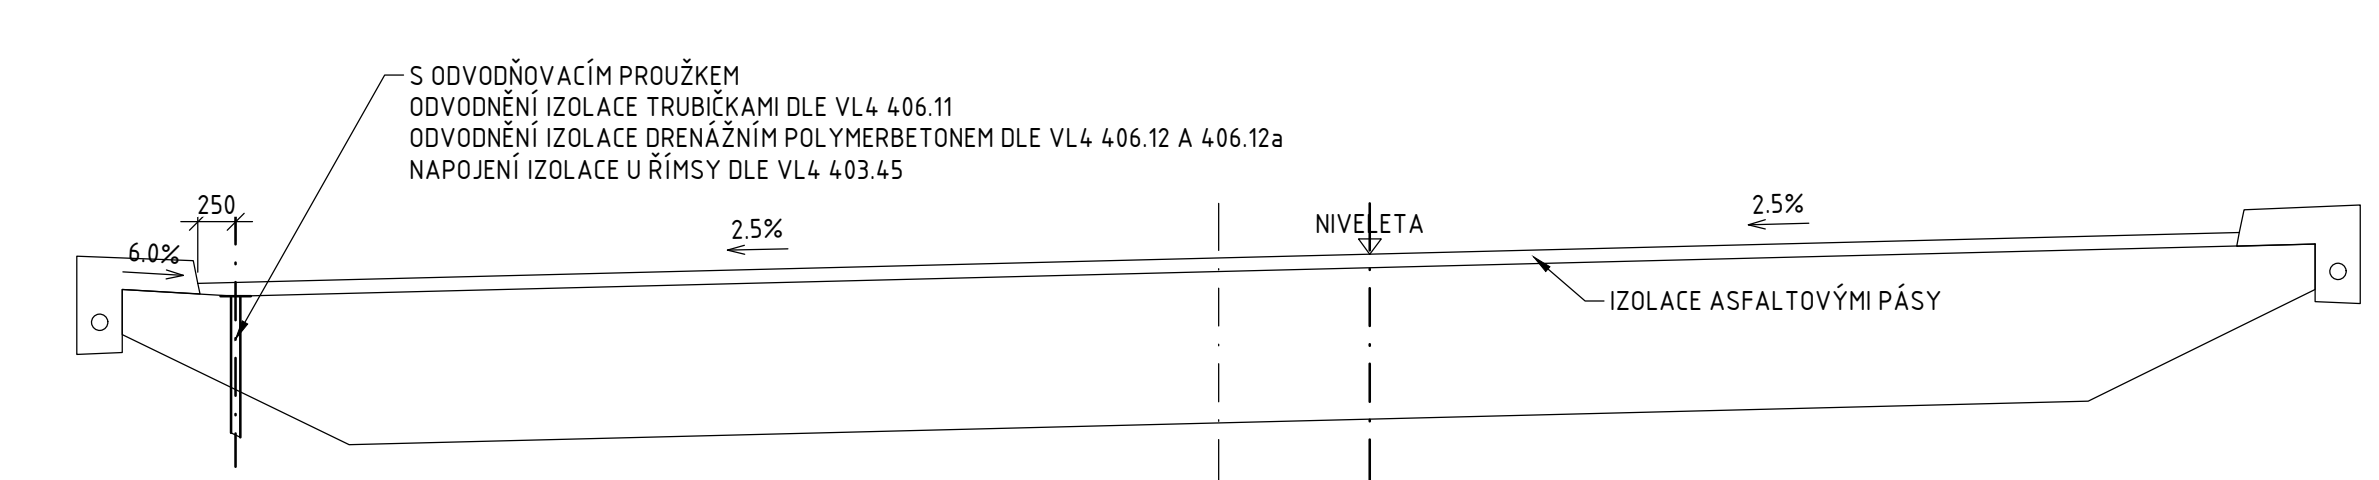



PODÉLNÝ ŘEZ PŘECHODOVOU DESKOU 1:50

VYKRESLENA PŘECHODOVÁ DESKA OPĚRY 2, PŘECHODOVÁ DESKA OPĚRY 1 ŘEŠENA ODOBNĚ

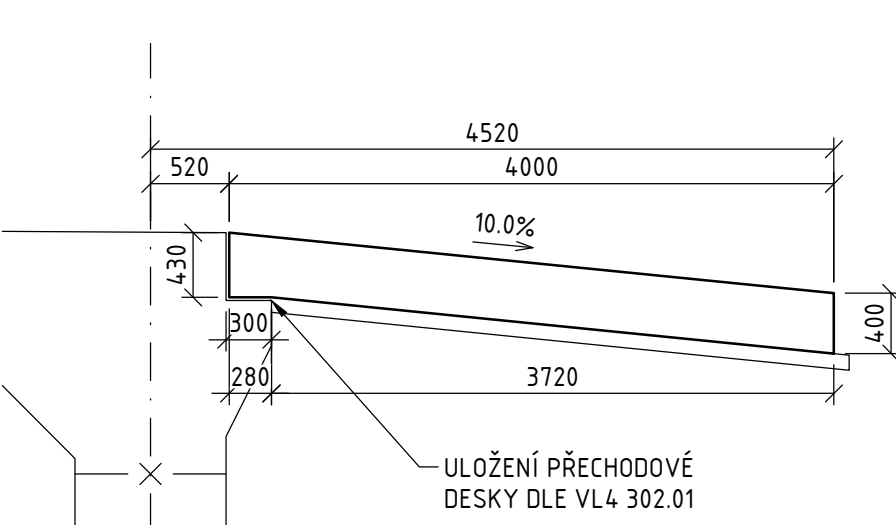

ŘEZ KŘÍDLEM 1, 2, 3, 4

1:50

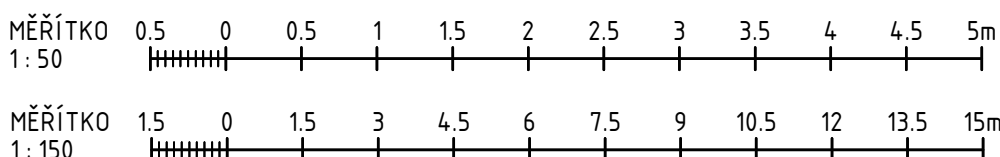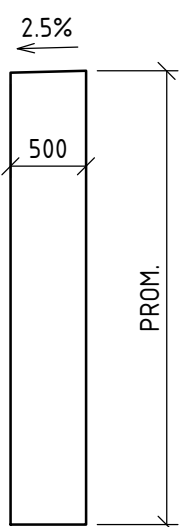

Souřadnicový systém: S-JTSK
Výškový systém: Bpv

SO 203 MOST NA I/16 PŘES PŘELOŽKU POLNÍ CESTY V KM 3,790

Objednatel:



Ředitelství silnic a dálnic s. p.
Čerčanská 2023/12, Krč, 140 00 Praha 4



Valbek, spol. s r.o.
Vaňurova 505/17
460 07 Liberec 3



Zhotovitel:

Valbek, spol. s r.o.
Vaňurova 505/17
460 07 Liberec 3

Příloha

TVAR NOSNÉ KONSTRUKCE
ČÁST 2

202

Počet formátů

8x A4

Měřítko

1:100,50

Č. přílohy

Paré

Zak. číslo

21-L113-001

Datum

02/2025

Stupeň

PDPS