




TVAR ŘÍMS
PŮDORYS 1:100

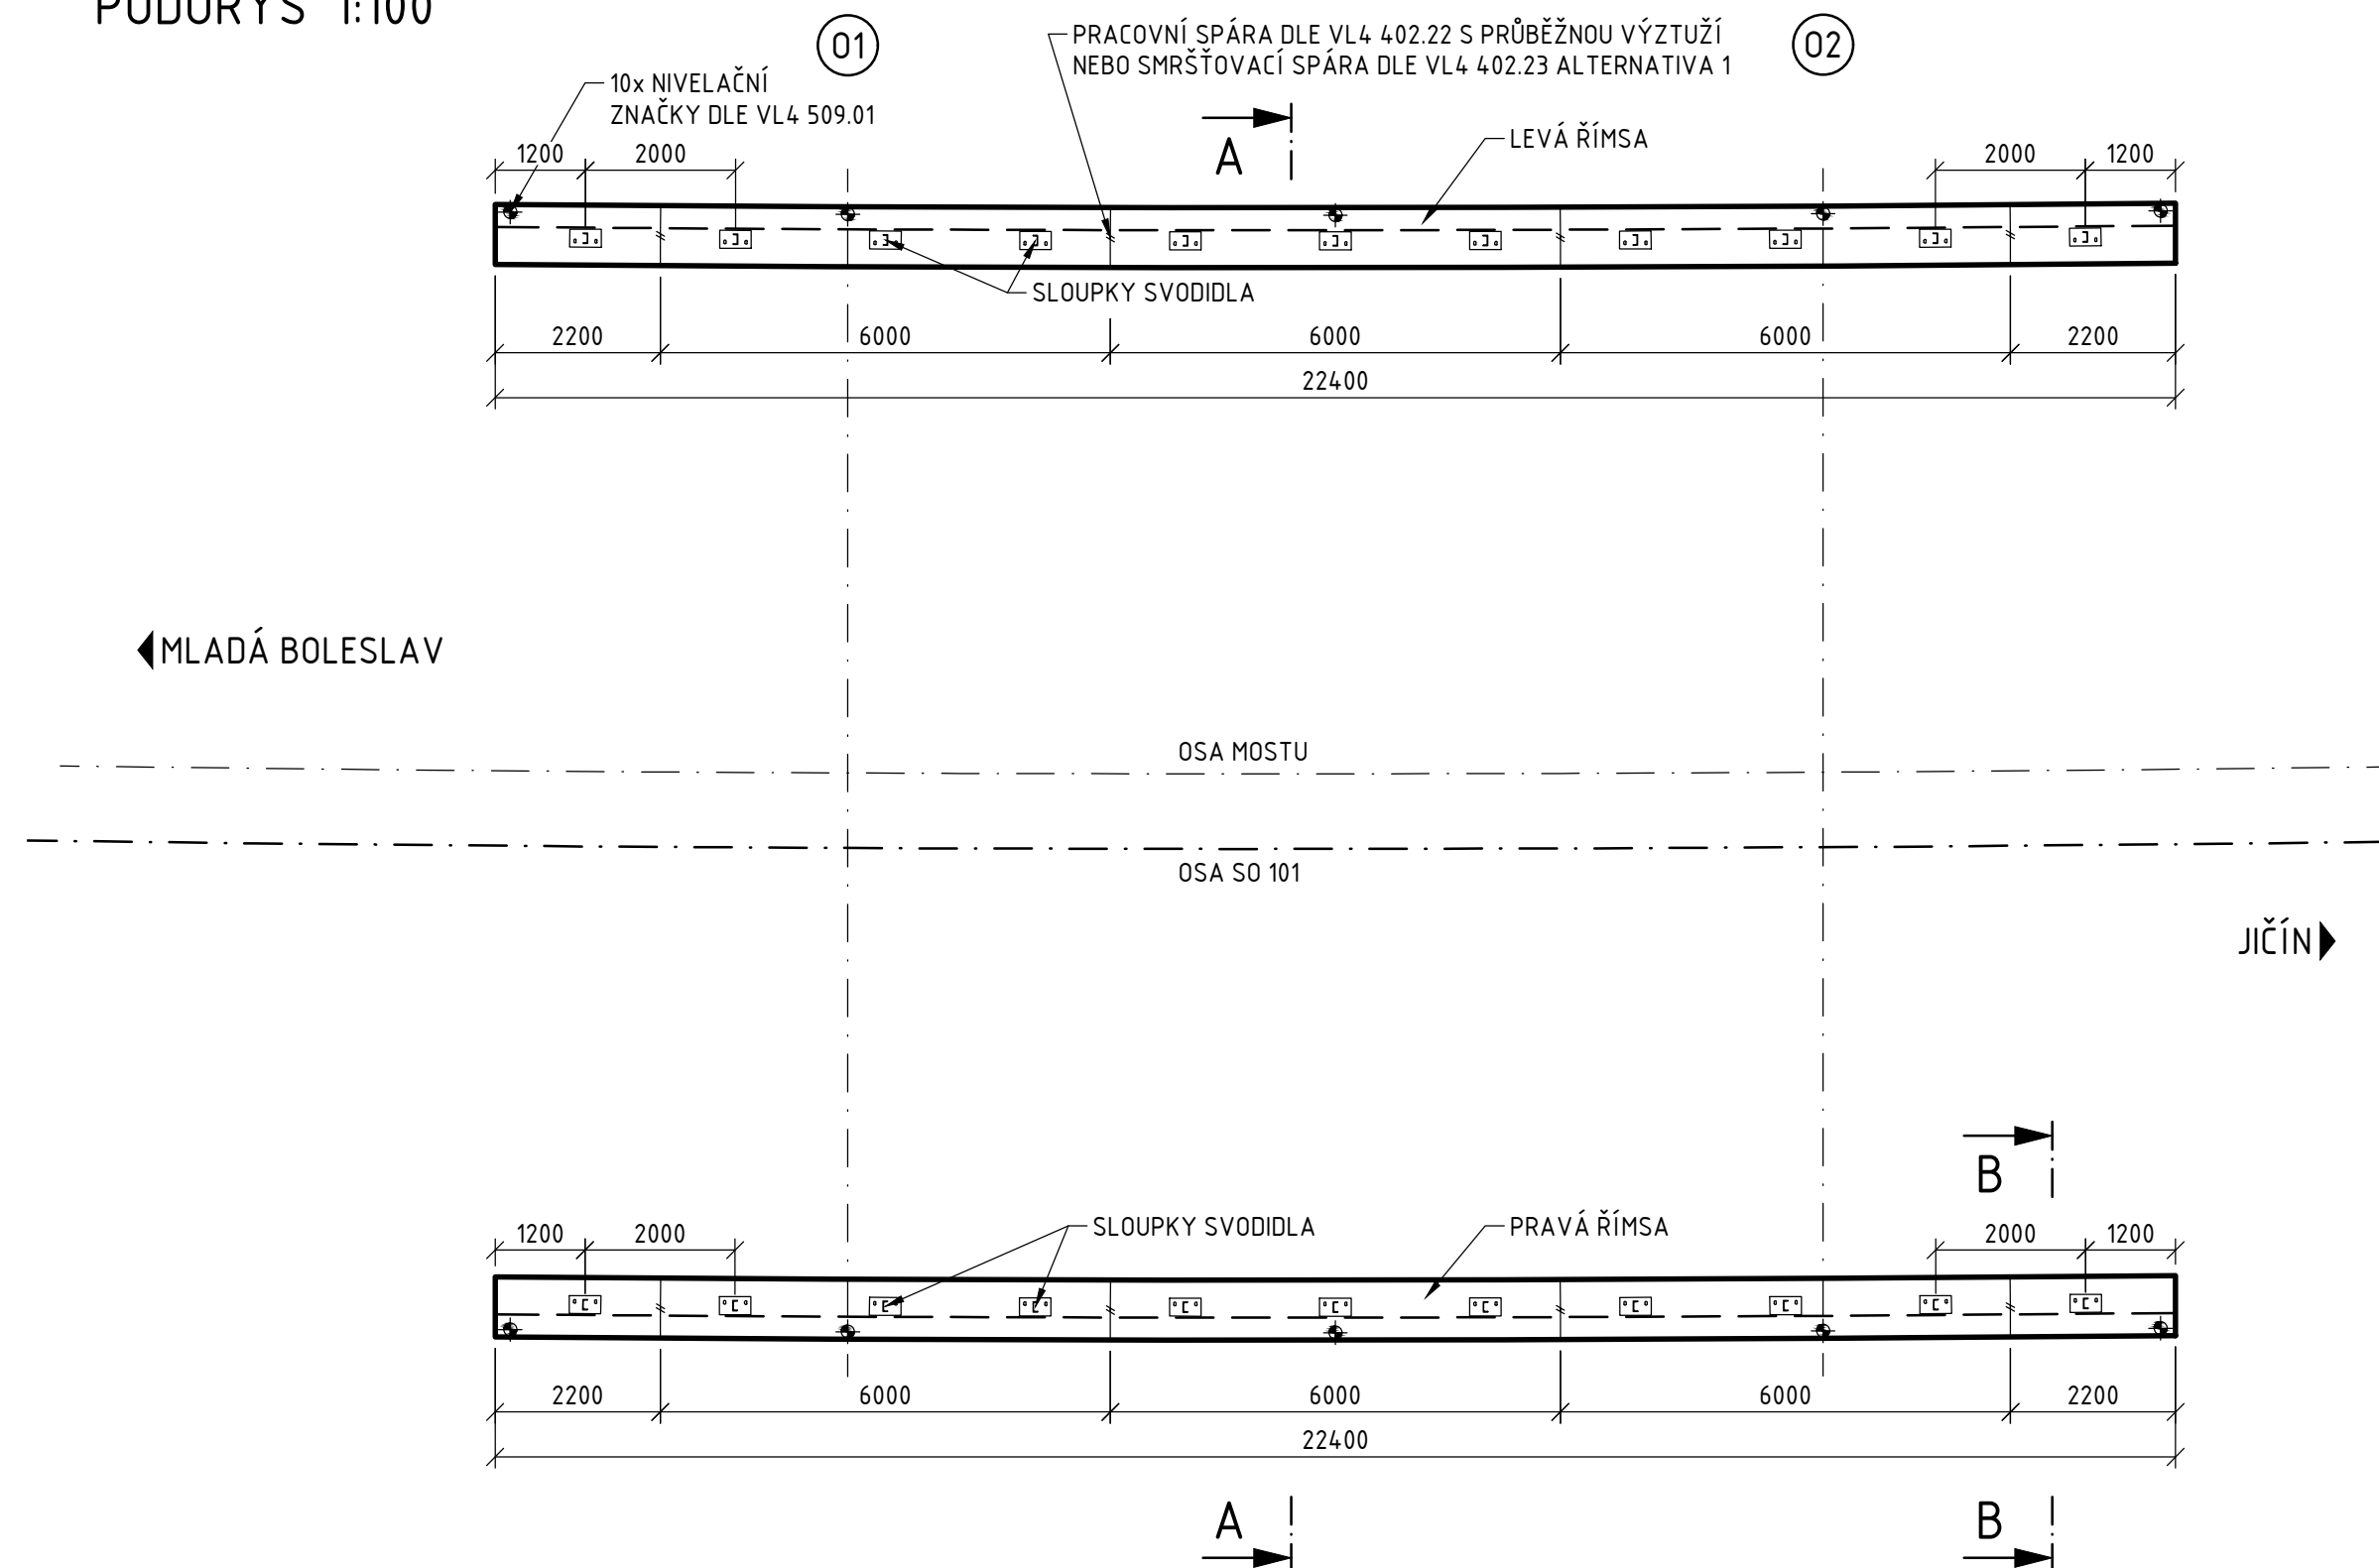


ŘEZ A-A 1:20

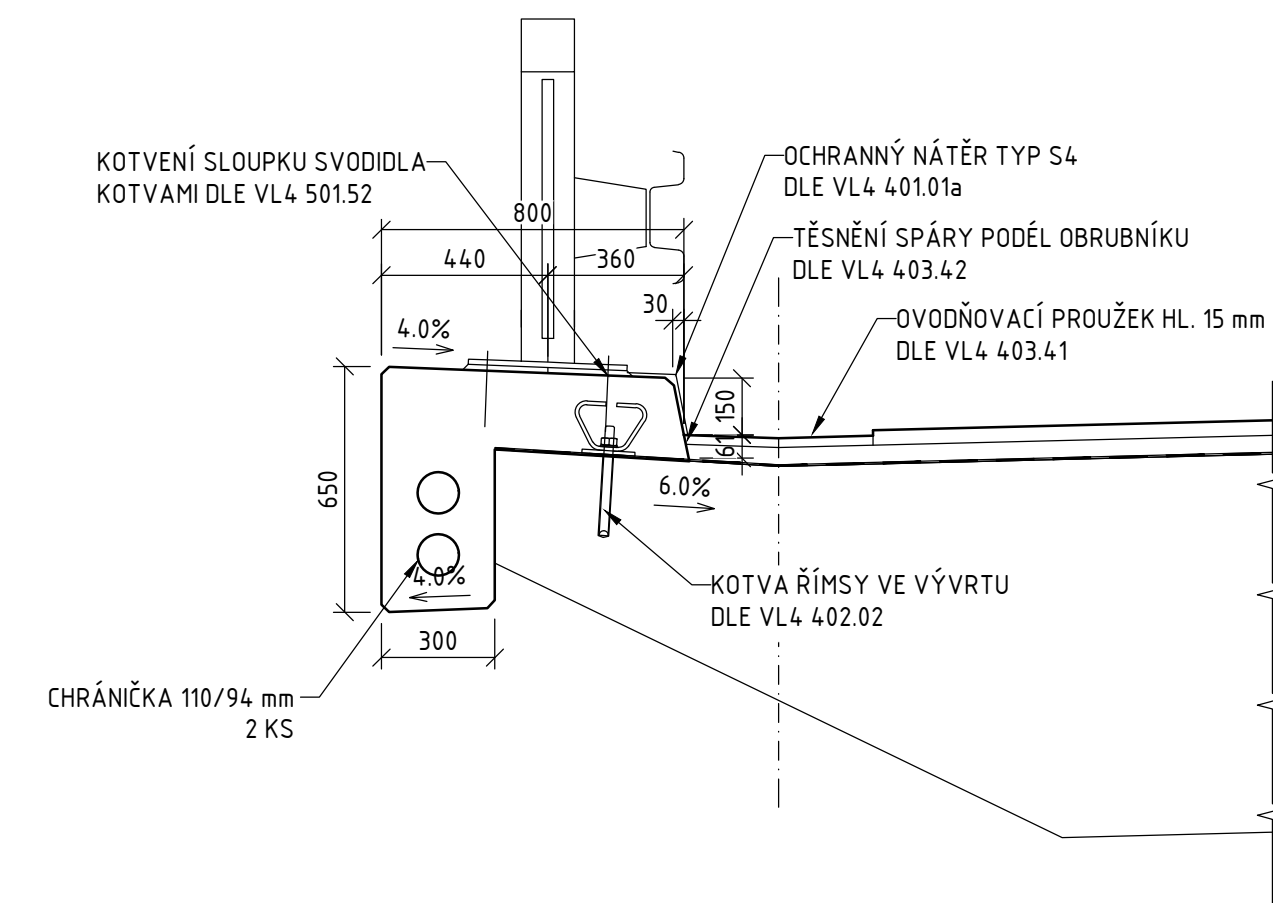

ŘEZ A-A 1:20

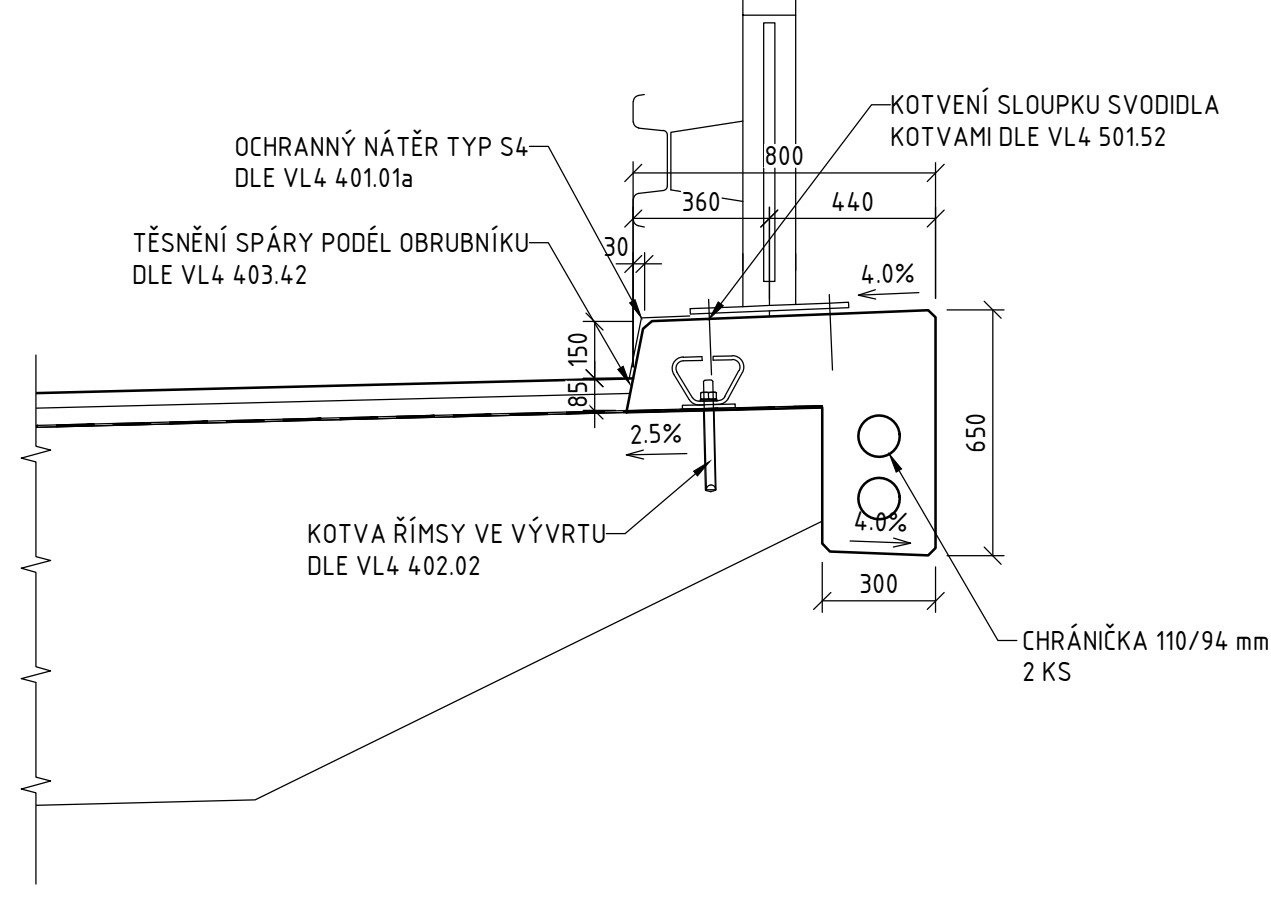


VYTYČOVACÍ VÝKRES, PŮDORYS 1:100

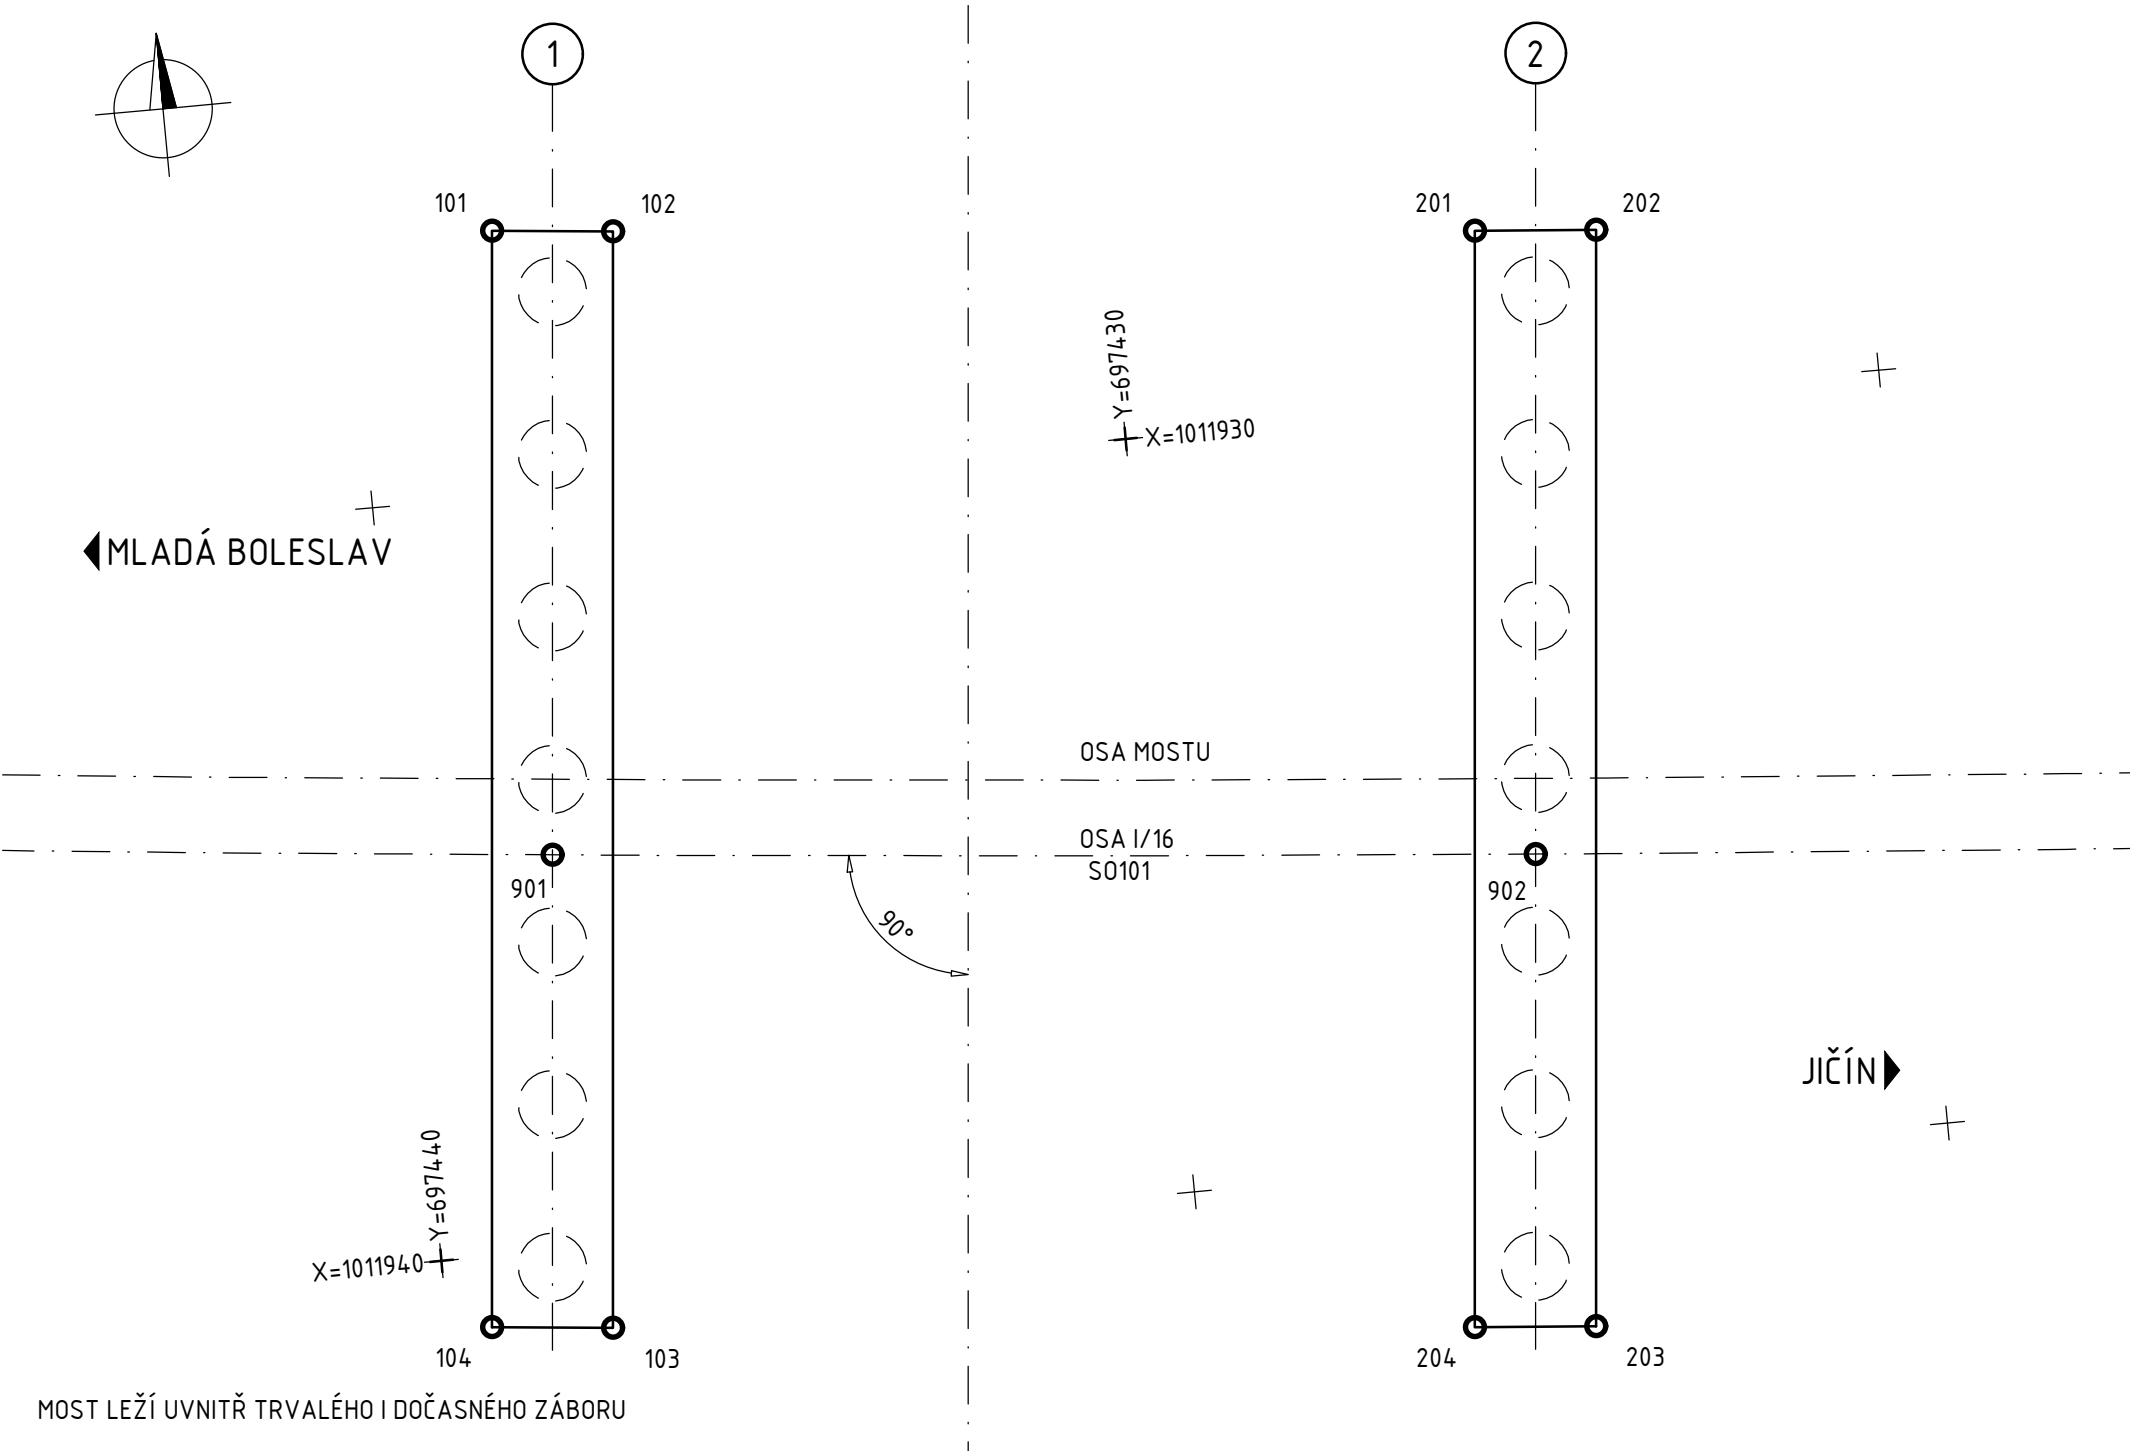

ŘEZ B-B 1:20

PRAVÁ ŘÍMSA (LEVÁ ŘÍMSA OBDOBNĚ)

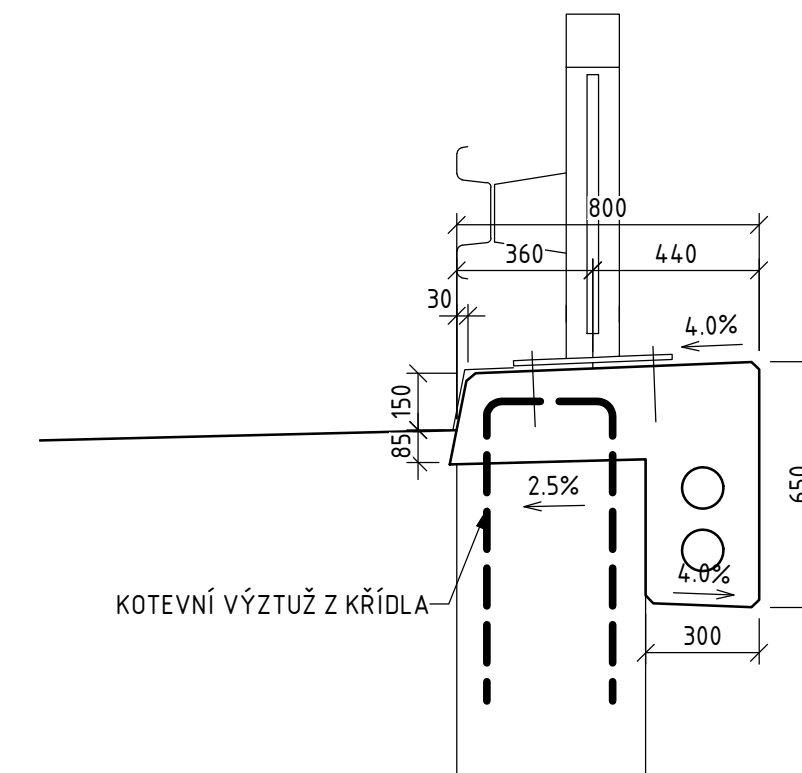


SOUŘADNICE VB

BOD	Y [m]	X [m]	Z [m]
101	697 438,095	1 011 926,497	216,500
102	697 436,503	1 011 926,650	216,500
103	697 437,823	1 011 941,089	216,500
104	697 439,416	1 011 940,937	216,500
201	697 425,149	1 011 927,678	216,500
202	697 423,555	1 011 927,814	216,500
203	697 424,875	1 011 942,254	216,500
204	697 426,469	1 011 942,118	216,500
901	697 438,050	1 011 934,789	-
902	697 425,103	1 011 935,962	-

POZNÁMKY:

- VYTYČOVACÍ ODCHYLKY: VIZ PŘÍLOHA E.4.5.1 - GVS - SEZNAM SOUŘADNIC
- NEDÍLNOU SOUČÁSTÍ VÝKRESU JSOU POZNÁMKY A SPECIFIKACE UVEDENÉ NA VÝKRESE
POZNÁMEK A TECHNICKÝCH SPECIFIKACÍ

PŘECHODOVÉ OBLASTI
PODÉLNÝ ŘEZ 1:100

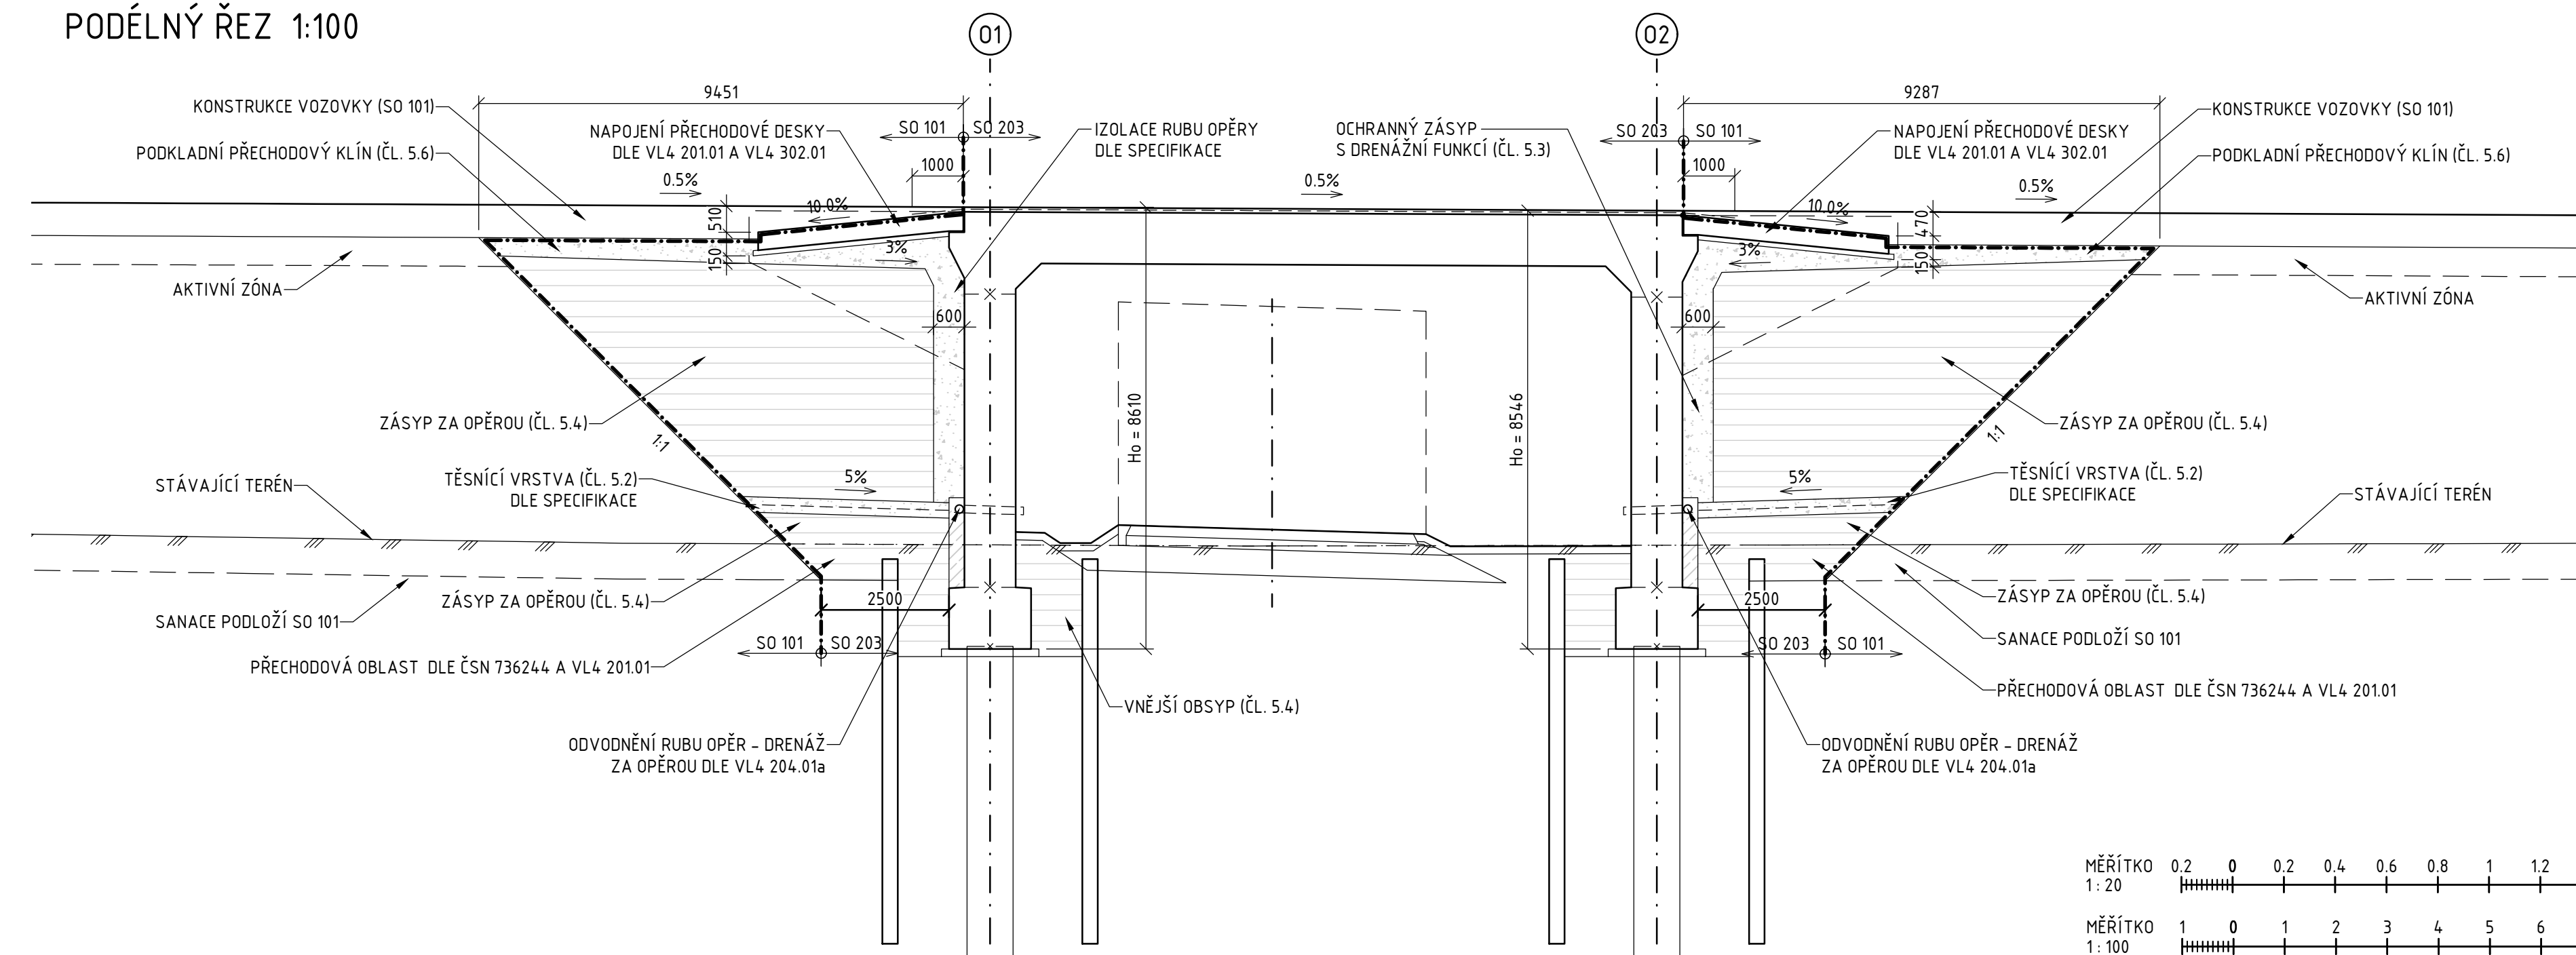

Souřadnicový systém: S-JTSK
Výškový systém: Bpv

SO 203 MOST NA I/16 PŘES PŘELOŽKU POLNÍ CESTY V KM 3,790

Objednatel:



Ředitelství silnic a dálnic s. p.
Čerčanská 2023/12, Krč, 140 00 Praha 4



Valbek, spol. s r.o.
Vaňurova 505/17
460 07 Liberec 3



Zhotovitel:
Valbek, spol. s r.o.
Vaňurova 505/17
460 07 Liberec 3

Příloha	TVAR ŘÍMS, SCHÉMA VYTYČENÍ PŘECHODOVÉ OBLASTI
---------	--

203

Měřitko
Č. přílohy