



PŮDORYS 1:150

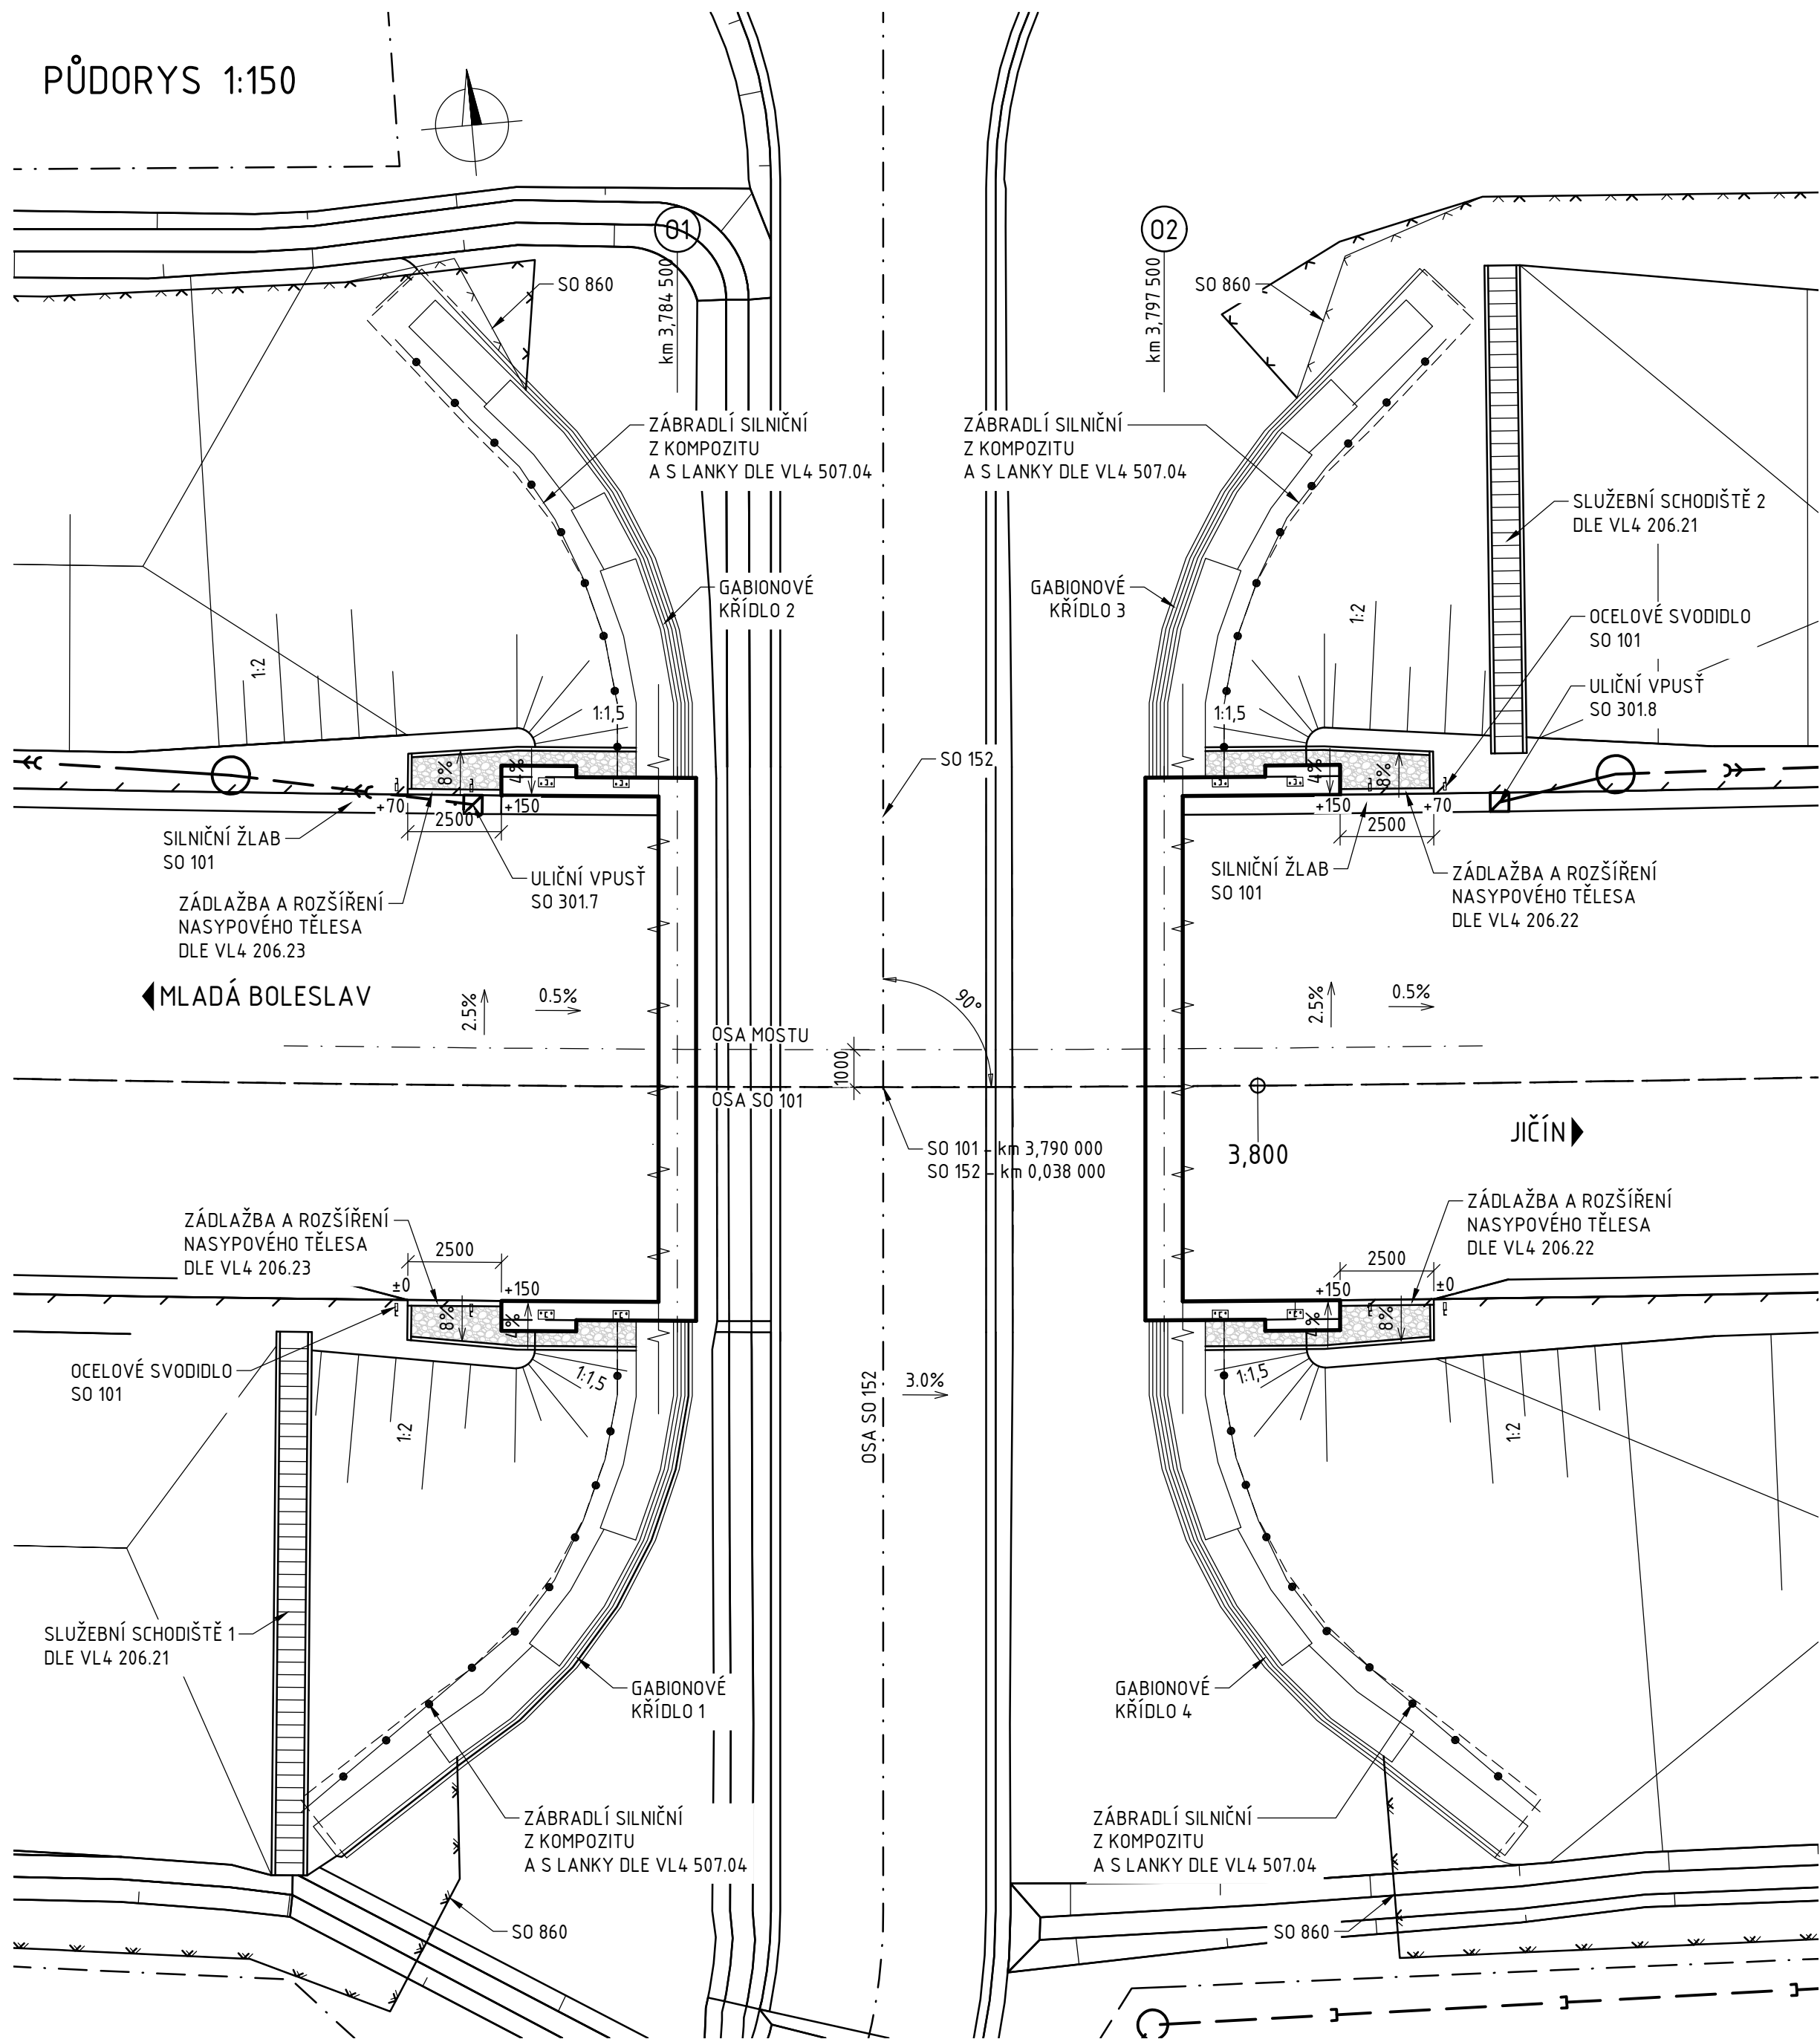



SCHODIŠTĚ 1  
PODÉLNÝ ŘEZ 1:50

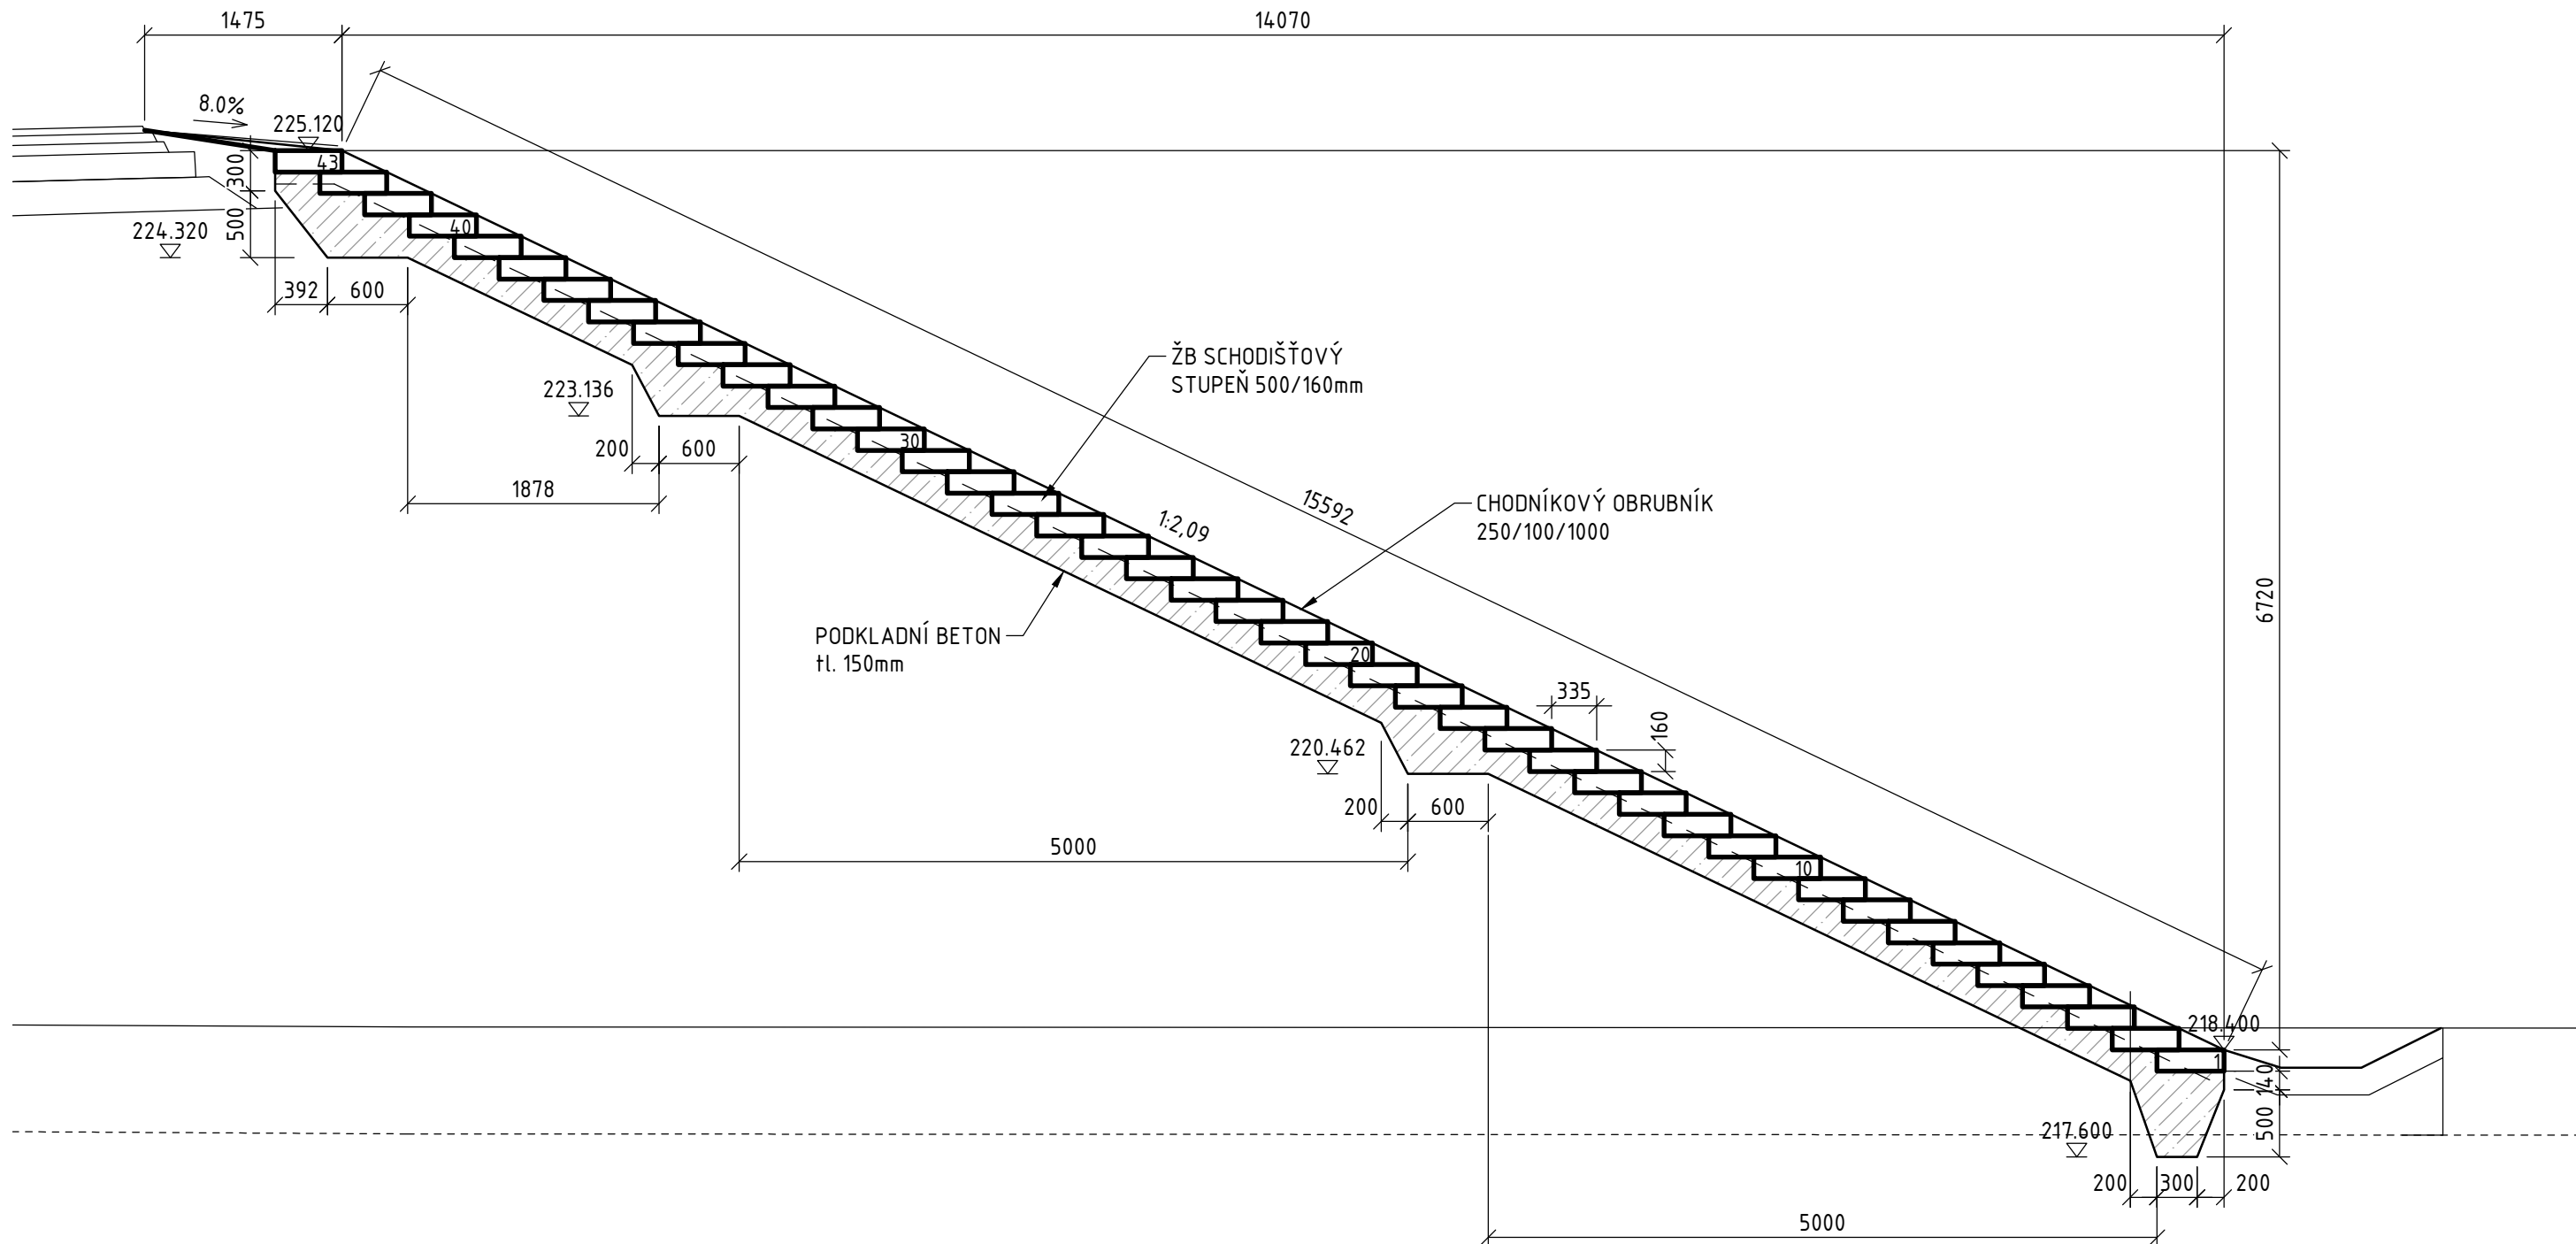

POZNÁMKY:

- NEDÍLNOU SOUČÁSTÍ VÝKRESU JSOU POZNÁMKY A SPECIFIKACE UVEDENÉ NA VÝKRESE  
POZNÁMEK A TECHNICKÝCH SPECIFIKACÍ

SCHODIŠTĚ 2  
PODÉLNÝ ŘEZ 1:50

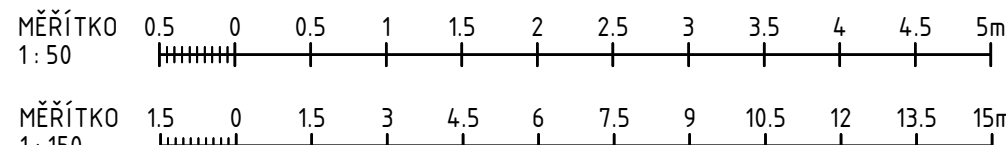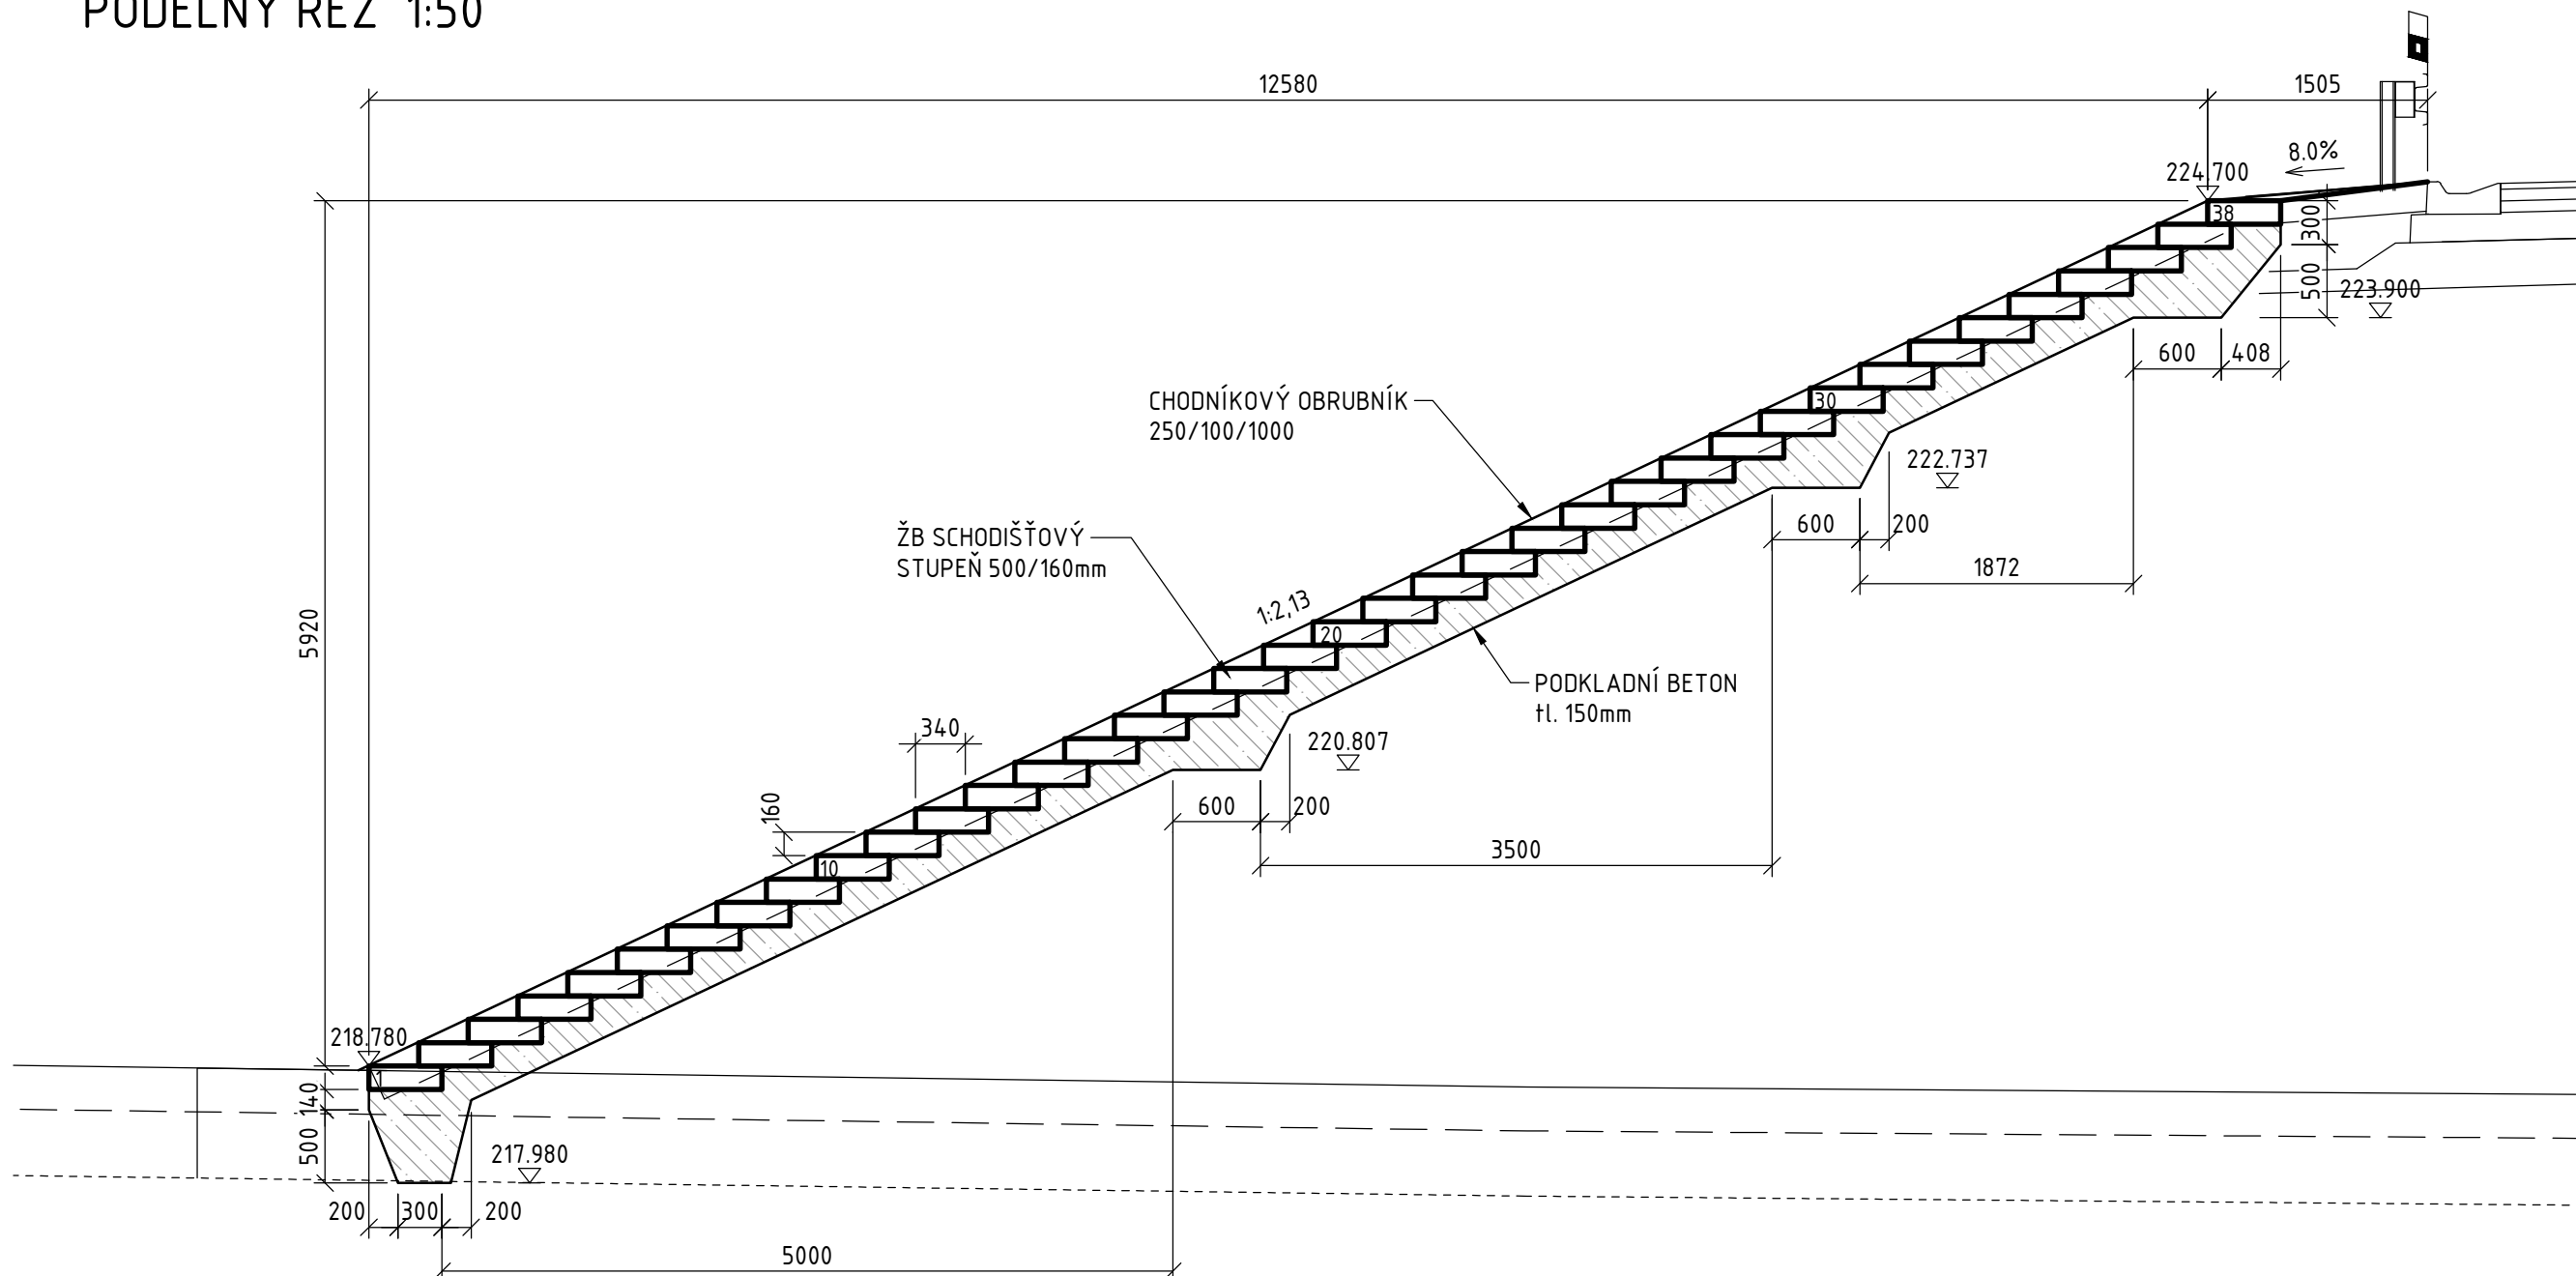

Souřadnicový systém: S-JTSK  
Výškový systém: Bpv

**SO 203** MOST NA I/16 PŘES PŘELOŽKU POLNÍ CESTY V KM 3,790

Objednatel:



**Ředitelství silnic a dálnic s. p.**  
Čerčanská 2023/12, Krč, 140 00 Praha 4



**Valbek, spol. s r.o.**  
Vaňurova 505/17  
460 07 Liberec 3



**I/16 MLADÁ BOLESLAV - MARTINOVICE**

Zhotovitel:  
Valbek, spol. s r.o.  
Vaňurova 505/17  
460 07 Liberec 3

Příloha  
ÚPRAVY POD MOSTEM, SLUŽEBNÍ SCHODIŠTĚ

|               |             |
|---------------|-------------|
| Zak. číslo    | 21-L113-001 |
| Datum         | 02/2025     |
| Stupeň        | PDPS        |
| Počet formátů | 8x A4       |
| Měřítko       | 1:150, 50   |
| Č. přílohy    | Paré        |
| 204           |             |