



ROZVINUTÉ POHLEDY - OPĚRA 01 1:100

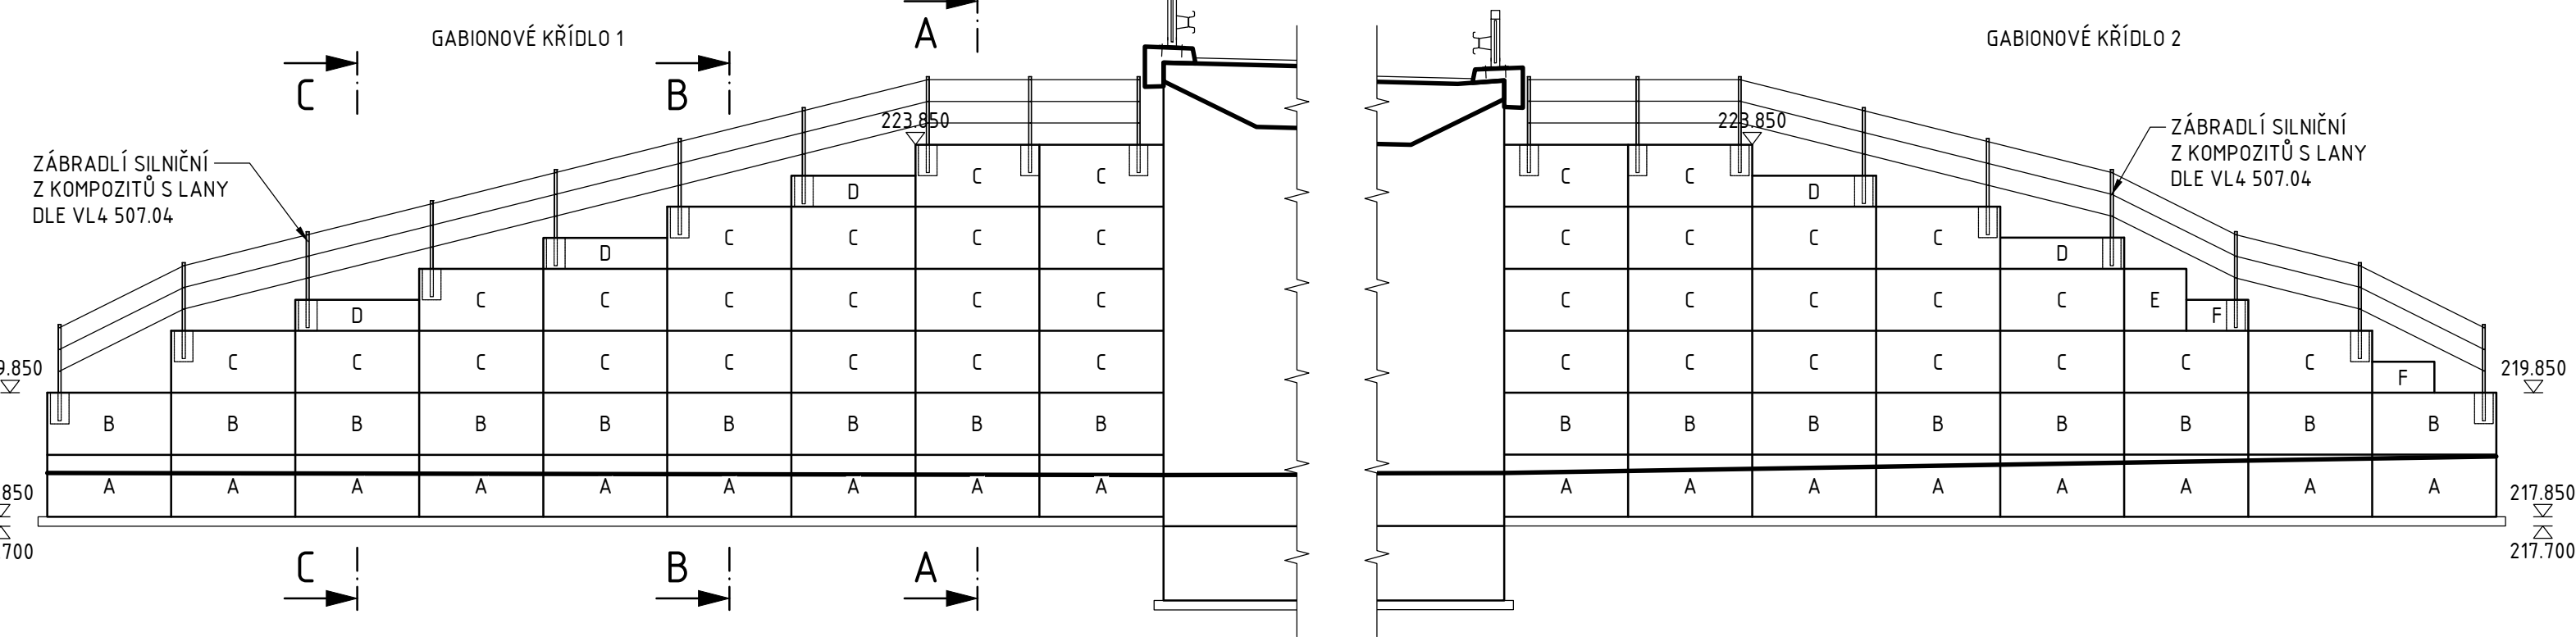


PŘÍČNÝ ŘEZ GABIONOVÝMI KŘÍDLY V LÍCI NK 1:100

VE SMĚRU STANIČENÍ

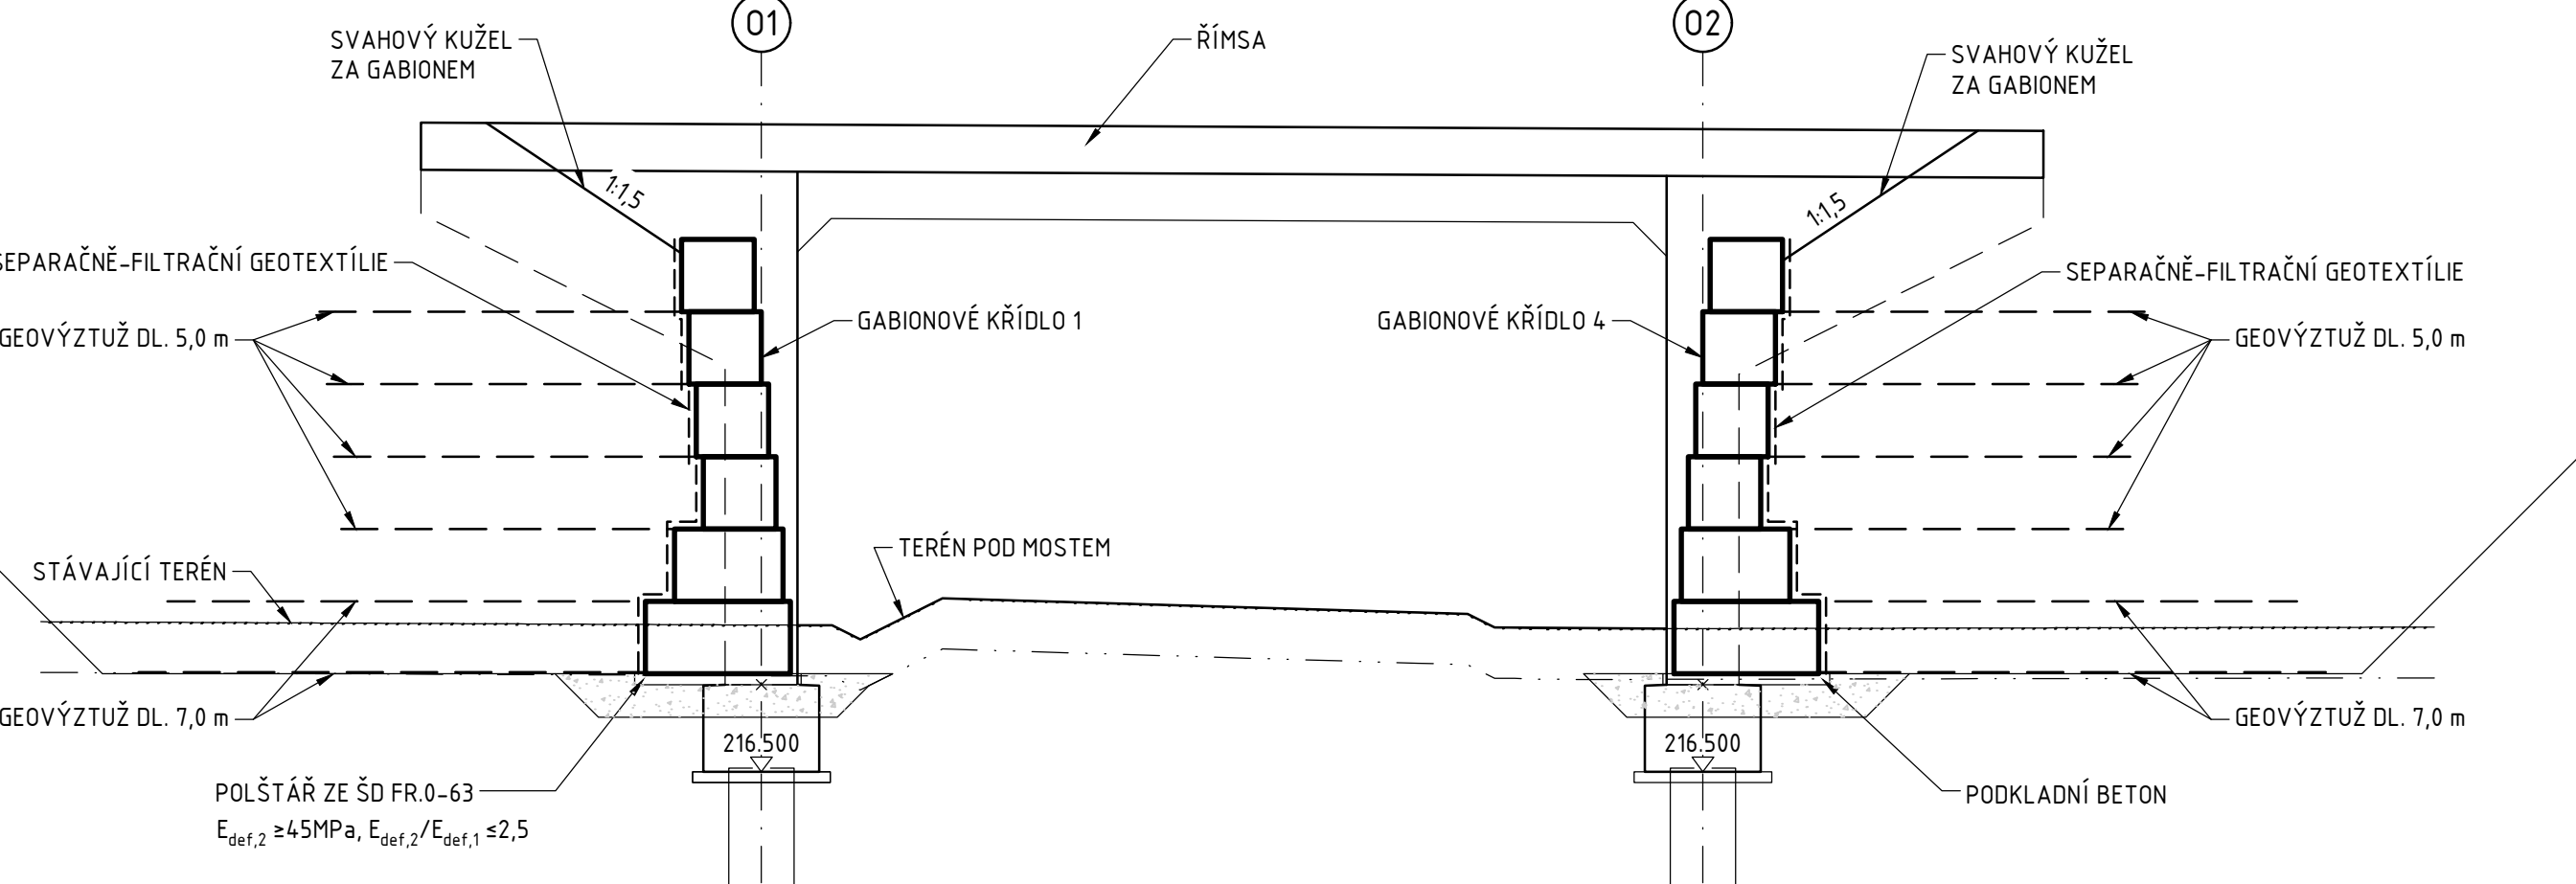

PŘÍČNÉ ŘEZY 1:100

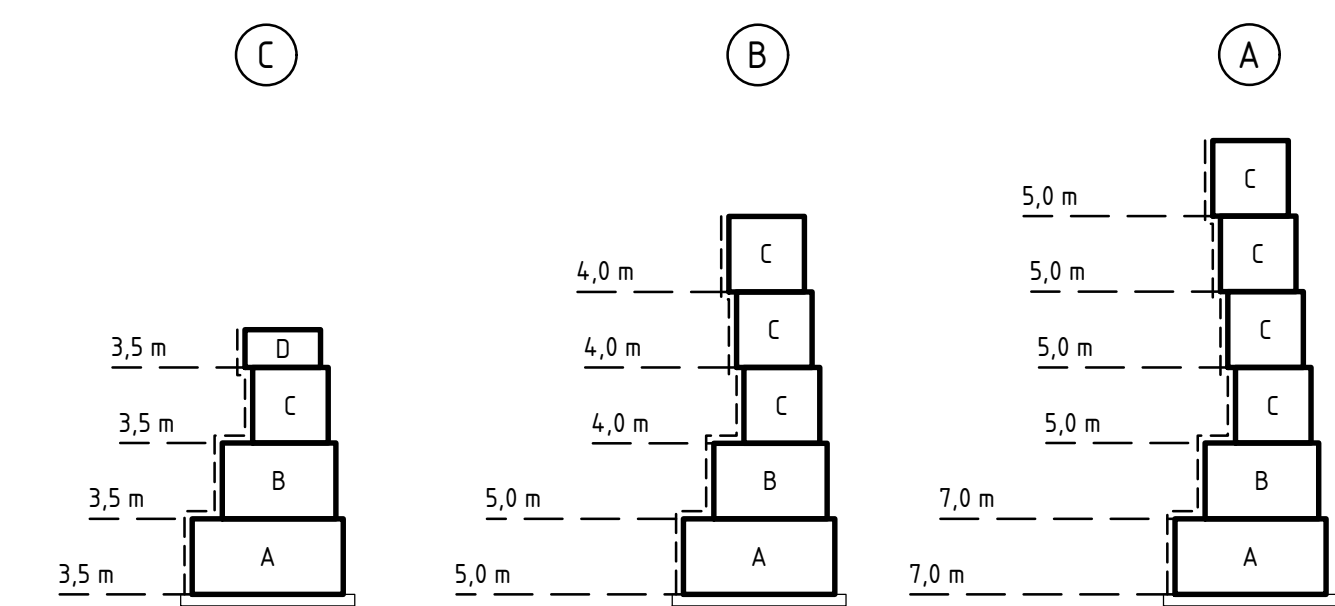


ROZMĚRY GABIONOVÝCH KOŠŮ:

- OZN. Š. DL. V.
- A - 2000 x 2000 x 1000
 - B - 1500 x 2000 x 1000
 - C - 1000 x 2000 x 1000
 - D - 1000 x 2000 x 500
 - E - 1000 x 1000 x 1000
 - F - 1000 x 1000 x 500

POZNÁMKY:


- NEDÍLNOU SOUČÁSTÍ VÝKRESU JSOU POZNÁMKY A SPECIFIKACE UVEDENÉ NA VÝKRESE POZNÁMEK A TECHNICKÝCH SPECIFIKACÍ

ROZVINUTÉ POHLEDY - OPĚRA 02 1:100

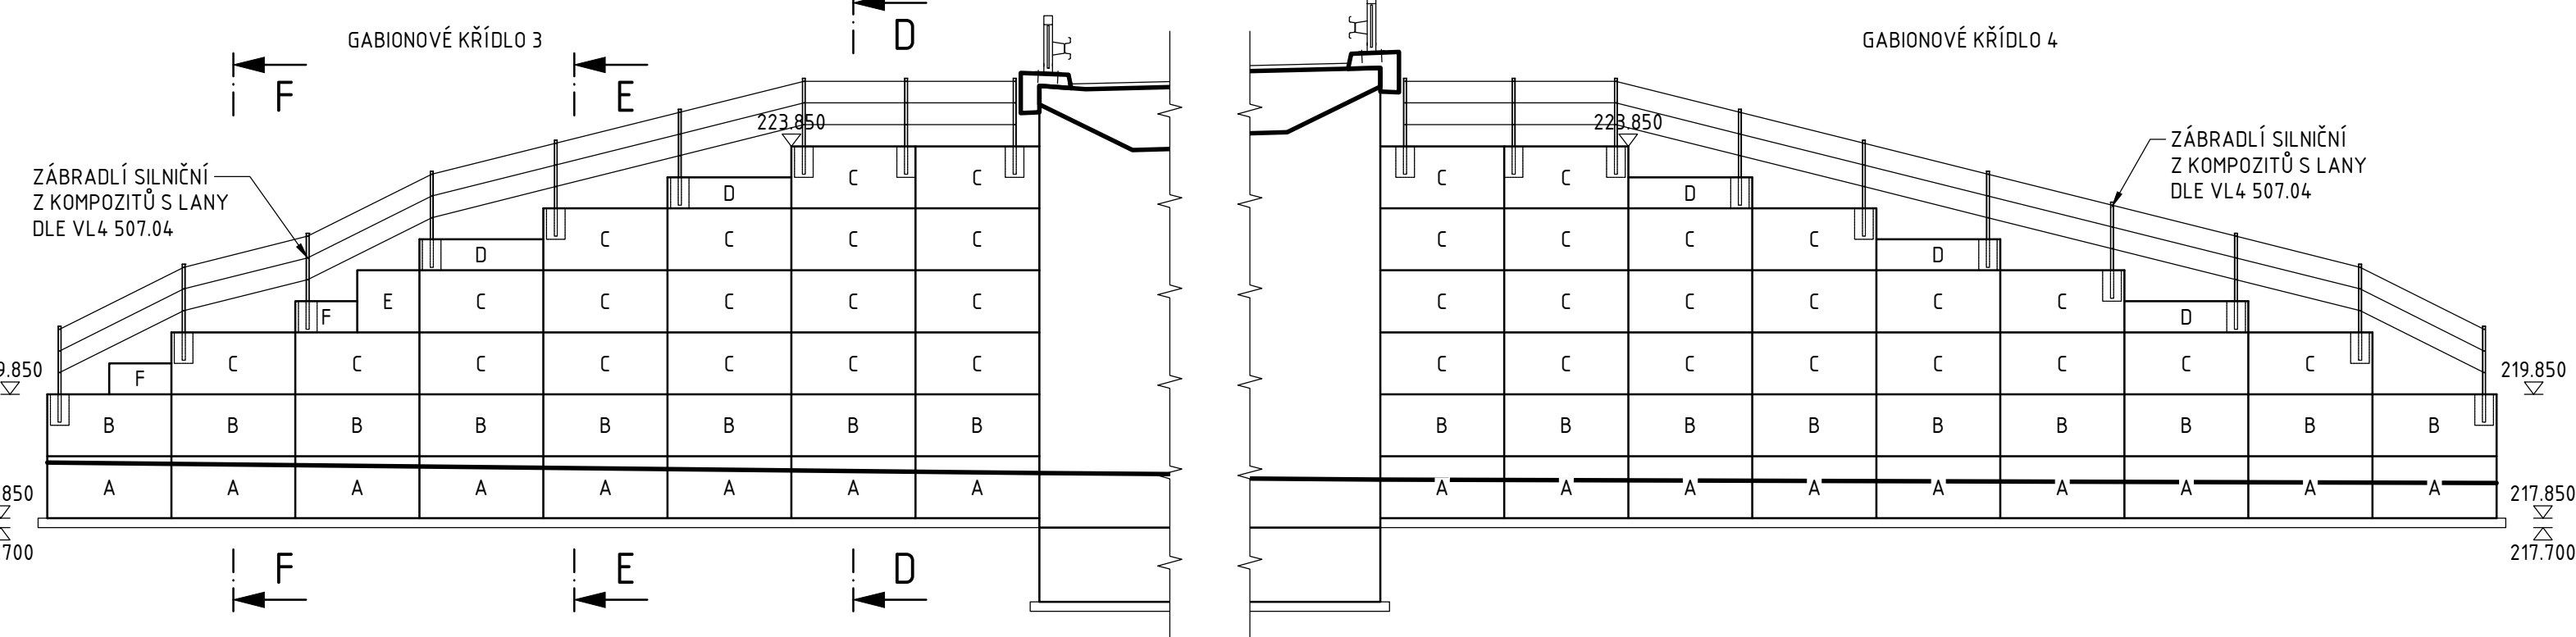


PŘÍČNÝ ŘEZ GABIONOVÝMI KŘÍDLY V LÍCI NK 1:100

PROTI SMĚRU STANIČENÍ

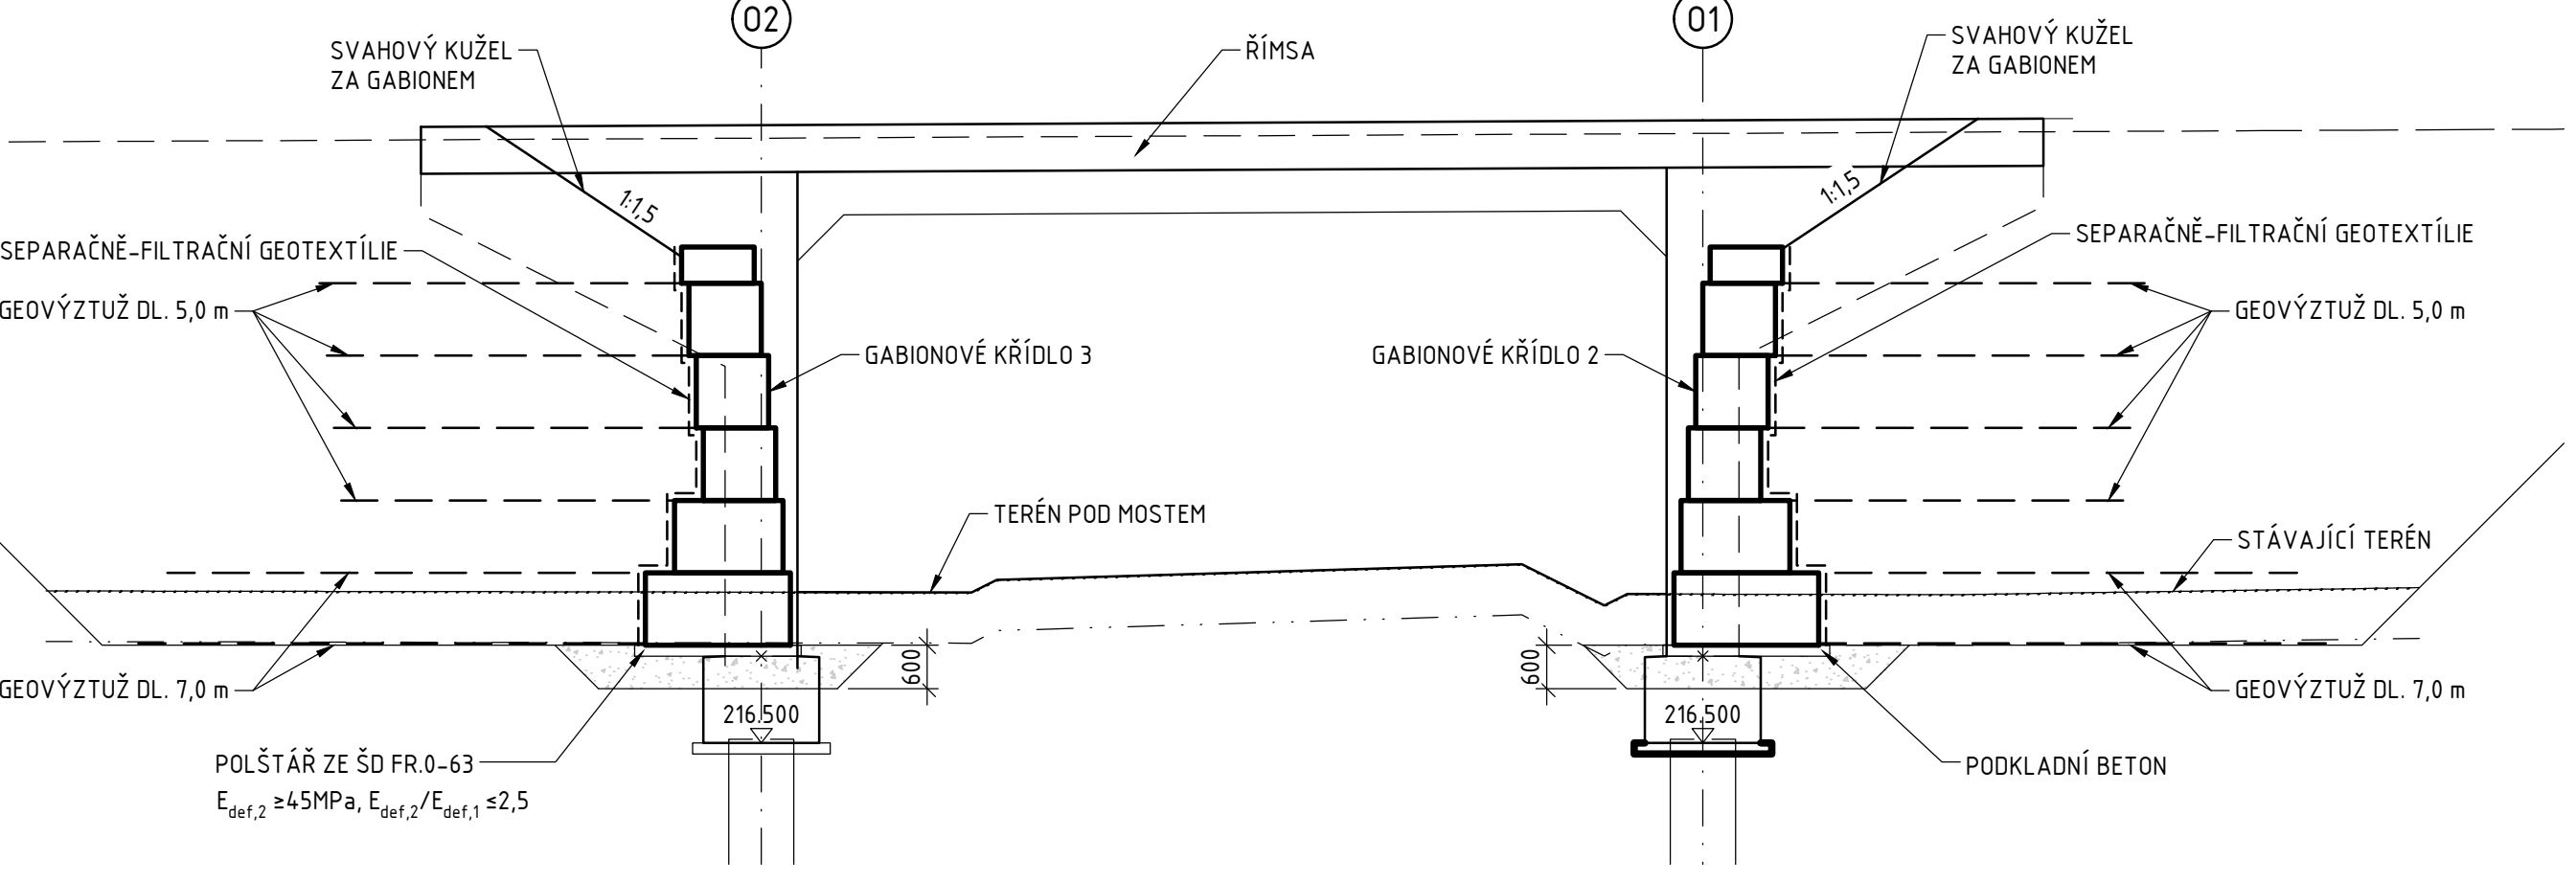

PŘÍČNÉ ŘEZY 1:100

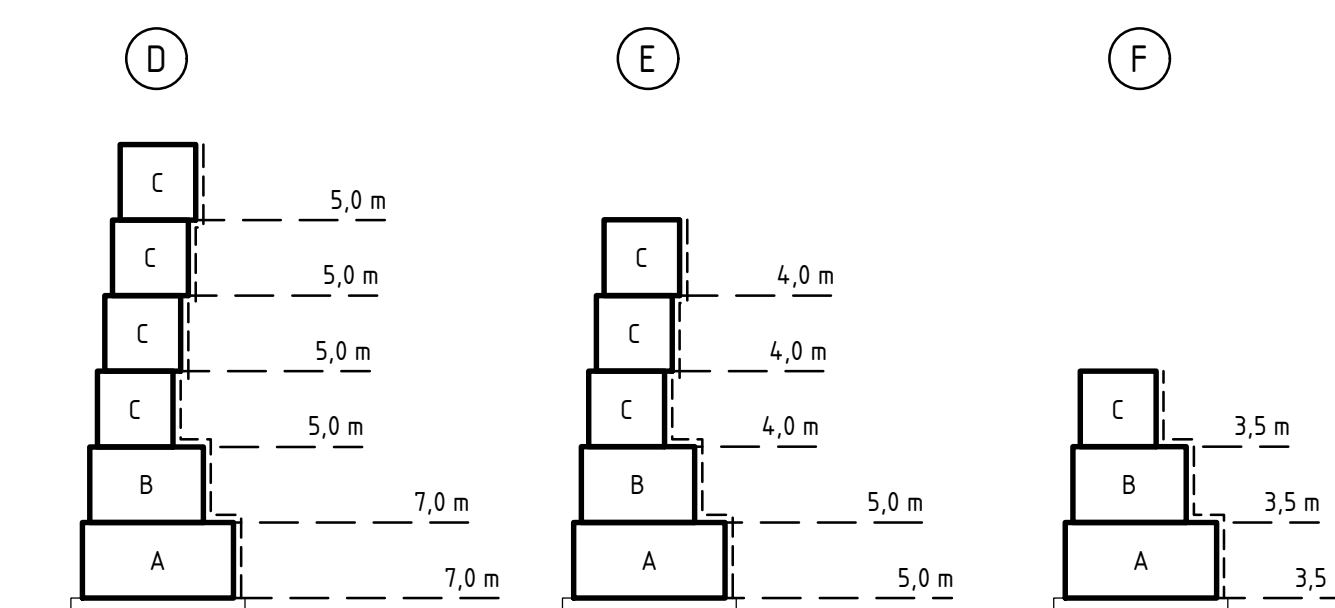

Souřadnicový systém: S-JTSK
Výškový systém: BpV

SO 203 MOST NA I/16 PŘES PŘELOŽKU POLNÍ CESTY V KM 3,790

Objednatel:
ŘEDITELSTVÍ SILNIC A DÁLNIC
Ředitelství silnic a dálnic s. p.
Čerčanská 2023/12, Krč, 140 00 Praha 4

Valbek, spol. s r.o.
Vaňurova 505/17
460 07 Liberec 3

	Vypracoval	L. MARTÍNEK	Zak. číslo	21-L113-001
	Zodp. projektant	ING. I. BELDA	Datum	02/2025
	Tech. kontrola	ING. I. BELDA	Stupeň	PDPS
	Akce	I/16 MLADÁ BOLESLAV - MARTINOVICE		
Zhotovitel: Valbek, spol. s r.o. Vaňurova 505/17 460 07 Liberec 3	Příloha GABIONOVÁ KŘÍDLA		Počet formátů 8x A4	
			Měřítko 1:100	
			Č. přílohy Paré	
205				

