



PODÉLNÝ ŘEZ 1:50

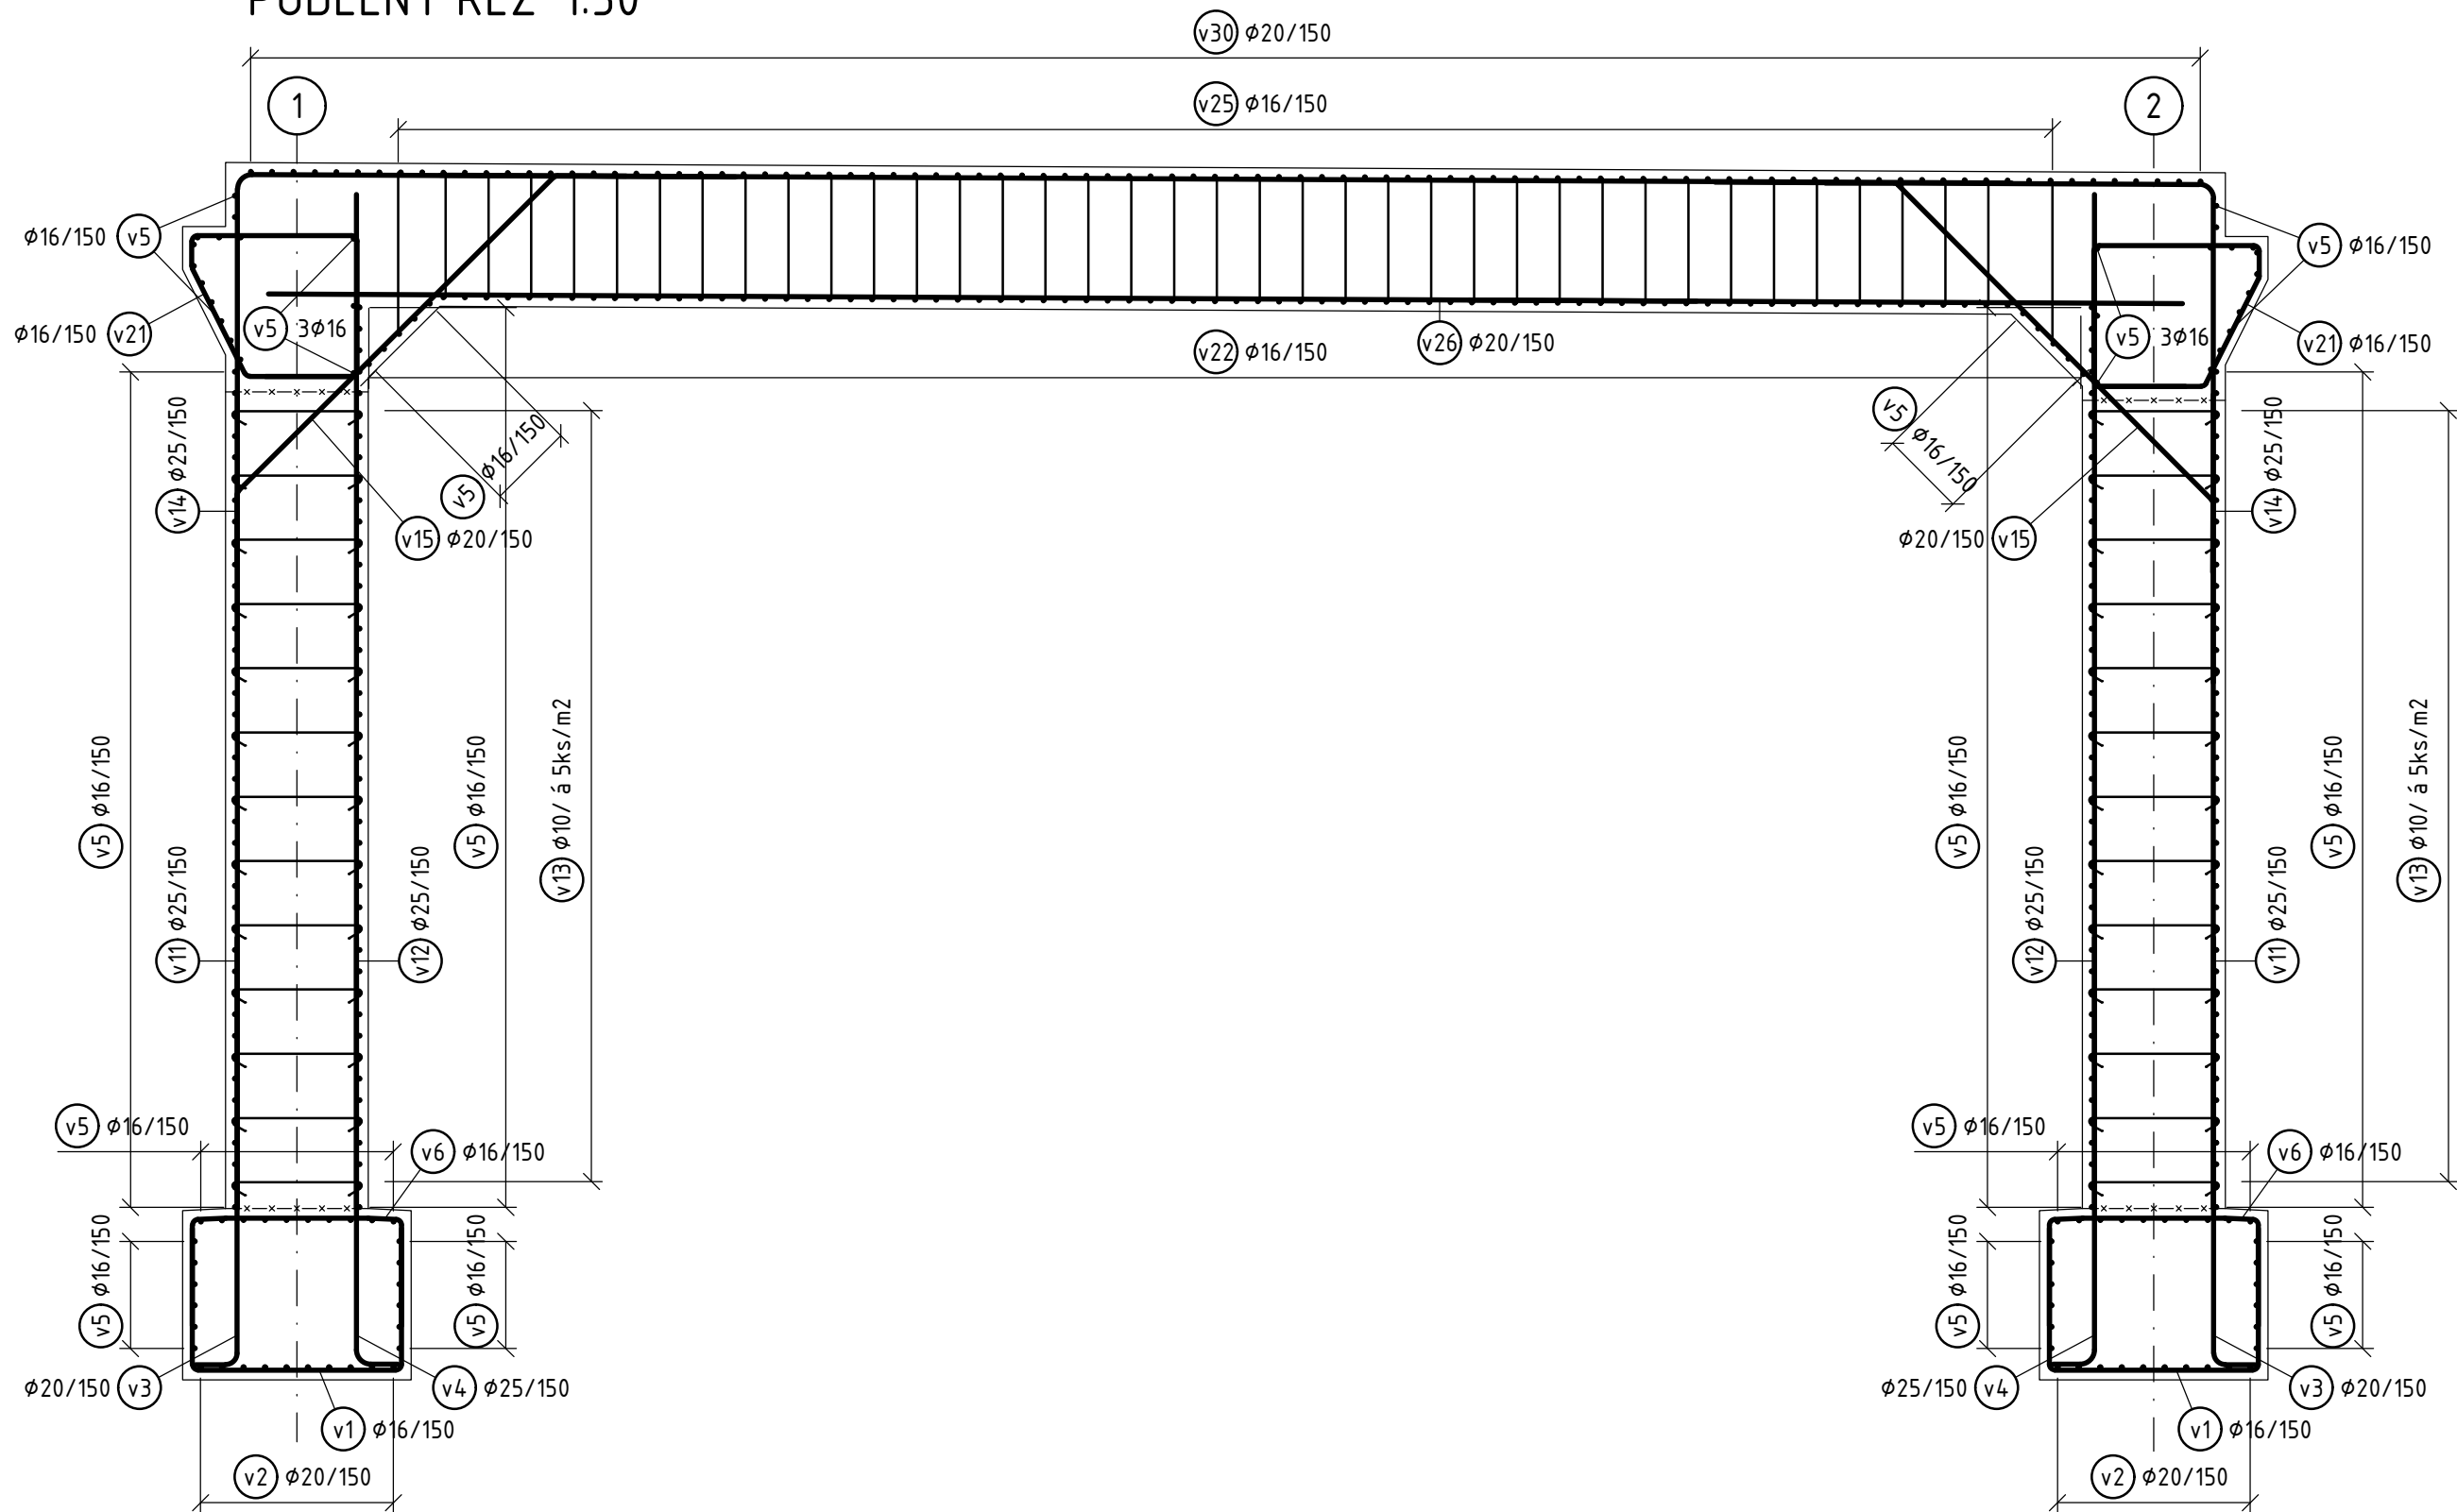

PŘÍČNÝ ŘEZ 1:50

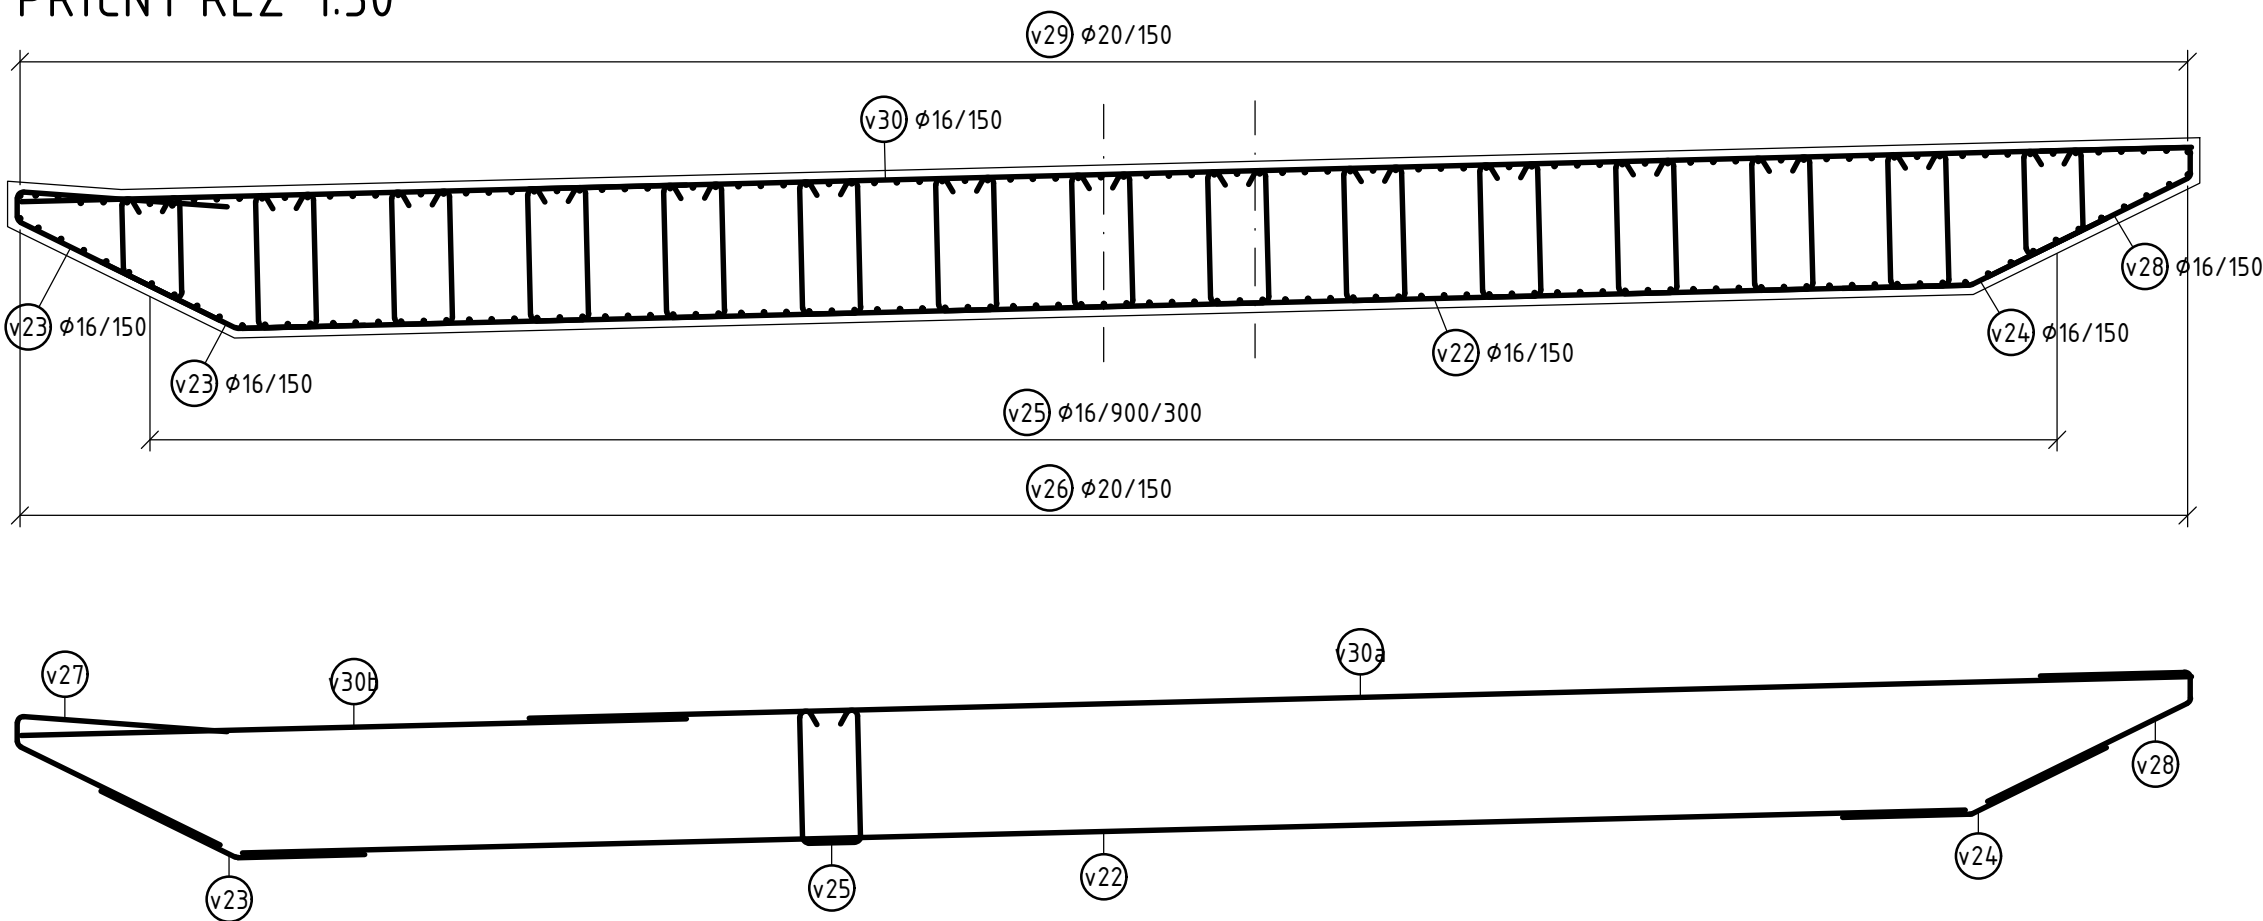


POZNÁMKY:

- NEDÍLNOU SOUČÁSTÍ VÝKRESU JSOU POZNÁMKY A SPECIFIKACE UVEDENÉ NA VÝKRESE POZNÁMEK A TECHNICKÝCH SPECIFIKACÍ

ODHAD MNOŽSTVÍ BETONÁŘSKÉ VÝZTUŽE SO 203	MNOŽSTVÍ VÝZTUŽE V %	MNOŽSTVÍ VÝZT.V KG/M3
VÝZTUŽ PILOT POD OPĚROU 01, D 900 mm	2.10%	165.0
VÝZTUŽ PILOT POD OPĚROU 02, D 900 mm	2.10%	165.0
VÝZTUŽ ZÁKLADŮ OPĚRY 01	3.18%	250.0
VÝZTUŽ ZÁKLADŮ OPĚRY 02	3.18%	250.0
VÝZTUŽ NOSNÉ KONSTRUKCE	1.27%	100.0
VÝZTUŽ ŘÍMS	1.78%	140.0
VÝZTUŽ PŘECHODOVÝCH DESEK	1.91%	150.0

ŘEZ KŘÍDELM 1:50

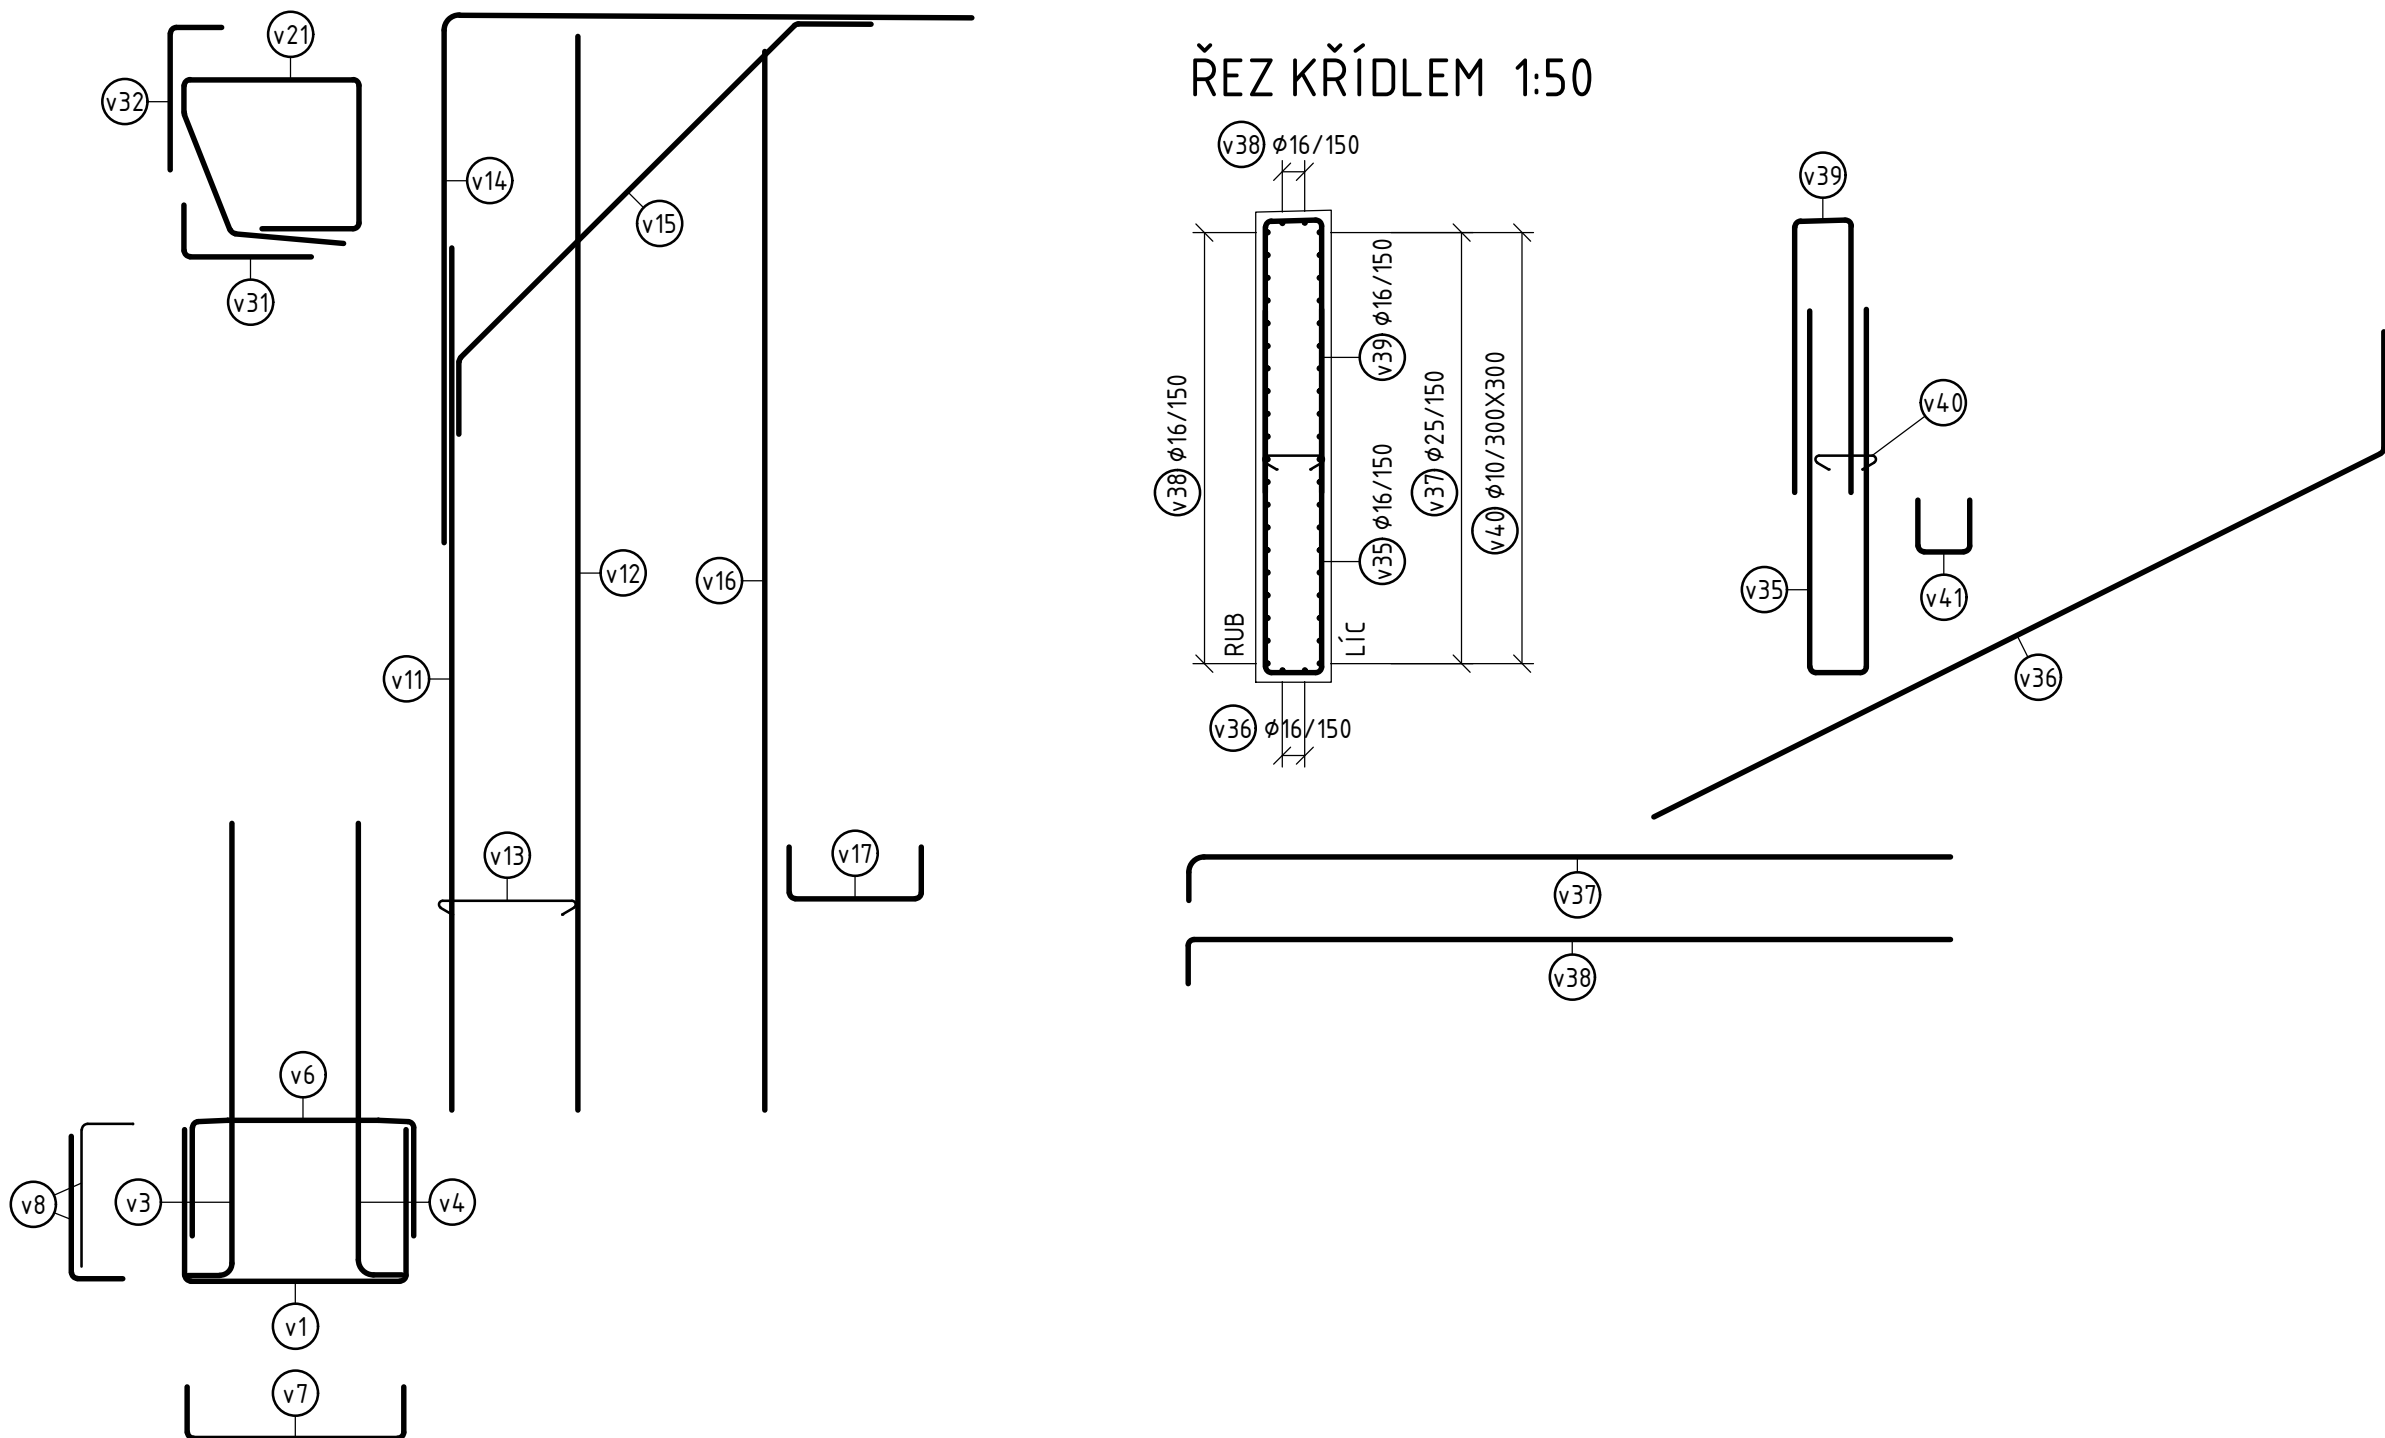

Souřadnicový systém: S-JTSK
Výškový systém: BpV

SO 203 MOST NA I/16 PŘES PŘELOŽKU POLNÍ CESTY V KM 3,790

Objednatel:



Ředitelství silnic a dálnic s. p.
Čerčanská 2023/12, Krč, 140 00 Praha 4



Valbek, spol. s r.o.
Vaňurova 505/17
460 07 Liberec 3



Vypracoval	L. MARTINEK	<i>Handwritten signature</i>	Zak. číslo	21-L113-001
Zodp. projektant	ING. I. BELDA	<i>Handwritten signature</i>	Datum	02/2025
Tech. kontrola	ING. I. BELDA	<i>Handwritten signature</i>	Stupeň	PDPS
Akce	I/16 MLADÁ BOLESLAV - MARTINOVICE		Počet formátů	8x A4
			Měřítko	1:50
Příloha			Č. přílohy	Paré
SCHÉMATICKÝ VÝKRES VÝZTUŽE			301	

MĚŘÍTKO 1:50 0.5 0 0.5 1 1.5 2 2.5 3 3.5 4 4.5 5m