



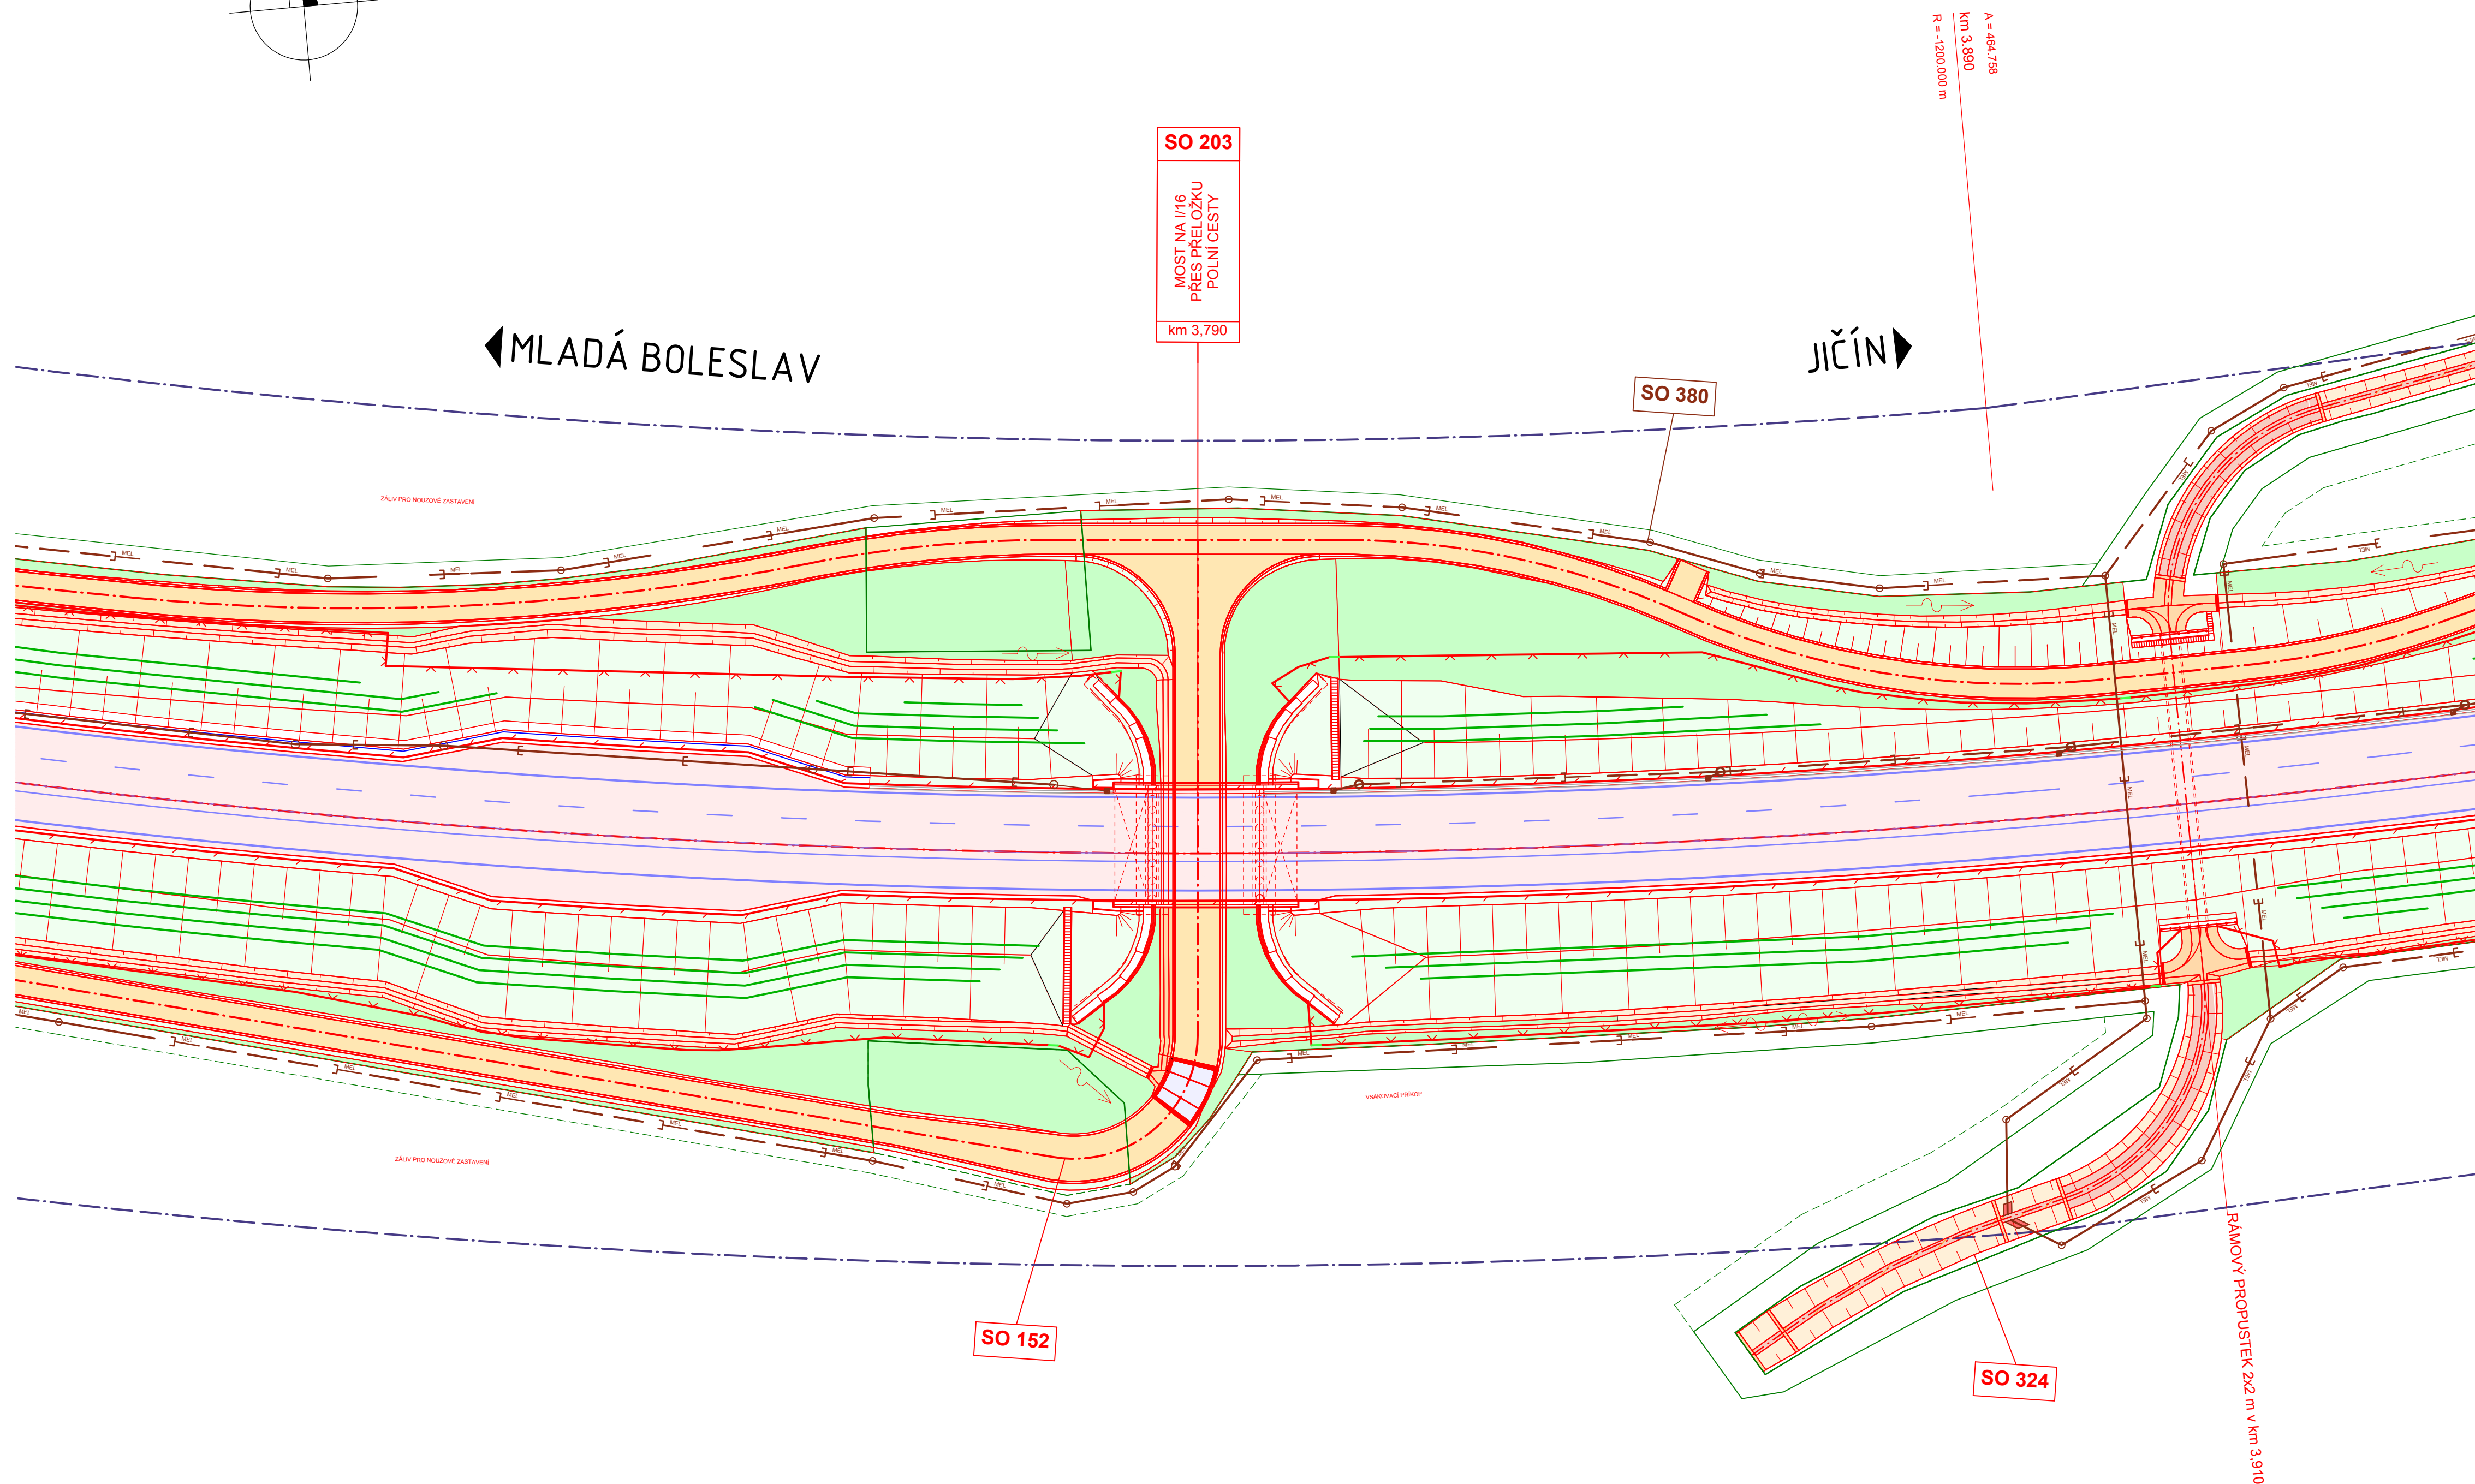

Souřadnicový systém: S-JTSK
Výškový systém: Bpv

SO 203 MOST NA I/16 PŘES PŘELOŽKU POLNÍ CESTY V KM 3,790

Objednatel:

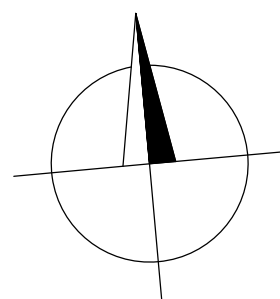

Ředitelství silnic a dálnic s. p.
Čerčanská 2023/12, Krč, 140 00 Praha 4



Valbek, spol. s r.o.
Vaňurova 505/17
460 07 Liberec 3

	Vypracoval	ING. I. BELDA	<i>[Signature]</i>	Zak. číslo	21-L113-001
	Zodp. projektant	ING. I. BELDA	<i>[Signature]</i>	Datum	02/2025
	Tech. kontrola	ING. I. BELDA	<i>[Signature]</i>	Stupeň	PDPS
	Akce	I/16 MLADÁ BOLESLAV - MARTINOVICE			Počet formátů 8x A4
Zhotovitel:		Příloha		401	
Valbek, spol. s r.o. Vaňurova 505/17 460 07 Liberec 3		PŘEHLEDNÁ SITUACE		Měřítko 1:500 Č. přílohy Paré	