

PŮDORYS 1:150

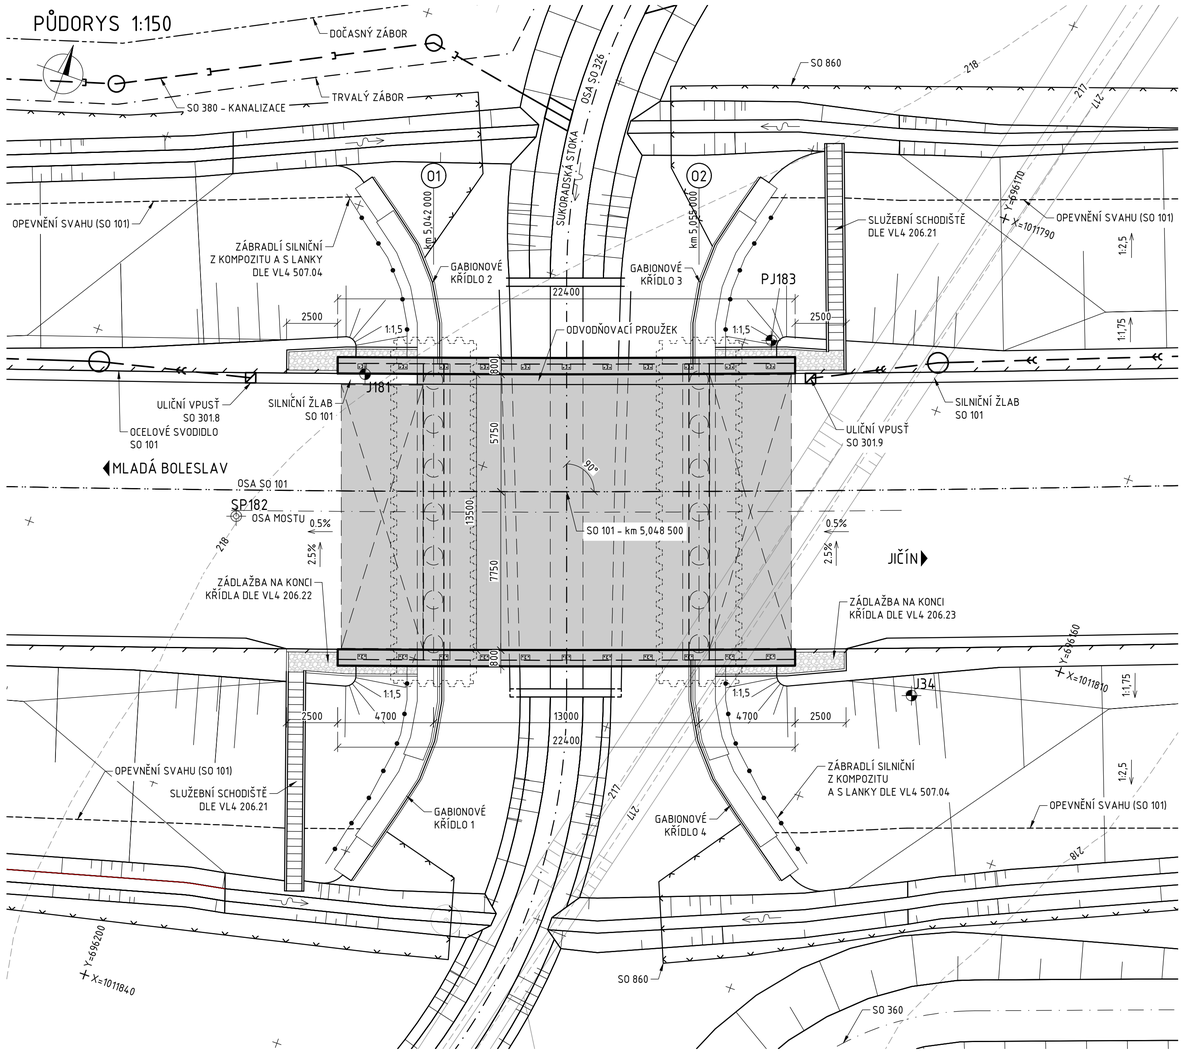

PODÉLNÝ ŘEZ 1:150

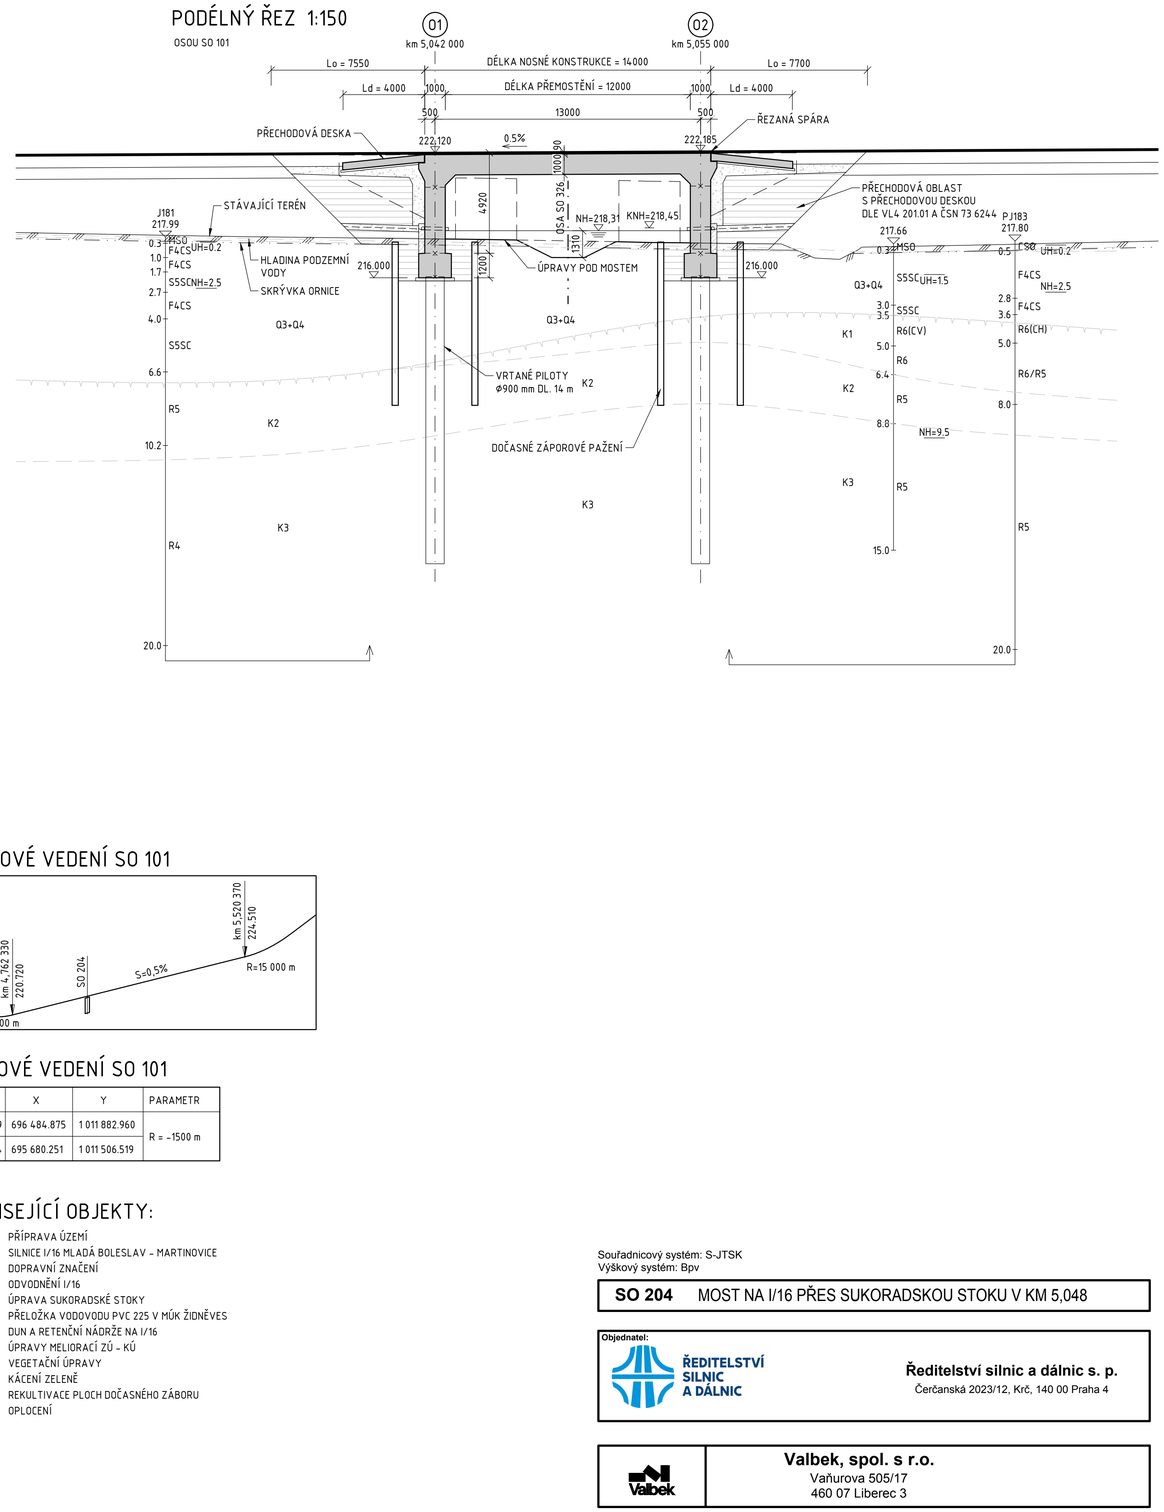

VÝŠKOVÉ VEDENÍ SO 101

SMĚROVÉ VEDENÍ SO 101


STANIČENÍ	X	Y	PARAMETR
km 3.339 39	696 484.875	1 011 882.960	R = –1500 m
km 5.641 84	695 680.251	1 011 506.519	

SOUVISEJÍCÍ OBJEKTY:

SO 020	PŘÍPRAVA ÚZEMÍ
SO 101	SILNICE I/16 MLADÁ BOLESLAV – MARTINOVICE
SO 190	DOPRAVNÍ ZNAČENÍ
SO 301.x	ODVODNĚNÍ I/16
SO 326	ÚPRAVA SUKORADSKÉ STOKY
SO 342	PŘELOŽKA VODOVODU PVC 225 V MÚK ŽIDNĚVES
SO 360.x	DUN A RETENČNÍ NÁDRŽE NA I/16
SO 380	ÚPRAVY MELIORACÍ ZÚ – KÚ
SO 801	VEGETAČNÍ ÚPRAVY
SO 810	KÁCENÍ ZELENĚ
SO 830	REKULTIVACE PLOCH DOČASNÉHO ZÁBORU
SO 860	OPLOCENÍ

VZOROVÝ PŘÍČNÝ ŘEZ 1:75

S13,5/90

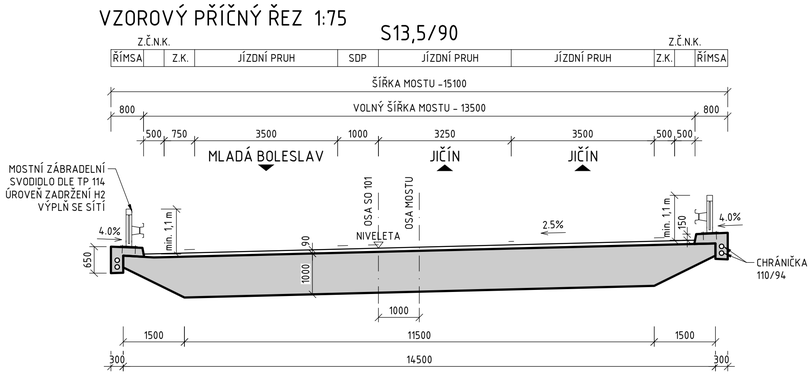

LEGENDA

TRVALÝ ZÁBOR
DOČASNÝ ZÁBOR nad 1 rok
DOČASNÝ ZÁBOR do 1 roku

MĚŘÍTKO 1 : 75 — 0.75 0 0.75 1.5 2.25 3 3.75 4.5 5.25 6 6.75 7.5m

MĚŘÍTKO 1 : 150 — 1.5 0 1.5 3 4.5 6 7.5 9 10.5 12 13.5 15m

Souřadnicový systém: S-JTSK
Výškový systém: Bpv

SO 204 MOST NA I/16 PŘES SUKORADSKOU STOKU V KM 5,048

Objednatel:
ŘEDITELSTVÍ SILNIC A DÁLNIC
Ředitelství silnic a dálnic s. p.
Čerčanská 2023/12, Krč, 140 00 Praha 4

Valbek
Valbek, spol. s r.o.
Vaňurova 505/17
460 07 Liberec 3

Vypracoval	L. MARTÍNEK		Zak. číslo	21-LI13-001
Zodp. projektant	ING. I. BELDA		Datum	02/2025
Tech. kontrola	ING. I. BELDA		Stupeň	PDPS
Akce: I/16 MLADÁ BOLESLAV - MARTINOVICE			Počet formátů	8x A4
			Měřítko	1:150,75
			Č. přílohy	Paré
Zhotovitel: Valbek, spol. s r.o. Vaňurova 505/17 460 07 Liberec 3	Příloha: PŮDORYS, PODÉLNÝ ŘEZ, VZOROVÝ PŘÍČNÝ ŘEZ		102	