




PŮDORYS 1:100

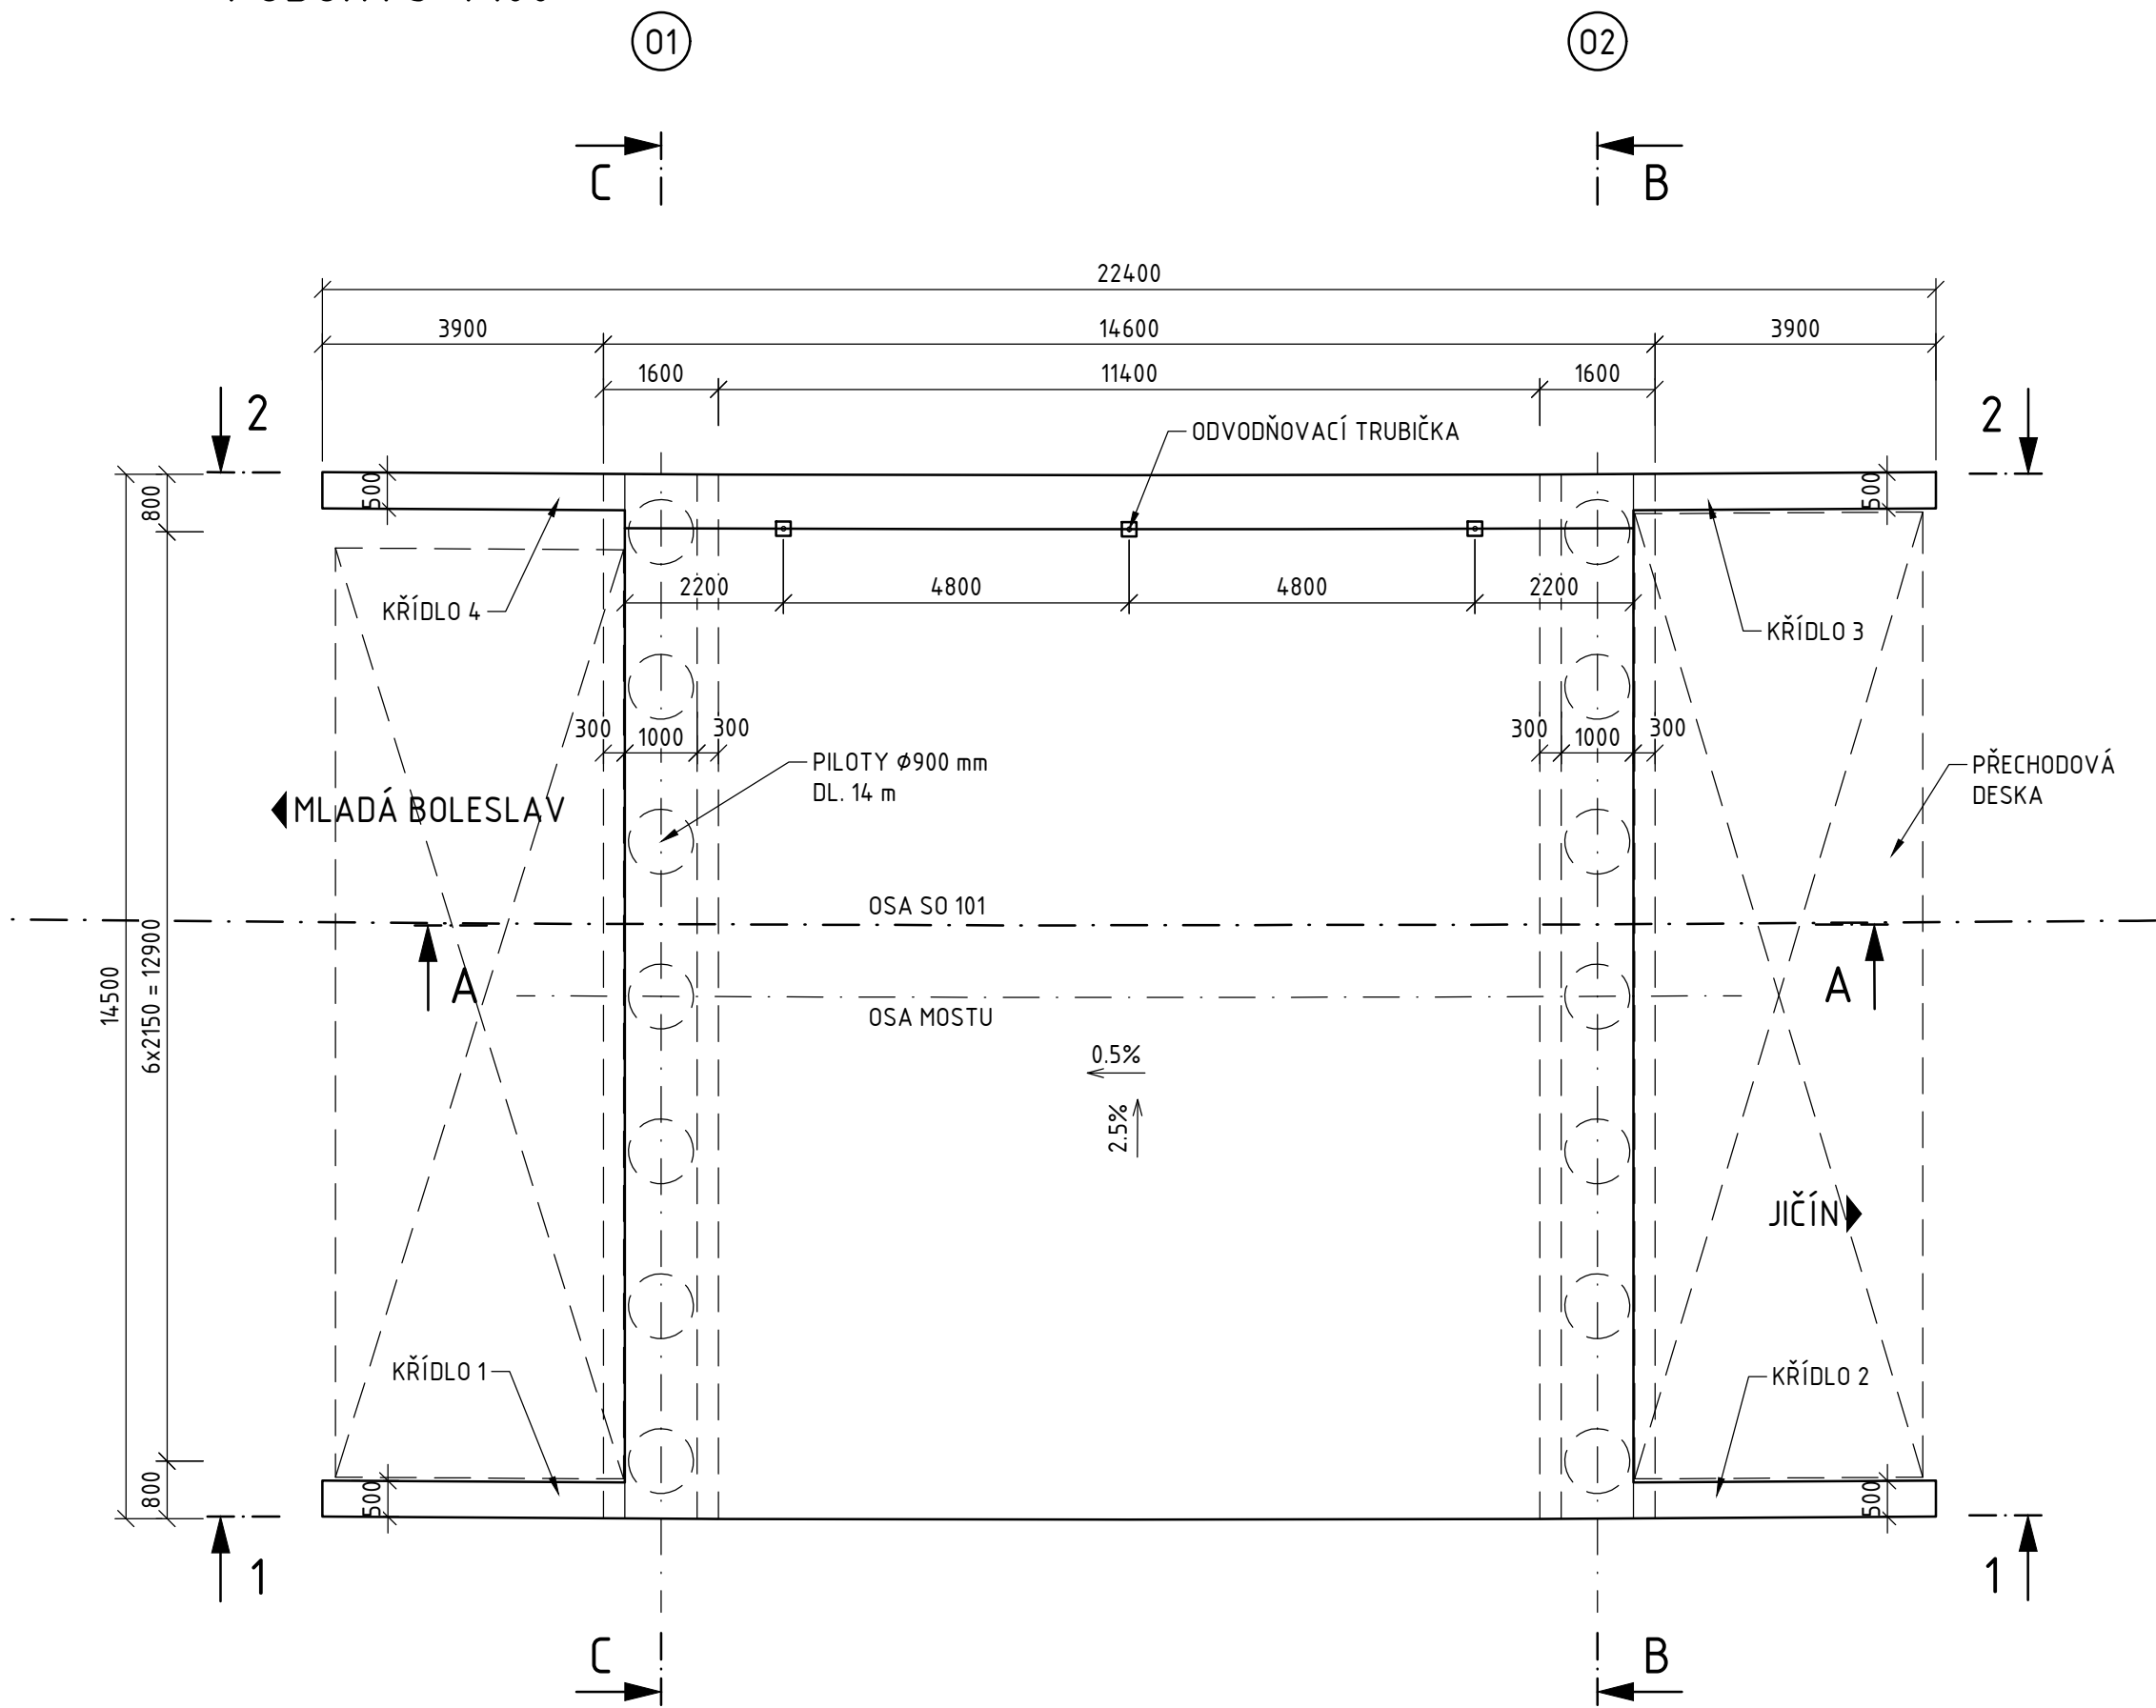


POHLED 1-1 1:100

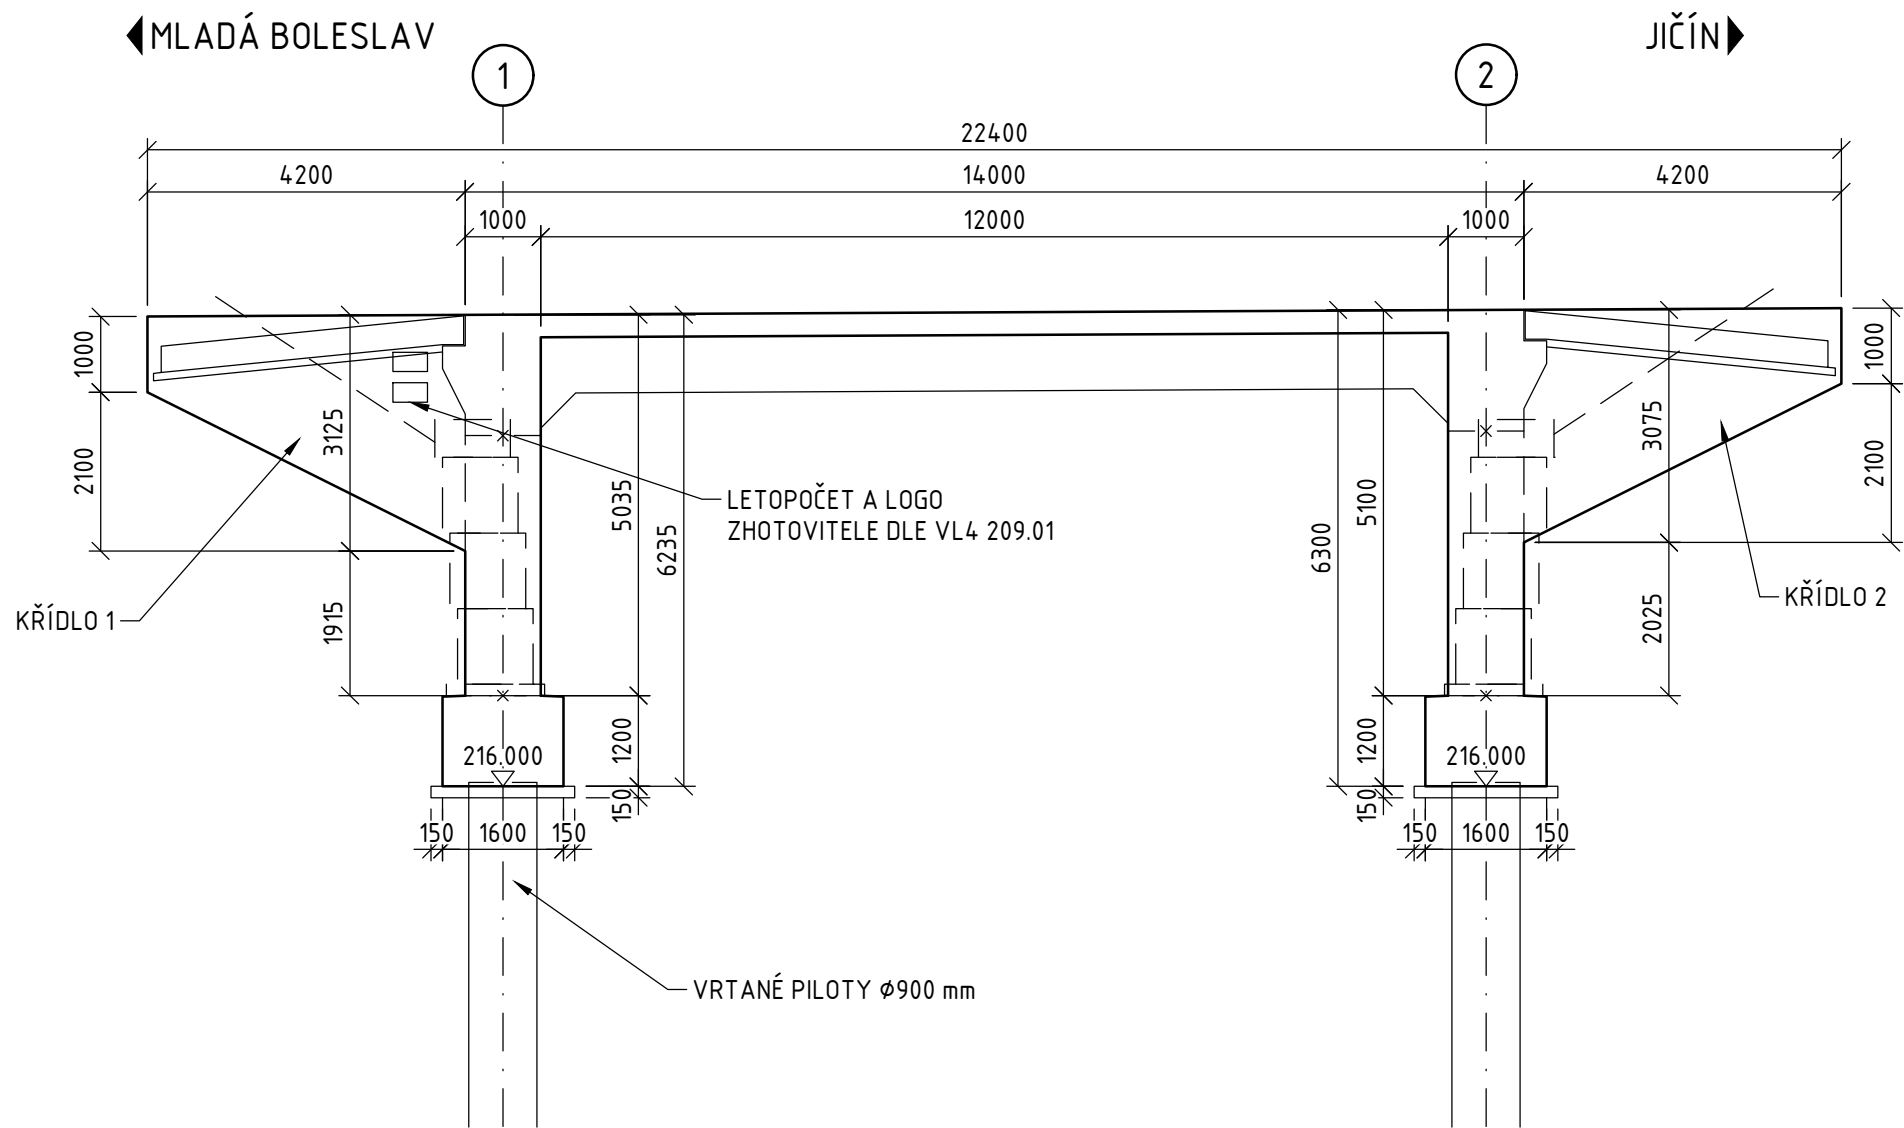

ŘEZ A-A 1:100

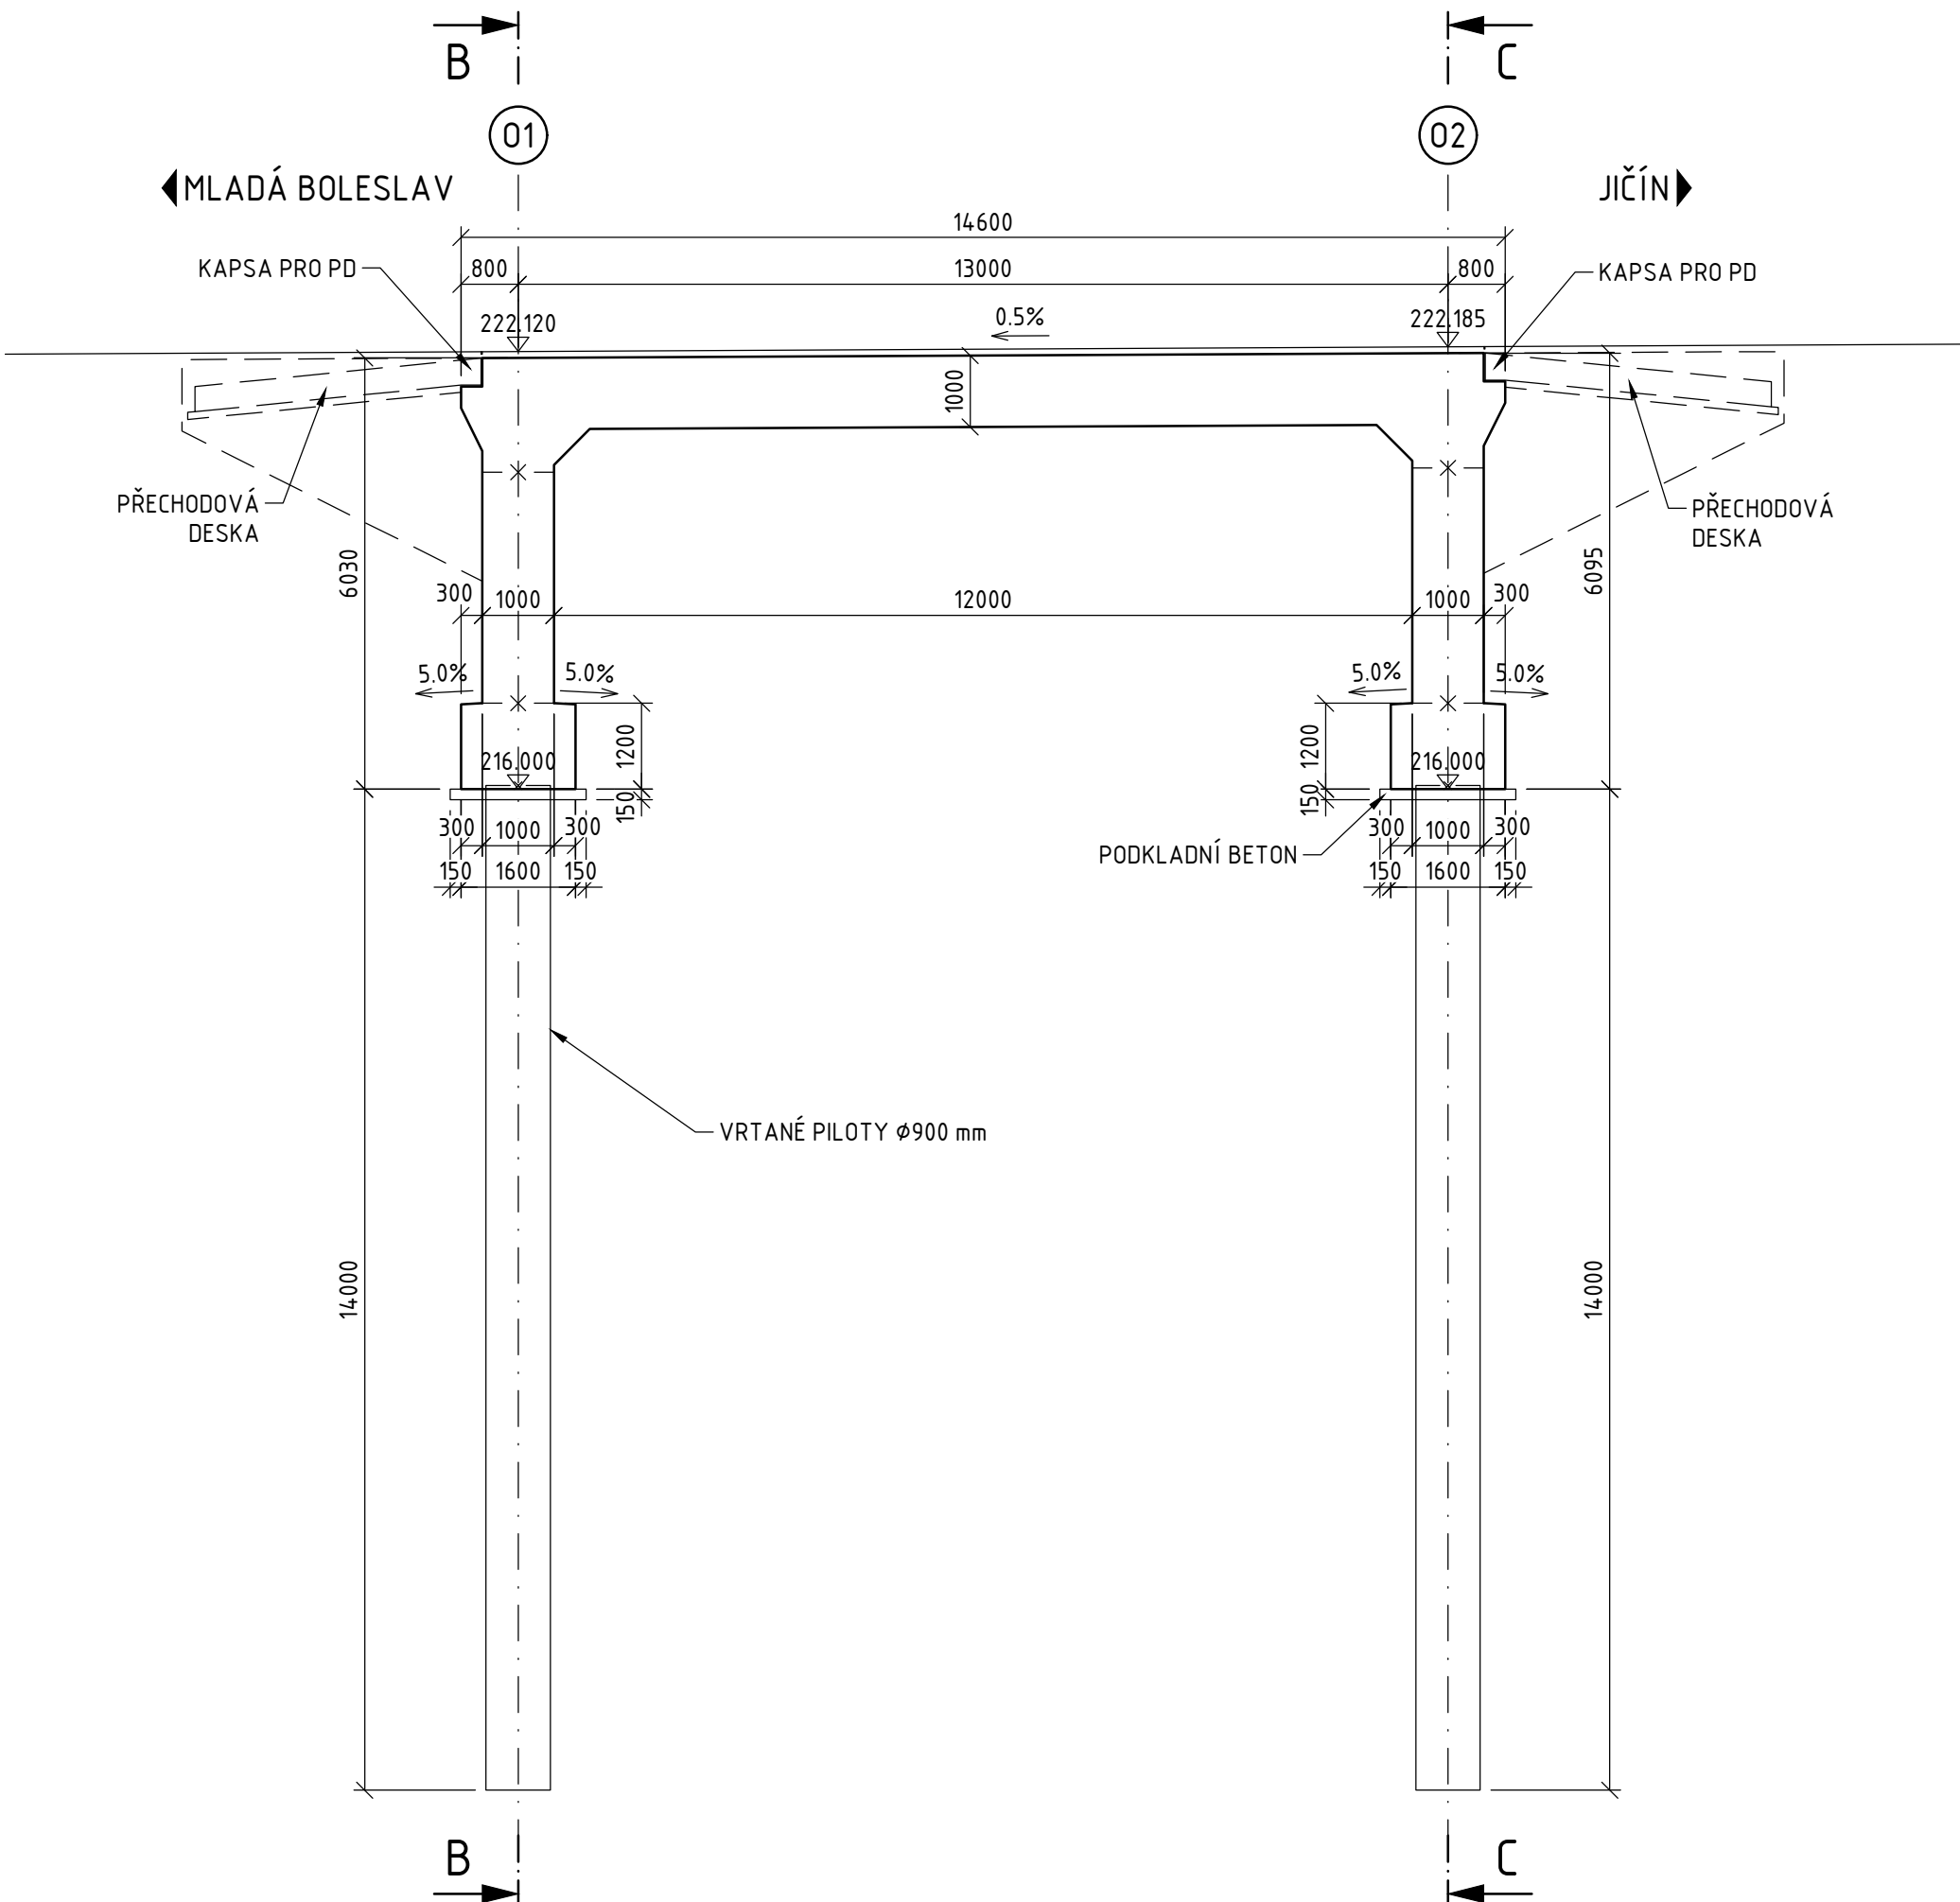

POHLED 2-2 1:100

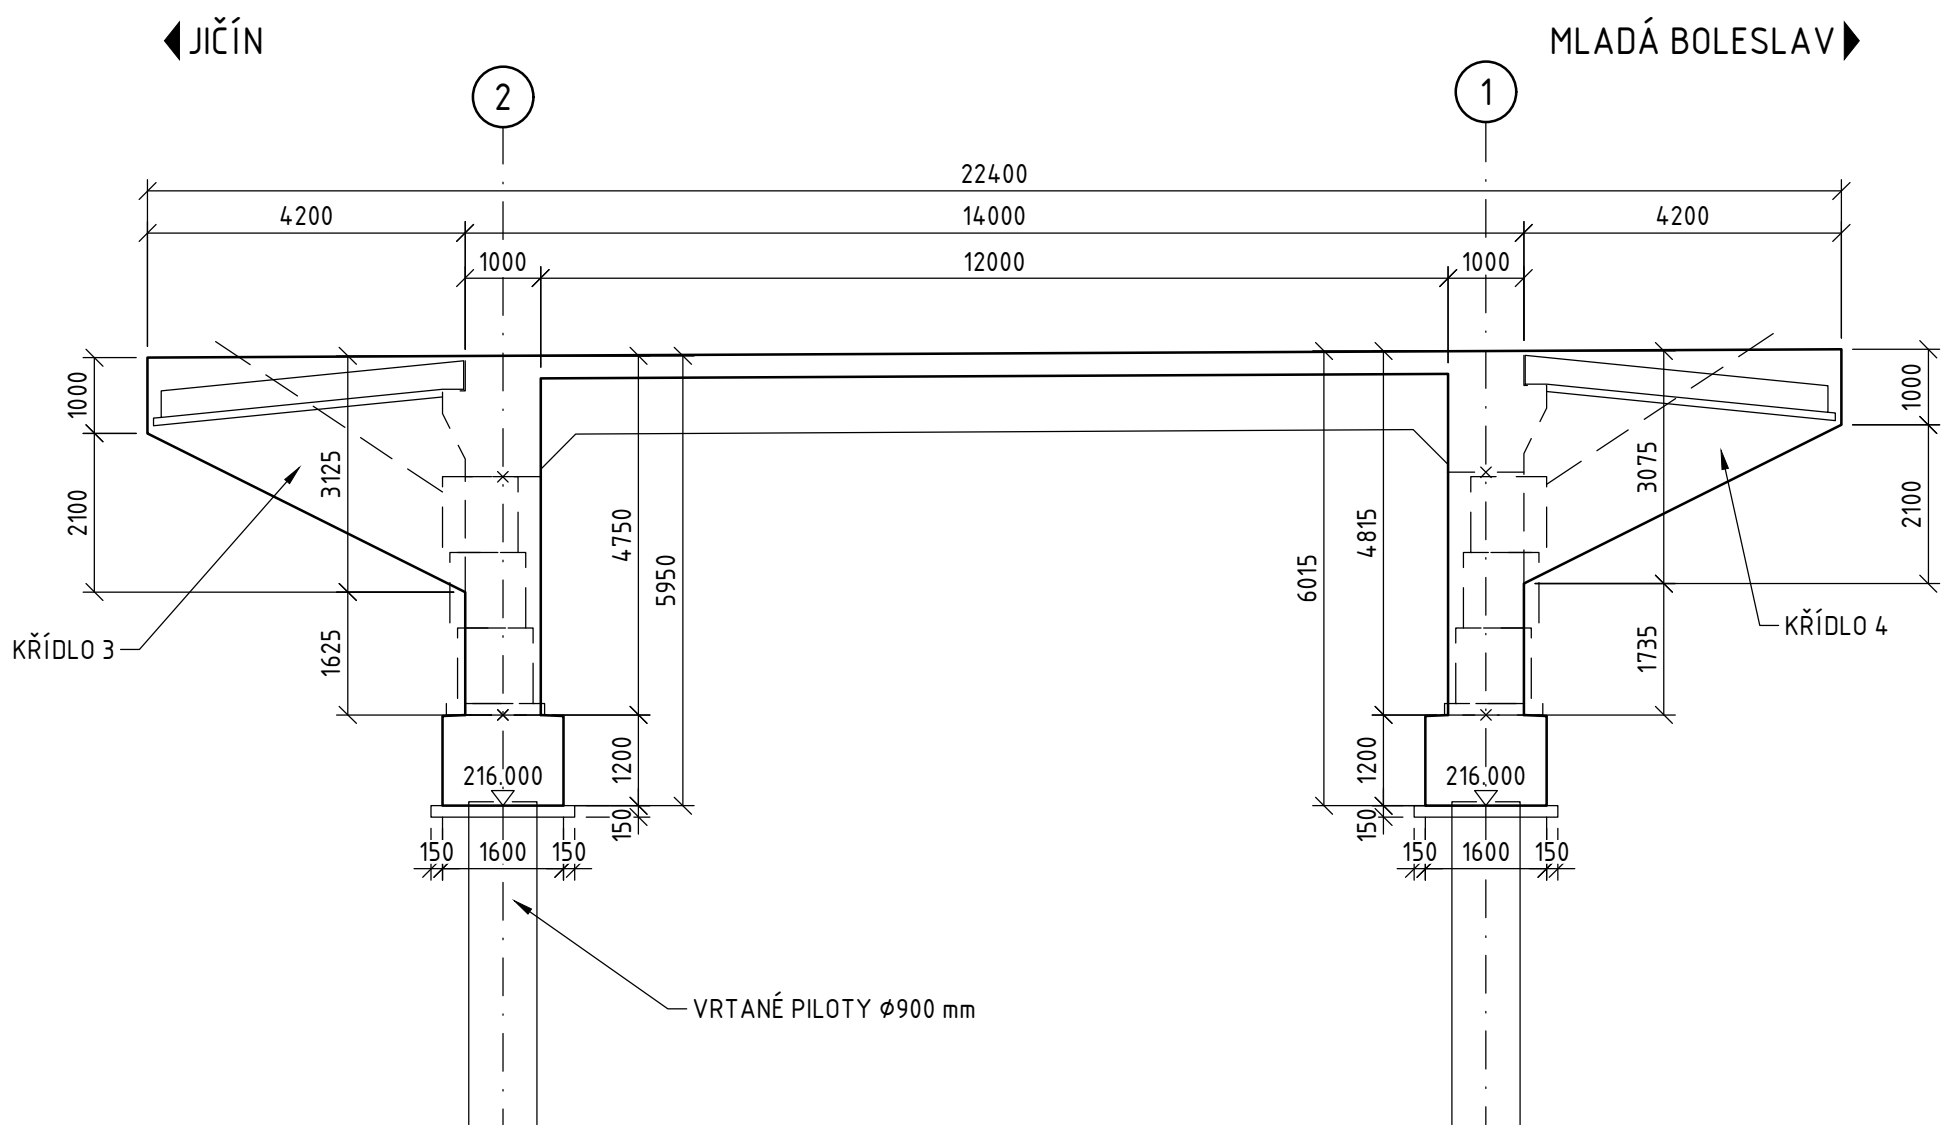

LEGENDA:

— x — PRACOVNÍ SPÁRA

POZNÁMKY:

- NEDÍLNOU SOUČÁSTÍ VÝKRESU JSOU POZNÁMKY A SPECIFIKACE UVEDENÉ NA VÝKRESE POZNÁMEK A TECHNICKÝCH SPECIFIKACÍ

Souřadnicový systém: S-JTSK
Výškový systém: Bpv

SO 204 MOST NA I/16 PŘES SUKORADSKOU STOKU V KM 5,048

Objednatel:



Ředitelství silnic a dálnic s. p.
Čerčanská 2023/12, Krč, 140 00 Praha 4



Valbek, spol. s r.o.
Vaňurova 505/17
460 07 Liberec 3



Vypracoval	L. MARTINEK		Zak. číslo	21-L113-001	
Zodp. projektant	ING. I. BELDA		Datum	02/2025	
Tech. kontrola	ING. I. BELDA		Stupeň	PDPS	
Akce	I/16 MLADÁ BOESLAV - MARTINOVICE			Počet formátů	8x A4
Příloha TVAR NOSNÉ KONSTRUKCE ČÁST 1				Měřítko	1:100
				Č. přílohy	Paré
				201	

MĚŘÍTKO 1:100