



ŘEZ B-B 1:100

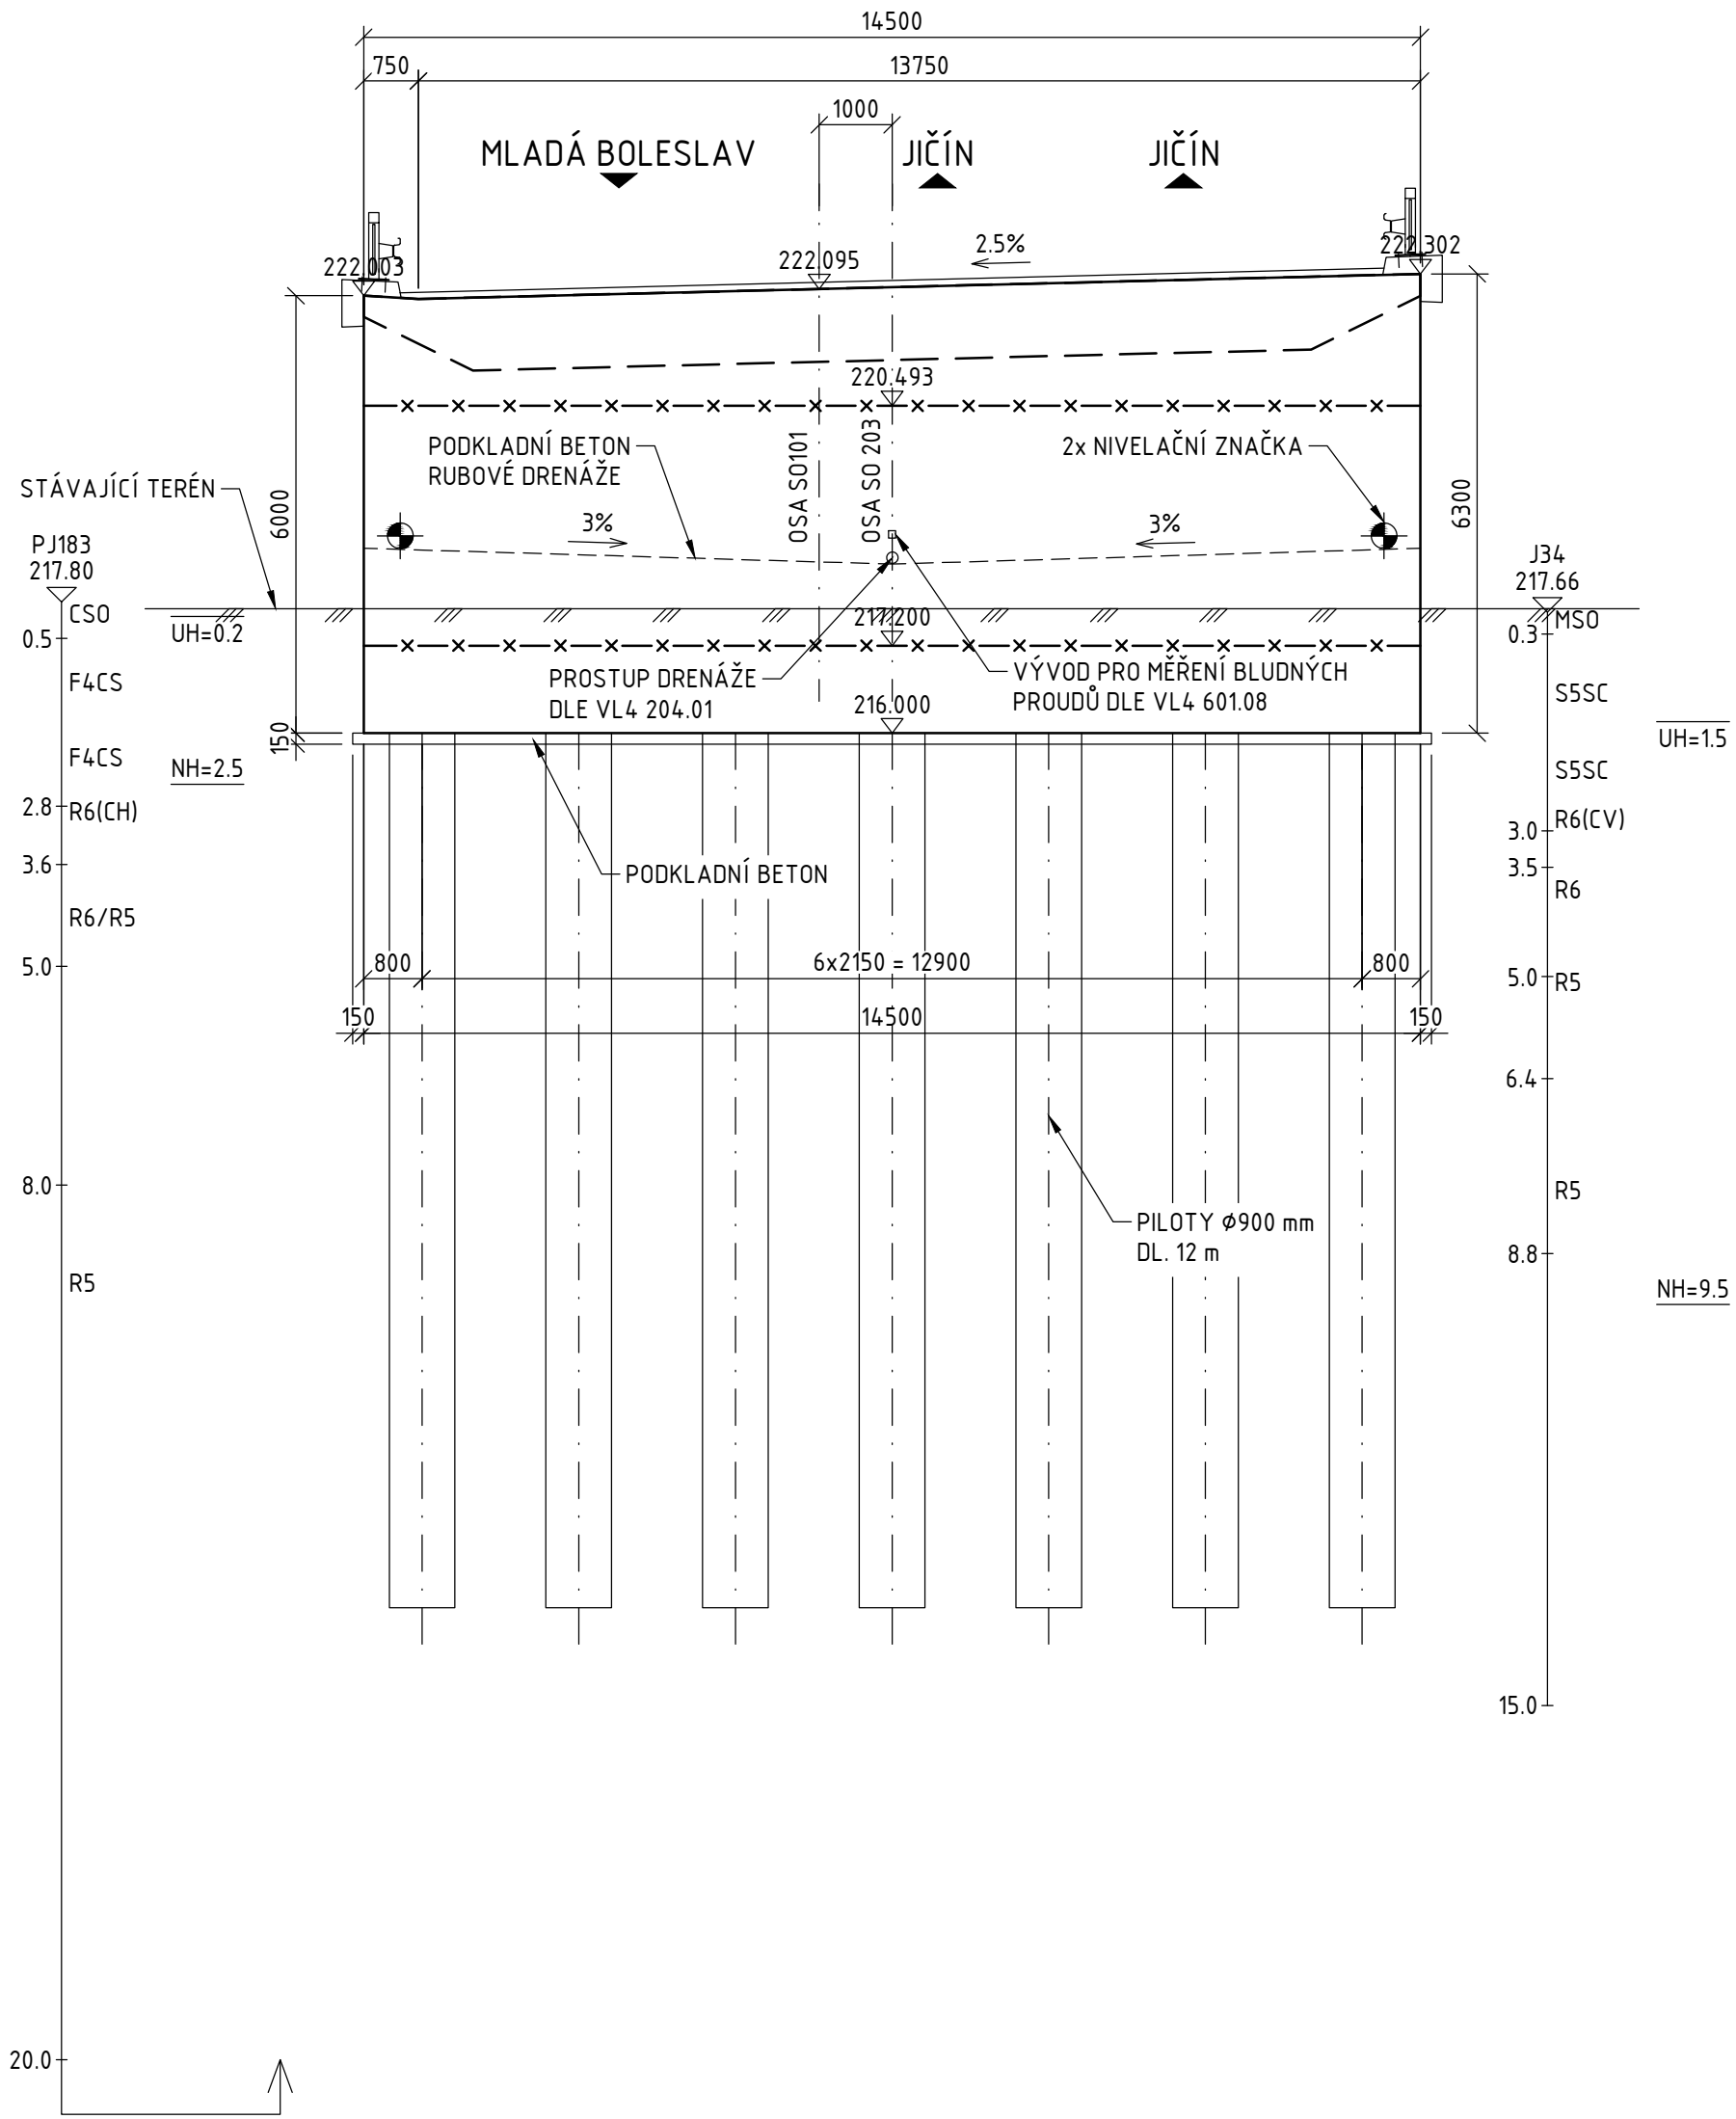

ŘEZ C-C 1:100

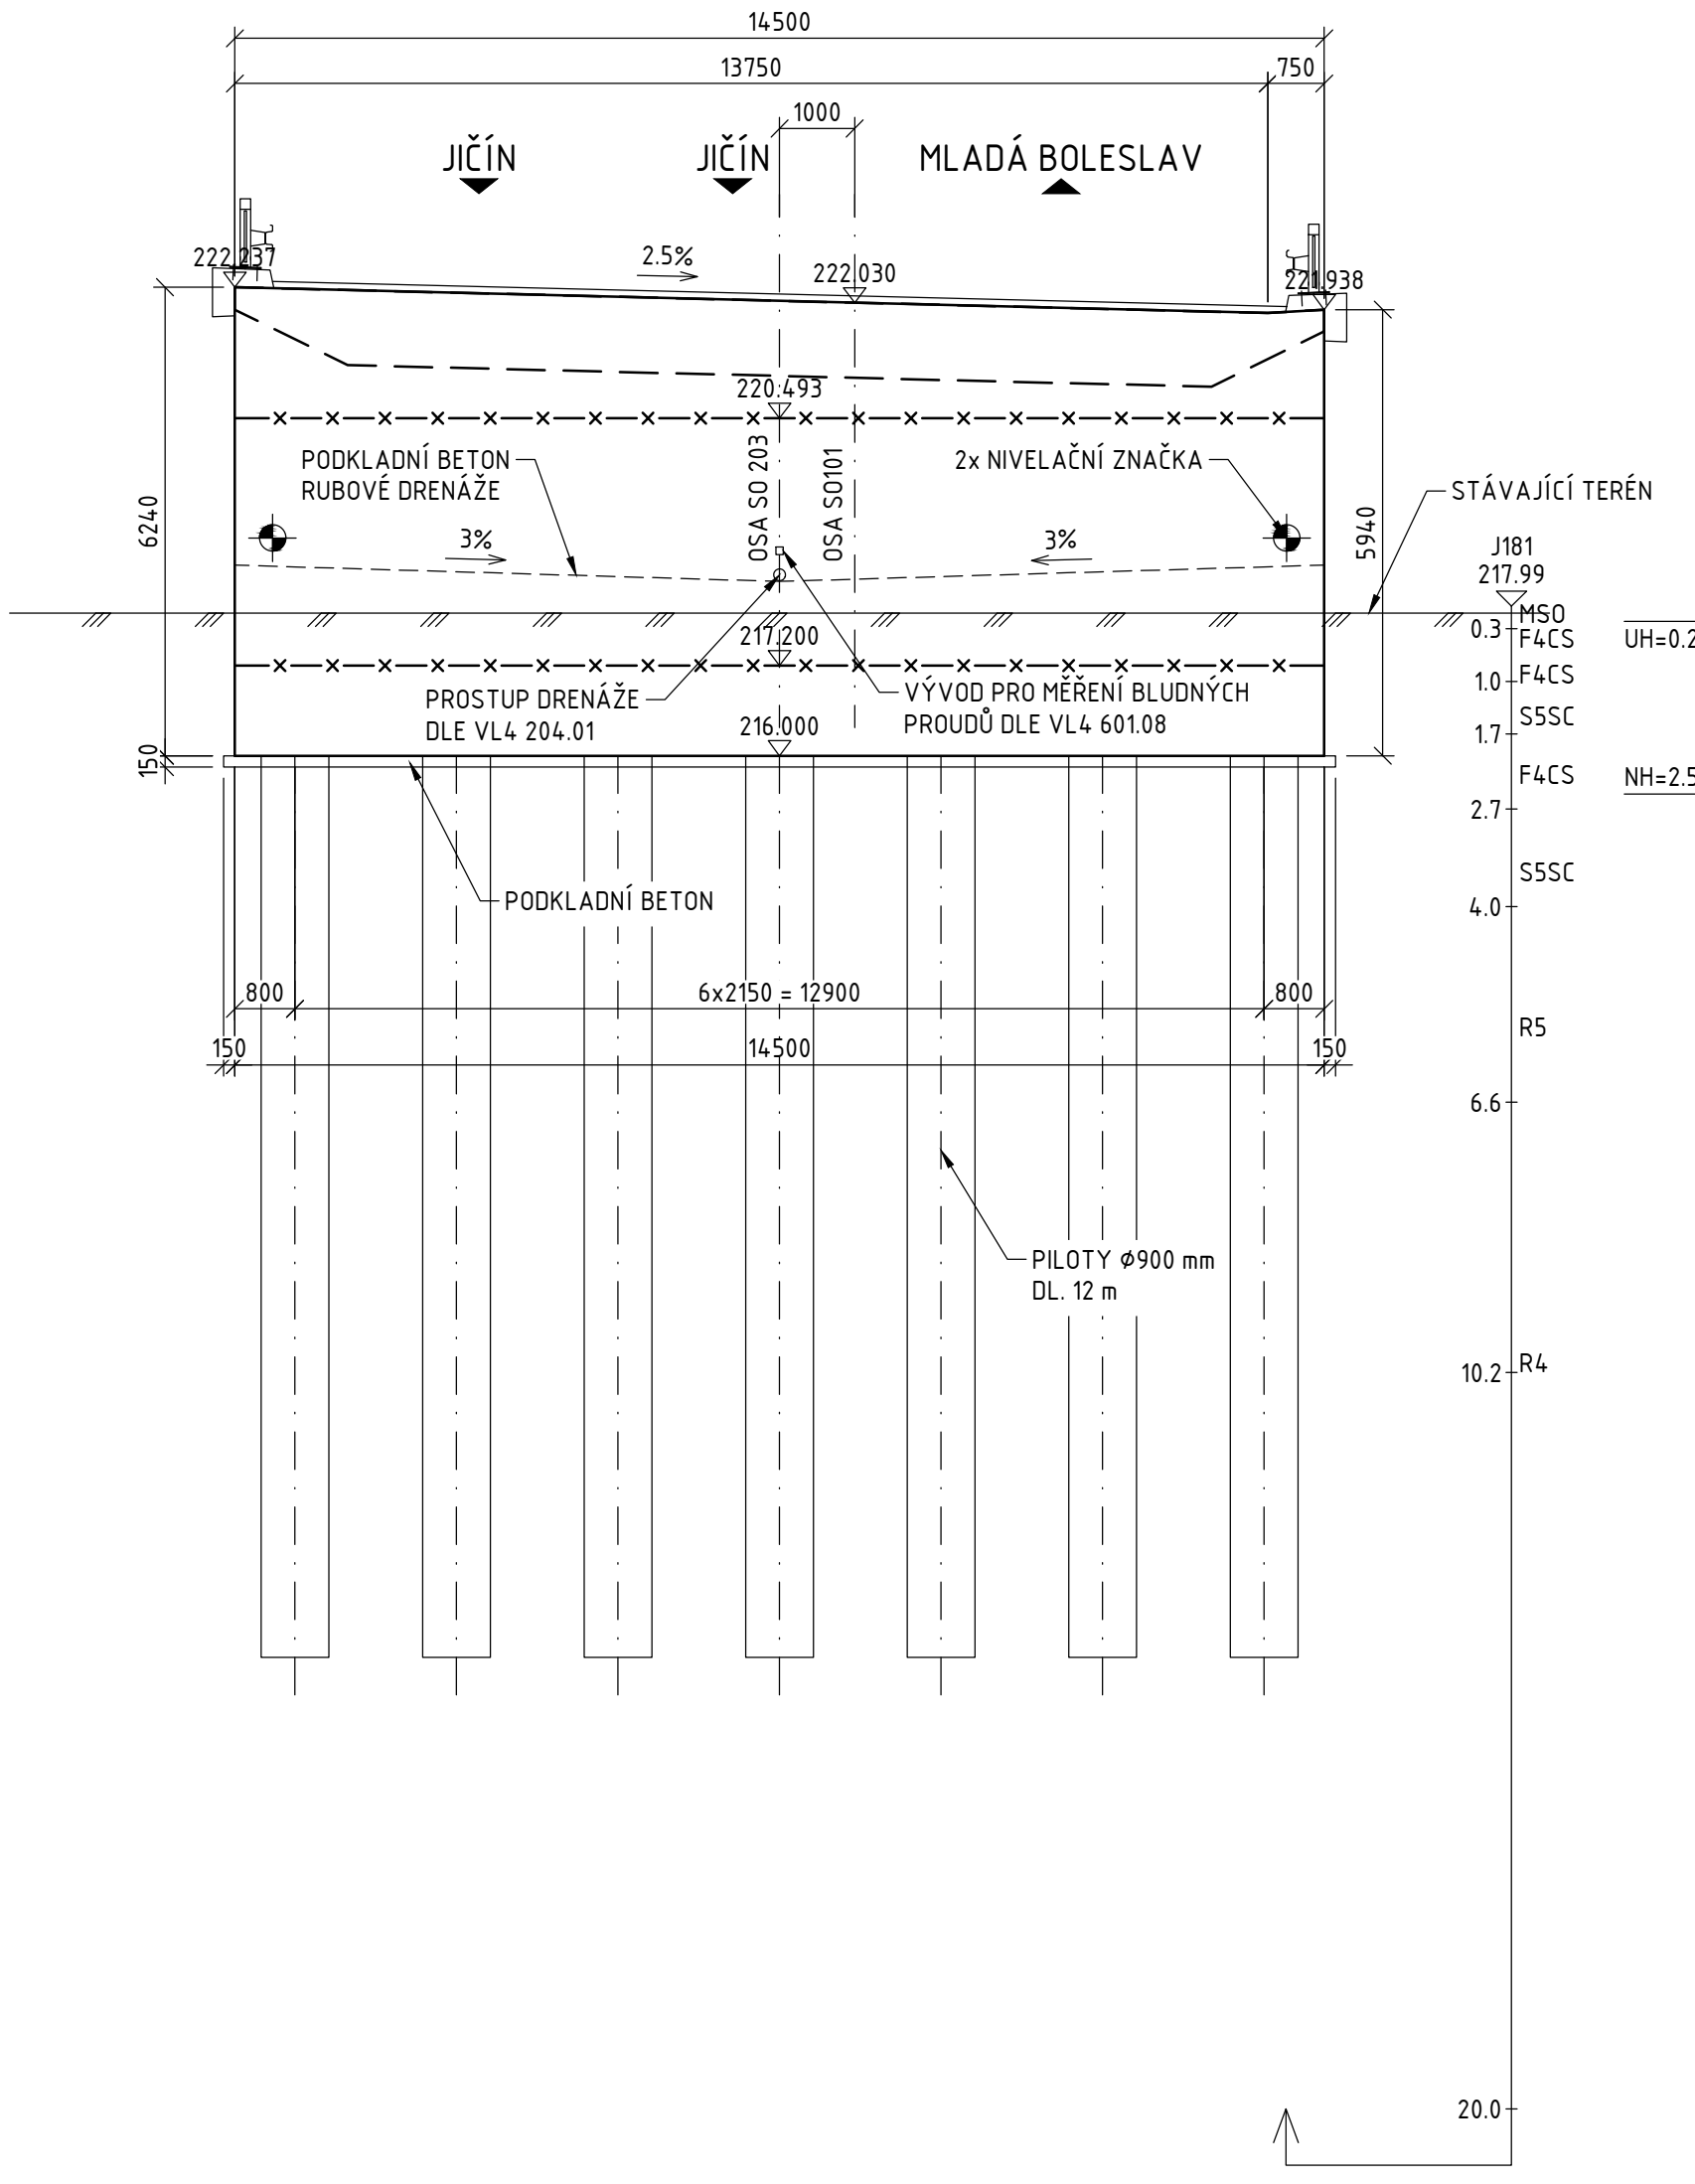


LEGENDA:

— x — PRACOVNÍ SPÁRA


POZNÁMKY:

- NEDÍLNOU SOUČÁSTÍ VÝKRESU JSOU POZNÁMKY A SPECIFIKACE UVEDENÉ NA VÝKRESE POZNÁMEK A TECHNICKÝCH SPECIFIKACÍ



VZOROVÝ PŘÍČNÝ ŘEZ 1:50

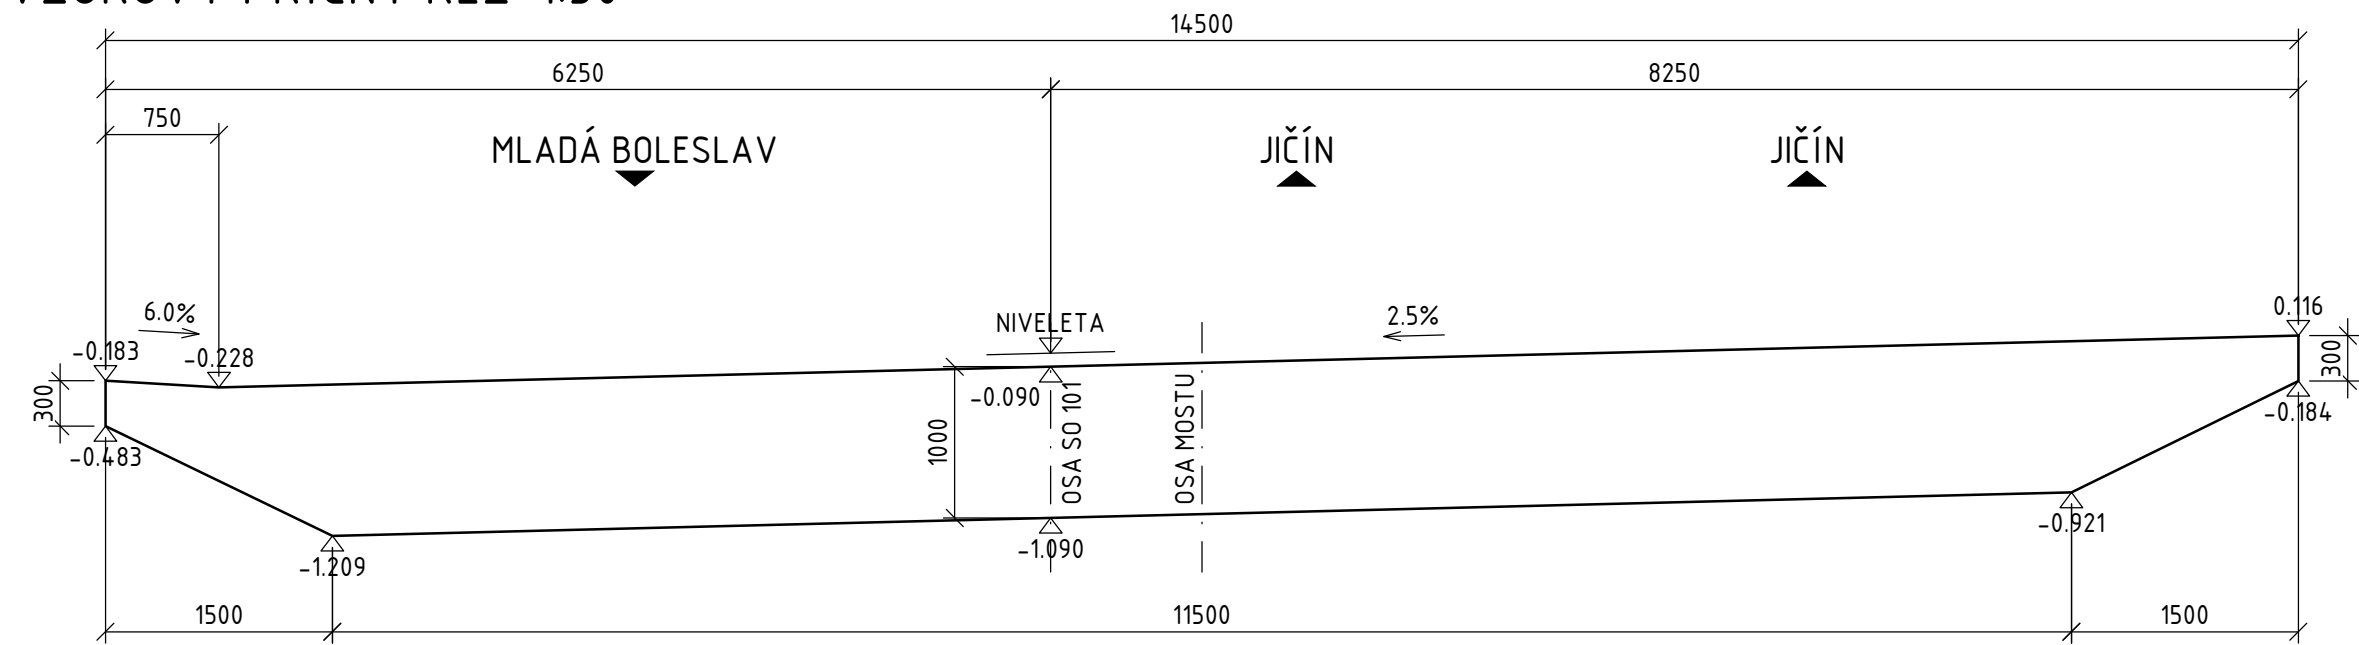

ŘEZ KŘÍDLEM 1, 2, 3, 4
1:50

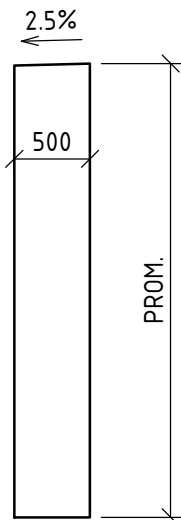

PODÉLNÝ ŘEZ PŘECHODOVOU DESKOU 1:50
VYKRESLENA PŘECHODOVÁ DESKA OPĚRY 2, PŘECHODOVÁ DESKA OPĚRY 1 ŘEŠENA OBDOBNĚ

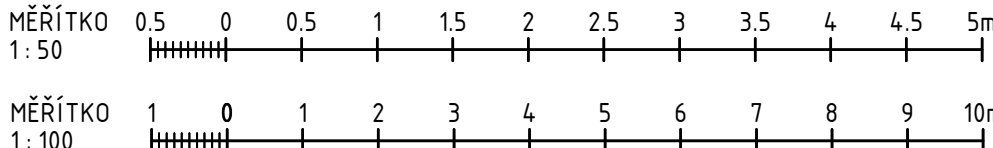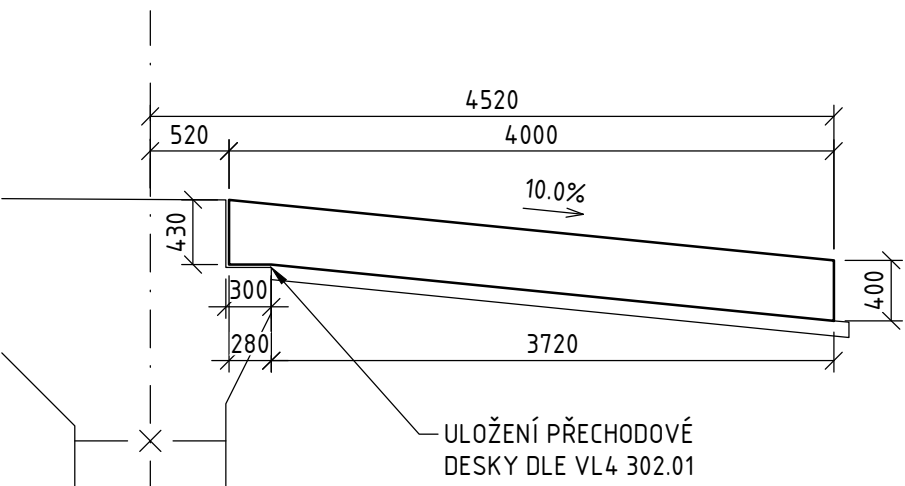

Souřadnicový systém: S-JTSK
Výškový systém: BpV

SO 204 MOST NA I/16 PŘES SUKORADSKOU STOKU V KM 5,048

Objednatel:




Ředitelství silnic a dálnic s. p.
Čerčanská 2023/12, Krč, 140 00 Praha 4



Valbek, spol. s r.o.
Vaňurova 505/17
460 07 Liberec 3

 

	Vypracoval	L. MARTINEK		Zak. číslo	21-L113-001
	Zodp. projektant	ING. I. BELDA		Datum	02/2025
	Tech. kontrola	ING. I. BELDA		Stupeň	PDPS
Akce	I/16 MLADÁ BOLESLAV - MARTINOVICE			Počet formátů	8x A4
				Měřítko	1:100,50
				Č. přílohy	Paré
Zhotovitel:	Příloha			202	
TVAR NOSNÉ KONSTRUKCE					
ČÁST 2					