




PŮDORYS 1:100

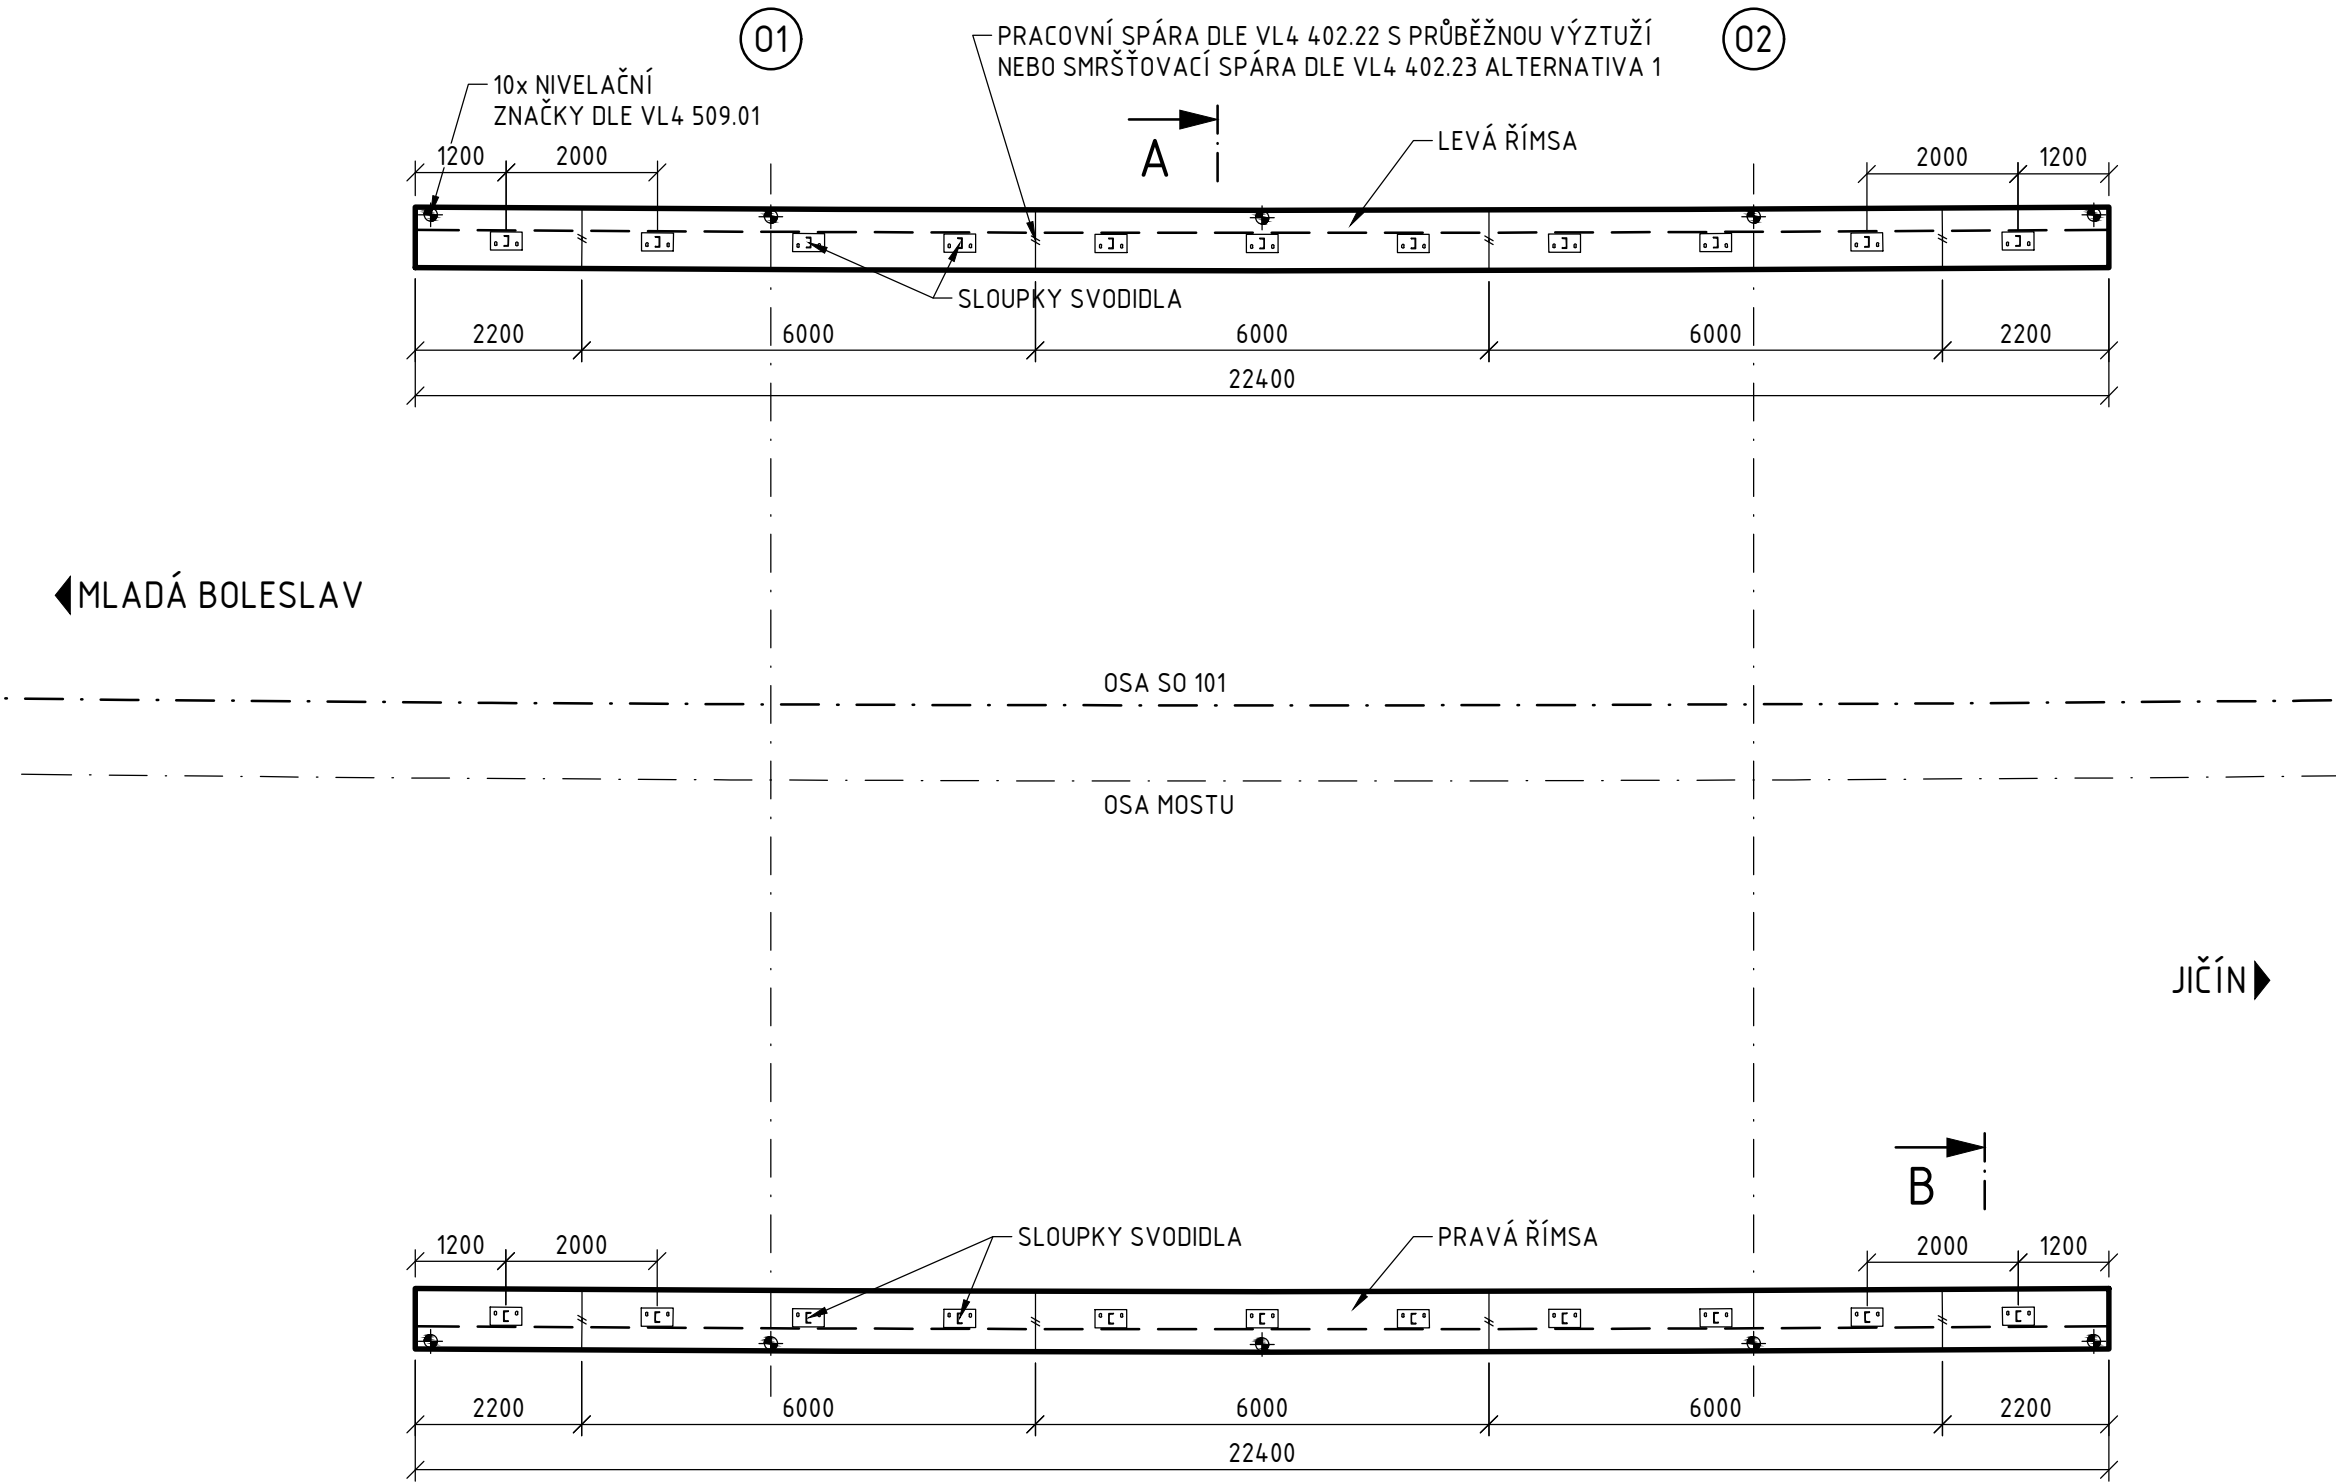


ŘEZ A-A 1:20

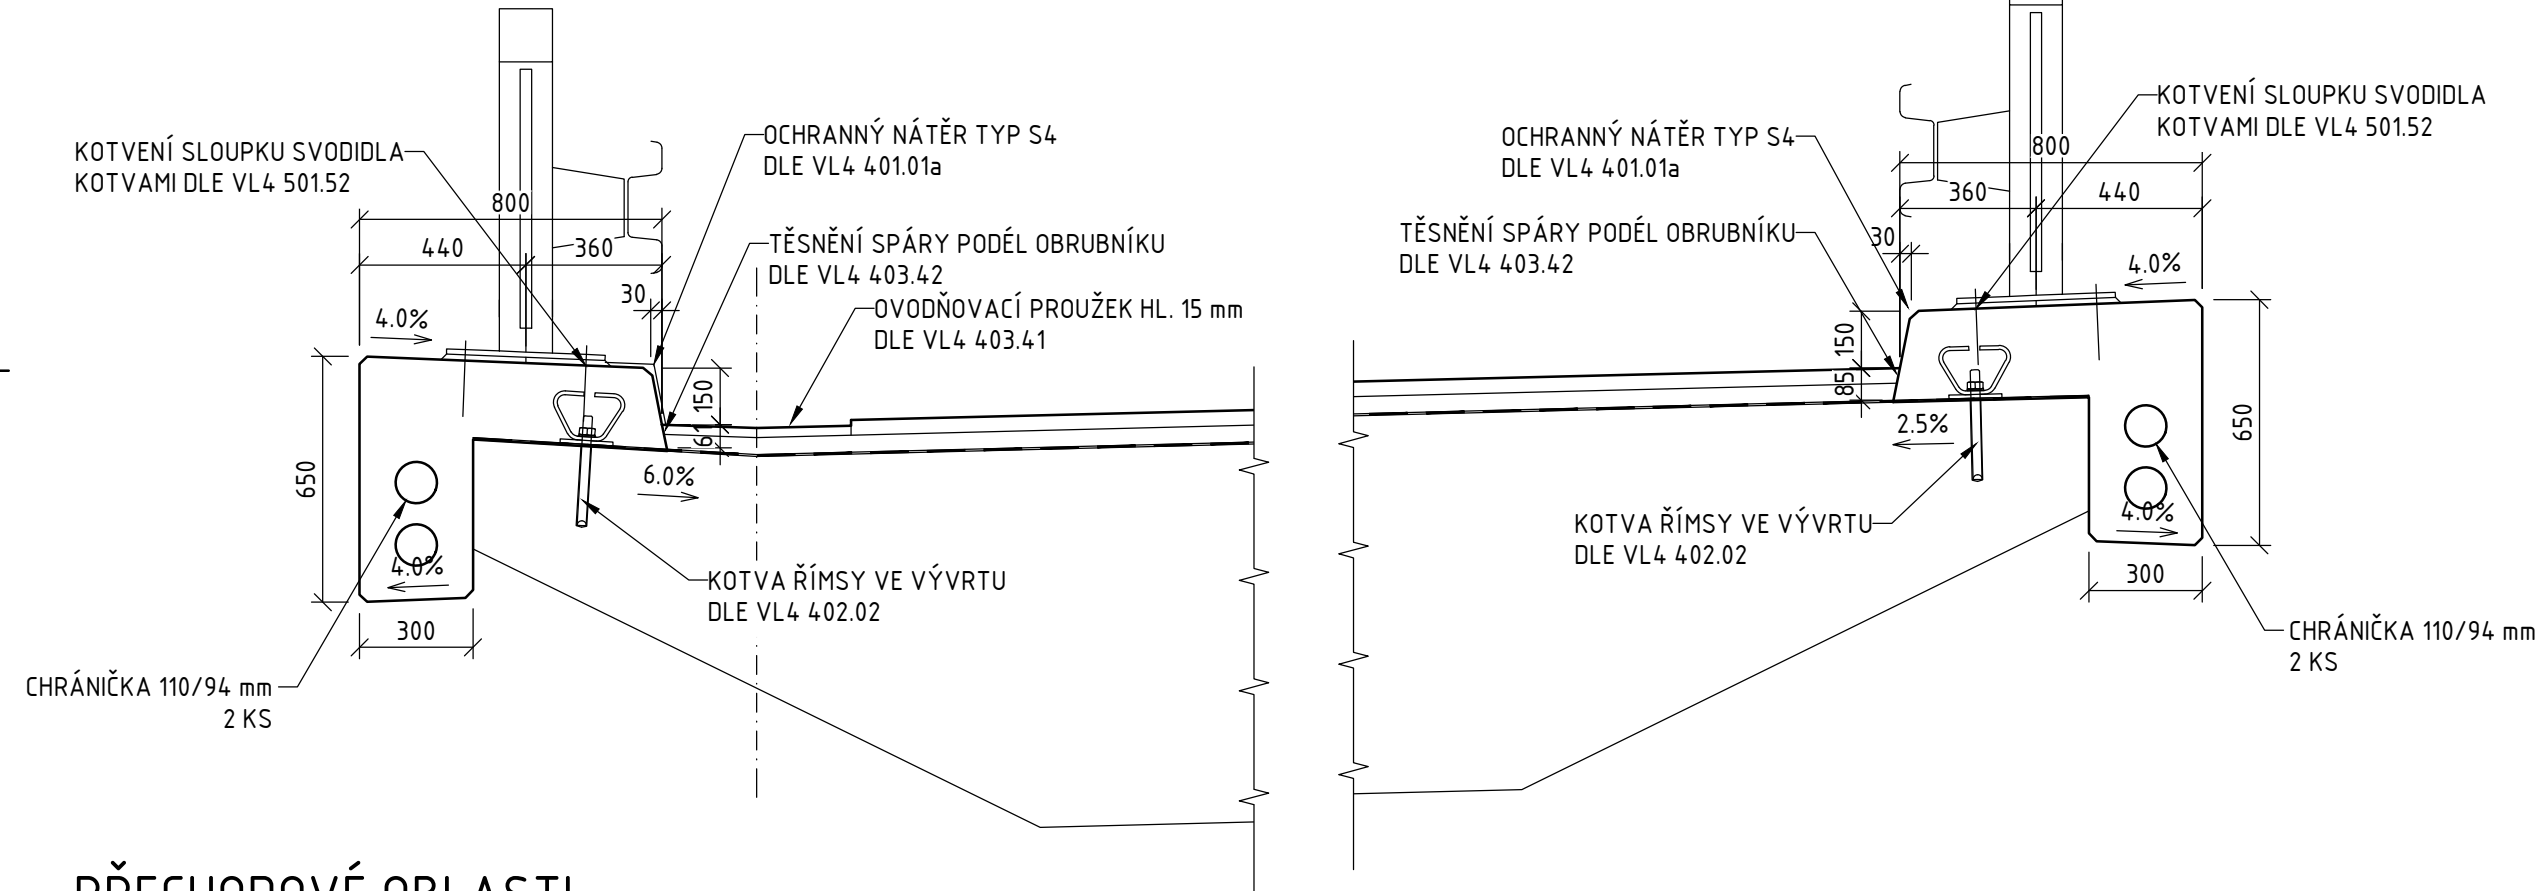

PŘECHODOVÉ OBLASTI
PODÉLNÝ ŘEZ 1:100

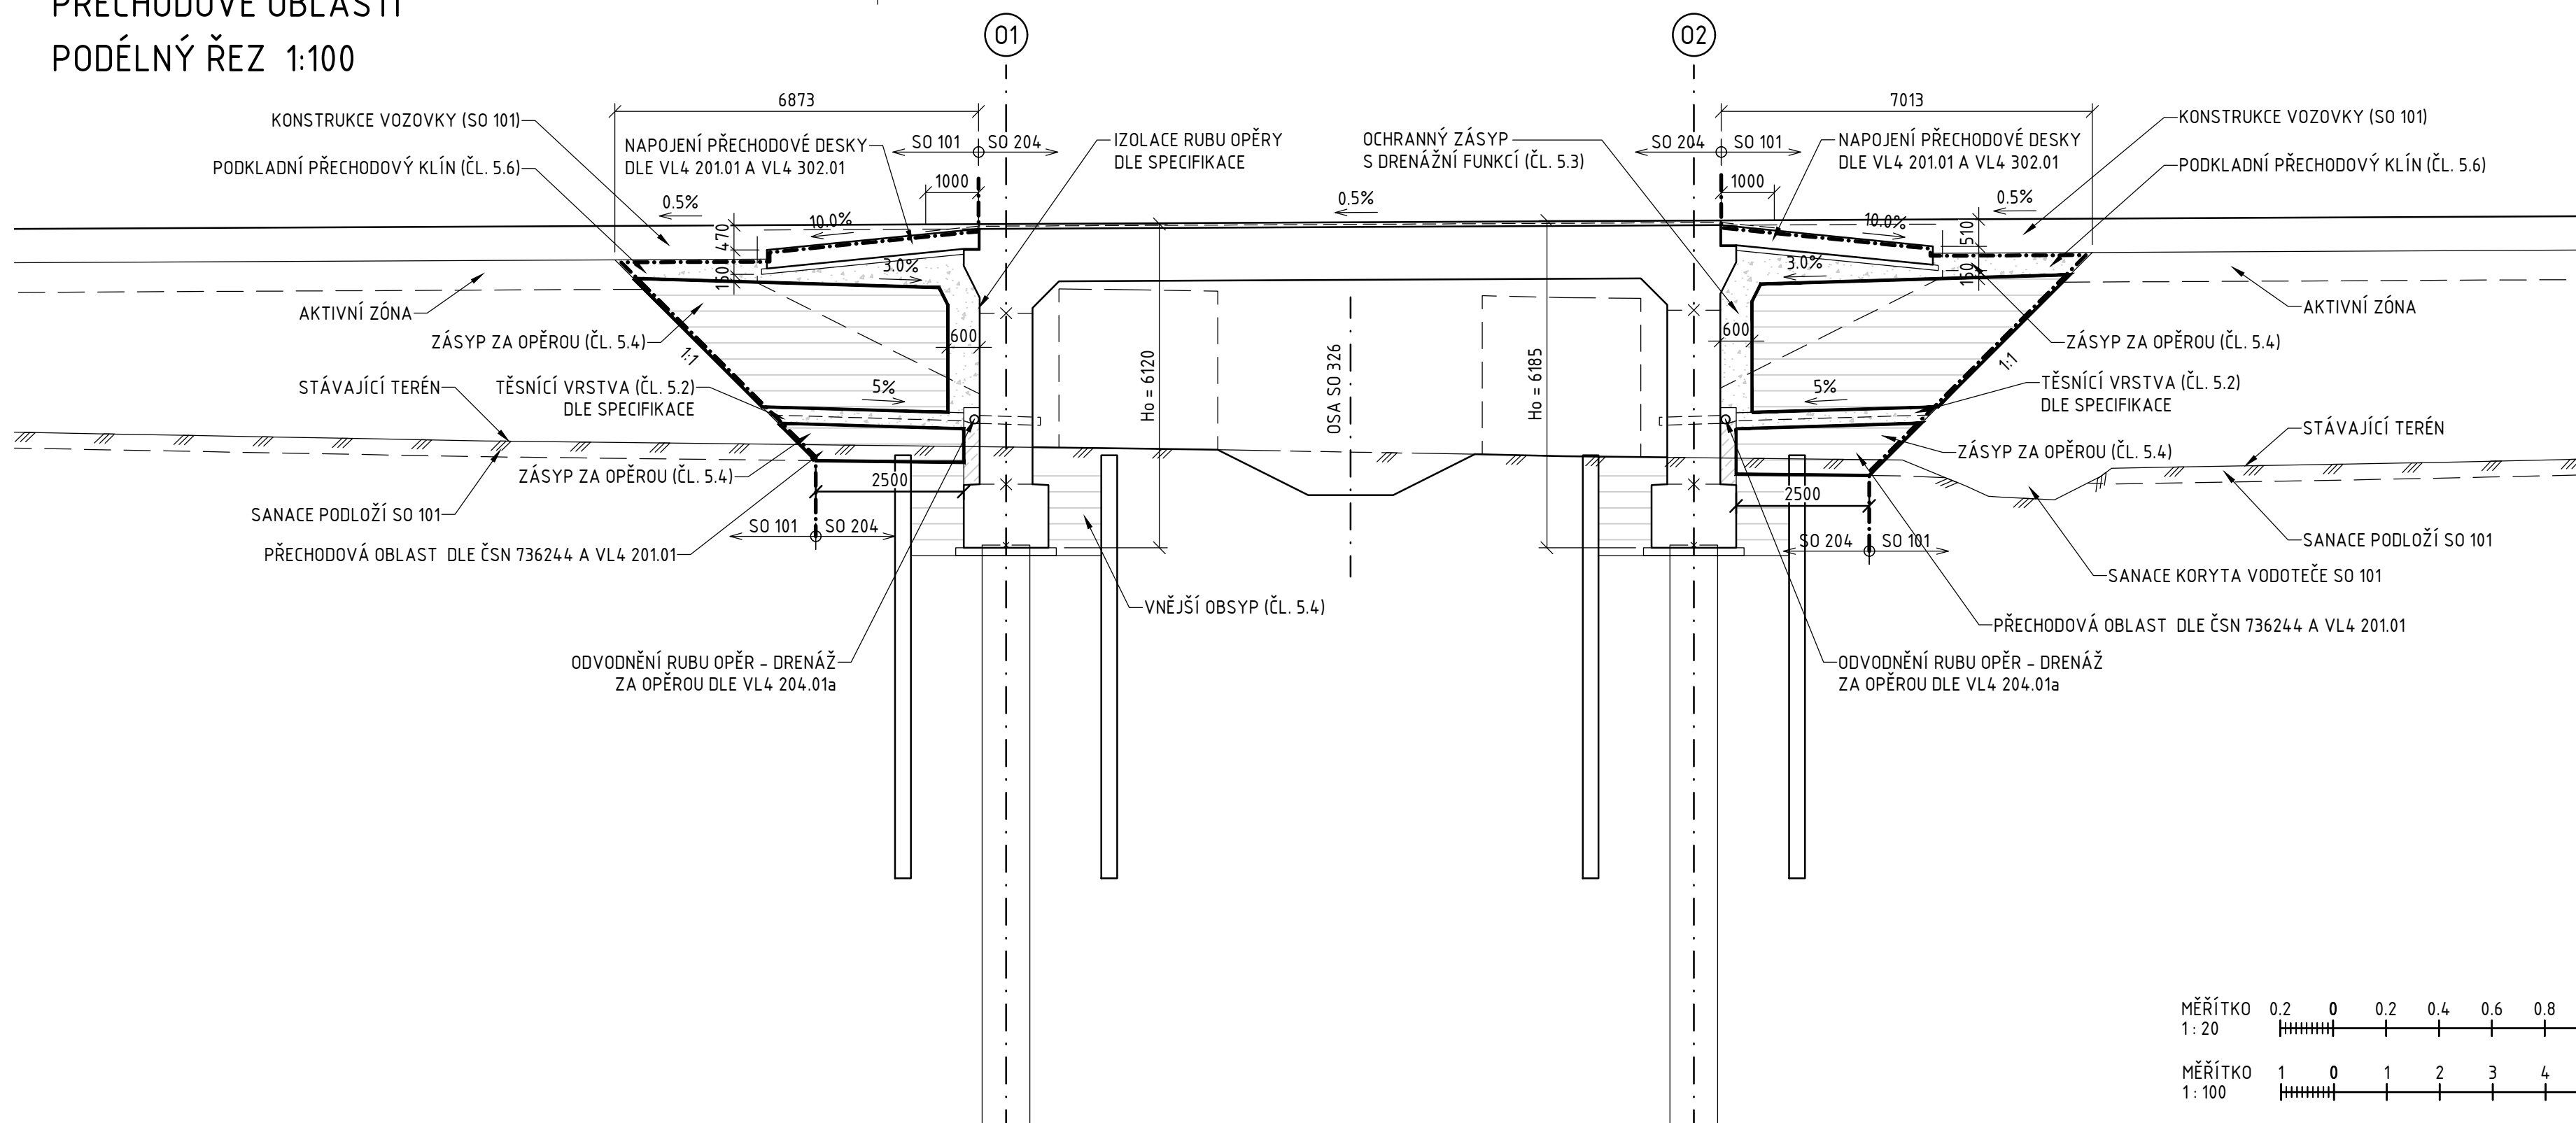


VYTYČOVACÍ VÝKRES, PŮDORYS 1:100

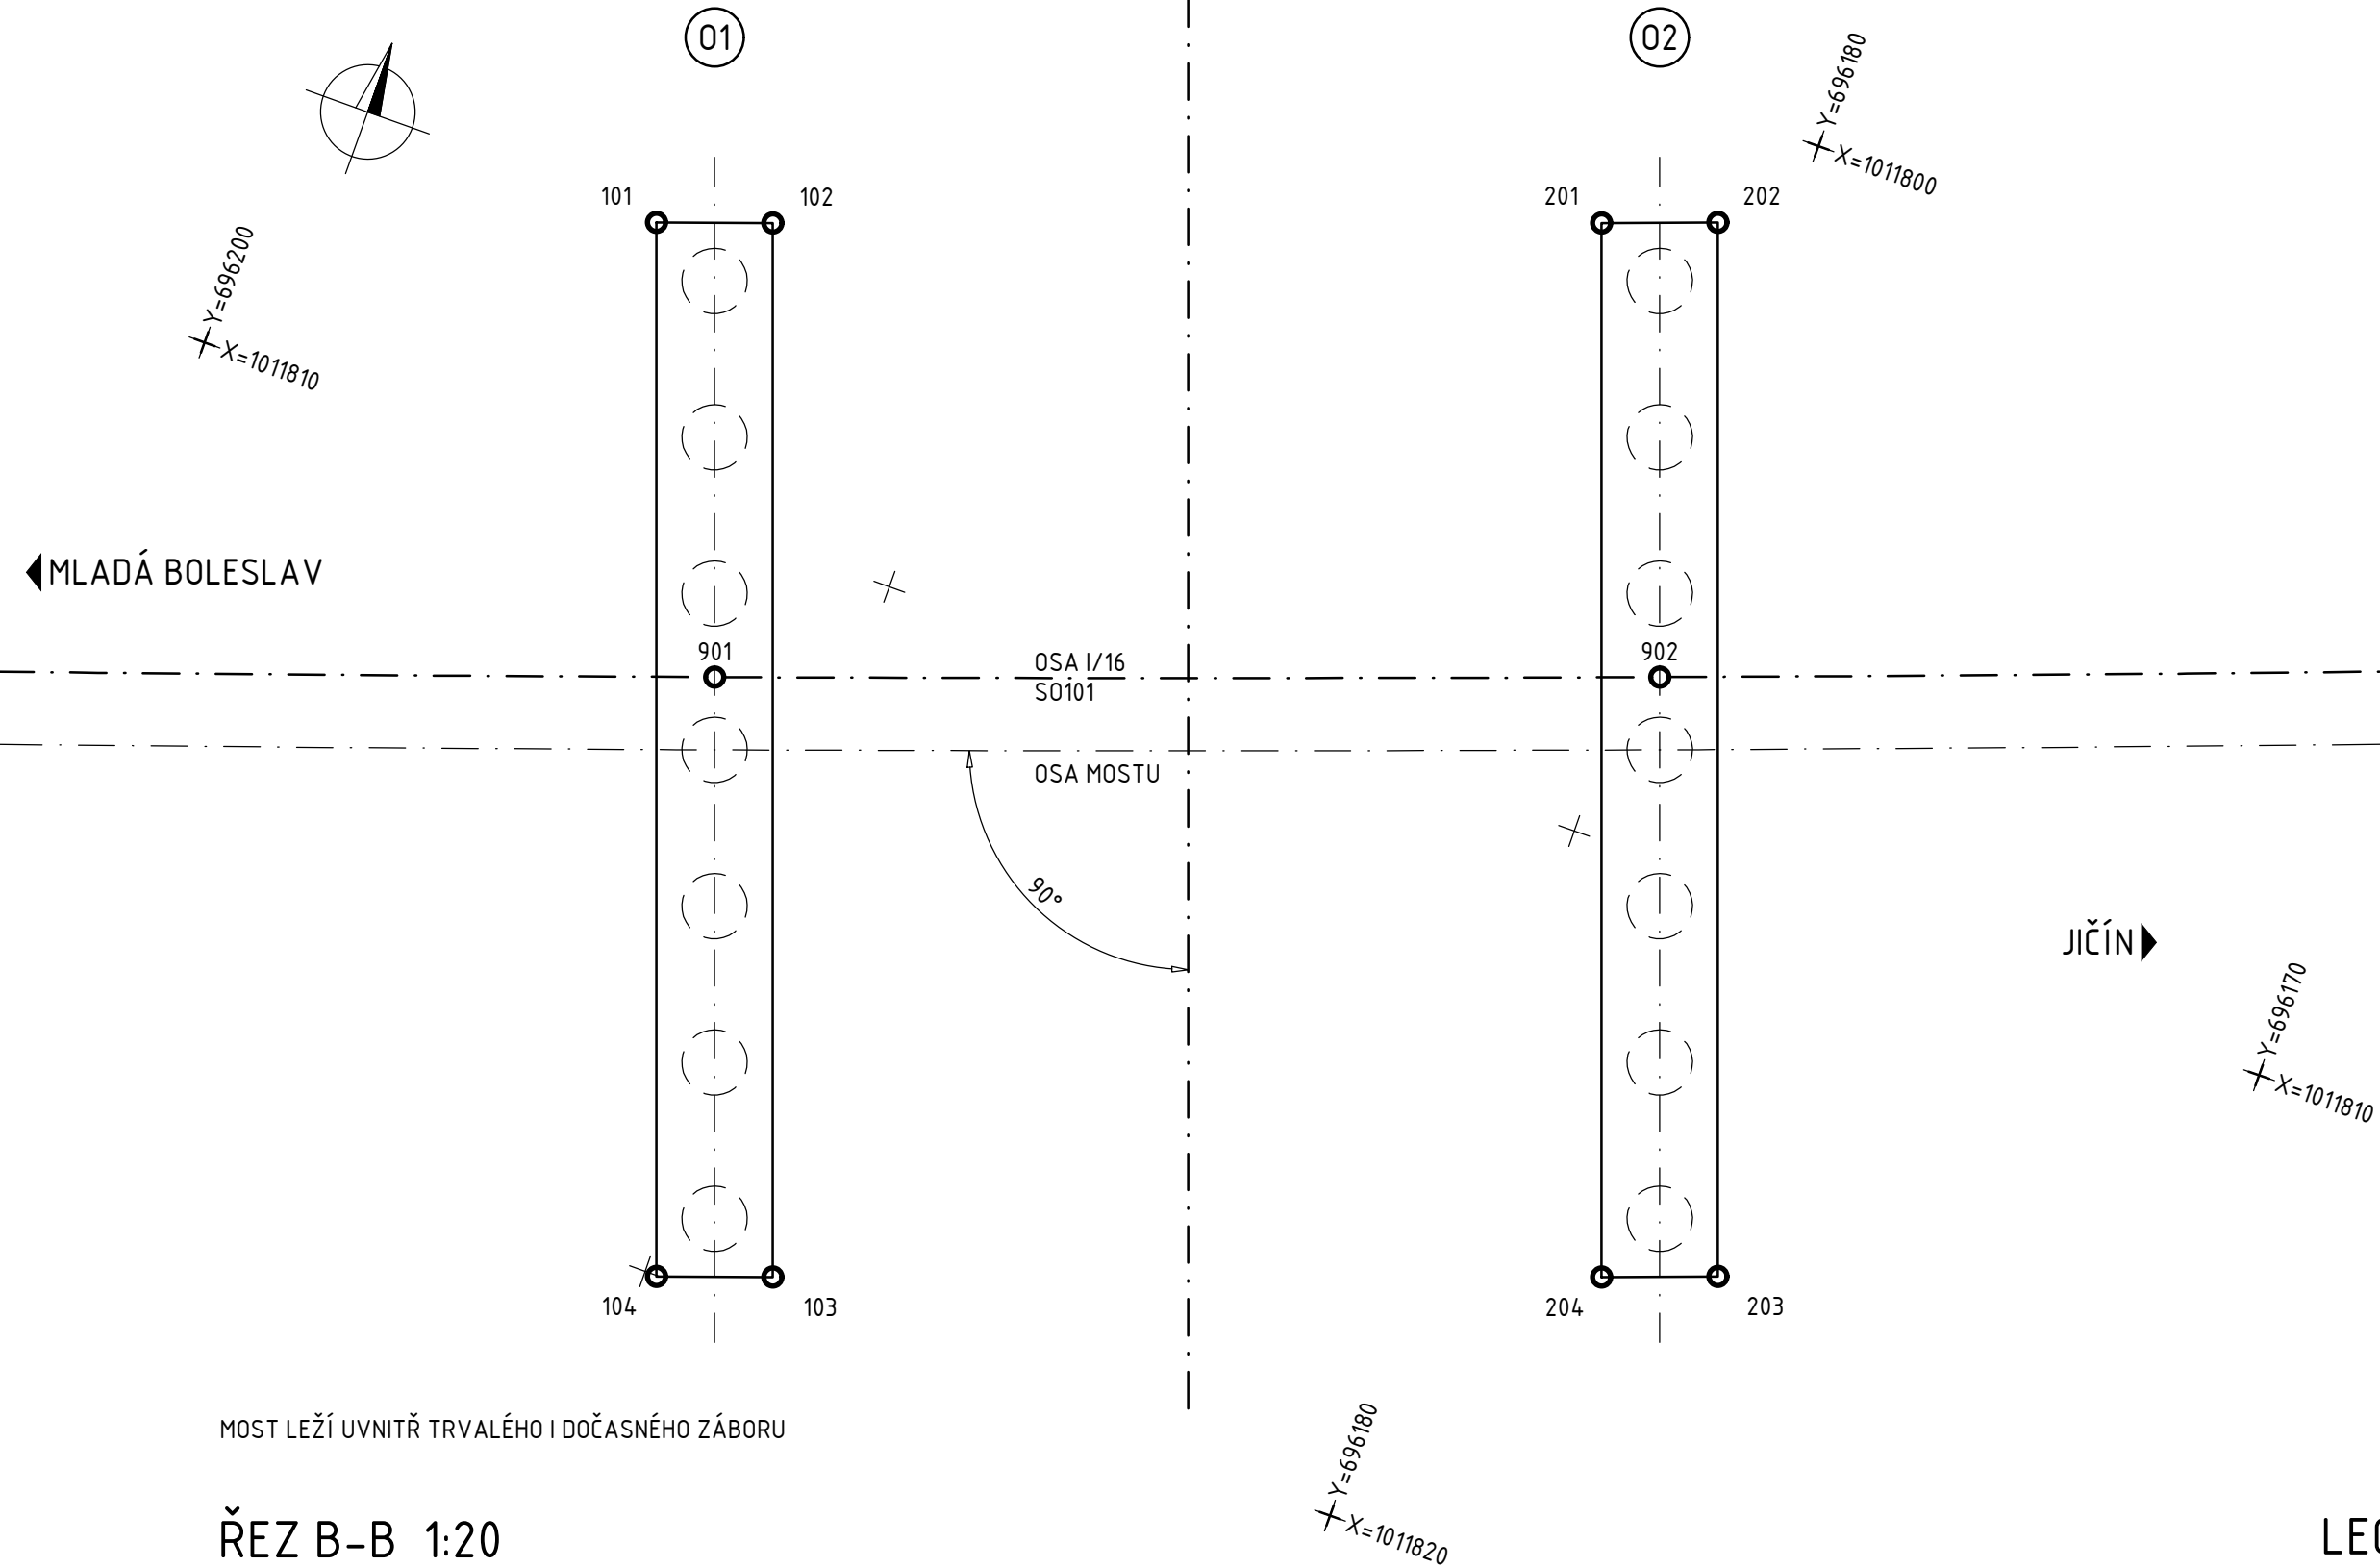

MOST LEŽÍ UVNITŘ TRVALÉHO I DOČASNÉHO ZÁBORU

ŘEZ B-B 1:20

PRAVÁ ŘÍMSA (LEVÁ ŘÍMSA OBDOBNĚ)

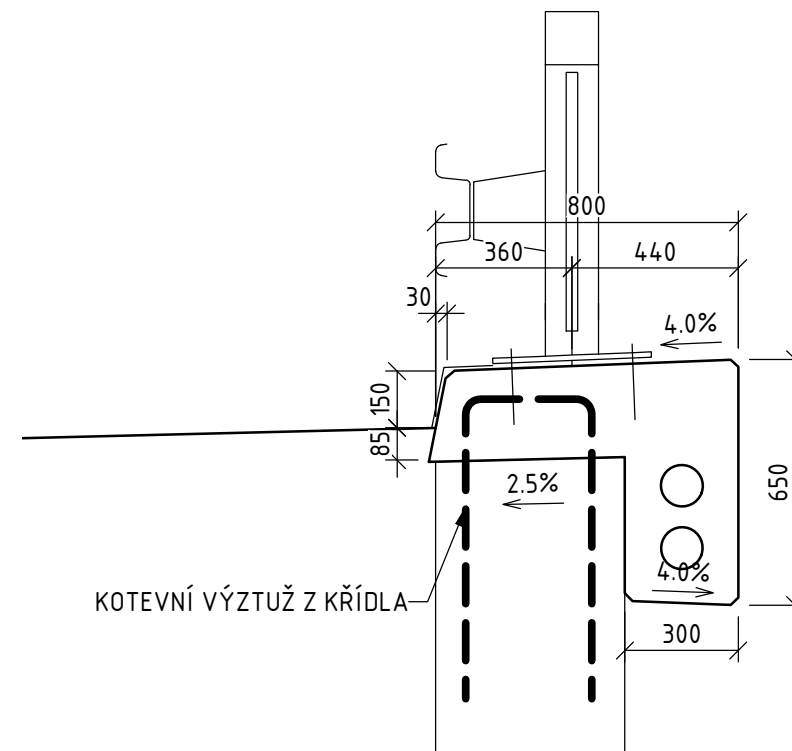

SOUŘADNICE VB

BOD	Y [m]	X [m]	Z [m]
101	696 194,701	1011 806,359	216,000
102	696 193,192	1011 805,828	216,000
103	696 188,320	1011 819,485	216,000
104	696 189,829	1011 820,016	216,000
201	696 182,455	1011 801,998	216,000
202	696 180,950	1011 801,454	216,000
203	696 176,078	1011 815,111	216,000
204	696 177,583	1011 815,655	216,000
901	696 191,846	1011 811,980	-
902	696 179,602	1011 807,613	-

LEGENDA:

— X — PRACOVNÍ SPÁRA

POZNÁMKY:

- VYTYČOVACÍ ODCHYLKY: VIZ PŘÍLOHA E.4.5.1 - GVS - SEZNAM SOUŘADNIC
- NEDÍLNOU SOUČÁSTÍ VÝKRESU JSOU POZNÁMKY A SPECIFIKACE UVEDENÉ NA VÝKRESE
POZNÁMEK A TECHNICKÝCH SPECIFIKACÍ

Souřadnicový systém: S-JTSK
Výškový systém: BpV

SO 204 MOST NA I/16 PŘES SUKORADSKOU STOKU V KM 5,048

Objednatel:



Ředitelství silnic a dálnic s. p.
Čerčanská 2023/12, Krč, 140 00 Praha 4



Valbek, spol. s r.o.
Vaňurova 505/17
460 07 Liberec 3



	Vypracoval	L. MARTINEK	<i>Havla</i>	Zak. číslo	21-L113-001
	Zodp. projektant	ING. I. BELDA	<i>Belda</i>	Datum	02/2025
	Tech. kontrola	ING. I. BELDA	<i>Belda</i>	Stupeň	PDPS
	Akce			Počet formátů	8x A4
I/16 MLADÁ BOLESLAV - MARTINOVICE					
Zhotovitel: Valbek, spol. s r.o. Vaňurova 505/17 460 07 Liberec 3	Příloha TVAR ŘÍMS, SCHÉMA VYTYČENÍ, PŘECHODOVÉ OBLASTI			Měřítko	1:100, 20
				Č. přílohy	Paré
				203	