

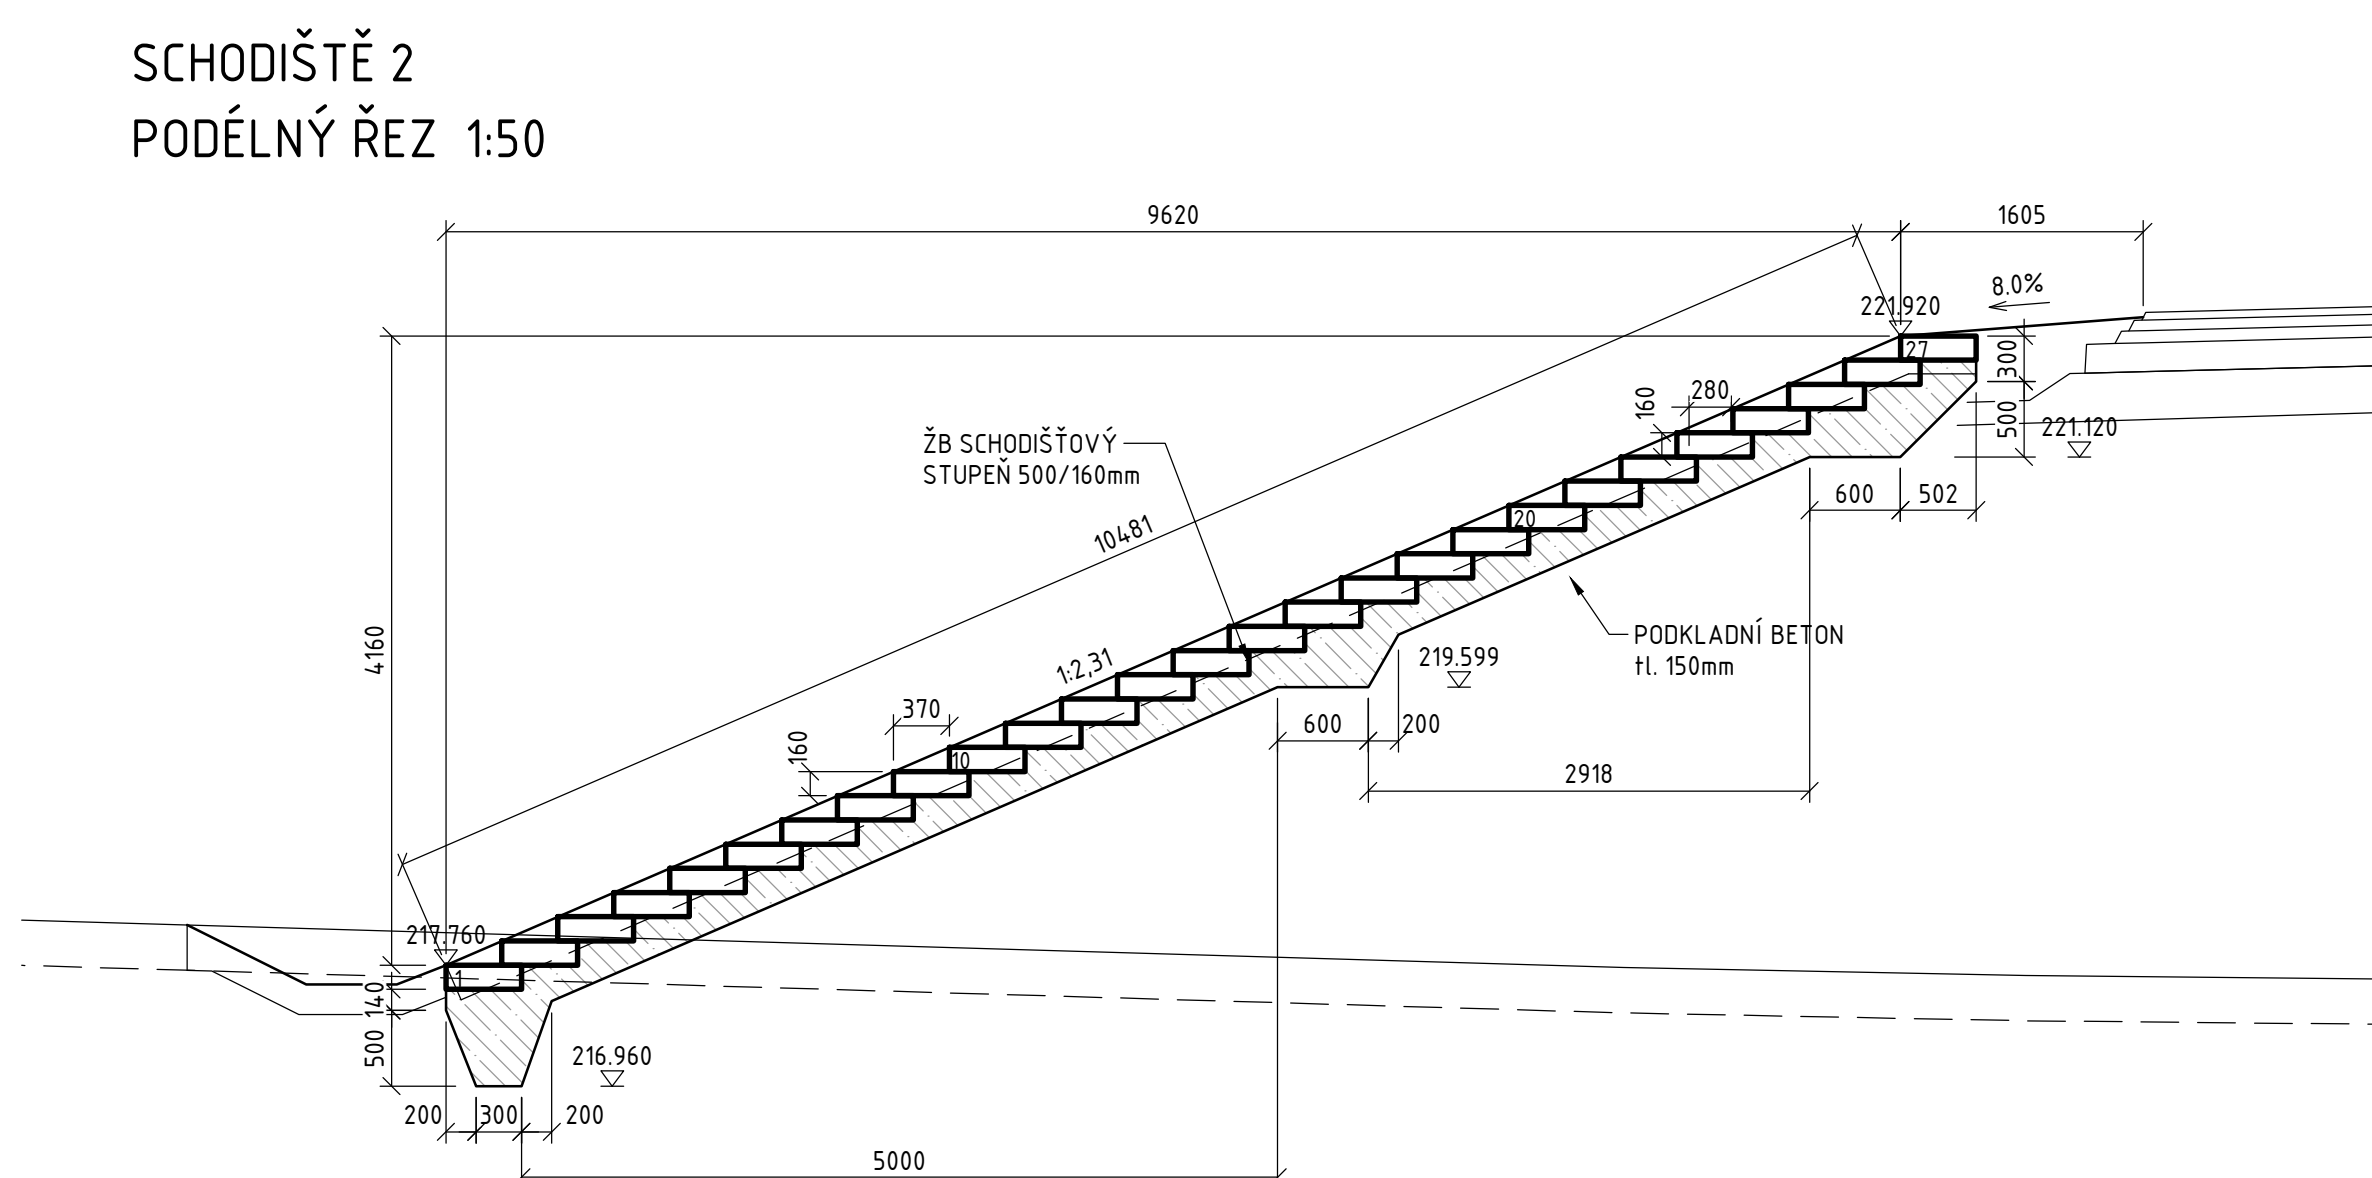


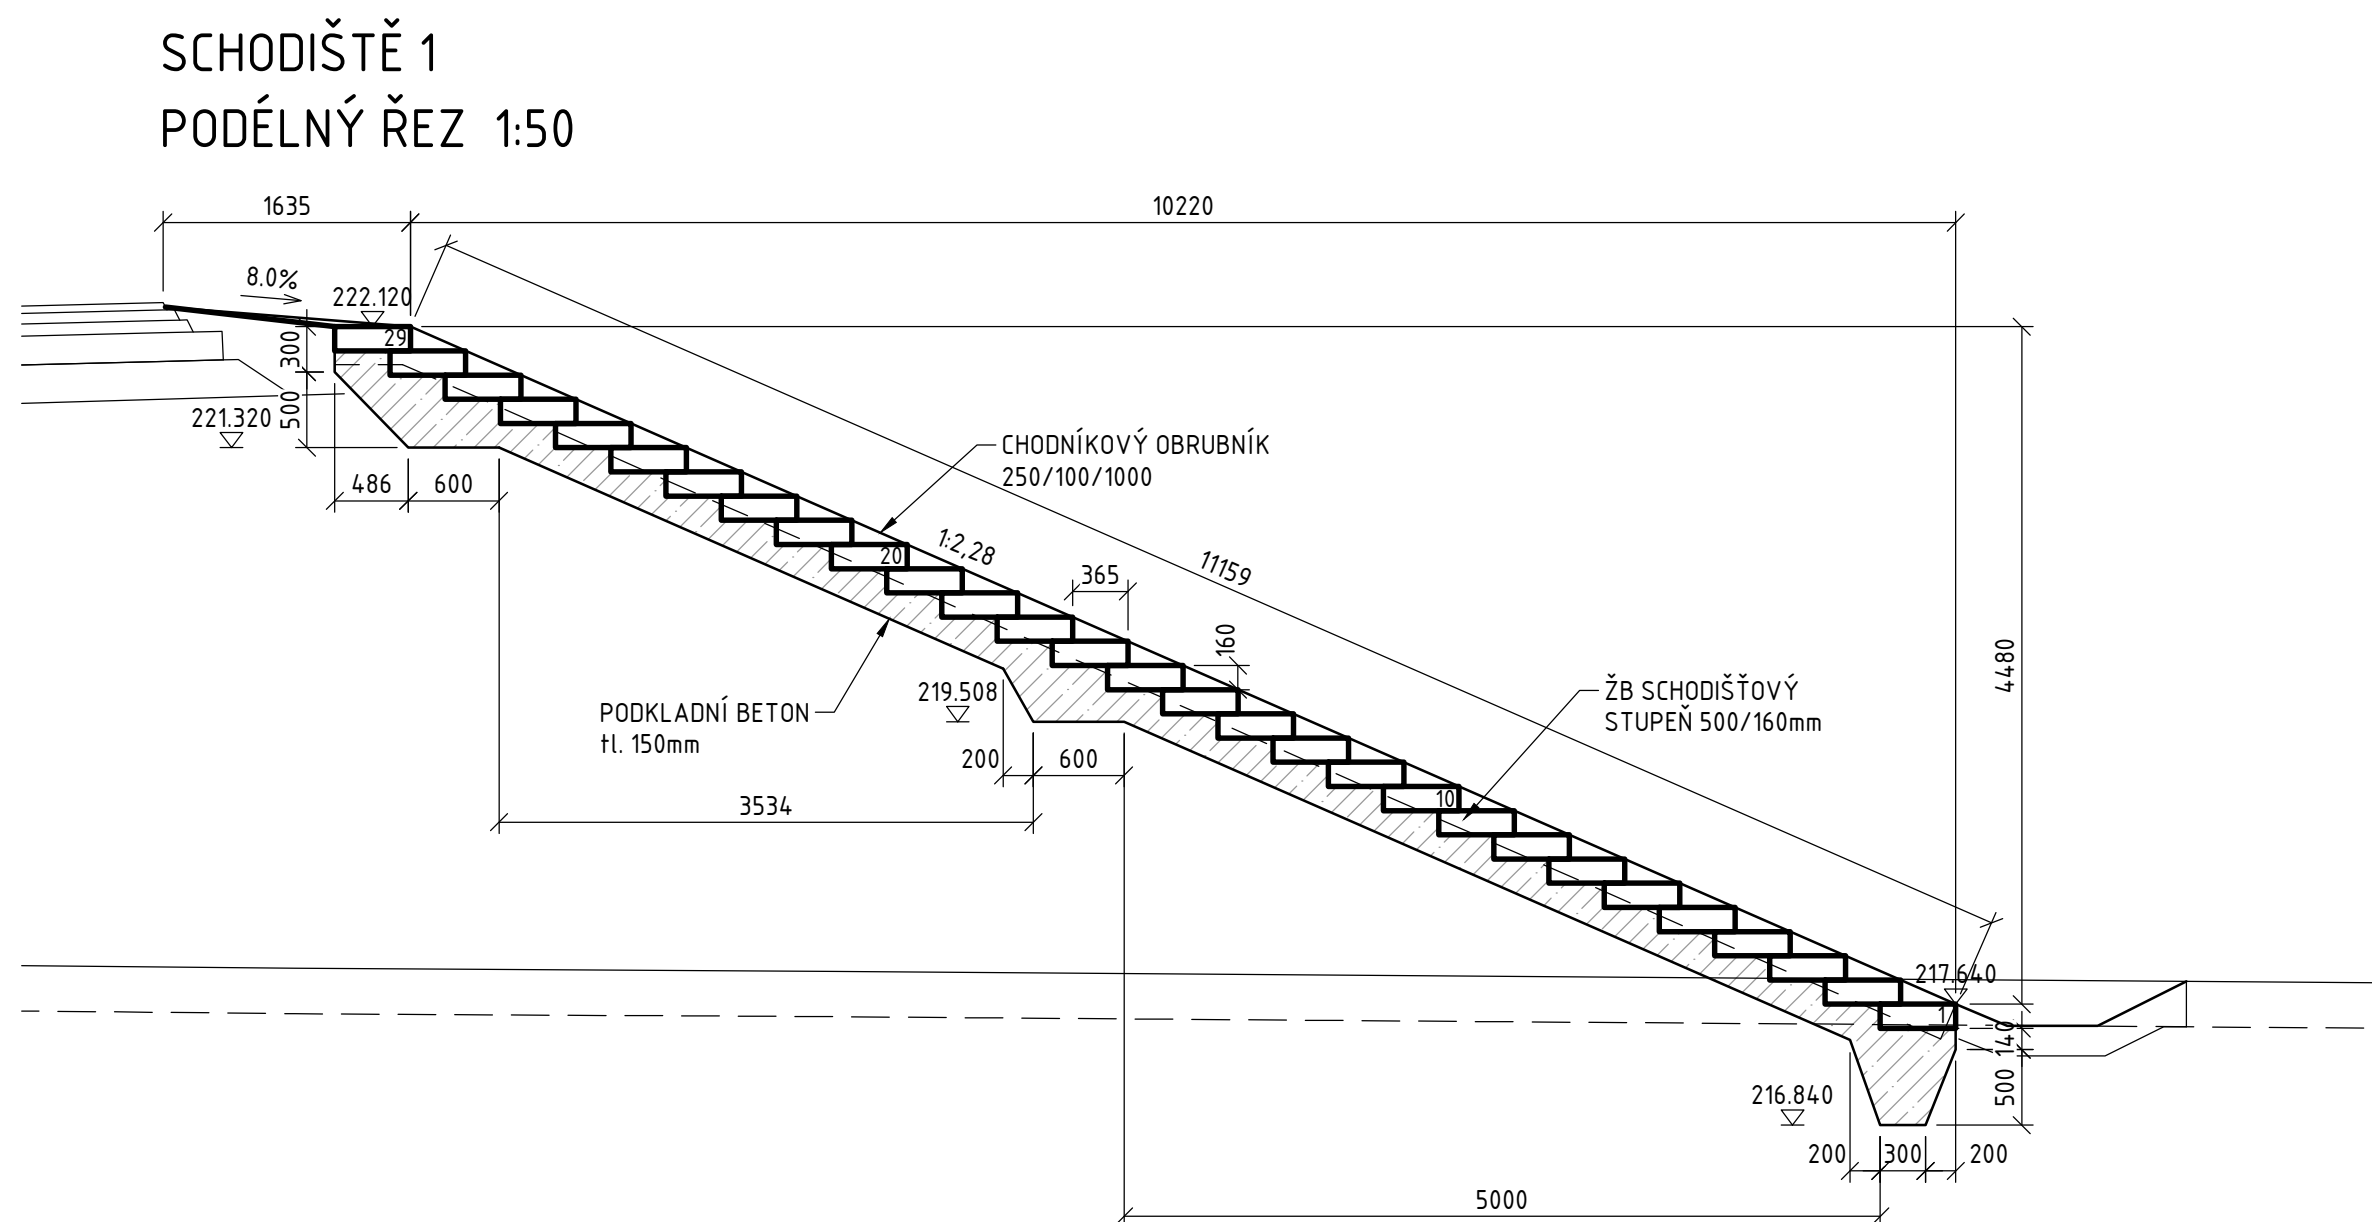

- NEDÍLNOU SOUČÁSTÍ VÝKRESU JSOU POZNÁMKY A SPECIFIKACE UVEDENÉ NA VÝKRESE POZNÁMEK A TECHNICKÝCH SPECIFIKACÍ

SO 204 MOST NA I/16 PŘES SUKORADSKOU STOKU V KM 5,048

 

	Vypracoval	L. MARTÍNEK		Zak. číslo	21-L113-001
	Zodp. projektant	ING. I. BELDA		Datum	02/2025
	Tech. kontrola	ING. I. BELDA		Stupeň	PPDS
	Akce	I/16 MLADÁ BOLESLAV - MARTINOVICE			Počet formátů
	Měřítko				1:150,50
				C. přílohy	Paré
Zhotovitel: Valbek, spol. s r.o. Valbarkova 506/17 460 07 Ústí nad Labem	Příloha ÚPRAVY POD MOSTEM, SLUŽEBNÍ SCHODIŠTĚ	204			

